



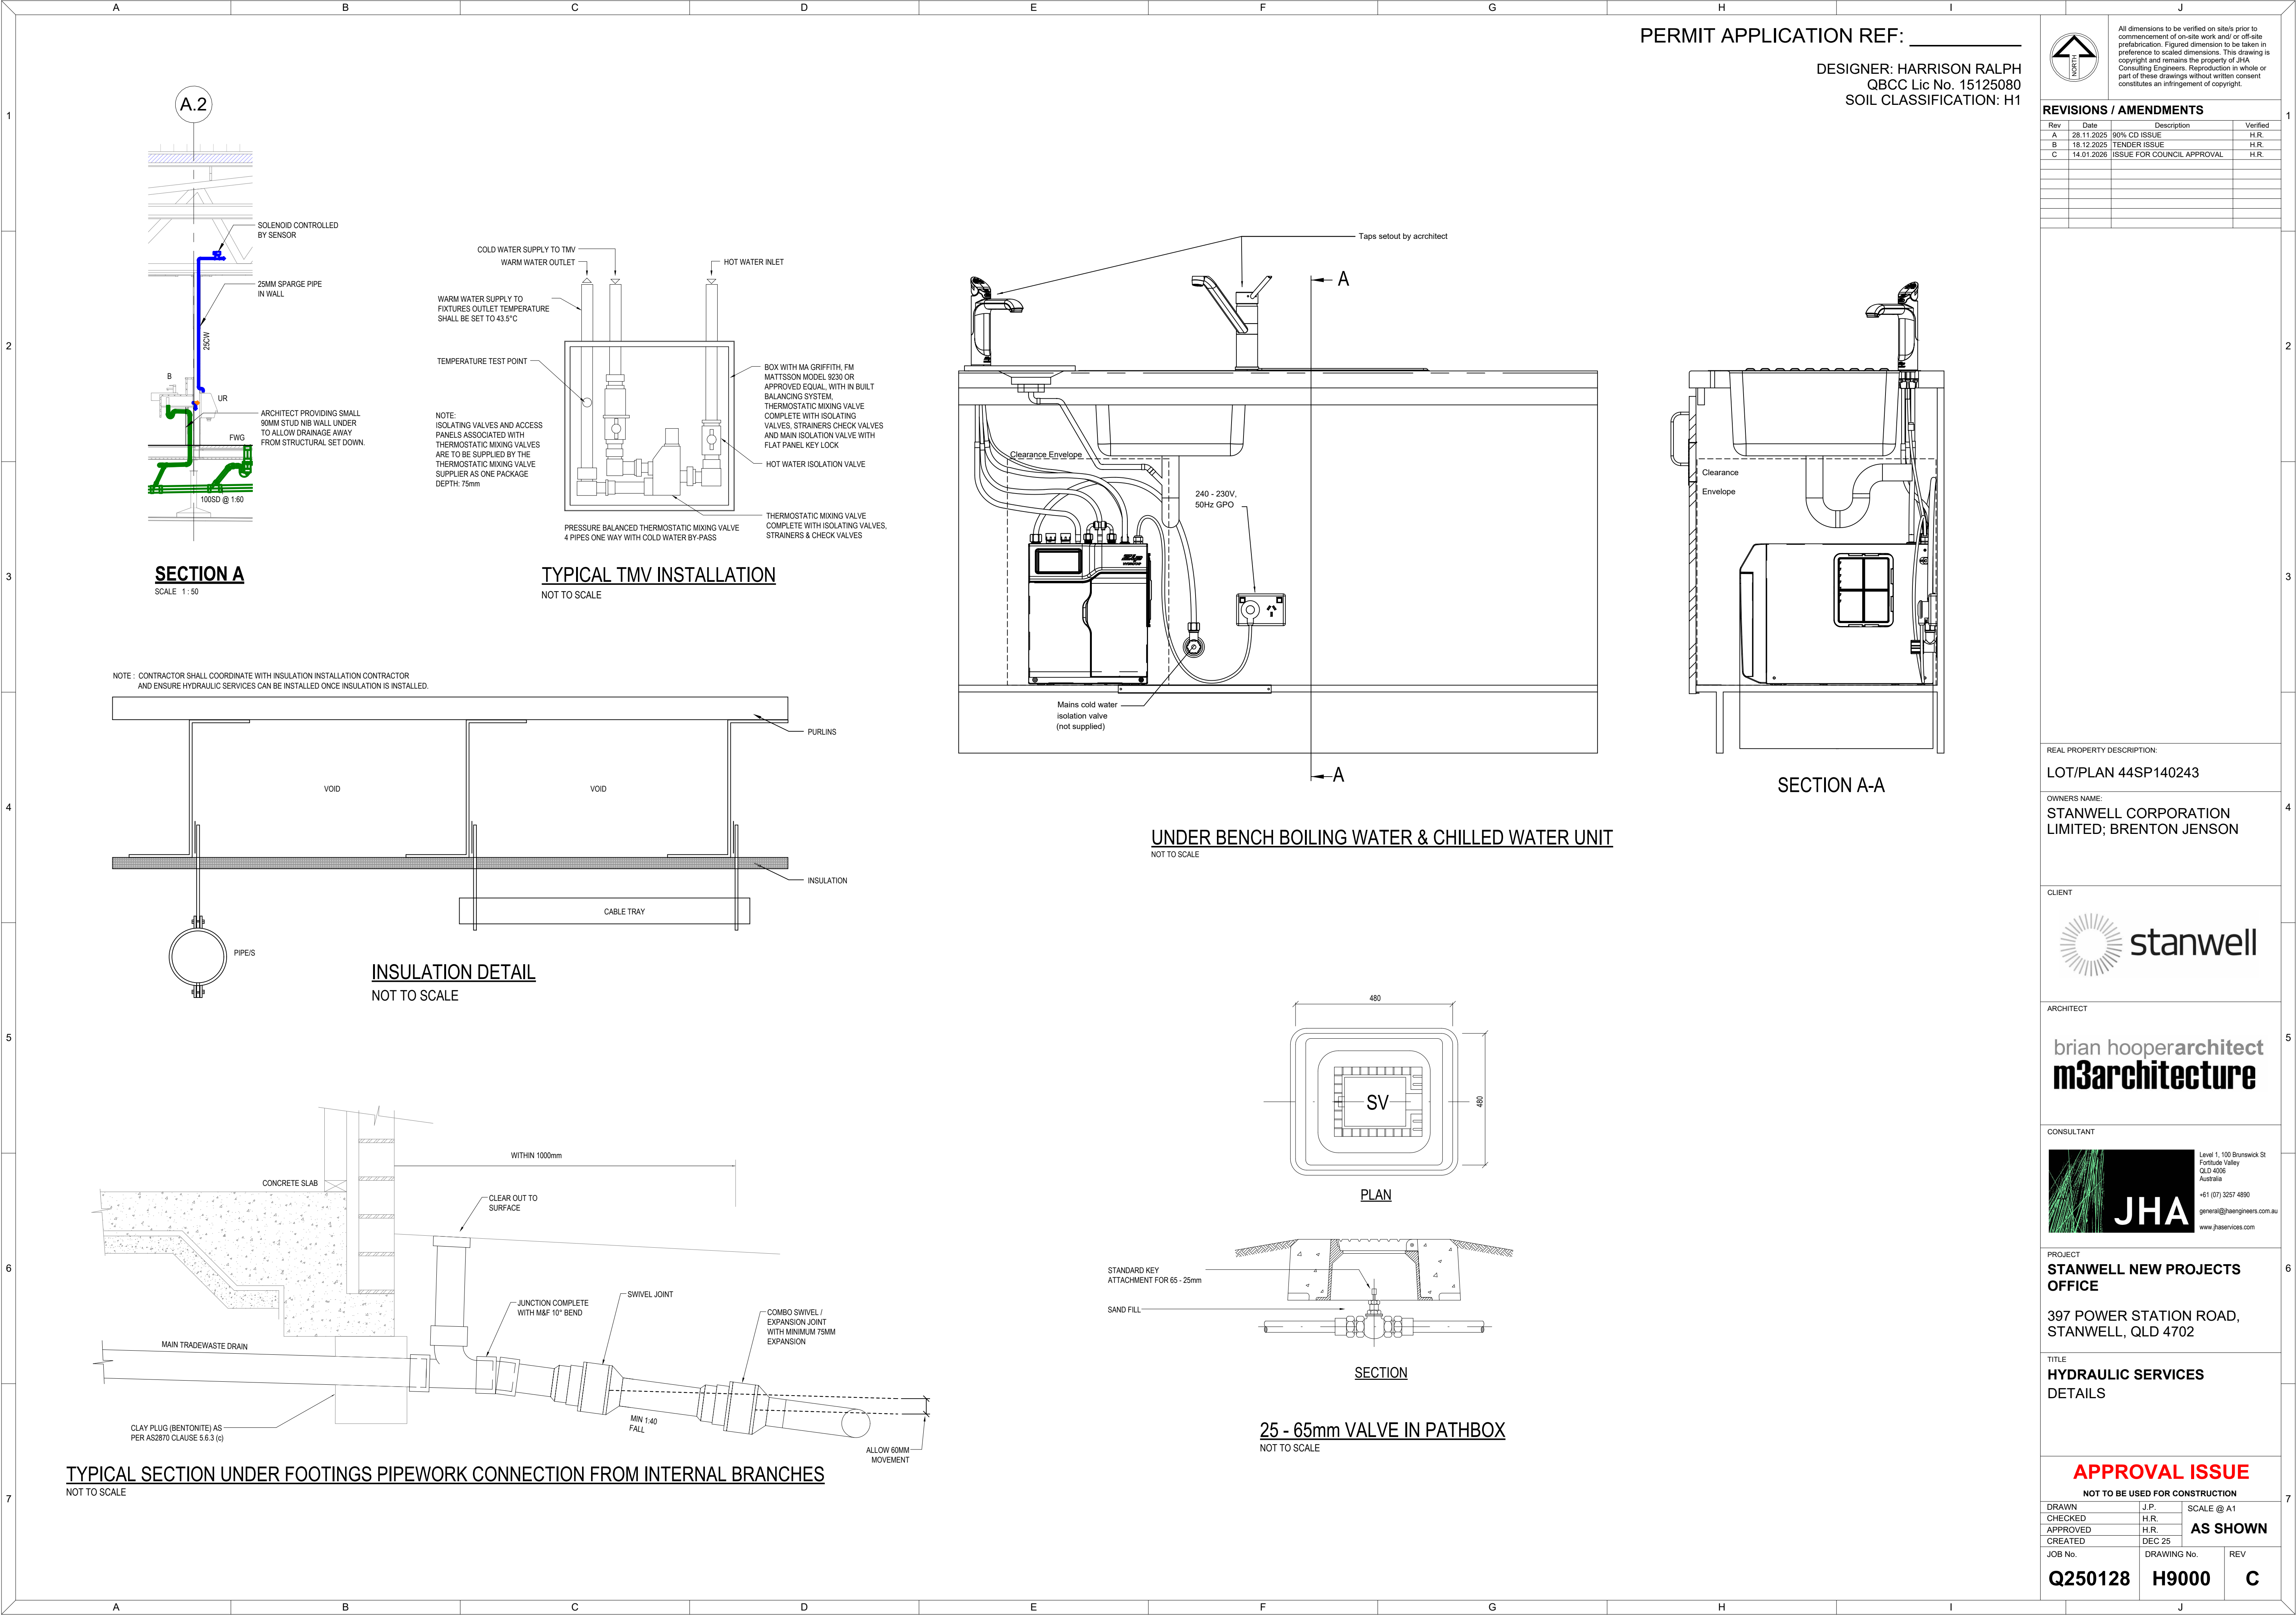

PERMIT APPLICATION REF: _____

DESIGNER: HARRISON RALPH
QBCC Lic No. 15125080
SOIL CLASSIFICATION: H1

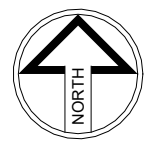

All dimensions to be verified on site/s prior to commencement of on-site work and/or off-site prefabrication. Figured dimension to be taken in preference to scaled dimensions. This drawing is copyright and remains the property of JHA Consulting Engineers. Reproduction in whole or part of these drawings without written consent constitutes an infringement of copyright.

REVISIONS / AMENDMENTS			
Rev	Date	Description	Verified
A	28.11.2025	90% CD ISSUE	H.R.
B	18.12.2025	TENDER ISSUE	H.R.
C	14.01.2026	ISSUE FOR COUNCIL APPROVAL	H.R.

REAL PROPERTY DESCRIPTION:
LOT/PLAN 44SP140243
OWNERS NAME:
STANWELL CORPORATION LIMITED; BRENTON JENSON



ARCHITECT
brian hooper**architect**
m3architecture

CONSULTANT



JHA

Level 1, 100 Brunswick St
Fortitude Valley
QLD 4006
Australia
+61 (07) 3257 4890
general@jhaservices.com.au
www.jhaservices.com

PROJECT
STANWELL NEW PROJECTS OFFICE
397 POWER STATION ROAD,
STANWELL, QLD 4702
TITLE
HYDRAULIC SERVICES DETAILS

APPROVAL ISSUE

NOT TO BE USED FOR CONSTRUCTION

DRAWN	J.P.	SCALE @ A1
CHECKED	H.R.	AS SHOWN
APPROVED	H.R.	
CREATED	DEC 25	

JOB No.	DRAWING No.	REV
Q250128	H9000	C