

GENERAL SERVICES DISCLAIMER

While every effort has been made to locate, identify, and where appropriate, indicate the extent & connectivity of all relevant visible and underground infrastructure within the survey area, no guarantee, either explicit or implied, can be given as to the correctness and completeness of such infrastructure shown hereon.

Due to the intrusive, high impact and potentially dangerous nature of exposing underground infrastructure, the risk of serious injury and damage to infrastructure is very high, therefore further investigation by suitably qualified personnel with the relevant skills, techniques and equipment will be required to comprehensively establish and qualify the true state of all infrastructure on site.


Please refer to each of the relevant service providers rules, procedures, guidelines, rights and responsibilities when designing or working in the vicinity of each respective plant or service.

SPECIFIC SERVICES DISCLAIMER

Services shown in this plan are derived from Stanwell Power Station Underground Services Index, being Drawing No. A3-P-621584-001 Rev G dated 22.10.2007, provided by Stanwell Corporation Ltd. Capricorn Survey Group CQ Pty Ltd accepts no responsibility or liability for any errors or omissions therein.


Service lines shown in this plan are intended as a general guide to presence and location and are not presented in their totality. Single lines may represent multiple cables for the same service running in close parallel proximity.

This note is an integral part of this plan, being 5 sheets in total, and all subsequent iterations of this plan. ©

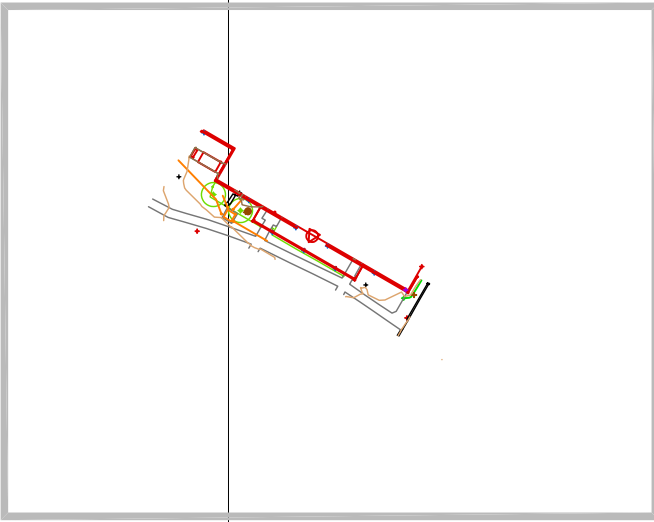


1

KEY DIAGRAM

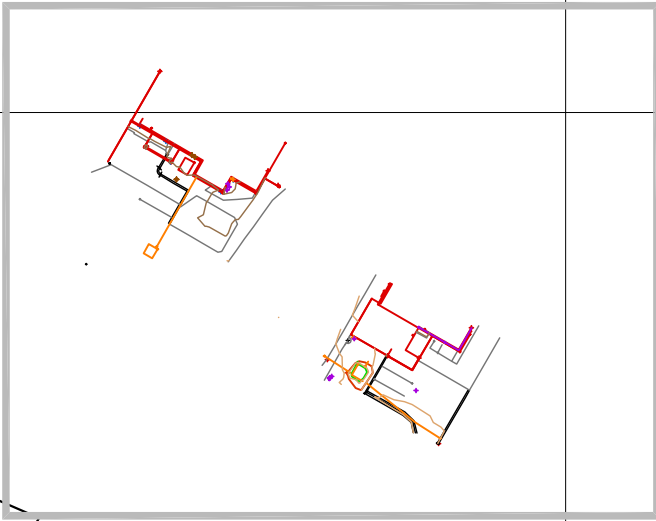

2

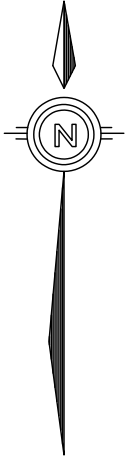

DEZIGN ELEMENTS

DESCRIPTION

**PARTIAL DETAIL SURVEY OF
LOT 44 ON SP140243**

**STANWELL POWER STATION
397 POWER STATION ROAD,
STANWELL**

REAL PROPERTY DESCRIPTION

Lot/Plan : Lot 44 on SP140243
Area : 1118 ha (Deed)
Locality : Stanwell
Local Authority : Rockhampton Regional Council

NOTES

This plan was prepared for DEZIGN ELEMENTS from field survey for the purpose of designing new constructions on the subject land and should not be used by any other persons for any other purpose.

Property boundaries have not been reinstated or marked at the time of survey and are approximate only, based on appropriate boundary connections.

Where possible underground services have been located by field survey. Some services shown hereon are compiled from local authority and service provider plans and/or plans provided by the client and are noted accordingly on the plan.

Prior to any design, excavation or construction on site, the relevant authorities, and a qualified service locator should be engaged to ensure all services that may be affected by any future works have been located.

These plans have been prepared as verification plots only. Some text RL's have been omitted for clarity. Please refer to the relevant 3D data files for any spatial interrogation requirements.

Any discrepancies should be verified in writing with Capricorn Survey Group (CQ) Pty Ltd.

This note is an integral part of this plan.

LEGEND	
LINETYPE LEGEND	
	UG Sewerage Line (S)
	UG Sewerage Line (Compiled) (SC)
	UG Effluent Line (Compiled) (E)
	UG Industrial Waste Line (Compiled) (IWL)
	UG Stormwater Line (Compiled) (SWC)
	UG Stormwater Line (Surveyed) (W)
	UG Electrical Line (Compiled) (EC)
	UG Electrical Line (Surveyed) (E)
	UG Electrical Line (Compiled) (EC)
	UG Communication Line (Compiled) (TC)
	UG Water Line (Compiled) (W)
	UG Domestic Water Line (Compiled) (WC)
	UG Raw Water Line (Compiled) (RW)
	UG Fire Services Pipe (Compiled) (FSP)
	Top of Bank
	Toe of Bank
	C/L of Bitumen
	Edge of Bitumen
	Line Marking
	Fence Line
	Roof / Guttering
	Eaves
CONTOUR LEGEND	
	0.25m Interval
	1.00m Interval

GENERAL SYMBOL LEGEND	
	Comms Conduit Marker
	Comms Pit
	Elec Conduit Marker
	Elec Turret
	Elec Pit
	Elec Light Bollard
	Elec Light Pole
	Elec Power Pole
	Elec Power Pole + Light
	Elec Power Pole + Transformer
	Elec Stay Point
	Elec Service (Unclass.)
	Gas Marker
	Gas Valve
	Gas Hot Water System
	Sewerage M/H
	Sewerage Vent
	Sewerage IO
	Stormwater M/H
	Stormwater Pit
	Stormwater DP/Kb Outlet
	Stormwater IO
	Water Fire Hydrant
	Water Meter
	Water Valve
	Water Tap
	Water Control Tap
	Water Service (Unclass.)
	Water Conduit Marker
	Water Tapping Band
	Metal Post
	Bollard
	Guide Sign
	Flag Pole
	Australia Post Box
	Shrub

DATUM

Vertical Datum : AHD Vide SmartNet Aus
Horizontal Datum : MGA2020 Vide SmartNet Aus
Contour Interval : 0.25m, 1.0m Index
Co-ord System : MGA2020 Vide SmartNet Aus

WARNING

LOCATION AND CONNECTIVITY OF U/G SERVICES SHOWN HEREON HAVE BEEN DETERMINED BY DIRECT ACCESS OR COMPILED FROM LOCAL AUTHORITY AND SERVICE PROVIDER PLANS ONLY. FURTHER INVESTIGATION MAY BE REQUIRED TO DETERMINE LOCATIONS OF ALL INACCESSIBLE SERVICES.

REVISION			
Issue	Date	Details	Authorised
A	08.12.2025	Initial Issue	RJKF

CREATED


capricornsurveygroupcq
SURVEYING & PLANNING SOLUTIONS

07 4927 5199 | reception@csagcq.com.au | 132 Victoria Parade, Rockhampton QLD 4700

SCALE

1:1250 @ A1

DRAWING NUMBER	ISSUE
9813-05-DTL (1/5)	A

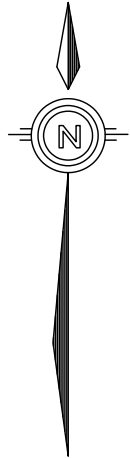

7397650N

GENERAL SERVICES DISCLAIMER

While every effort has been made to locate, identify, and where appropriate, indicate the extent & connectivity of all relevant visible and underground infrastructure within the survey area, no guarantee, either explicit or implied, can be given as to the correctness and completeness of such infrastructure shown hereon.

Due to the intrusive, high impact and potentially dangerous nature of exposing underground infrastructure, the risk of serious injury and damage to infrastructure is very high, therefore further investigation by suitably qualified personnel with the relevant skills, techniques and equipment will be required to comprehensively establish and qualify the true state of all infrastructure on site.

Please refer to each of the relevant service providers rules, procedures, guidelines, rights and responsibilities when designing or working in the vicinity of each respective plant or service.

SPECIFIC SERVICES DISCLAIMER

Services shown in this plan are derived from Stanwell Power Station Underground Services Index, being Drawing No. A3-P-621584-001 Rev G dated 22.10.2007, provided by Stanwell Corporation Ltd. Capricorn Survey Group CQ Pty Ltd accepts no responsibility or liability for any errors or omissions therein.

Service lines shown in this plan are intended as a general guide to presence and location and are not presented in their totality. Single lines may represent multiple cables for the same service running in close parallel proximity.

This note is an integral part of this plan, being 5 sheets in total, and all subsequent iterations of this plan. ©

0m 1 2 3 4 5 6 7 8 9 10 11 12 13 14 15 16 17 18 19 20m

226300E

226300E

44
SP140243
Stanwell
Power Station

1 Storey
Concrete Block Building
(Main Workshop)

Site BM
Plug in Kerb
RL 61.59

To Workshop Road

PRINCIPAL

DEZIGN ELEMENTS

DESCRIPTION

**PARTIAL DETAIL SURVEY OF
LOT 44 ON SP140243**

**STANWELL POWER STATION
397 POWER STATION ROAD,
STANWELL**

REAL PROPERTY DESCRIPTION

Lot/Plan : Lot 44 on SP140243
Area : 1118 ha (Deed)
Locality : Stanwell
Local Authority : Rockhampton Regional Council

NOTES

This plan was prepared for DEZIGN ELEMENTS from field survey for the purpose of designing new constructions on the subject land and should not be used by any other persons for any other purpose.

Property boundaries have not been reinstated or marked at the time of survey and are approximate only, based on appropriate boundary connections.

Where possible underground services have been located by field survey. Some services shown hereon are compiled from local authority and service provider plans and/or plans provided by the client and are noted accordingly on the plan.

Prior to any design, excavation or construction on site, the relevant authorities, and a qualified service locator should be engaged to ensure all services that may be affected by any future works have been located.

These plans have been prepared as verification plots only. Some text RL's have been omitted for clarity. Please refer to the relevant 3D data files for any spatial interrogation requirements.

Any discrepancies should be verified in writing with Capricorn Survey Group (CQ) Pty Ltd.

This note is an integral part of this plan.

LEGEND

LINETYPE LEGEND

— S —	UG Sewerage Line
— SC —	UG Sewerage Line (Compiled)
— E —	UG Effluent Line (Compiled)
— I —	UG Industrial Waste Line (Compiled)
— SW —	UG Stormwater Line
— SWC —	UG Stormwater Line (Compiled)
— W —	UG Electrical Line (Surveyed)
— EC —	UG Electrical Line (Compiled)
— T —	UG Communication Line (Compiled)
— TC —	UG Communication Line (Compiled)
— W —	UG Water Line
— WC —	UG Domestic Water Line (Compiled)
— R —	UG Raw Water Line (Compiled)
— S —	UG Sprinkler Piping (Compiled)
— F —	UG Fire Services Pipe (Compiled)
—	Top of Bank
—	Toe of Bank
—	CL of Bitumen
—	Edge of Bitumen
—	Line Marking
—	Fence Line
—	Roof / Guttering
—	Eaves

CONTOUR LEGEND

—	0.25m Interval
—	1.00m Interval

GENERAL SYMBOL LEGEND

Comms Conduit Marker	Stormwater M/H
Comms Pit	Stormwater Pit
Elec Conduit Marker	Stormwater DP/Kb Outlet
Elec Turret	Stormwater IO
Elec Pit	Water Fire Hydrant
Elec Light Bollard	Water Meter
Elec Light Pole	Water Valve
Elec Power Pole	Water Tap
Elec Power Pole + Light	Water Control Tap
Elec Power Pole + Transformer	Water Service (Unclass.)
Elec Stay Point	Water Conduit Marker
Elec Service (Unclass.)	Water Tapping Band
Gas Marker	Metal Post
Gas Valve	Bollard
Gas Hot Water System	Guide Sign
Sewerage M/H	Flag Pole
Sewerage Vent	Australia Post Box
Sewerage IO	Shrub

DATUM

Vertical Datum : AHD Vide SmartNet Aus
Horizontal Datum : MGA2020 Vide SmartNet Aus
Contour Interval : 0.25m, 1.0m Index
Co-ord System : MGA2020 Vide SmartNet Aus

WARNING

LOCATION AND CONNECTIVITY OF U/G SERVICES SHOWN HEREON HAVE BEEN DETERMINED BY DIRECT ACCESS OR COMPILED FROM LOCAL AUTHORITY AND SERVICE PROVIDER PLANS ONLY. FURTHER INVESTIGATION MAY BE REQUIRED TO DETERMINE LOCATIONS OF ALL INACCESSIBLE SERVICES.

REVISION

Issue	Date	Details	Authorised
A	08.12.2025	Initial Issue	RJKF

CREATED



SCALE

1:150 @ A1



DRAWING NUMBER

9813-05-DTL (2/5)

ISSUE

A

Drafted : KB

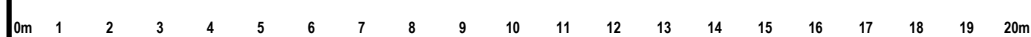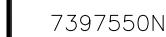

	Elec Light Bolland		Water Meter
	Elec Light Pole		Water Valve
	Elec Power Pole		Water Tap
	Elec Power Pole + Light		Water Control Tap
	Elec Power Pole + Transformer		Water Service (Unclass.)
	Elec Stay Point		Water Conduit Marker
	Elec Service (Unclass.)		Water Tapping Marker
	Gas Marker		Metal Post
	Gas Valve		Bollard
	Gas Hot Water System		Guide Sign
	Sewerage MH		Flag Pole
	Sewerage Vent		Australia Post Box
	Sewerage IO		Shrub

DATUM

Vertical Datum : AHD Wide SmartNet Aus

Horizontal Datum : MGA2020 Wide SmartNet Aus

Contour Interval : 0.25m, 1.0m Index

Co-ord System : MGA2020 Wide SmartNet Aus

DATUM


Vertical Datum : AHD Vide SmartNet Aus

Horizontal Datum : MGA2020 Vide SmartNet Aus

Contour Interval : 0.25m, 1.0m Index

Co-ord System : MGA2020 Vide SmartNet Aus

DRAWING NUMBER	ISSUE
9813-05-DTL (3/5)	A

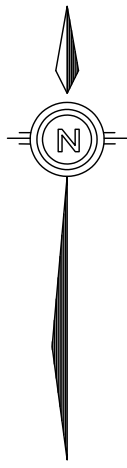

7397350N

7397350N

7397300N

7397300N

0m 1 2 3 4 5 6 7 8 9 10 11 12 13 14 15 16 17 18 19 20m

GENERAL SERVICES DISCLAIMER

While every effort has been made to locate, identify, and where appropriate, indicate the extent & connectivity of all relevant visible and underground infrastructure within the survey area, no guarantee, either explicit or implied, can be given as to the correctness and completeness of such infrastructure shown hereon.

Due to the intrusive, high impact and potentially dangerous nature of exposing underground infrastructure, the risk of serious injury and damage to infrastructure is very high, therefore further investigation by suitably qualified personnel with the relevant skills, techniques and equipment will be required to comprehensively establish and qualify the true state of all infrastructure on site.

Please refer to each of the relevant service providers rules, procedures, guidelines, rights and responsibilities when designing or working in the vicinity of each respective plant or service.

SPECIFIC SERVICES DISCLAIMER

Services shown in this plan are derived from Stanwell Power Station Underground Services Index, being Drawing No. A3-P-621584-001 Rev G dated 22.10.2007, provided by Stanwell Corporation Ltd. Capricorn Survey Group CQ Pty Ltd accepts no responsibility or liability for any errors or omissions therein.

Service lines shown in this plan are intended as a general guide to presence and location and are not presented in their totality. Single lines may represent multiple cables for the same service running in close parallel proximity.

This note is an integral part of this plan, being 5 sheets in total, and all subsequent iterations of this plan. ©

DEZIGN ELEMENTS

DESCRIPTION

PARTIAL DETAIL SURVEY OF
LOT 44 ON SP140243

STANWELL POWER STATION
397 POWER STATION ROAD,
STANWELL

REAL PROPERTY DESCRIPTION

Lot/Plan : Lot 44 on SP140243

Area : 1118 ha (Deed)

Locality : Stanwell

Local Authority : Rockhampton Regional Council

NOTES

This plan was prepared for DEZIGN ELEMENTS from field survey for the purpose of designing new constructions on the subject land and should not be used by any other persons for any other purpose.

Property boundaries have not been reinstated or marked at the time of survey and are approximate only, based on appropriate boundary connections.

Where possible underground services have been located by field survey. Some services shown hereon are compiled from local authority and service provider plans and/or plans provided by the client and are noted accordingly on the plan.

Prior to any design, excavation or construction on site, the relevant authorities, and a qualified service locator should be engaged to ensure all services that may be affected by any future works have been located.

These plans have been prepared as verification plots only. Some text RL's have been omitted for clarity. Please refer to the relevant 3D data files for any spatial interrogation requirements.

Any discrepancies should be verified in writing with Capricorn Survey Group (CQ) Pty Ltd.

This note is an integral part of this plan.

LEGEND

LINETYPE LEGEND

UG Sewerage Line

UG Sewerage Line (Compiled)

UG Effluent Line (Compiled)

UG Industrial Waste Line (Compiled)

UG Stormwater Line

UG Stormwater Line (Compiled)

UG Electrical Line (Surveyed)

UG Electrical Line (Compiled)

Disused UG Electrical Line (Compiled)

UG Communication Line (Compiled)

UG Water Line

UG Domestic Water Line (Compiled)

UG Raw Water Line (Compiled)

UG Sprinkler Piping (Compiled)

UG Fire Services Pipe (Compiled)

Top of Bank

Toe of Bank

CL of Bitumen

Edge of Bitumen

Line Marking

Fence Line

Roof / Guttering

Eaves

CONTOUR LEGEND

0.25m Interval

1.00m Interval

GENERAL SYMBOL LEGEND

Comms Conduit Marker

Comms Pit

Elec Conduit Marker

Elec Turret

Elec Pit

Elec Light Bollard

Elec Light Pole

Elec Power Pole

Elec Power Pole + Light

Elec Power Pole + Transformer

Elec Stay Point

Elec Service (Unclass.)

Gas Marker

Gas Valve

Gas Hot Water System

Sewerage MH

Sewerage Vent

Sewerage IO

Stormwater MH

Stormwater Pit

Stormwater DP/Kb Outlet

Stormwater IO

Water Fire Hydrant

Water Meter

Water Valve

Water Tap

Water Control Tap

Water Service (Unclass.)

Water Conduit Marker

Water Tapping Band

Metal Post

Bollard

Guide Sign

Flag Pole

Australia Post Box

Shrub

DATUM

Vertical Datum : AHD Vide SmartNet Aus

Horizontal Datum : MGA2020 Vide SmartNet Aus

Contour Interval : 0.25m, 1.0m Index

Co-ord System : MGA2020 Vide SmartNet Aus

WARNING

LOCATION AND CONNECTIVITY OF U/G SERVICES SHOWN HEREON HAVE BEEN DETERMINED BY DIRECT ACCESS OR COMPILED FROM LOCAL AUTHORITY AND SERVICE PROVIDER PLANS ONLY. FURTHER INVESTIGATION MAY BE REQUIRED TO DETERMINE LOCATIONS OF ALL INACCESSIBLE SERVICES.

REVISION

Issue

Date

Details

Authorised

A

08.12.2025

Initial Issue

RJKF

CREATED

capricornsurveygroupcqc

SURVEYING & PLANNING SOLUTIONS

07 4927 5199 | reception@capicorg.com.au | 132 Victoria Parade, Rockhampton QLD 4700

SCALE

1:150 @ A1


DRAWING NUMBER

9813-05-DTL (4/5)

ISSUE

A

Drafted : KB

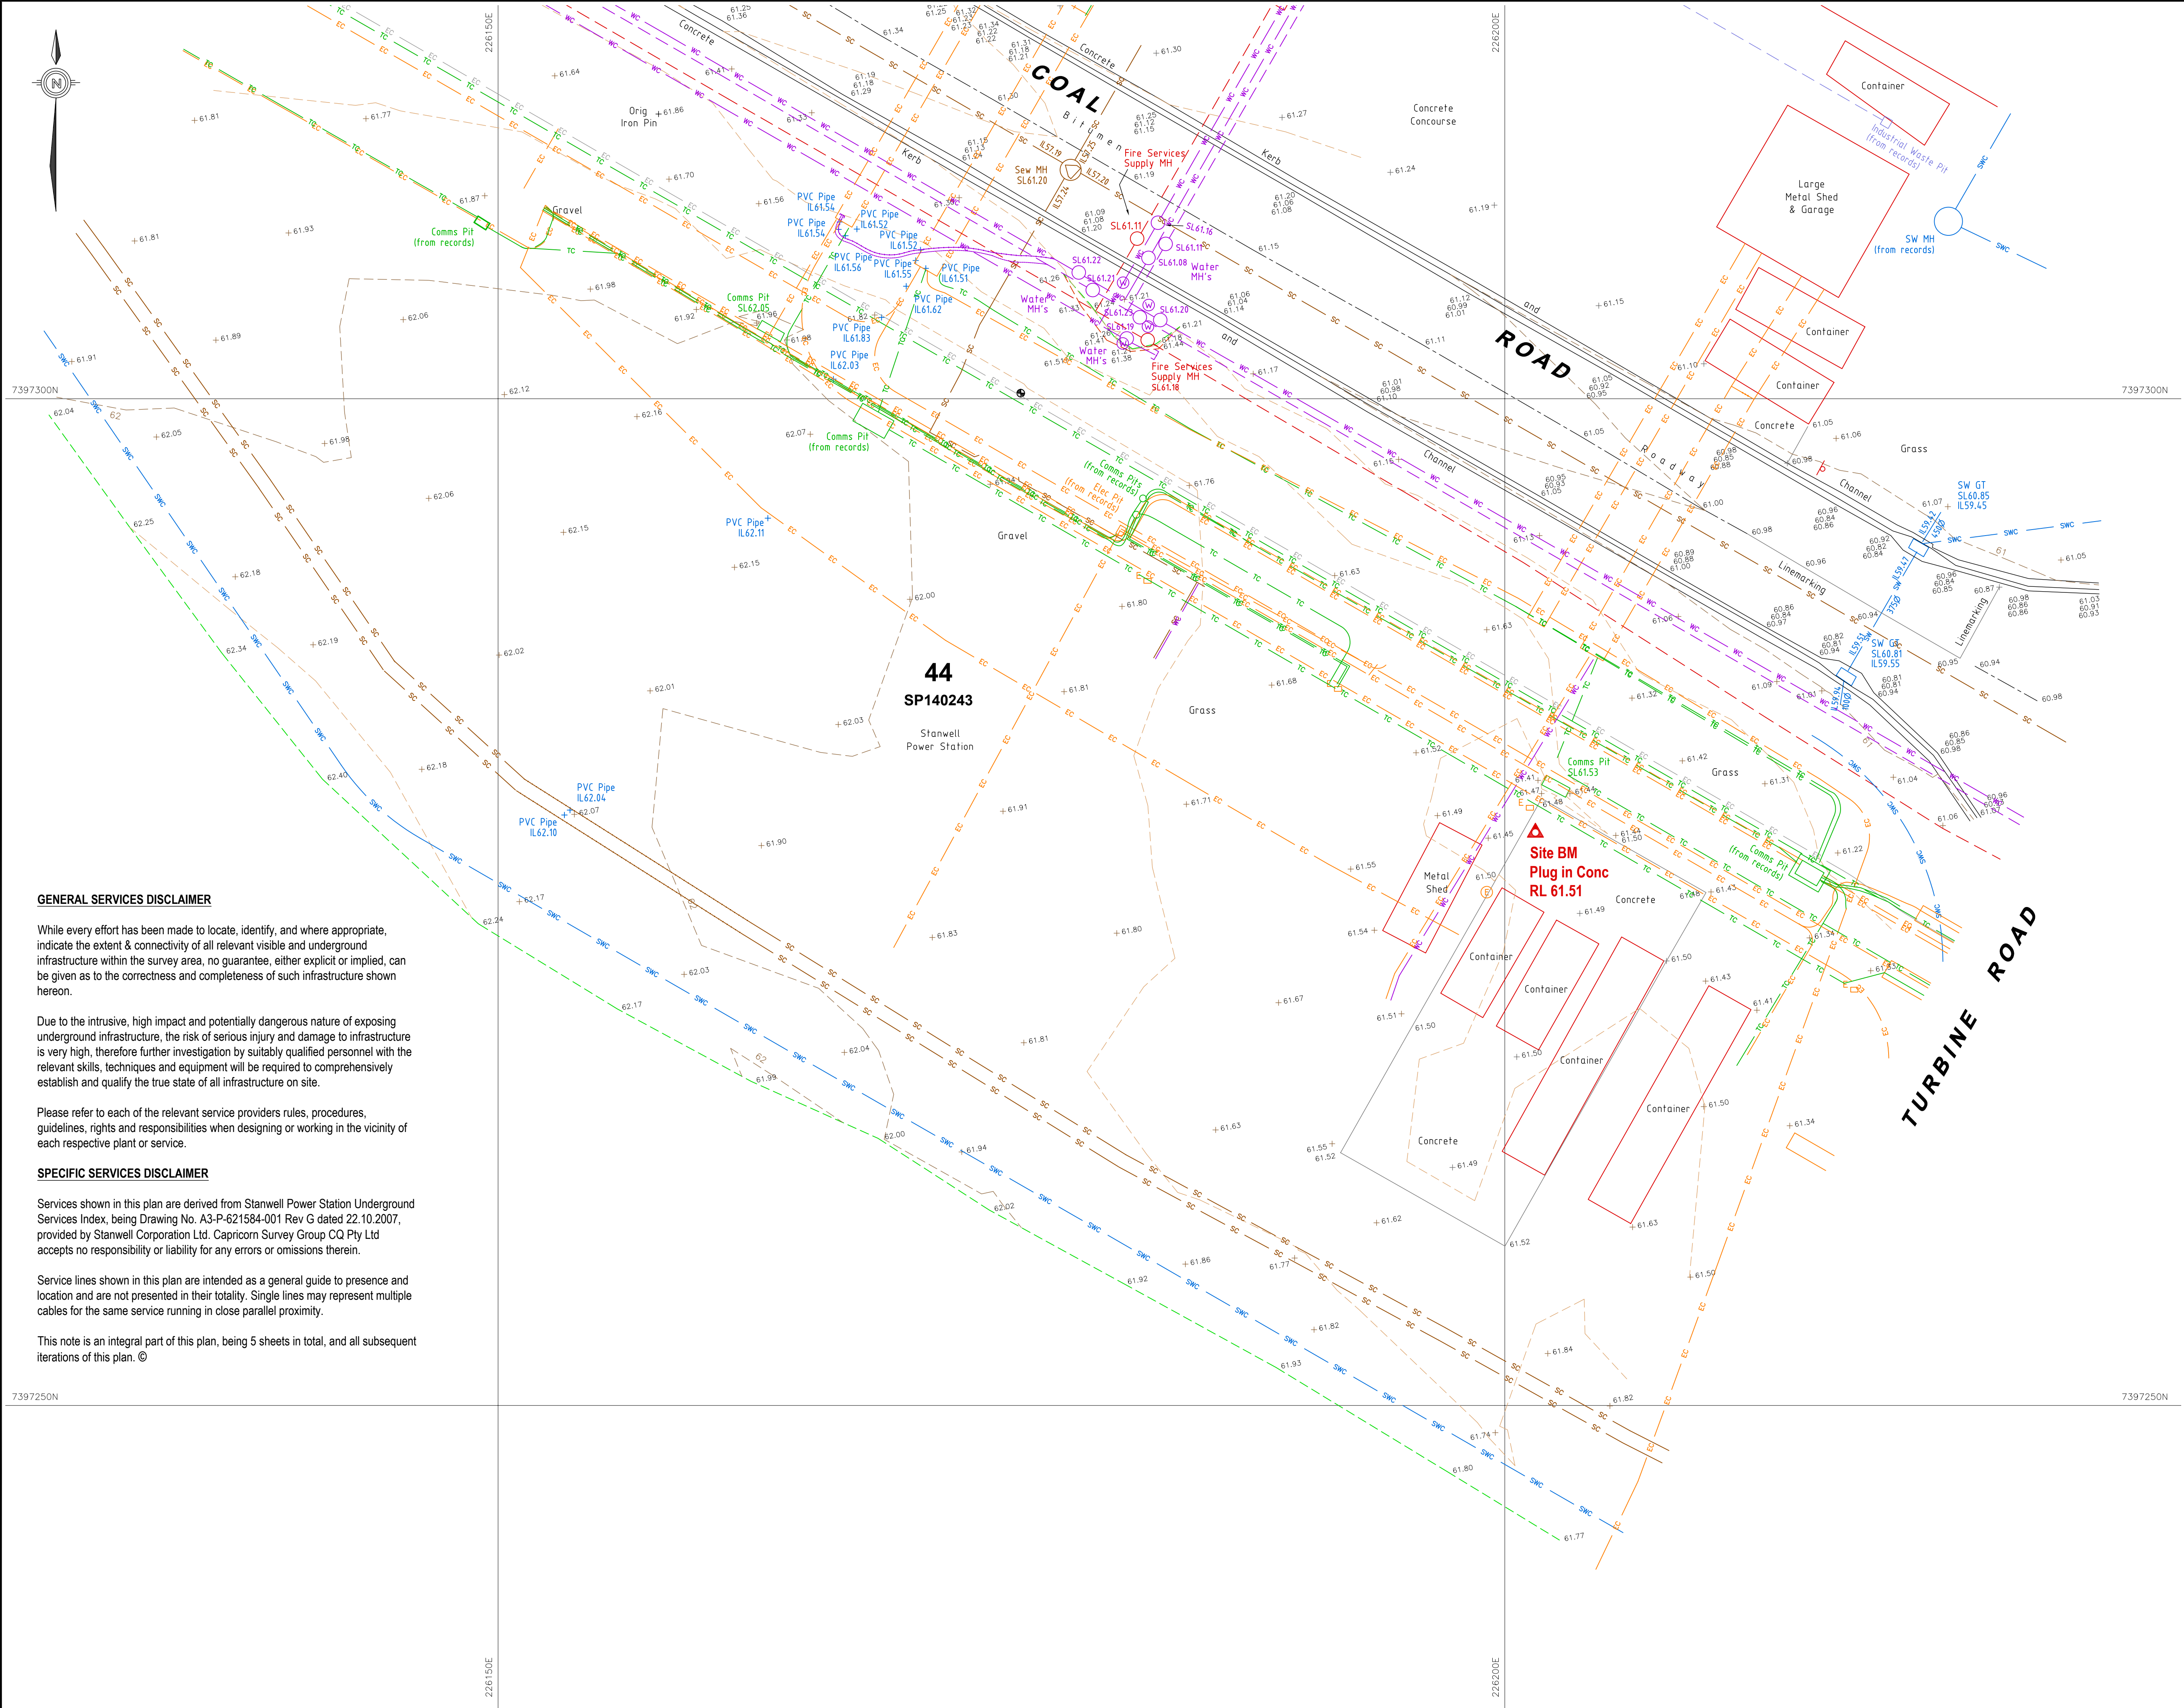

GENERAL SERVICES DISCLAIMER

While every effort has been made to locate, identify, and where appropriate, indicate the extent & connectivity of all relevant visible and underground infrastructure within the survey area, no guarantee, either explicit or implied, can be given as to the correctness and completeness of such infrastructure shown hereon.

Due to the intrusive, high impact and potentially dangerous nature of exposing underground infrastructure, the risk of serious injury and damage to infrastructure is very high, therefore further investigation by suitably qualified personnel with the relevant skills, techniques and equipment will be required to comprehensively establish and qualify the true state of all infrastructure on site.

Please refer to each of the relevant service providers rules, procedures, guidelines, rights and responsibilities when designing or working in the vicinity of each respective plant or service.

SPECIFIC SERVICES DISCLAIMER

Services shown in this plan are derived from Stanwell Power Station Underground Services Index, being Drawing No. A3-P-621584-001 Rev G dated 22.10.2007, provided by Stanwell Corporation Ltd. Capricorn Survey Group CQ Pty Ltd accepts no responsibility or liability for any errors or omissions therein.

Service lines shown in this plan are intended as a general guide to presence and location and are not presented in their totality. Single lines may represent multiple cables for the same service running in close parallel proximity.

This note is an integral part of this plan, being 5 sheets in total, and all subsequent iterations of this plan. ©

DEZIGN ELEMENTS

PARTIAL DETAIL SURVEY OF
LOT 44 ON SP140243

STANWELL POWER STATION
397 POWER STATION ROAD,
STANWELL

REAL PROPERTY DESCRIPTION
Lot/Plan : Lot 44 on SP140243
Area : 1118 ha (Deed)
Locality : Stanwell
Local Authority : Rockhampton Regional Council

NOTES
This plan was prepared for DEZIGN ELEMENTS from field survey for the purpose of designing new constructions on the subject land and should not be used by any other persons for any other purpose.

Property boundaries have not been reinstated or marked at the time of survey and are approximate only, based on appropriate boundary connections.

Where possible underground services have been located by field survey. Some services shown hereon are compiled from local authority and service provider plans and/or plans provided by the client and are noted accordingly on the plan.

Prior to any design, excavation or construction on site, the relevant authorities, and a qualified service locator should be engaged to ensure all services that may be affected by any future works have been located.

These plans have been prepared as verification plots only. Some text RL's have been omitted for clarity. Please refer to the relevant 3D data files for any spatial interrogation requirements.

Any discrepancies should be verified in writing with Capricorn Survey Group (CQ) Pty Ltd.

This note is an integral part of this plan.

LEGEND	
LINETYPE LEGEND	
	UG Sewerage Line
	UG Sewerage Line (Compiled)
	UG Effluent Line (Compiled)
	UG Industrial Waste Line (Compiled)
	UG Stormwater Line
	UG Stormwater Line (Compiled)
	UG Electrical Line (Surveyed)
	UG Electrical Line (Compiled)
	Draused UG Electrical Line (Compiled)
	UG Communication Line
	UG Communication Line (Compiled)
	UG Water Line
	UG Domestic Water Line (Compiled)
	UG Raw Water Line (Compiled)
	UG Sprinkler Piping (Compiled)
	UG Fire Services Pipe (Compiled)
	Top of Bank
	Toe of Bank
	C/L of Bitumen
	Edge of Bitumen
	Line Marking
	Fence Line
	Roof / Guttering
	Eaves
CONTOUR LEGEND	
	0.25m Interval
	1.00m Interval

GENERAL SYMBOL LEGEND	
	Comms Conduit Marker
	Comms Pit
	Elec Conduit Marker
	Elec Turret
	Elec Pit
	Elec Light Bollard
	Elec Light Pole
	Elec Power Pole
	Elec Power Pole + Light
	Elec Power Pole + Transformer
	Elec Stay Point
	Elec Service (Unclass.)
	Gas Marker
	Gas Valve
	Gas Hot Water System
	Sewerage M/H
	Sewerage Vent
	Sewerage IO
	Stormwater M/H
	Stormwater Pit
	Stormwater DP/Kb Outlet
	Stormwater IO
	Water Fire Hydrant
	Water Meter
	Water Valve
	Water Tap
	Water Control Tap
	Water Service (Unclass.)
	Water Conduit Marker
	Water Tapping Band
	Metal Post
	Bollard
	Guide Sign
	Flag Pole
	Australia Post Box
	Shrub

DATUM
Vertical Datum : AHD Vide SmartNet Aus
Horizontal Datum : MGA2020 Vide SmartNet Aus
Contour Interval : 0.25m, 1.0m Index
Co-ord System : MGA2020 Vide SmartNet Aus

WARNING

LOCATION AND CONNECTIVITY OF U/G SERVICES SHOWN HEREON HAVE BEEN DETERMINED BY DIRECT ACCESS OR COMPILED FROM LOCAL AUTHORITY AND SERVICE PROVIDER PLANS ONLY. FURTHER INVESTIGATION MAY BE REQUIRED TO DETERMINE LOCATIONS OF ALL INACCESSIBLE SERVICES.

REVISION				Authorised
Issue	Date	Details		
A	08.12.2025	Initial Issue		RJKF

CREATED

capricornsurveygroupcq
SURVEYING & PLANNING SOLUTIONS

07 4927 5199 | reception@csqcg.com.au | 132 Victoria Parade, Rockhampton QLD 4700

SCALE
1:150 @ A1

DRAWING NUMBER	ISSUE
9813-05-DTL (5/5)	A