

KEY DIAGRAM




IMPORTANT NOTE

Prior to the final design of any proposed improvements in the vicinity of the surveyed area shown hereon, external independent professional service locators will be required to determine the true location of all inaccessible underground services using appropriate methods and equipment, including pot holing where appropriate.

LOCALITY

1:15000

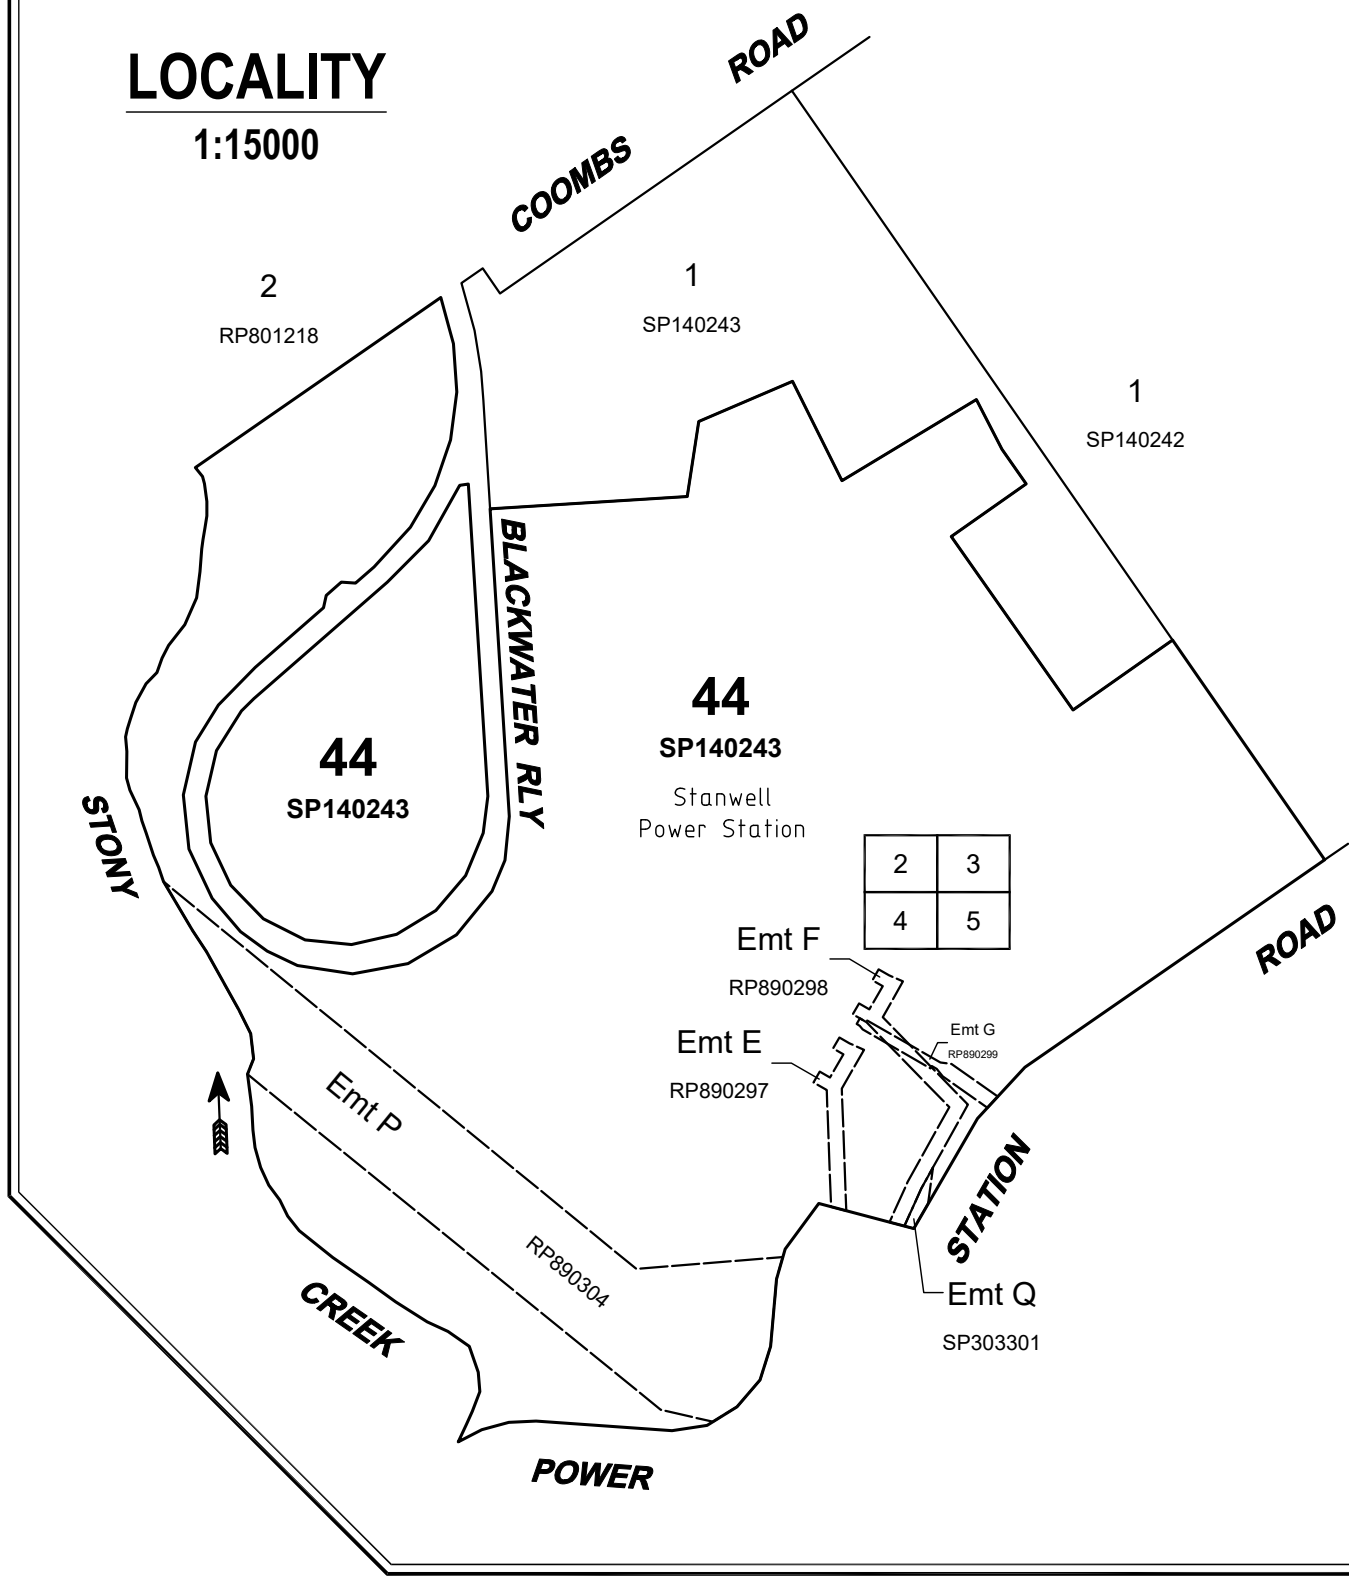

STANWELL CORPORATION LTD

ADDITIONAL DETAIL SURVEY OF
PART OF STANWELL POWER STATION
(NEW PROJECTS OFFICE)

397 POWER STATION ROAD,
STANWELL

Lot/Plan : Lot 44 on SP140243
Area : 1118.2565 ha (Deed)
Locality : Stanwell
Local Authority : Rockhampton Regional Council

This plan was prepared for STANWELL CORPORATION LTD from field survey for the purpose of designing new constructions on the subject land and should not be used by any other persons for any other purpose.

Property boundaries have not been reinstated or marked at the time of survey and are approximate only, based on appropriate boundary connections.

Where possible underground services have been located by field survey. Some services shown hereon are compiled from local authority and service provider plans and/or plans provided by the client and are noted accordingly on the plan.

Prior to any design, excavation or construction on site, the relevant authorities, and a qualified service locator should be engaged to ensure all services that may be affected by any future works have been located.

These plans have been prepared as verification plots only. Some text RL's have been omitted for clarity. Please refer to the relevant 3D data files for any spatial interrogation requirements.

Any discrepancies should be verified in writing with Capricorn Survey Group (CQ) Pty Ltd.

This note is an integral part of this plan.

LINETYPE LEGEND

- UG Sewerage Line
- UG Sewerage Line (Compiled)
- UG Stormwater Line
- UG Stormwater Line (Compiled)
- Overland Flow/Direction
- UG Electrical Line
- UG Electrical Line (Compiled)
- OH Electrical Line
- UG Communication Line
- UG Communication Line (Compiled)
- UG Water Line
- UG Water Line (Compiled)
- AG Water Line
- UG Gas Line
- UG Gas Line (Compiled)
- Top of Bank
- Toe of Bank
- CL of Bitumen
- Edge of Bitumen
- Retaining Wall
- Line Marking
- Fence Line
- Roof / Guttering
- Eaves

CONTOUR LEGEND

- 0.25m Interval
- 1.00m Interval

GENERAL SYMBOL LEGEND

- Comms Conduit Marker
- Comms Pit
- Elec Conduit Marker
- Elec Turret
- Elec Pit
- Elec Light Bollard
- Elec Light Pole
- Elec Power Pole
- Elec Power Pole + Light
- Elec Power Pole + Transformer
- Elec Stay Point
- Traffic Lights
- Gas Marker
- Gas Valve
- Gas Hot Water System
- Sewerage MIH
- Sewerage Vent
- Sewerage IO
- Stormwater MIH
- Stormwater Pit
- Stormwater Kerb Outlet
- Stormwater IO
- Water Fire Hydrant
- Water Meter
- Water Valve
- Water Tap
- Water Control Tap
- Water Tee
- Water Conduit Marker
- Water Tapping Band
- Post
- Bollard
- Guide Sign
- Flag Pole
- Australia Post Box
- Shrub

DATUM

Vertical Datum : AHD Vide PM70424 RL 60.69
Horizontal Datum : MGA2020 Vide PM70424
Contour Interval : 0.25m, 1.0m Index
Co-ord System : MGA2020 Vide PM70424

WARNING

LOCATION AND CONNECTIVITY OF U/G SERVICES SHOWN
HEREON HAVE BEEN DETERMINED BY DIRECT ACCESS OR
COMPILED FROM LOCAL AUTHORITY AND SERVICE PROVIDER
PLANS ONLY. FURTHER INVESTIGATION MAY BE REQUIRED TO
DETERMINE LOCATIONS OF ALL INACCESSIBLE SERVICES.

REVISION

Issue	Date	Details	Authorised
A	2-06-2025	Initial Issue	RJKF

CREATED

capricornsurveygroup
SURVEYING & PLANNING SOLUTIONS

07 4927 5199 | reception@csagroup.com.au | 132 Victoria Parade, Rockhampton QLD 4700

SCALE

1:1250 @ A1

DRAWING NUMBER

9555-40-DTL (1/5)

ISSUE

A


SERVICES DISCLAIMER

While every effort has been made to locate, identify, and where appropriate, indicate the extent & connectivity of all relevant visible and underground infrastructure within the survey area, no guarantee, either explicit or implied, can be given as to the correctness and completeness of such infrastructure shown hereon.

Due to the intrusive, high impact and potentially dangerous nature of exposing underground infrastructure, the risk of serious injury and damage to infrastructure is very high, therefore further investigation by suitably qualified personnel with the relevant skills, techniques and equipment will be required to comprehensively establish and qualify the true state of all infrastructure on site.

Please refer to each of the relevant service providers rules, procedures, guidelines, rights and responsibilities when designing or working in the vicinity of each respective plant or service.

This note is an integral part of this plan, being 5 sheets in total, and all subsequent iterations of this plan. ©

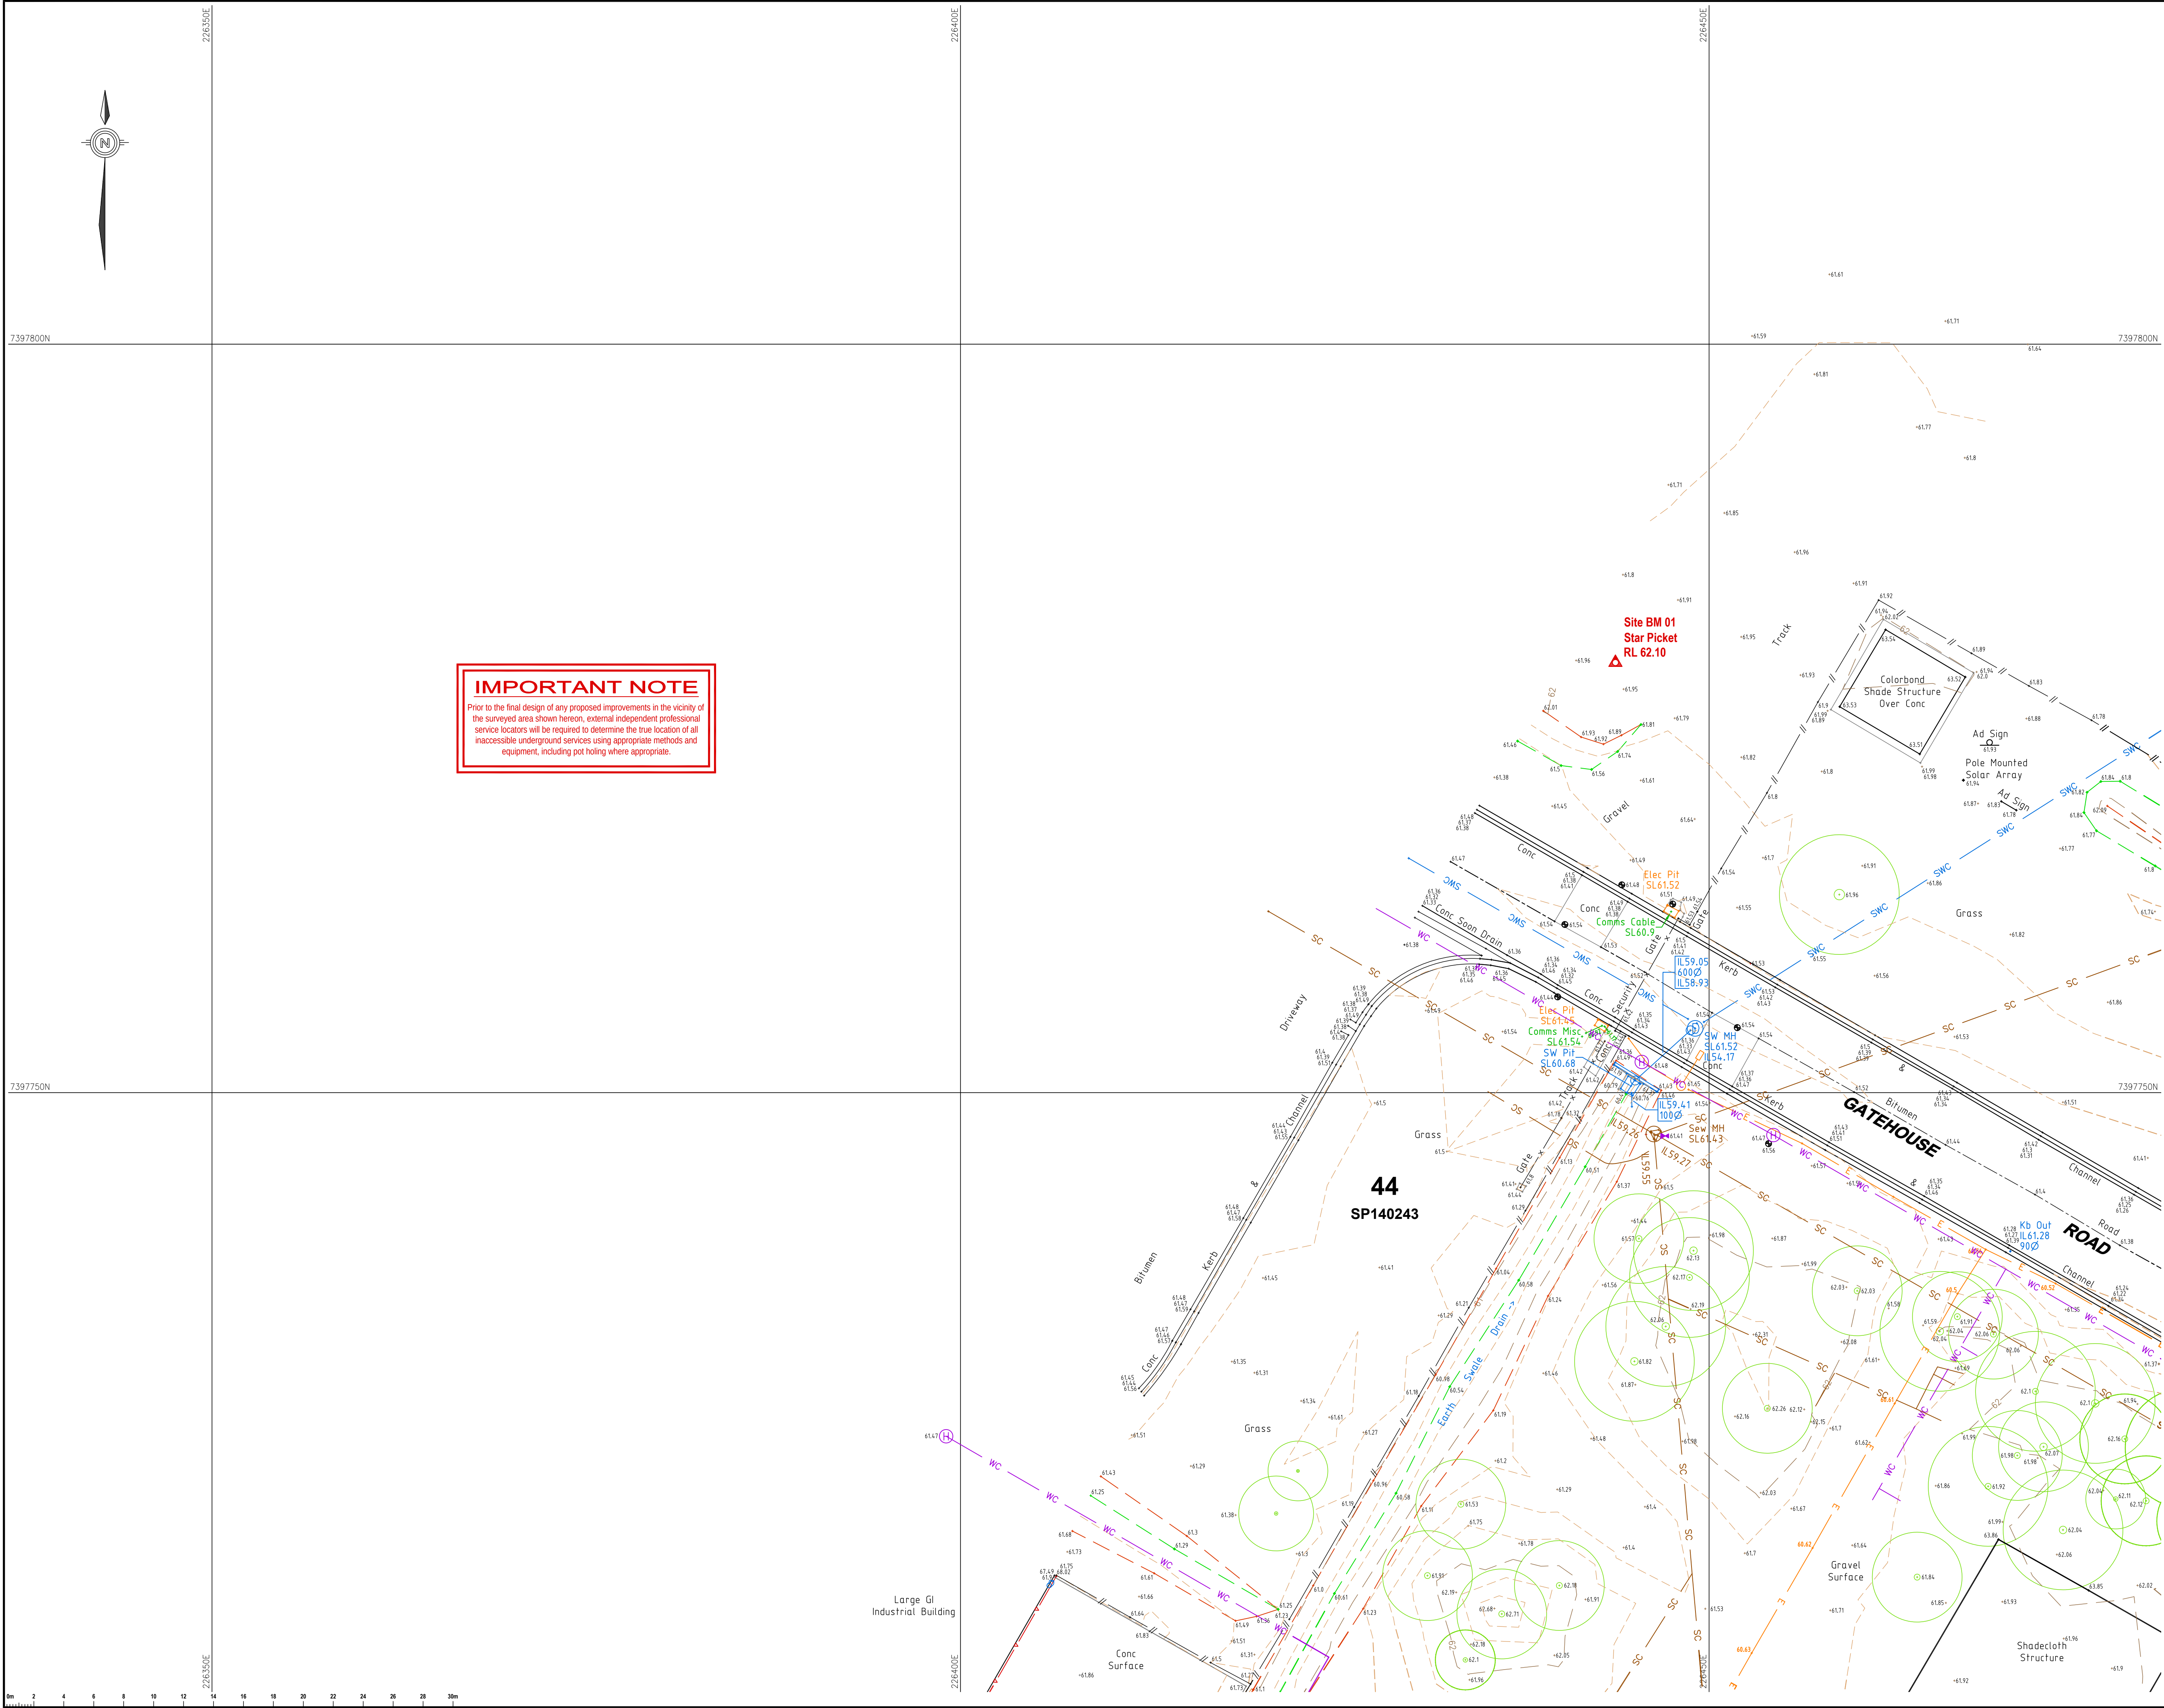

IMPORTANT NOTE
Prior to the final design of any proposed improvements in the vicinity of the surveyed area shown hereon, external independent professional service locators will be required to determine the true location of all inaccessible underground services using appropriate methods and equipment, including pot holing where appropriate.

STANWELL CORPORATION LTD

DESCRIPTION

ADDITIONAL DETAIL SURVEY OF
PART OF STANWELL POWER STATION
(NEW PROJECTS OFFICE)

397 POWER STATION ROAD,
STANWELL

REAL PROPERTY DESCRIPTION

Lot/Plan : Lot 44 on SP140243
Area : 1118.2565 ha (Deed)
Locality : Stanwell
Local Authority : Rockhampton Regional Council

NOTES

This plan was prepared for STANWELL CORPORATION LTD from field survey for the purpose of designing new constructions on the subject land and should not be used by any other persons for any other purpose.

Property boundaries have not been reinstated or marked at the time of survey and are approximate only, based on appropriate boundary connections.

Where possible underground services have been located by field survey. Some services shown hereon are compiled from local authority and service provider plans and/or plans provided by the client and are noted accordingly on the plan.

Prior to any design, excavation or construction on site, the relevant authorities, and a qualified service locator should be engaged to ensure all services that may be affected by any future works have been located.

These plans have been prepared as verification plots only. Some text RL's have been omitted for clarity. Please refer to the relevant 3D data files for any spatial interrogation requirements.

Any discrepancies should be verified in writing with Capricorn Survey Group (CQ) Pty Ltd.

This note is an integral part of this plan.

LEGEND

LINETYPE LEGEND

S

UG Sewerage Line

SC

UG Sewerage Line (Compiled)

SW

UG Stormwater Line

SWC

UG Stormwater Line (Compiled)

Overland Flow/Direction

Overland Flow/Direction

E

UG Electrical Line

EC

UG Electrical Line (Compiled)

T

UG Communication Line

TC

UG Communication Line (Compiled)

WC

UG Water Line (Compiled)

W

AG Water Line

G

UG Gas Line

GC

UG Gas Line (Compiled)

Top of Bank

Top of Bank

Toe of Bank

Toe of Bank

CIL of Bitumen

CIL of Bitumen

Edge of Bitumen

Edge of Bitumen

Retaining Wall

Retaining Wall

Line Marking

Line Marking

///

Fence Line

△

Roof / Guttering

○

Eaves

CONTOUR LEGEND

0.25m Interval

0.25m Interval

1.00m Interval

1.00m Interval

GENERAL SYMBOL LEGEND

Comms Conduit Marker

Comms Pit

Elec Conduit Marker

Elec Turret

Elec Pit

Elec Light Bollard

Elec Light Pole

Elec Power Pole

Elec Power Pole + Light

Elec Power Pole + Transformer

Elec Stay Point

Traffic Lights

Gas Marker

Gas Valve

Gas Hot Water System

Sewerage MIH

Sewerage Vent

Sewerage IO

Stormwater MH

Stormwater Pit

Stormwater Kerb Outlet

Stormwater IO

Water Fire Hydrant

Water Meter

Water Valve

Water Tap

Water Control Tap

Water Tee

Water Conduit Marker

Water Tapping Band

Post

Bollard

Guide Sign

Flag Pole

Australia Post Box

Shrub

DATUM

Vertical Datum : AHD Vide PM70424 RL 60.69

Horizontal Datum : MGA2020 Vide PM70424

Contour Interval : 0.25m, 1.0m Index

Co-ord System : MGA2020 Vide PM70424

WARNING

LOCATION AND CONNECTIVITY OF U/G SERVICES SHOWN
HEREON HAVE BEEN DETERMINED BY DIRECT ACCESS OR
COMPILED FROM LOCAL AUTHORITY AND SERVICE PROVIDER
PLANS ONLY. FURTHER INVESTIGATION MAY BE REQUIRED TO
DETERMINE LOCATIONS OF ALL INACCESSIBLE SERVICES.

REVISION

Issue	Date	Details	Authorised
A	2-06-2025	Initial Issue	RJKF

CREATED

capricornsurveygroupcqc
SURVEYING & PLANNING SOLUTIONS
07 4927 5199 | reception@csqcqc.com.au | 132 Victoria Parade, Rockhampton QLD 4700

SCALE


1:200 @ A1

DRAWING NUMBER

9555-40-DTL (2/5)

ISSUE

A

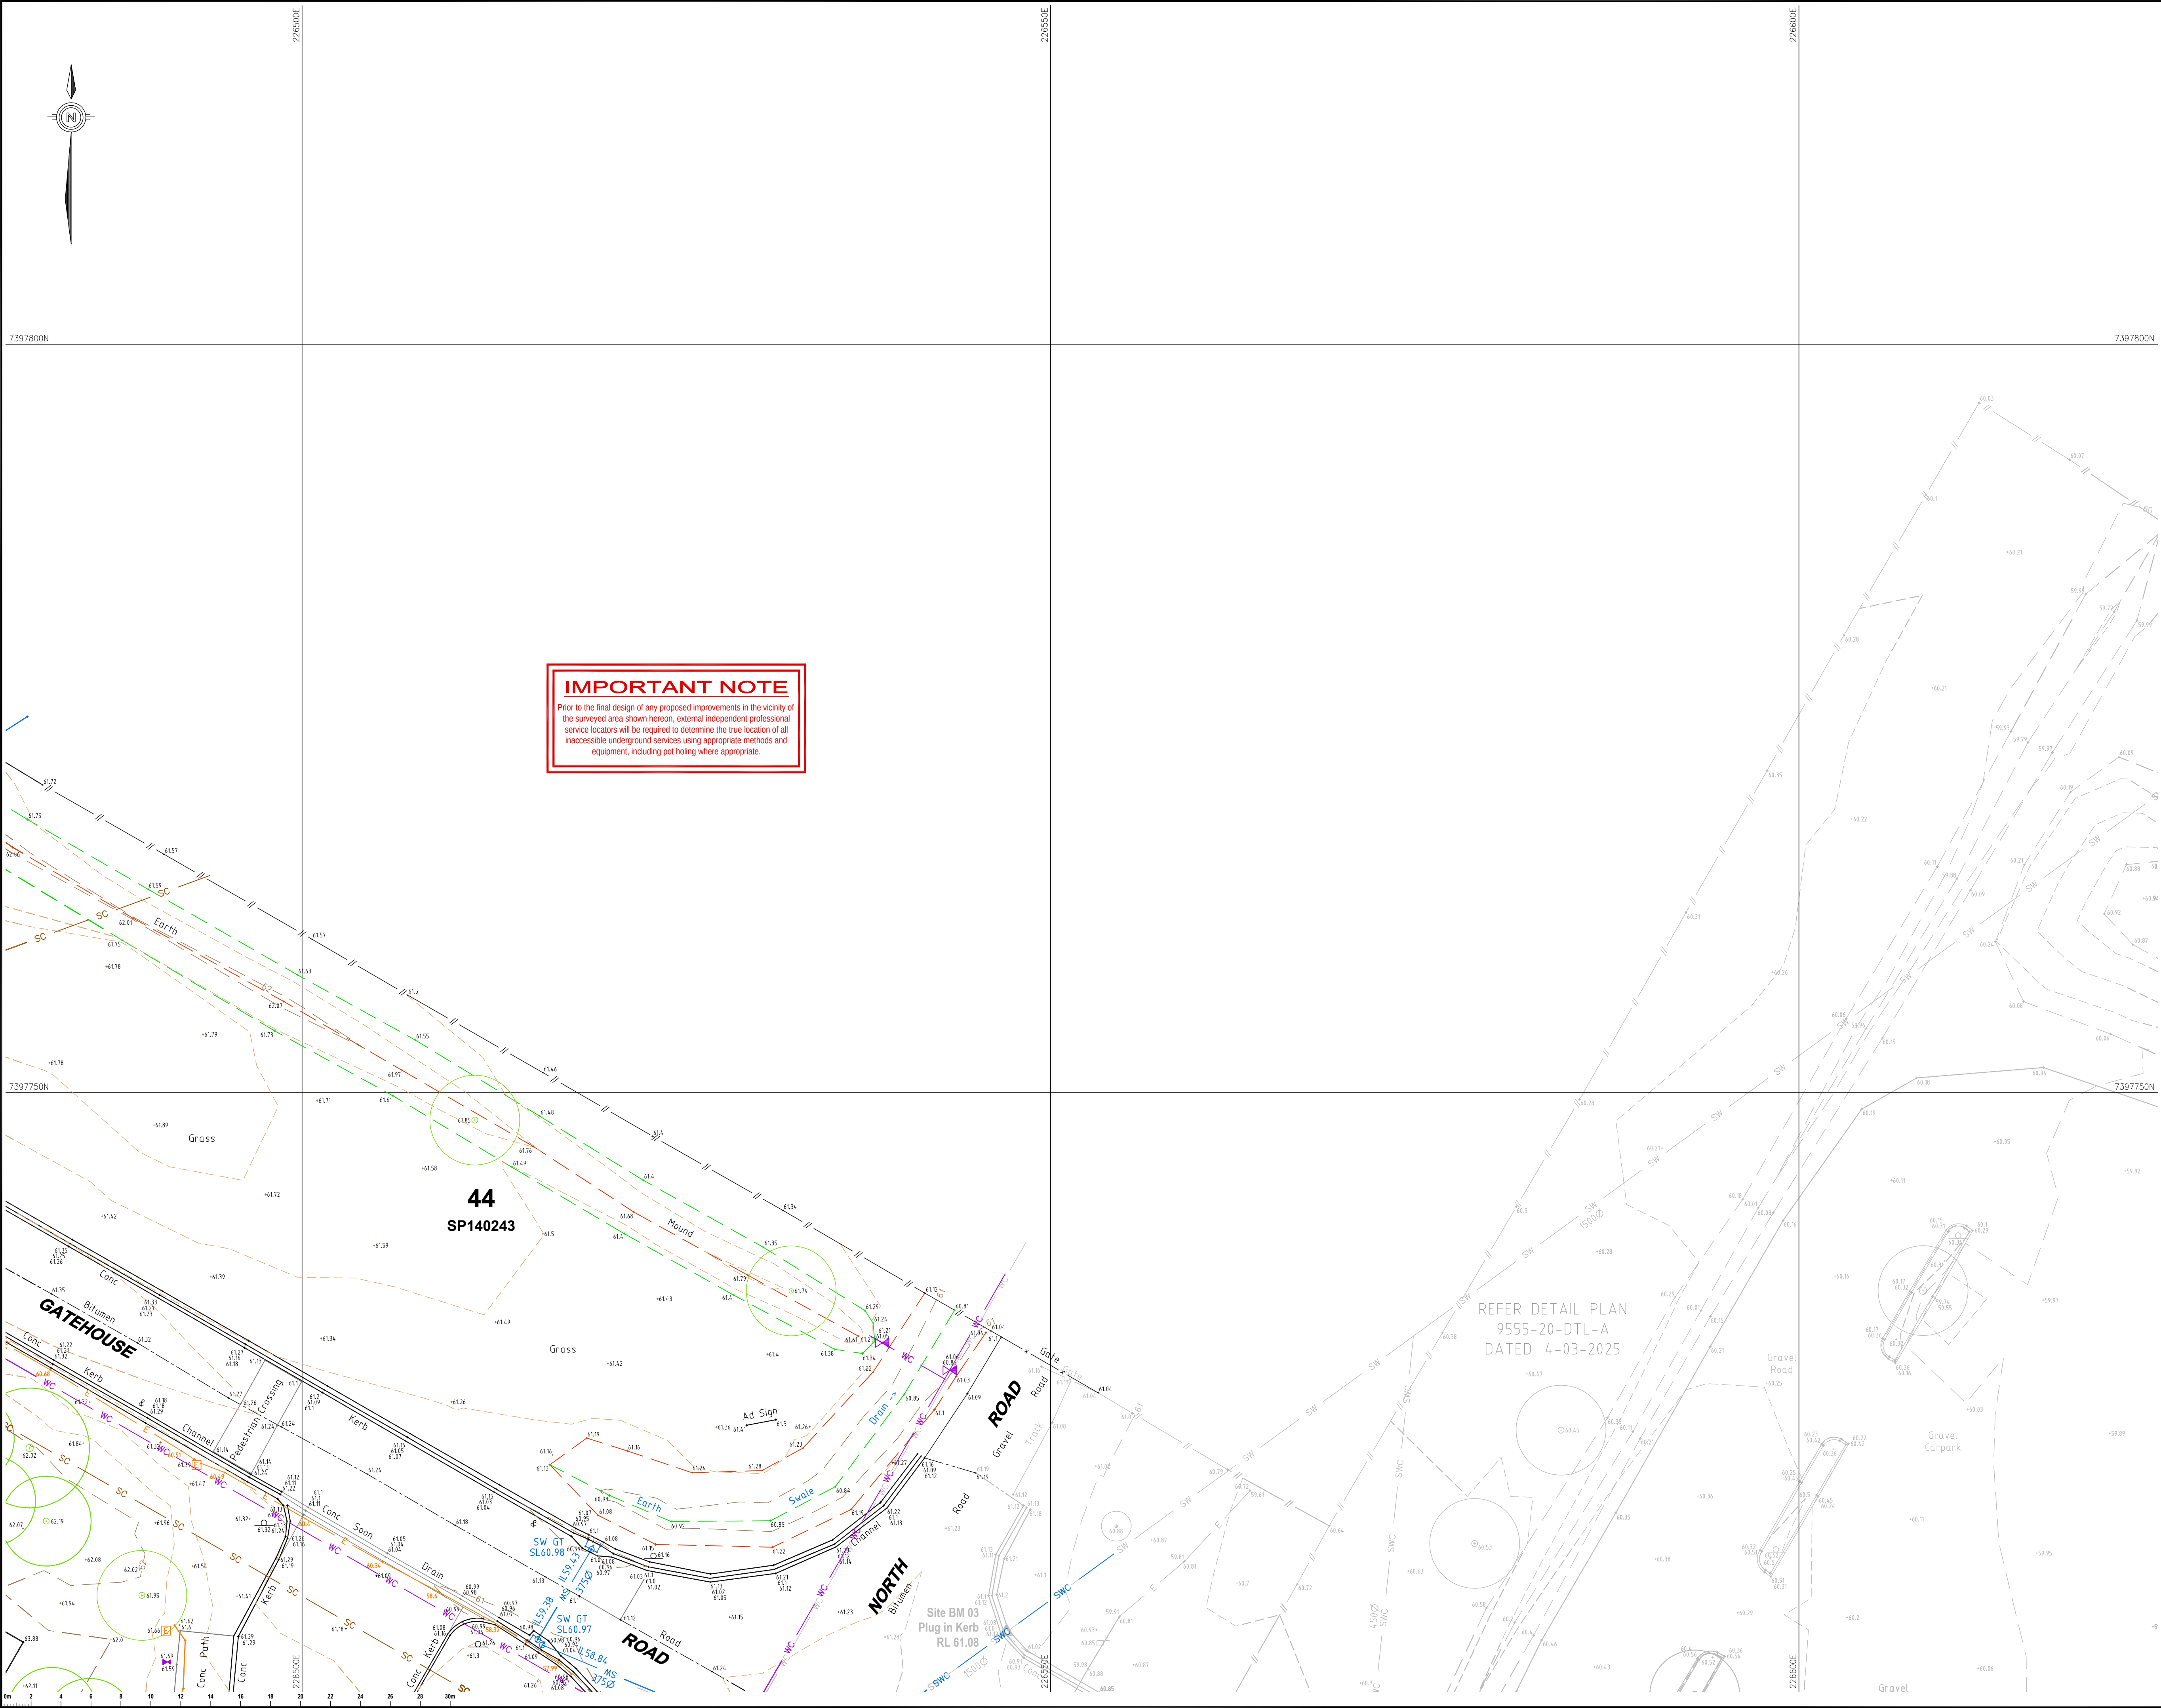

IMPORTANT NOTE
Prior to the final design of any proposed improvements in the vicinity of the surveyed area shown hereon, external independent professional service locators will be required to determine the true location of all inaccessible underground services using appropriate methods and equipment, including pot holing where appropriate.

PRINCIPAL

STANWELL CORPORATION LTD

DESCRIPTION

ADDITIONAL DETAIL SURVEY OF
PART OF STANWELL POWER STATION
(NEW PROJECTS OFFICE)

397 POWER STATION ROAD,
STANWELL

REAL PROPERTY DESCRIPTION

Lot/Plan : Lot 44 on SP140243
Area : 1118.2565 ha (Deed)
Locality : Stanwell
Local Authority : Rockhampton Regional Council

NOTES

This plan was prepared for STANWELL CORPORATION LTD from field survey for the purpose of designing new constructions on the subject land and should not be used by any other persons for any other purpose.

Property boundaries have not been reinstated or marked at the time of survey and are approximate only, based on appropriate boundary connections.

Where possible underground services have been located by field survey. Some services shown hereon are compiled from local authority and service provider plans and/or plans provided by the client and are noted accordingly on the plan.

Prior to any design, excavation or construction on site, the relevant authorities, and a qualified service locator should be engaged to ensure all services that may be affected by any future works have been located.

These plans have been prepared as verification plots only. Some text RL's have been omitted for clarity. Please refer to the relevant 3D data files for any spatial interrogation requirements.

Any discrepancies should be verified in writing with Capricorn Survey Group (CQ) Pty Ltd.

This note is an integral part of this plan.

LEGEND

LINETYPE LEGEND

- S UG Sewerage Line
- SC UG Sewerage Line (Compiled)
- SW UG Stormwater Line
- SWC UG Stormwater Line (Compiled)
- Overland Flow/Direction
- E UG Electrical Line
- EC UG Electrical Line (Compiled)
- W UG Water Line
- WC UG Water Line (Compiled)
- W AG Water Line
- G UG Gas Line
- GC UG Gas Line (Compiled)
- Top of Bank
- Toe of Bank
- CIL of Bitumen
- Edge of Bitumen
- Retaining Wall
- Line Marking
- Fence Line
- Roof / Guttering
- Eaves

CONTOUR LEGEND

- 0.25m Interval
- 1.00m Interval

GENERAL SYMBOL LEGEND

- Comms Conduit Marker
- Comms Pit
- Elec Conduit Marker
- Elec Turret
- Elec Pit
- Elec Light Bollard
- Elec Light Pole
- Elec Power Pole
- Elec Power Pole + Light
- Elec Power Pole + Transformer
- Elec Stay Point
- Traffic Lights
- Gas Marker
- Gas Valve
- Gas Hot Water System
- Sewerage MH
- Sewerage Vent
- Sewerage IO
- Stormwater MH
- Stormwater Pit
- Stormwater Kerb Outlet
- Stormwater IO
- Water Fire Hydrant
- Water Meter
- Water Valve
- Water Tap
- Water Control Tap
- Water Tee
- Water Conduit Marker
- Post
- Bollard
- Guide Sign
- Flag Pole
- Australia Post Box
- Shrub

DATUM

Vertical Datum : AHD Vide PM70424 RL 60.69
Horizontal Datum : MGA2020 Vide PM70424
Contour Interval : 0.25m, 1.0m Index
Co-ord System : MGA2020 Vide PM70424

WARNING

LOCATION AND CONNECTIVITY OF UG SERVICES SHOWN
HEREON HAVE BEEN DETERMINED BY DIRECT ACCESS OR
COMPILED FROM LOCAL AUTHORITY AND SERVICE PROVIDER
PLANS ONLY. FURTHER INVESTIGATION MAY BE REQUIRED TO
DETERMINE LOCATIONS OF ALL INACCESSIBLE SERVICES.

REVISION

Issue	Date	Details	Authorised
A	2-06-2025	Initial Issue	RJKF

CREATED

capricornsurveygroupcq
SURVEYING & PLANNING SOLUTIONS
07 4927 5199 | reception@csqcg.com.au | 132 Victoria Parade, Rockhampton QLD 4700

SCALE


1:200 @ A1

DRAWING NUMBER

9555-40-DTL (3/5)

ISSUE

A

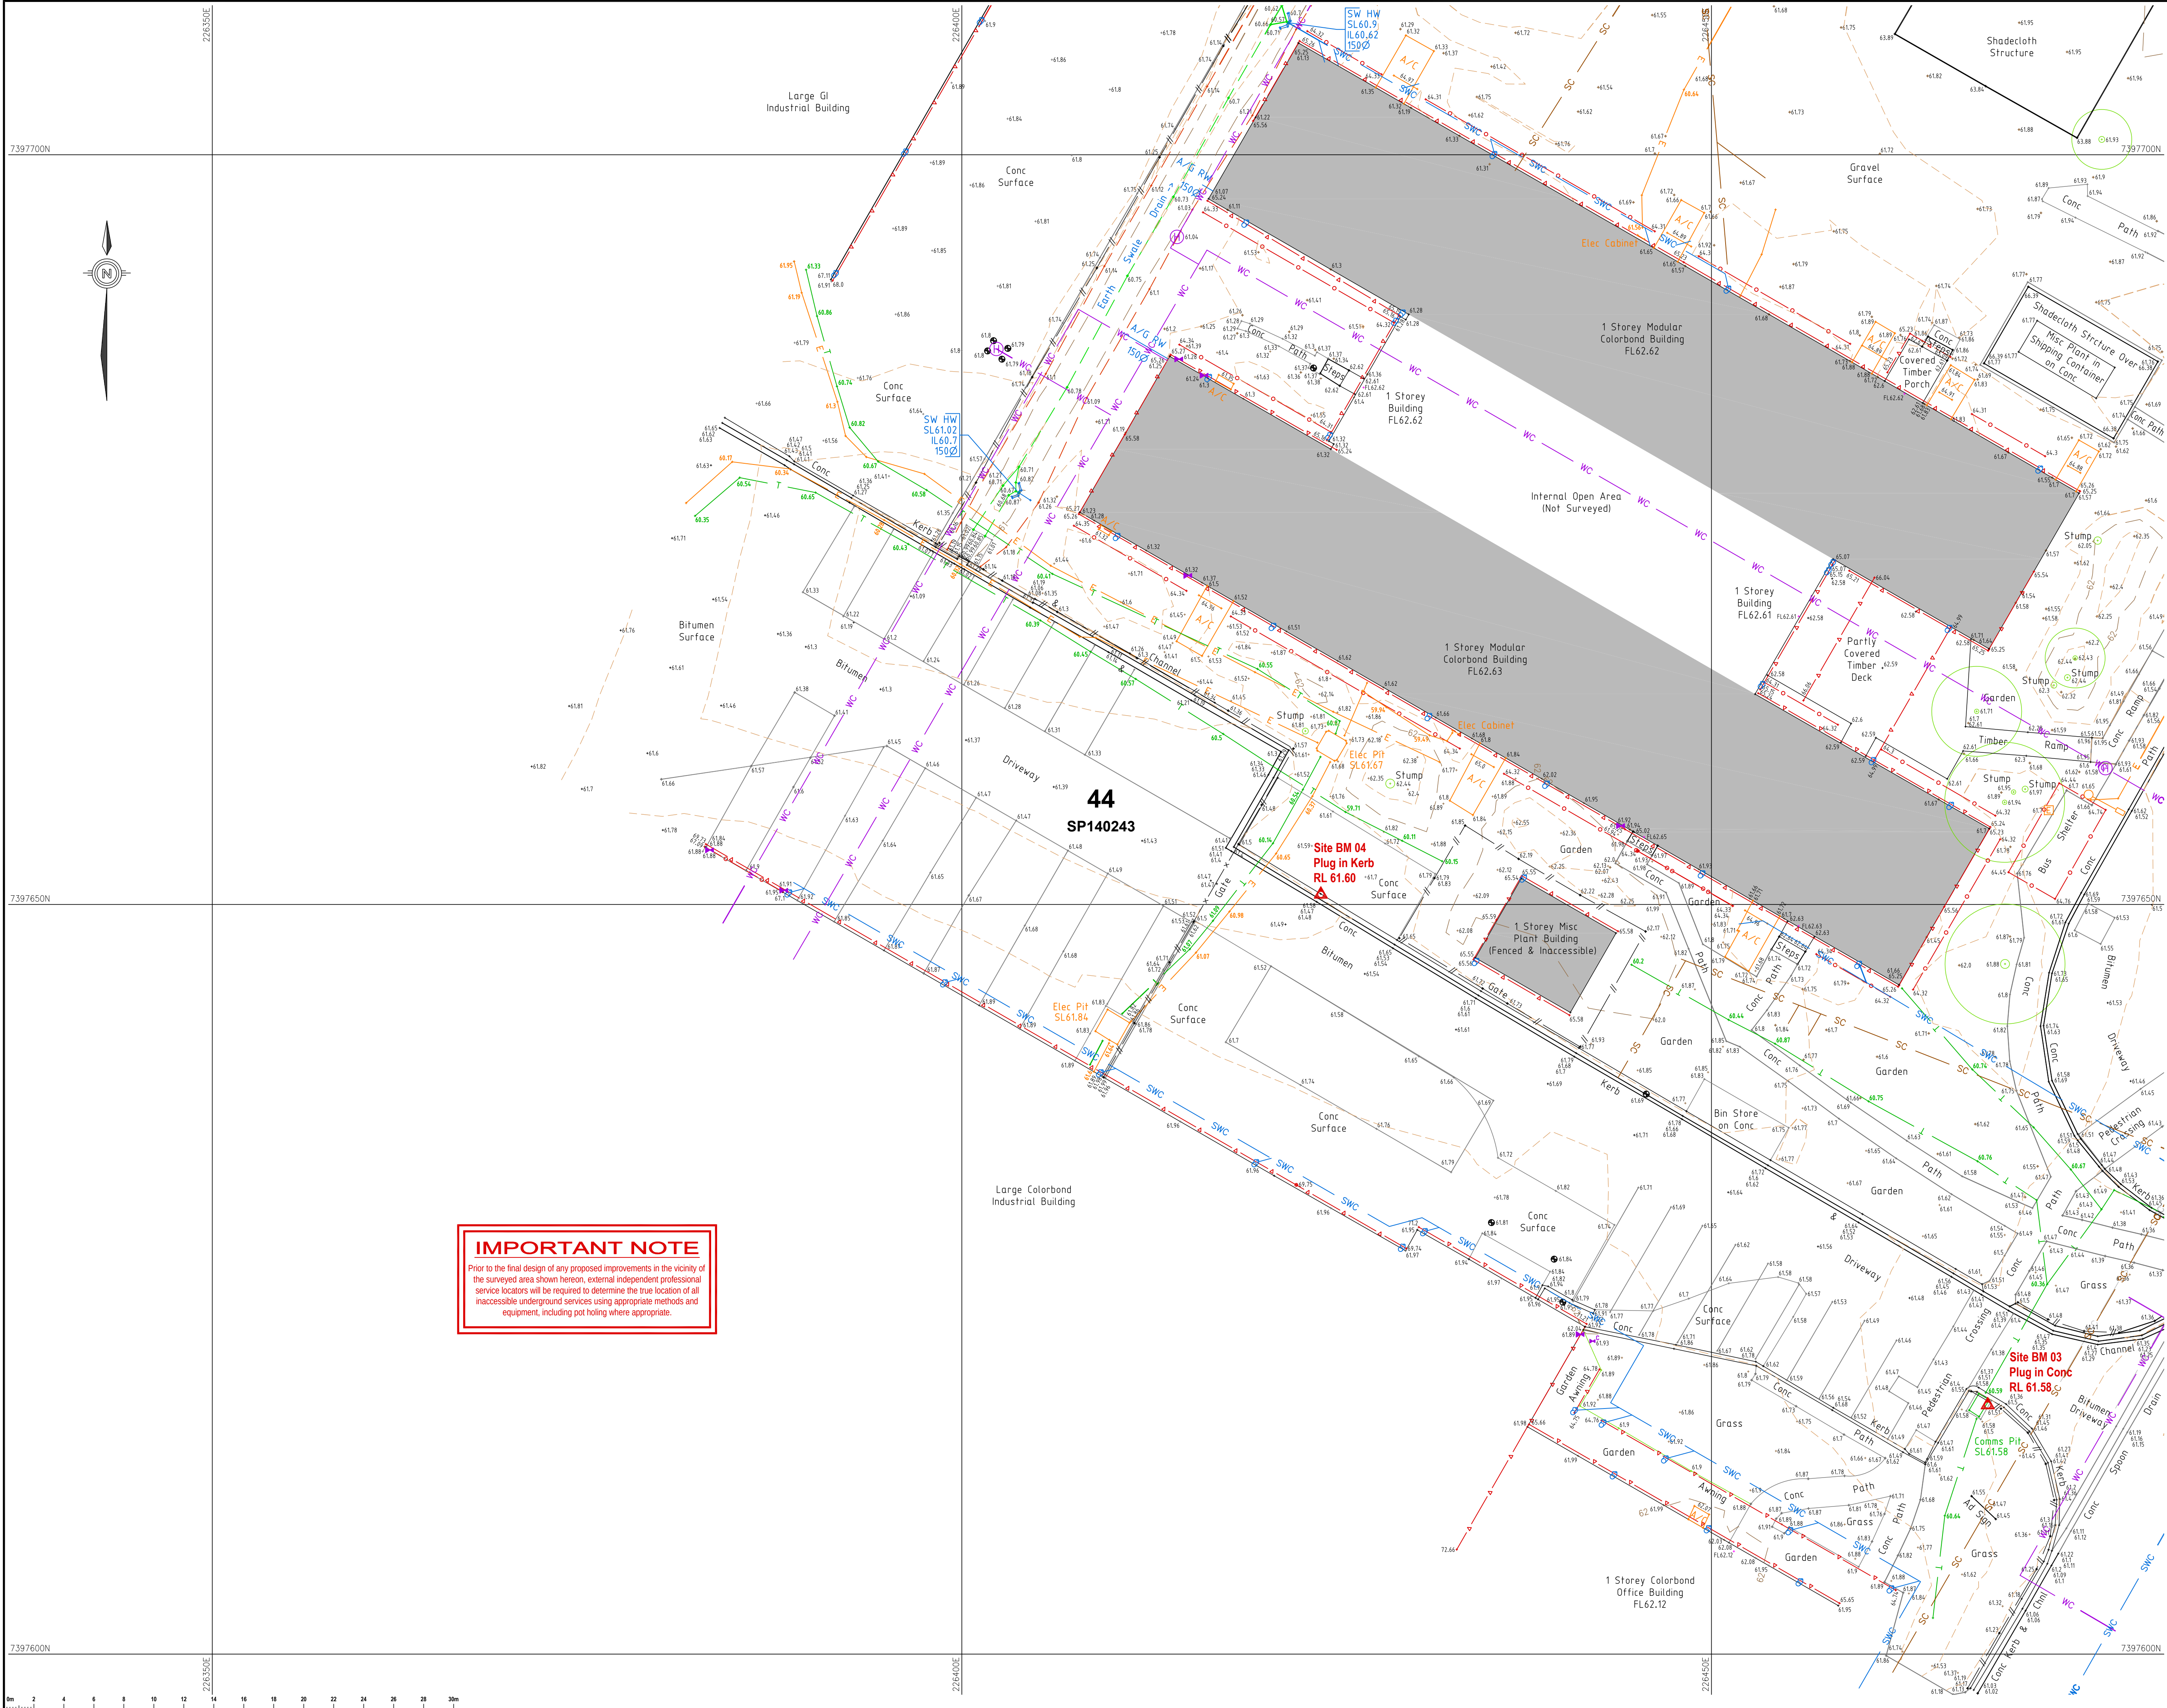

IMPORTANT NOTE
Prior to the final design of any proposed improvements in the vicinity of the surveyed area shown hereon, external independent professional service locators will be required to determine the true location of all inaccessible underground services using appropriate methods and equipment, including pot holing where appropriate.

STANWELL CORPORATION LTD

ADDITIONAL DETAIL SURVEY OF
PART OF STANWELL POWER STATION
(NEW PROJECTS OFFICE)

397 POWER STATION ROAD,
STANWELL

Lot/Plan : Lot 44 on SP140243

Area : 1118.2565 ha (Deed)

Locality : Stanwell

Local Authority : Rockhampton Regional Council

This plan was prepared for STANWELL CORPORATION LTD from field survey for the purpose of designing new constructions on the subject land and should not be used by any other persons for any other purpose.

Property boundaries have not been reinstated or marked at the time of survey and are approximate only, based on appropriate boundary connections.

Where possible underground services have been located by field survey. Some services shown hereon are compiled from local authority and service provider plans and/or plans provided by the client and are noted accordingly on the plan.

Prior to any design, excavation or construction on site, the relevant authorities, and a qualified service locator should be engaged to ensure all services that may be affected by any future works have been located.

These plans have been prepared as verification plots only. Some text RL's have been omitted for clarity. Please refer to the relevant 3D data files for any spatial interrogation requirements.

Any discrepancies should be verified in writing with Capricorn Survey Group (CQ) Pty Ltd.

This note is an integral part of this plan.

LINETYPE LEGEND

S

UG Sewerage Line

SC

UG Sewerage Line (Compiled)

SW

UG Stormwater Line

SWC

UG Stormwater Line (Compiled)

Overland Flow/Direction

UG Electrical Line

E

UG Electrical Line (Compiled)

EC

UG Electrical Line (Compiled)

W

UG Communication Line

TC

UG Communication Line (Compiled)

WC

UG Water Line (Compiled)

W

UG Water Line

G

UG Gas Line

GC

UG Gas Line (Compiled)

Top of Bank

Toe of Bank

CIL of Bitumen

Edge of Bitumen

Retaining Wall

Line Marking

Fence Line

Roof / Gutting

Eaves

CONTOUR LEGEND

0.25m Interval

1.00m Interval

GENERAL SYMBOL LEGEND

Comms Conduit Marker

Stormwater MH

Comms Pit

Stormwater Pit

Elec Conduit Marker

Stormwater Kerb Outlet

Elec Turret

Stormwater IO

Elec Pit

Water Fire Hydrant

Elec Light Bollard

Water Meter

Elec Light Pole

Water Valve

Elec Power Pole

Water Tap

Elec Power Pole + Light

Water Control Tap

Elec Power Pole + Transformer

Water Tee

Elec Stay Point

Water Conduit Marker

Traffic Lights

Post

Gas Marker

Bollard

Gas Valve

Guide Sign

Gas Hot Water System

Flag Pole

Sewerage MH

Australia Post Box

Sewerage Vent

Shrub

Sewerage IO

Vertical Datum : AHD Vide PM70424 RL 60.69

Horizontal Datum : MGA2020 Vide PM70424

Contour Interval : 0.25m, 1.0m Index

Co-ord System : MGA2020 Vide PM70424

WARNING

LOCATION AND CONNECTIVITY OF UG SERVICES SHOWN
HEREON HAVE BEEN DETERMINED BY DIRECT ACCESS OR
COMPILED FROM LOCAL AUTHORITY AND SERVICE PROVIDER
PLANS ONLY. FURTHER INVESTIGATION MAY BE REQUIRED TO
DETERMINE LOCATIONS OF ALL INACCESSIBLE SERVICES.

REVISION	Issue	Date	Details	Authorised
A	2-06-2025	Initial Issue		RJKF

CREATED

capricornsurveygroupcq
SURVEYING & PLANNING SOLUTIONS

07 4927 5199 | reception@csqcg.com.au | 132 Victoria Parade, Rockhampton QLD 4700

SCALE


1:200 @ A1

DRAWING NUMBER

9555-40-DTL (4/5)

ISSUE

A

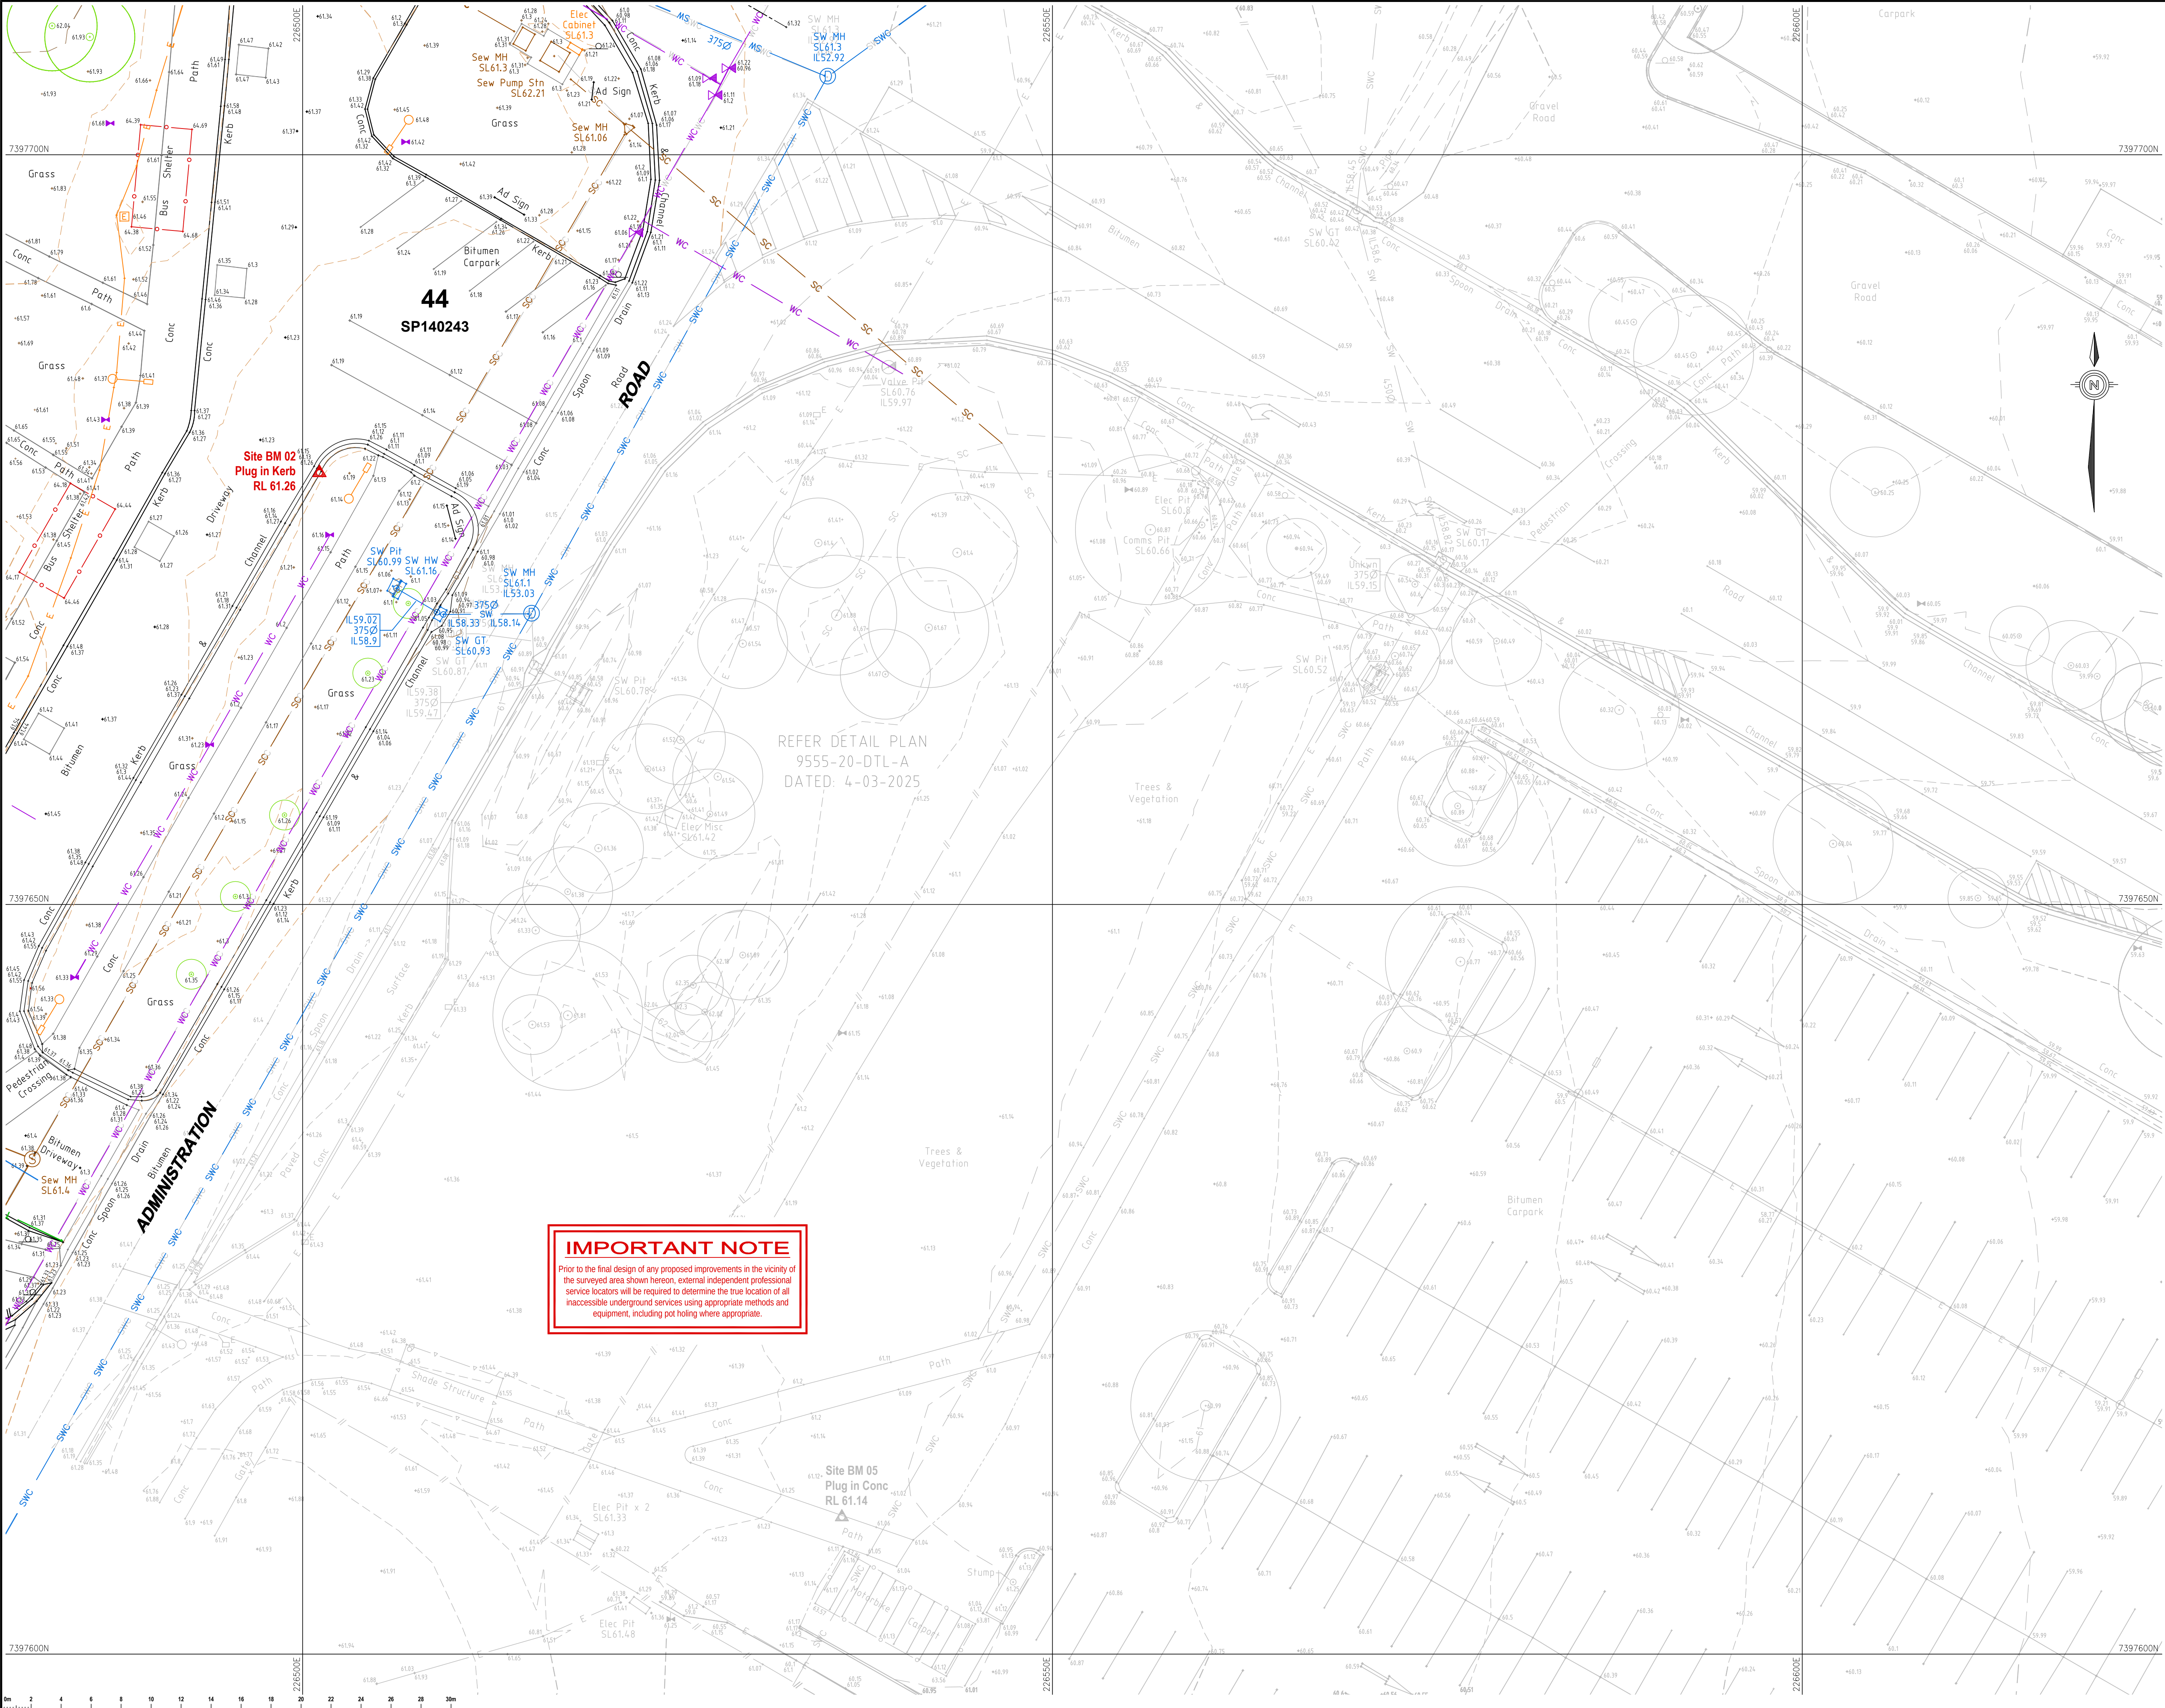

IMPORTANT NOTE
Prior to the final design of any proposed improvements in the vicinity of the surveyed area shown hereon, external independent professional service locators will be required to determine the true location of all inaccessible underground services using appropriate methods and equipment, including pot holing where appropriate.

STANWELL CORPORATION LTD

ADDITIONAL DETAIL SURVEY OF
PART OF STANWELL POWER STATION
(NEW PROJECTS OFFICE)

397 POWER STATION ROAD,
STANWELL

REAL PROPERTY DESCRIPTION

Lot/Plan : Lot 44 on SP140243
Area : 1118.2565 ha (Deed)
Locality : Stanwell
Local Authority : Rockhampton Regional Council

NOTES

This plan was prepared for STANWELL CORPORATION LTD from field survey for the purpose of designing new constructions on the subject land and should not be used by any other persons for any other purpose.

Property boundaries have not been reinstated or marked at the time of survey and are approximate only, based on appropriate boundary connections.

Where possible underground services have been located by field survey. Some services shown hereon are compiled from local authority and service provider plans and/or plans provided by the client and are noted accordingly on the plan.

Prior to any design, excavation or construction on site, the relevant authorities, and a qualified service locator should be engaged to ensure all services that may be affected by any future works have been located.

These plans have been prepared as verification plots only. Some text RL's have been omitted for clarity. Please refer to the relevant 3D data files for any spatial interrogation requirements.

Any discrepancies should be verified in writing with Capricorn Survey Group (CQ) Pty Ltd.

This note is an integral part of this plan.

LEGEND

LINETYPE LEGEND

- S UG Sewerage Line
- SC UG Sewerage Line (Compiled)
- SW UG Stormwater Line
- SWC UG Stormwater Line (Compiled)
- Overland Flow/Direction
- E UG Electrical Line
- EC UG Electrical Line (Compiled)
- W UG Water Line
- WC UG Water Line (Compiled)
- AG UG Gas Line
- G UG Gas Line (Compiled)
- GC UG Gas Line (Compiled)
- Top of Bank
- Toe of Bank
- CIL of Bitumen
- Edge of Bitumen
- Retaining Wall
- Line Marking
- Fence Line
- Roof / Gutting
- Eaves

CONTOUR LEGEND

- 0.25m Interval
- 1.00m Interval

GENERAL SYMBOL LEGEND

- Comms Conduit Marker
- Comms Pit
- Elec Conduit Marker
- Elec Turret
- Elec Pit
- Elec Light Bollard
- Elec Light Pole
- Elec Power Pole
- Elec Power Pole + Light
- Elec Power Pole + Transformer
- Elec Stay Point
- Traffic Lights
- Gas Marker
- Gas Valve
- Gas Hot Water System
- Sewerage MH
- Sewerage Vent
- Sewerage IO
- Stormwater MH
- Stormwater Pit
- Stormwater Kerb Outlet
- Stormwater IO
- Water Fire Hydrant
- Water Meter
- Water Valve
- Water Tap
- Water Control Tap
- Water Tee
- Water Conduit Marker
- Water Tapping Band
- Post
- Bollard
- Guide Sign
- Flag Pole
- Australia Post Box
- Shrub

DATUM

Vertical Datum : AHD Vide PM70424 RL 60.69
Horizontal Datum : MGA2020 Vide PM70424
Contour Interval : 0.25m, 1.0m Index
Co-ord System : MGA2020 Vide PM70424

WARNING

LOCATION AND CONNECTIVITY OF UG SERVICES SHOWN
HEREON HAVE BEEN DETERMINED BY DIRECT ACCESS OR
COMPILED FROM LOCAL AUTHORITY AND SERVICE PROVIDER
PLANS ONLY. FURTHER INVESTIGATION MAY BE REQUIRED TO
DETERMINE LOCATIONS OF ALL INACCESSIBLE SERVICES.

REVISION

Issue	Date	Details	Authorised
A	2-06-2025	Initial Issue	RJF

CREATED

capricornsurveygroupco
SURVEYING & PLANNING SOLUTIONS
07 4927 5199 | reception@csagq.com.au | 132 Victoria Parade, Rockhampton QLD 4700

SCALE

1:200 @ A1

DRAWING NUMBER

9555-40-DTL (5/5)

ISSUE

A