



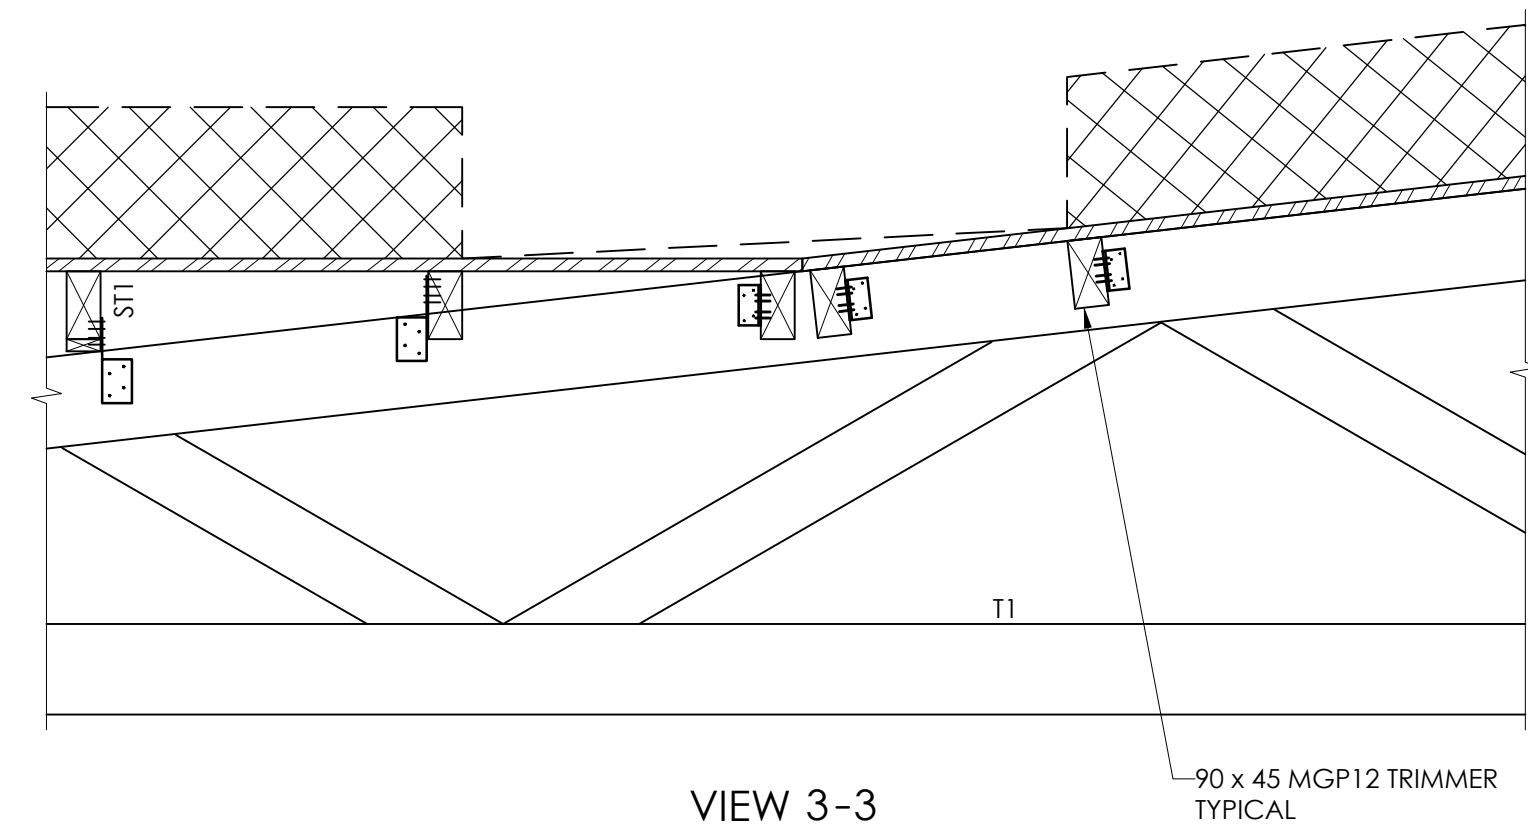


VIEW 3-3

90 x 45 MGP12 TRIMMER
TYPICAL

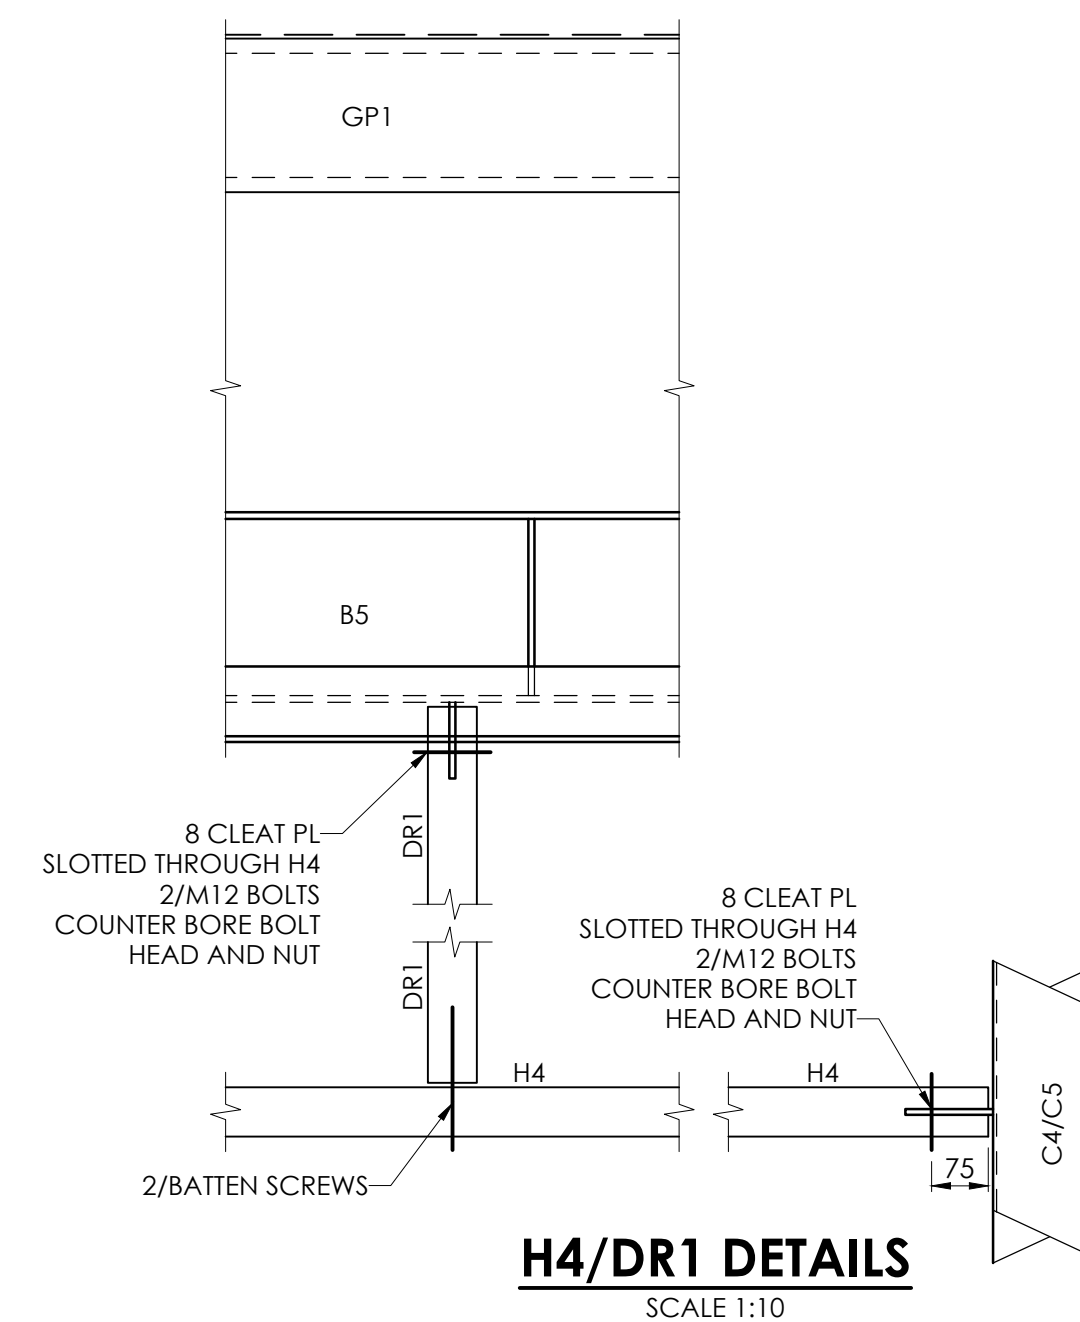


H4/DR1 DETAILS

SCALE 1:10

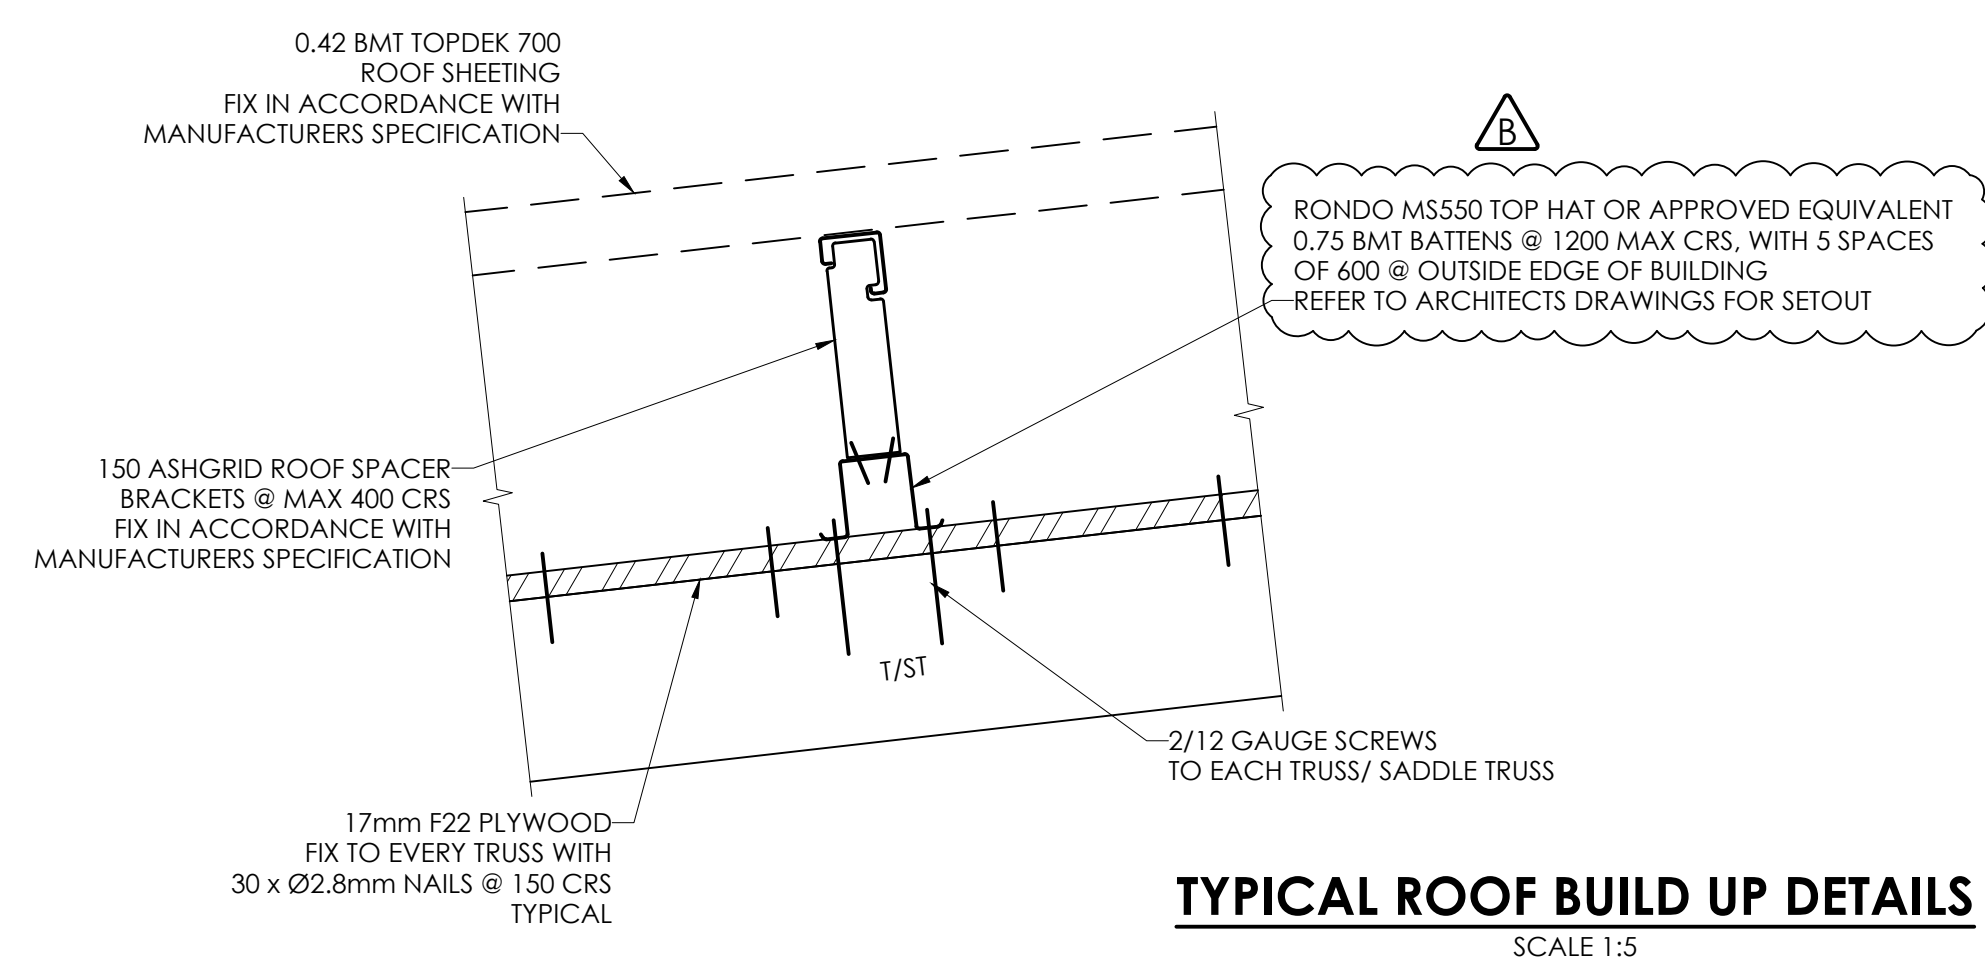

TYPICAL ROOF BUILD UP DETAILS


SCALE 1:5

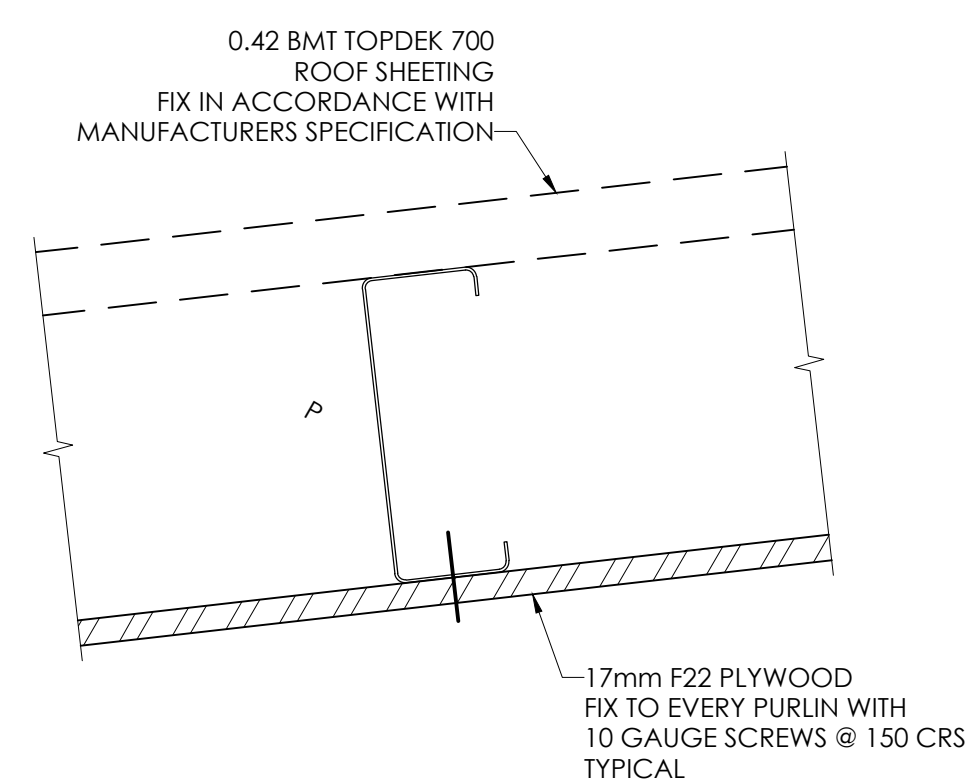[illegible]


GREG JANES R.P.E.Q. 10913

APPROVAL FOR ISSUE FOR AND ON BEHALF OF
JANES AND STEWART STRUCTURES PTY LTD

A1 SHEET - DO NOT SCALE

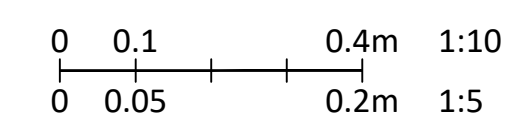

Client
STANWELL

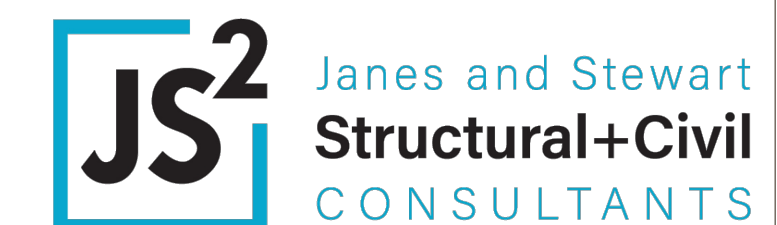

Janes and Stewart Structures Pty Ltd
120 William Street | Po Box 1072
Rockhampton 4700
07 4922 1948
janes.and.stewart@jsstructures.com.au
ABN 30 620 233 025

Project
STANWELL NEW PROJECTS OFFICE

SWITCHYARD ROAD
STANWELL
QUEENSLAND, 4702

TENDER NOT FOR CONSTRUCTION PURPOSES	Project Number 25052
---	-------------------------

ROOF FRAMING DETAILS
SHEET 3

Revision
B