
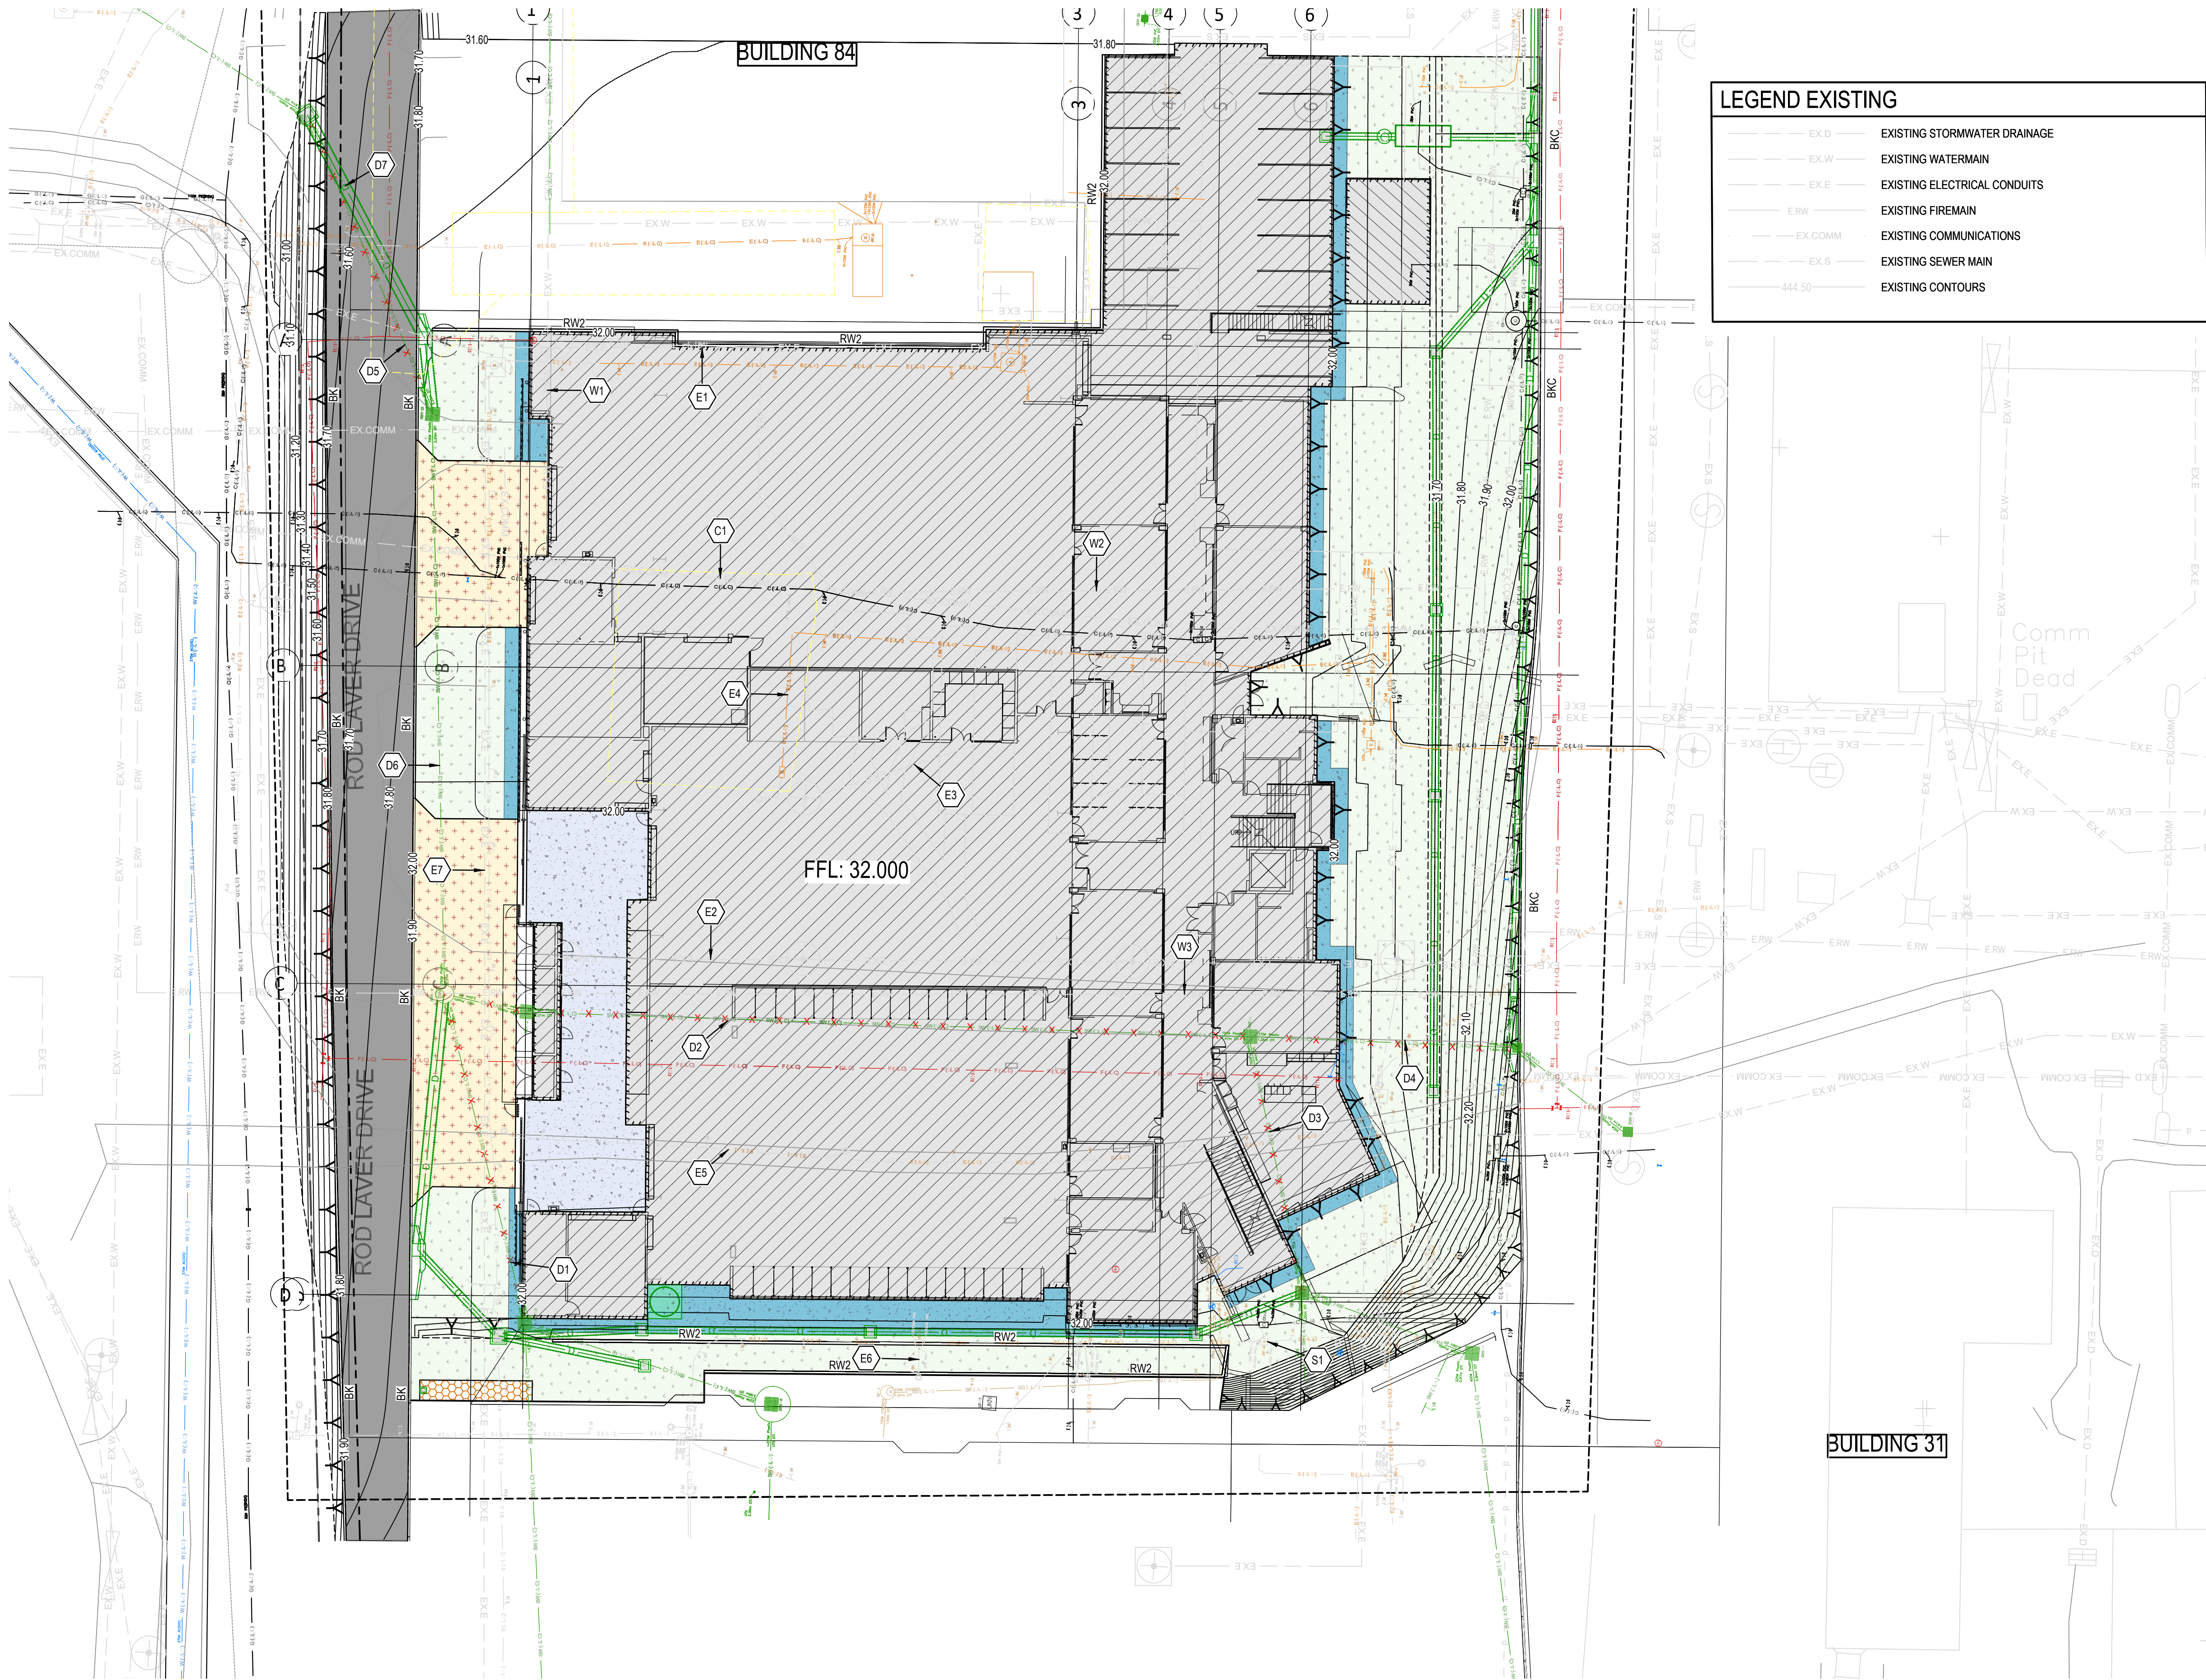


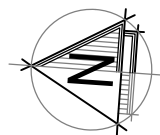

LEGEND EXISTING

- EX.D EXISTING STORMWATER DRAINAGE
- EX.W EXISTING WATERMAIN
- EX.E EXISTING ELECTRICAL CONDUITS
- ERW EXISTING FIREMAIN
- EX.COMM EXISTING COMMUNICATIONS
- EX.S EXISTING SEWER MAIN
- 444.50 EXISTING CONTOURS

LEGEND

- PROPOSED BUILDING AREA
- PROPOSED PAVEMENT TYPE 1
LIGHT DUTY ASPHALT - REFER DWG C140
- PROPOSED PAVEMENT TYPE 2
HEAVY DUTY ASPHALT - REFER DWG C140
- PROPOSED PAVEMENT TYPE 3
HEAVY DUTY CONCRETE - REFER DWG C140
- PROPOSED PAVEMENT TYPE 4
LIGHT DUTY CONCRETE - REFER DWG C140
- PROPOSED LANDSCAPE AREA
REFER LANDSCAPE PLANS FOR DETAILS
- RAINWATER TANK CONCRETE PAVEMENT
- CONTOURS MAJOR
- PROPOSED TOP OF BATTER
- PROPOSED BOTTOM OF BATTER
- PROPOSED BARRIER KERB AND CHANNEL
- PROPOSED BARRIER KERB
- PROPOSED BLOCK RETAINING WALL
- ITEMS / SERVICES TO BE REMOVED
- PROPOSED PAVEMENT LEVEL
- PROPOSED SURFACE LEVEL
- PROPOSED ROOFWATER DRAINAGE PIPE
- PROPOSED SUBSOL DRAINAGE
- PROPOSED STORMWATER DRAINAGE PIPE AND MANHOLE
- PROPOSED HEADWALL AND ROCK OUTLET PROTECTION
- PROPOSED TABLEDRAIN
- PROPOSED WATER PIPE
- PROPOSED ELECTRICAL CONDUIT/CABLES
- REFER NOTE 1 FOR DETAILS

- D1, D2, D3 EXISTING STORMWATER PIPE AND END STRUCTURES TO BE DEMOLISHED. END STRUCTURES TO BE CAPPED PRIOR TO REMOVAL.
- D4, D5 EXISTING STORMWATER PIPE AND END STRUCTURES TO BE DEMOLISHED. END STRUCTURES TO BE CAPPED PRIOR TO REMOVAL.
- D6 EXISTING STORMWATER PIPE TO BE CONNECTED INTO PROPOSED NETWORK. PIPE SIZE AND CONDITION TO BE VERIFIED VIA CCTV PRIOR TO CONSTRUCTION. BREAK INTO EXISTING STORMWATER PIT, NEATLY CONNECT PROPOSED RCP TO EXISTING DRAINAGE NETWORK.
- D7 EXISTING STORMWATER PIPE TO BE CONNECTED INTO PROPOSED NETWORK. PIPE SIZE AND CONDITION TO BE VERIFIED VIA CCTV PRIOR TO CONSTRUCTION. BREAK INTO EXISTING STORMWATER PIT, NEATLY CONNECT PROPOSED RCP TO EXISTING DRAINAGE NETWORK.
- E1, E2, E3 EXISTING ELECTRICAL CONDUITS AND PITS TO BE REMOVED AND RELOCATED. REFER TO ELECTRICAL SERVICES DRAWINGS.
- E4, E5 EXISTING LIGHT POLES AND ASSOCIATED CABLING TO BE REMOVED.
- E6 EXISTING LIGHT POLES AND ELECTRICAL CONDUITS TO BE DEMOLISHED. FOR RETAINING WALL INFLUENCE REFER TO STRUCTURAL PACKAGE.
- E7 EXISTING HV SERVICE. GROUND SURFACE TO BE RAISED OVER EXISTING SERVICE. RAISE COVERS TO NEW FINISHED SURFACE.
- C1 EXISTING COMMUNICATIONS CONDUITS TO BE REMOVED AND RELOCATED.
- S1 EXISTING SEWER PUMP STATION TO BE RELOCATED. INVERT AND SURFACE LEVELS ARE TO BE ADJUSTED TO SUIT NEW BUILDING LOCATION. ASSOCIATED ELECTRICAL CONDUITS ARE TO BE REMOVED AND RELOCATED.
- W1, W2, W3 EXISTING RECYCLED WATER MAIN TO BE REMOVED AND RELOCATED.

5 2.5 0 5 10 15m
1:250 @A1

P3	07/04/2026	RO	60% DESIGN DEVELOPMENT	SN	SN
P2	12/02/2026	RO	60% DESIGN DEVELOPMENT	JC	JC
P1	30/01/2026	RO	DRAFT 60% DESIGN DEVELOPMENT	JC	JC
REV	DATE	BY	DESCRIPTION	CHK	APP
DRAWING STATUS: PRELIMINARY					



http://www.wsp.com

CLIENT:



ARCHITECT:



PROJECT:

CQU ROCKHAMPTON TAFE

TITLE:

TRADES BUILDING SITeworks LAYOUT PLAN

SCALE @ A1:

1:250

CHECKED:

JC

APPROVED:

JC

PROJECT NUMBER:

PS229518

DRAWN:

RO

DATE:

12/02/2026

DRAWING No:

C110

REV:

P3

© WSP Australia Pty Ltd