


**CQU ROCKHAMPTON
TAFE
CONSOLIDATION -
STAGE 2**

554/700 Yaamba Rd, Norman
Gardens QLD 4701




A	2026-02-12	ISSUED FOR TENDER	BC
1	2026-01-30	60% DRAFT ISSUE	BC
rev	date	details	init.

drawn	date
JS/BC	19/01/2026
checked	date
BC	12/02/2026
verified	date

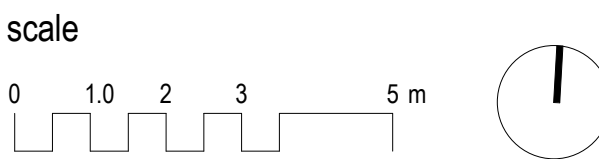

SLAB PLAN - LEVEL 1

scale	project no.
As indicated @ A1	25.0236.17
revision	
A	
sheet no.	
CQU-ROK-033-01-ARC-23-01	

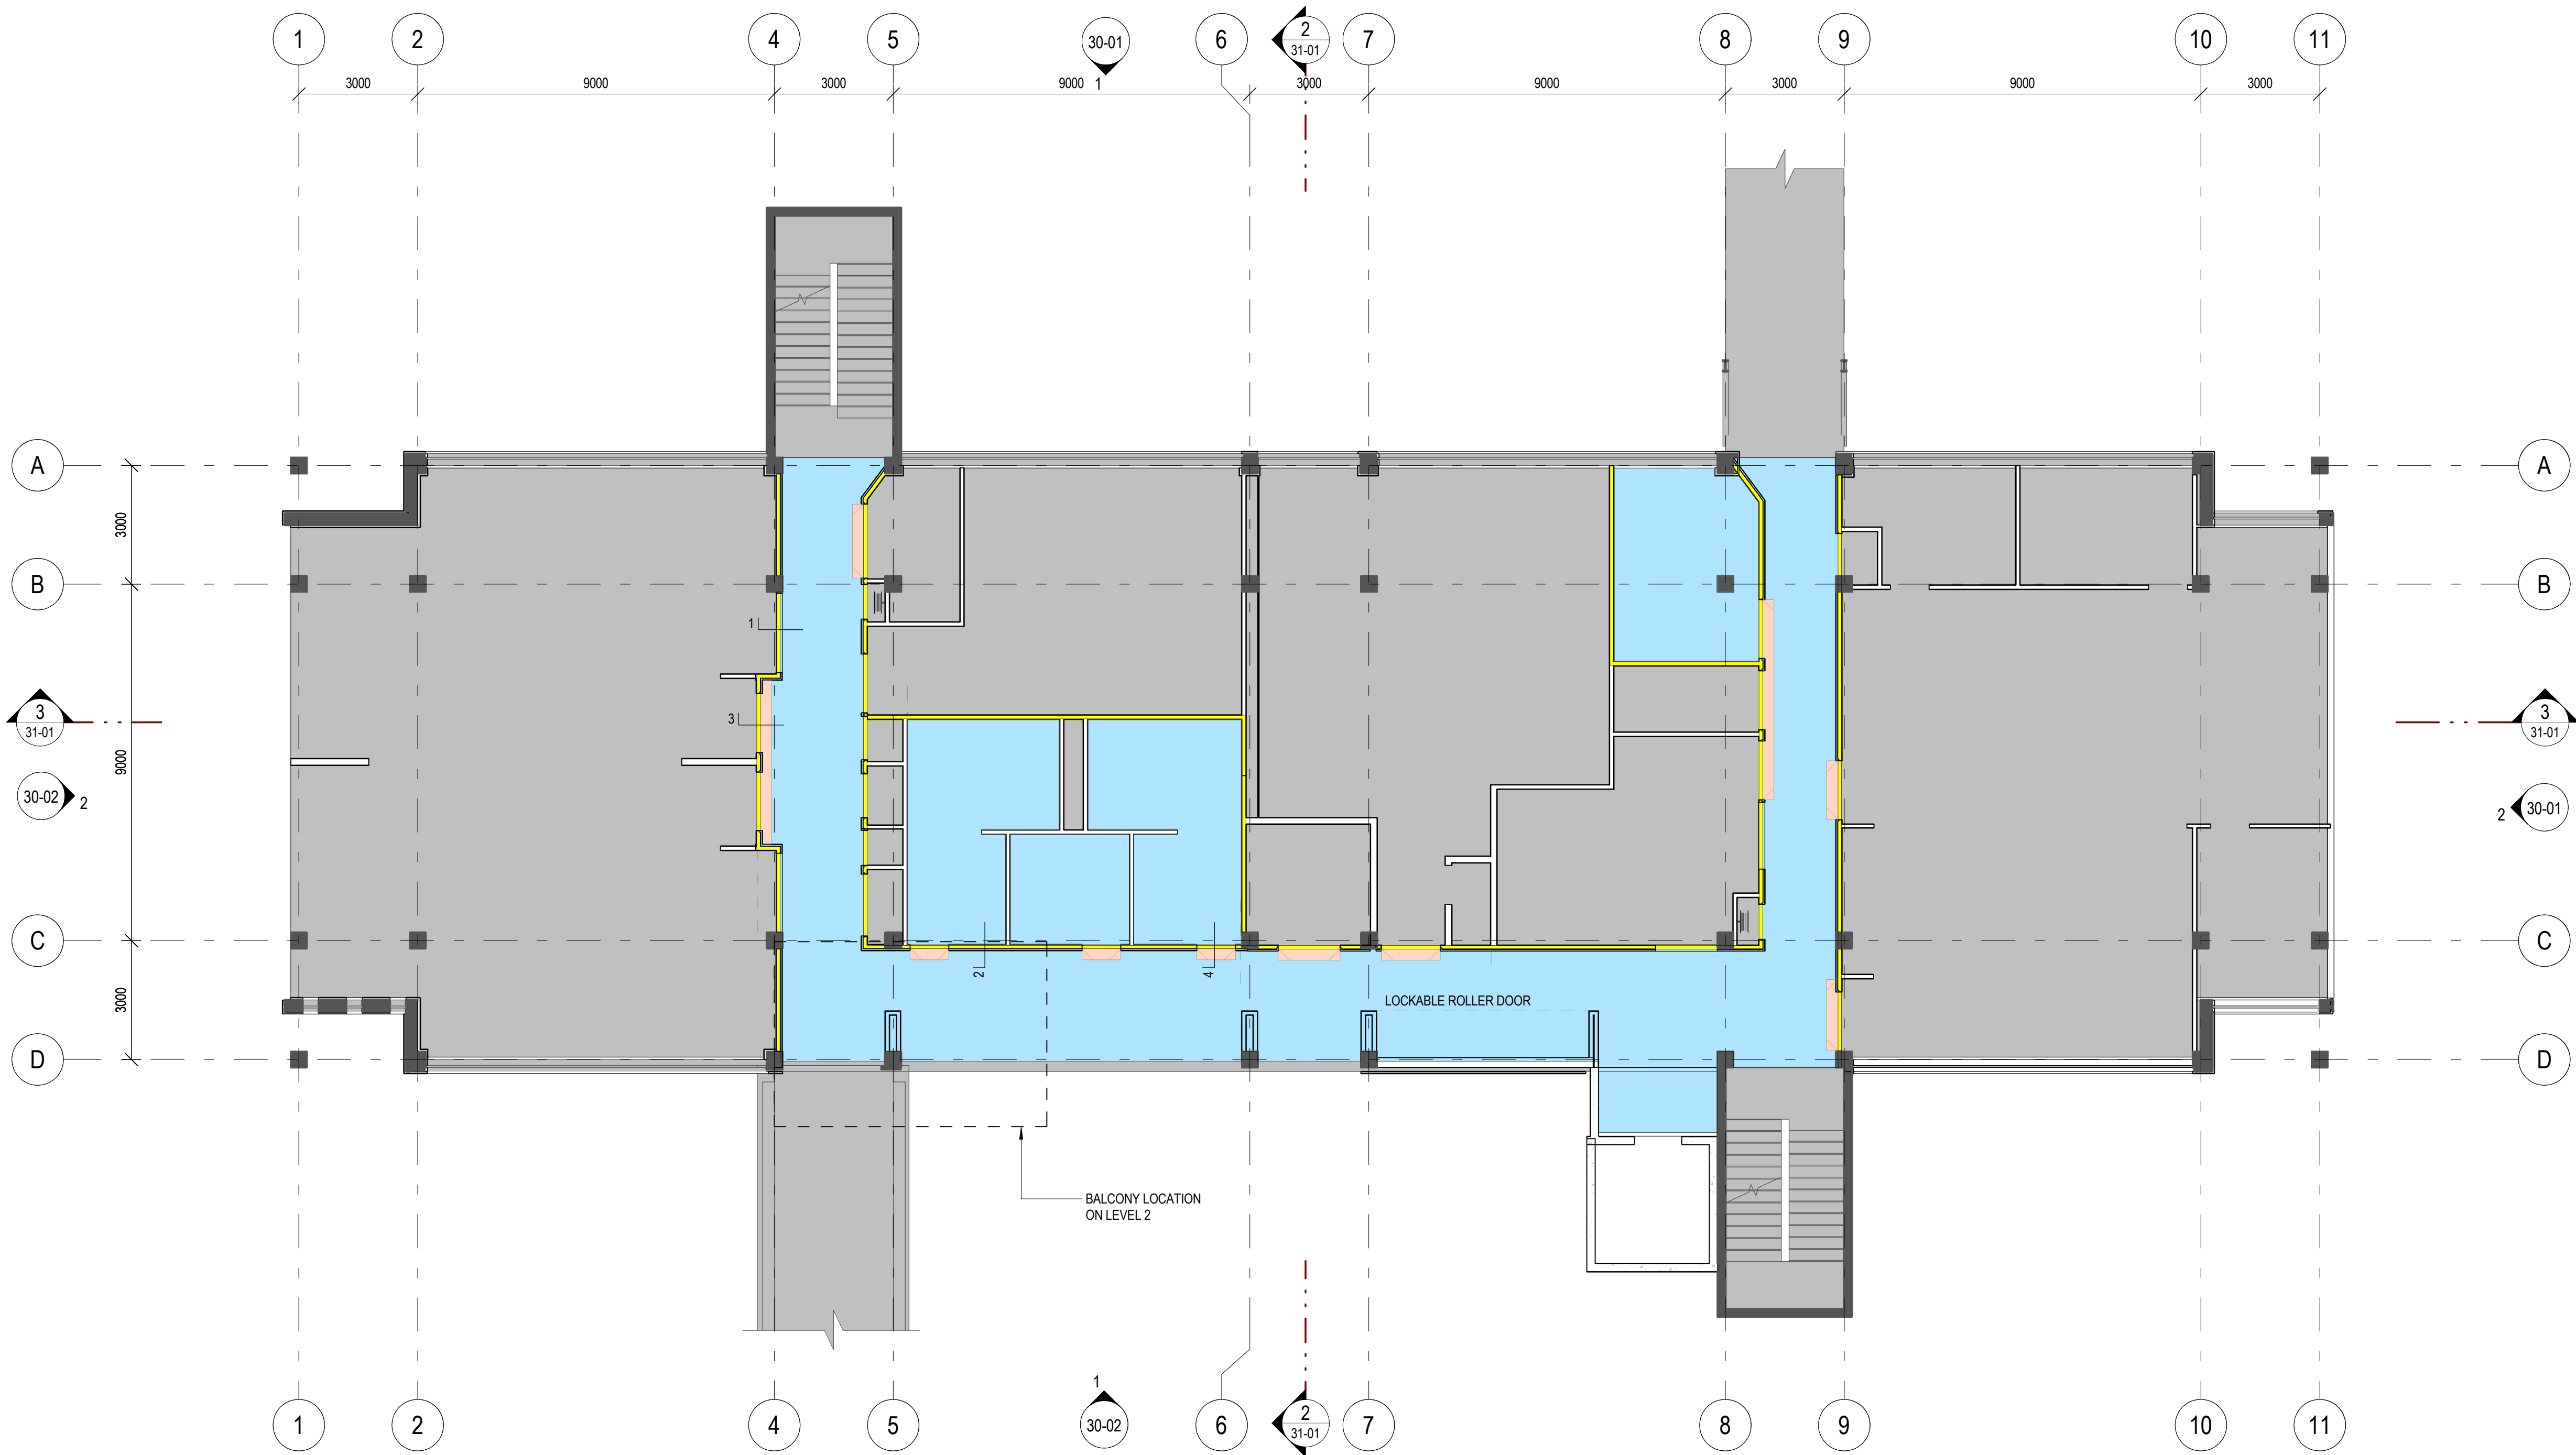


LEGEND	
	WATERPROOFING SYSTEM TO COMPLY WITH THE AUSTRALIAN STANDARDS & BUILDING CODE
	50mm HEIGHT HEBEL HOB ALONG EXTERNAL WALLS 35mm HEIGHT HEBEL HOB WHEN THERE IS THRESHOLD
	THRESHOLD RAMP (REFER TO AS 1428.1 FOR THRESHOLD RAMP INFO - 1:8 GRADE)


SLAB NOTE	
• FOR COLUMN TYPE REFER TO STRUCTURAL DRAWINGS	
• WHERE CONSTRUCTION MOVEMENT JOINTS ARE NOTED REFER TO STRUCTURAL DRAWINGS FOR TYPE	
• CONTRACTOR TO VERIFY ALL DIMENSIONS ON SITE PRIOR TO LOCATING SERVICES	
• REFER TO ROOM LAYOUT SHEETS FOR SETOUT OF FIXTURE AND FITTINGS - RLS DIMENSIONS NOMINATE THE FITTING TO THE FACE OF THE WALL LINING.	
• CONTRACTOR TO ADJUST AS REQUIRED WHEN SETTING OUT. FIXTURES SHOWN ON THIS DRAWING ARE AS A REFERENCE GUIDE ONLY	
• FLOOR WASTES ARE CENTRE OF ROOM UNLESS NOMINATED OTHERWISE ON THE ROOM LAYOUT SHEETS OR TYPICAL DETAILS (SHOWERS, BASINS WILL ALL BE SETOUT AS TYPICALS)	
• DRAWINGS TO BE READ IN CONJUNCTION WITH LATEST REVISION OF HYDRAULIC DRAWINGS	
• REFER ALSO TO STRUCTURAL AND HYDRAULIC DRAWINGS. NOT ALL PENETRATION ARE SHOWN HERE.	
• ARCHITECTURAL DRAWINGS WILL NOMINATE FINISH, EXTENT AND HEIGHT OF FLOORING. FOR ALL OTHER INFORMATION E.G. SLAB EDGE AND MATERIAL REFER TO STRUCTURAL ENGINEER DRAWINGS	
• CONTRACTOR TO ALLOW FOR WATERPROOFING SYSTEM TO WET AREA. ENSURE IT COMPLIES WITH AUSTRALIAN STANDARD	

HOB LEGEND_ (HEBEL BLOCK or SIMILAR) - 1.10 scale


1. TRANSITION BETWEEN EXTERIOR & DRY AREA

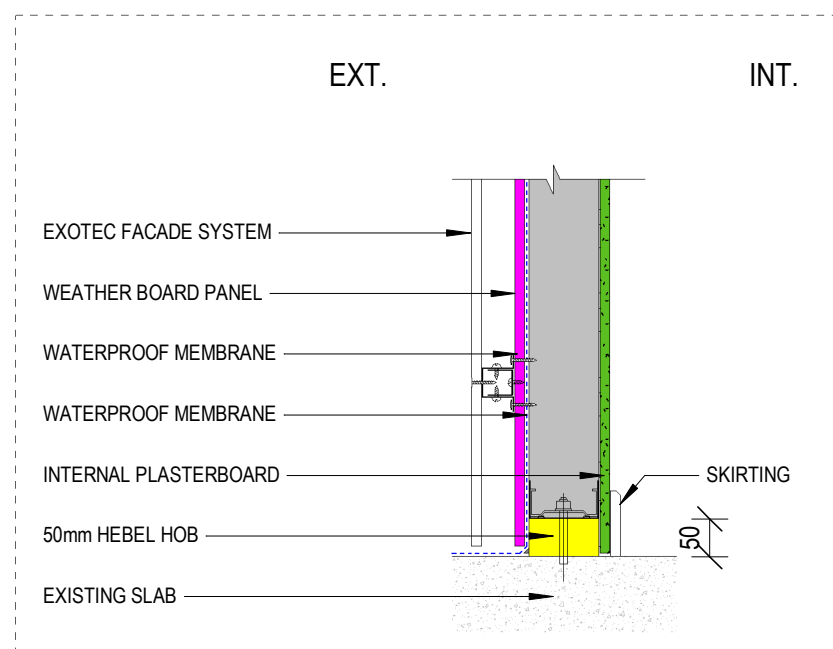


2. TRANSITION BETWEEN EXTERIOR & WET AREA

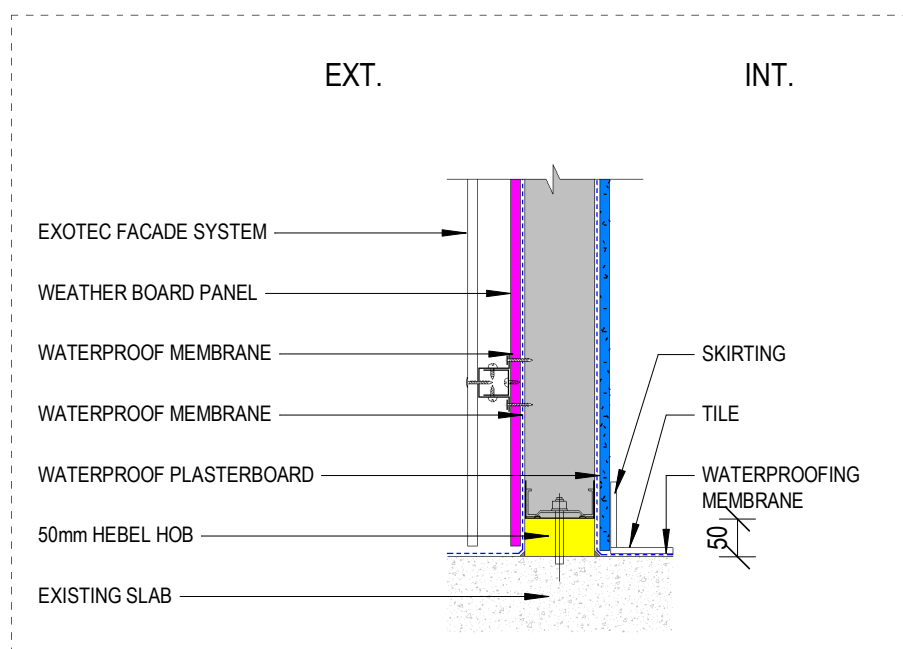

3. TRANSITION BETWEEN EXTERIOR & DRY AREA WITH DOOR

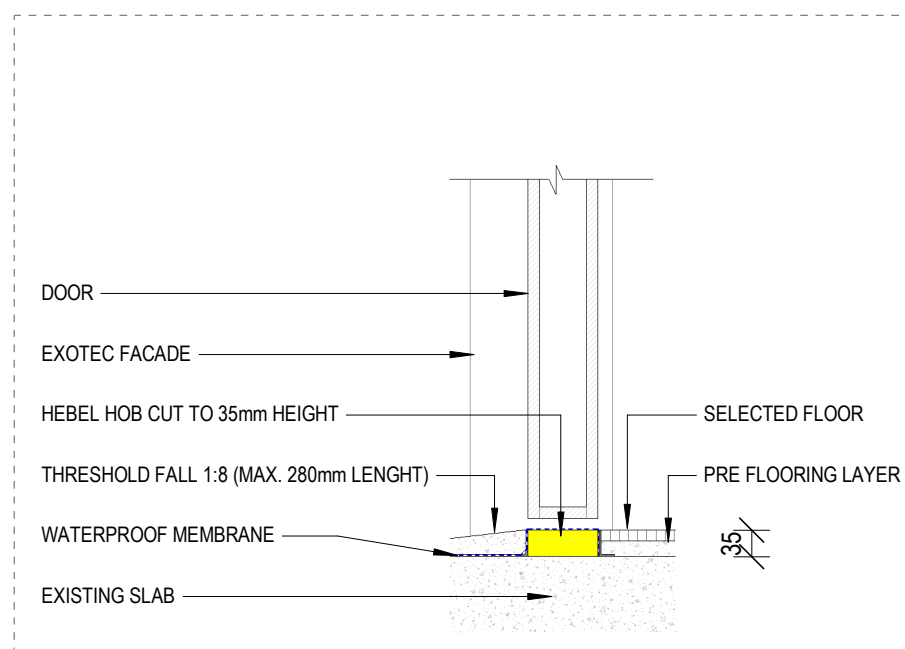

4. TRANSITION BETWEEN EXTERIOR & WET AREA WITH DOOR

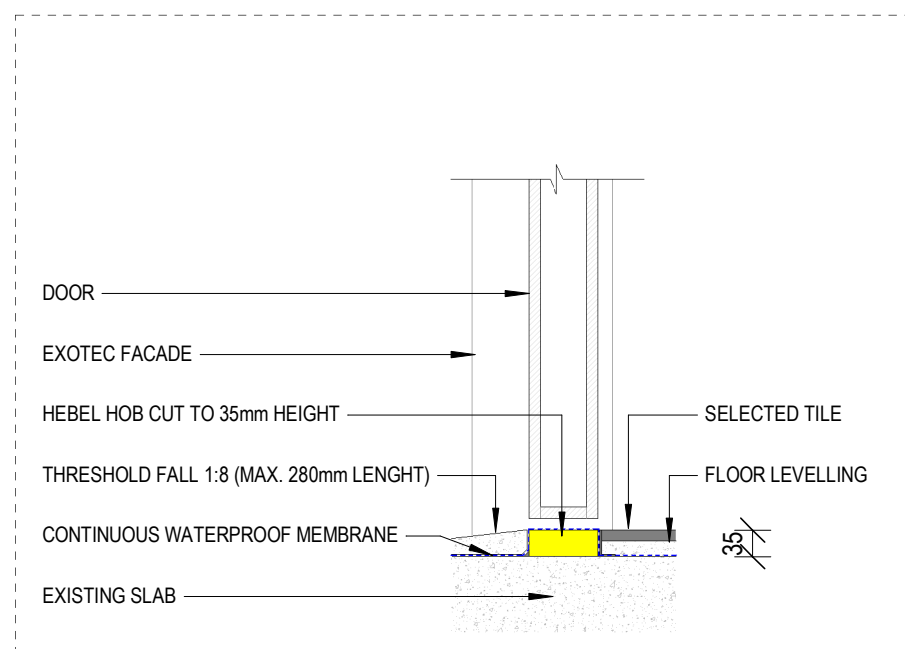

ISSUED FOR TENDER