


DO NOT SCALE


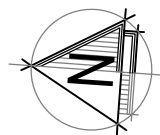


LEGEND EXISTING

- EX.D EXISTING STORMWATER DRAINAGE
- EX.W EXISTING WATERMAIN
- EX.E EXISTING ELECTRICAL CONDUITS
- ERW EXISTING FIREMAIN
- EX.COMM EXISTING COMMUNICATIONS
- EX.S EXISTING SEWER MAIN
- 444.50 EXISTING CONTOURS

LEGEND

- PROPOSED BUILDING AREA
- LANDSCAPE AREA
REFER LANDSCAPE PLANS FOR DETAILS
- PROPOSED TOP OF BATTER
- PROPOSED BOTTOM OF BATTER
- SD PROPOSED SUBSOIL DRAINAGE
- REFER NOTE 1 FOR DETAILS

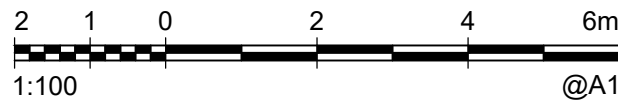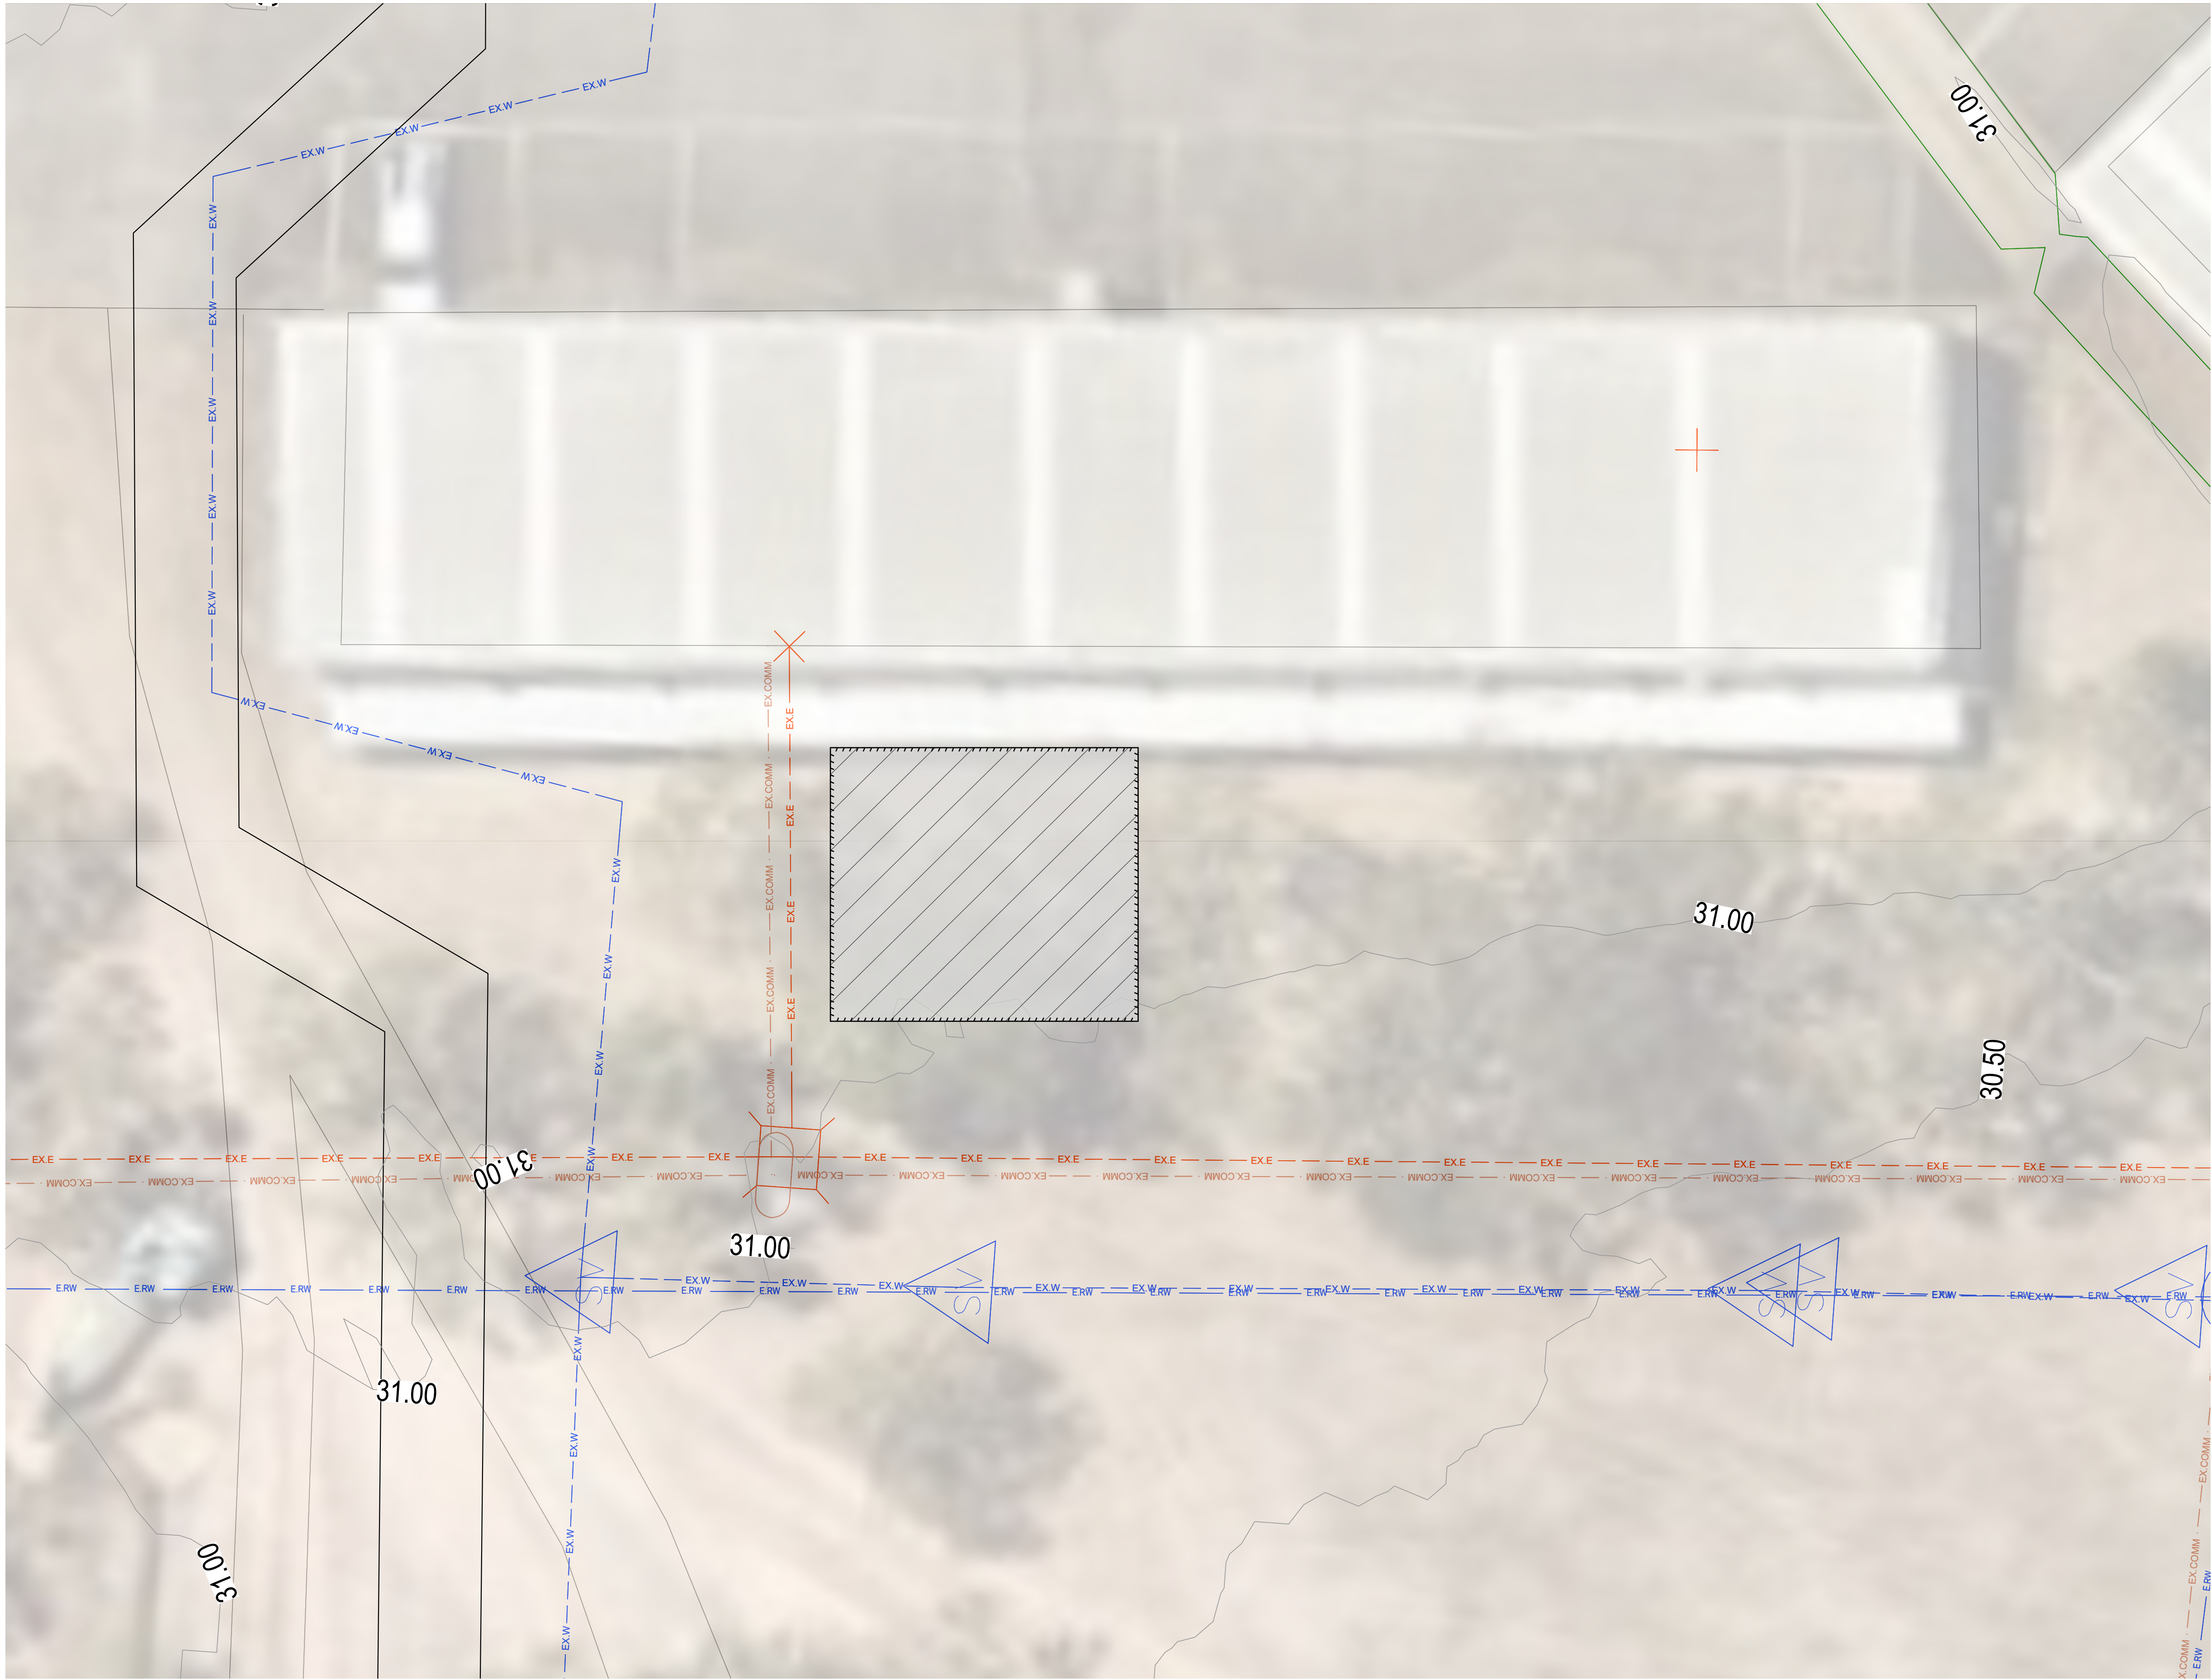

P1	30/01/2026	RO	DRAFT 60% DESIGN DEVELOPMENT	JC	JC
REV	DATE	BY	DESCRIPTION	CHK	APP
DRAWING STATUS:			PRELIMINARY		



<http://www.wsp.com>

CLIENT:



ARCHITECT:



PROJECT:

CQU ROCKHAMPTON TAFE

TITLE:

ENGINEERING SHED SITEWORKS LAYOUT PLAN

SCALE @ A1:

1:100

CHECKED:

JC

APPROVED:

JC

PROJECT NUMBER:

PS229518

DRAWN:

RO

DATE:

1/30/2026

DRAWING No:

C400

REV:

P1

© WSP Australia Pty Ltd