


DO NOT SCALE

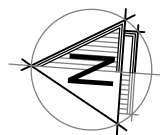

LEGEND EXISTING

- EX.D EXISTING STORMWATER DRAINAGE
- EX.W EXISTING WATERMAIN
- EX.E EXISTING ELECTRICAL CONDUITS
- ER.W EXISTING FIREMAIN
- EX.COMM EXISTING COMMUNICATIONS
- EX.S EXISTING SEWER MAIN
- 444.50 EXISTING CONTOURS

LEGEND



BULK EARTHWORKS TO PAVEMENT AREAS. ALLOW TO CARRY OUT THE WORKS IN ACCORDANCE WITH EARTHWORKS NOTES ON GENERAL NOTES DRAWING AND IN ACCORDANCE WITH THE PROJECT GEOTECHNICAL REPORT.

- PROPOSED PAVEMENT TYPE 1
LIGHT DUTY ASPHALT - REFER DWG C240
- PROPOSED PAVEMENT TYPE 2
HEAVY DUTY ASPHALT - REFER DWG C240
- PROPOSED PAVEMENT TYPE 3
HEAVY DUTY CONCRETE - REFER DWG C240
- PROPOSED PAVEMENT TYPE 4
LIGHT DUTY CONCRETE - REFER DWG C240

BULK EARTHWORKS TO BUILDING AREA. ALLOW TO CARRY OUT THE WORKS IN ACCORDANCE WITH EARTHWORKS NOTES ON GENERAL NOTES DRAWING INCLUDING STRIPPING, PROOF ROLLING AND FILLING WITH IMPORTED SELECT FILL MATERIAL TO ACHIEVE THE NOMINATED BULK EARTHWORKS LEVELS AS SPECIFIED IN THE PROJECT GEOTECHNICAL REPORT. ALLOW TO PROVIDE 100mm THICK TYPE 2.3 (CBR45%) MATERIAL.

BULK EARTHWORKS TO LANDSCAPE AREA. ALLOW TO FINISH EARTHWORKS TO LANDSCAPE ARCHITECTS DETAILS, GENERALLY 300mm BELOW FINISHED SURFACE LEVEL (UNO).

- BE15.28 +
- N1 REFER NOTE 1 FOR DETAILS

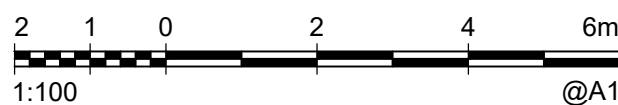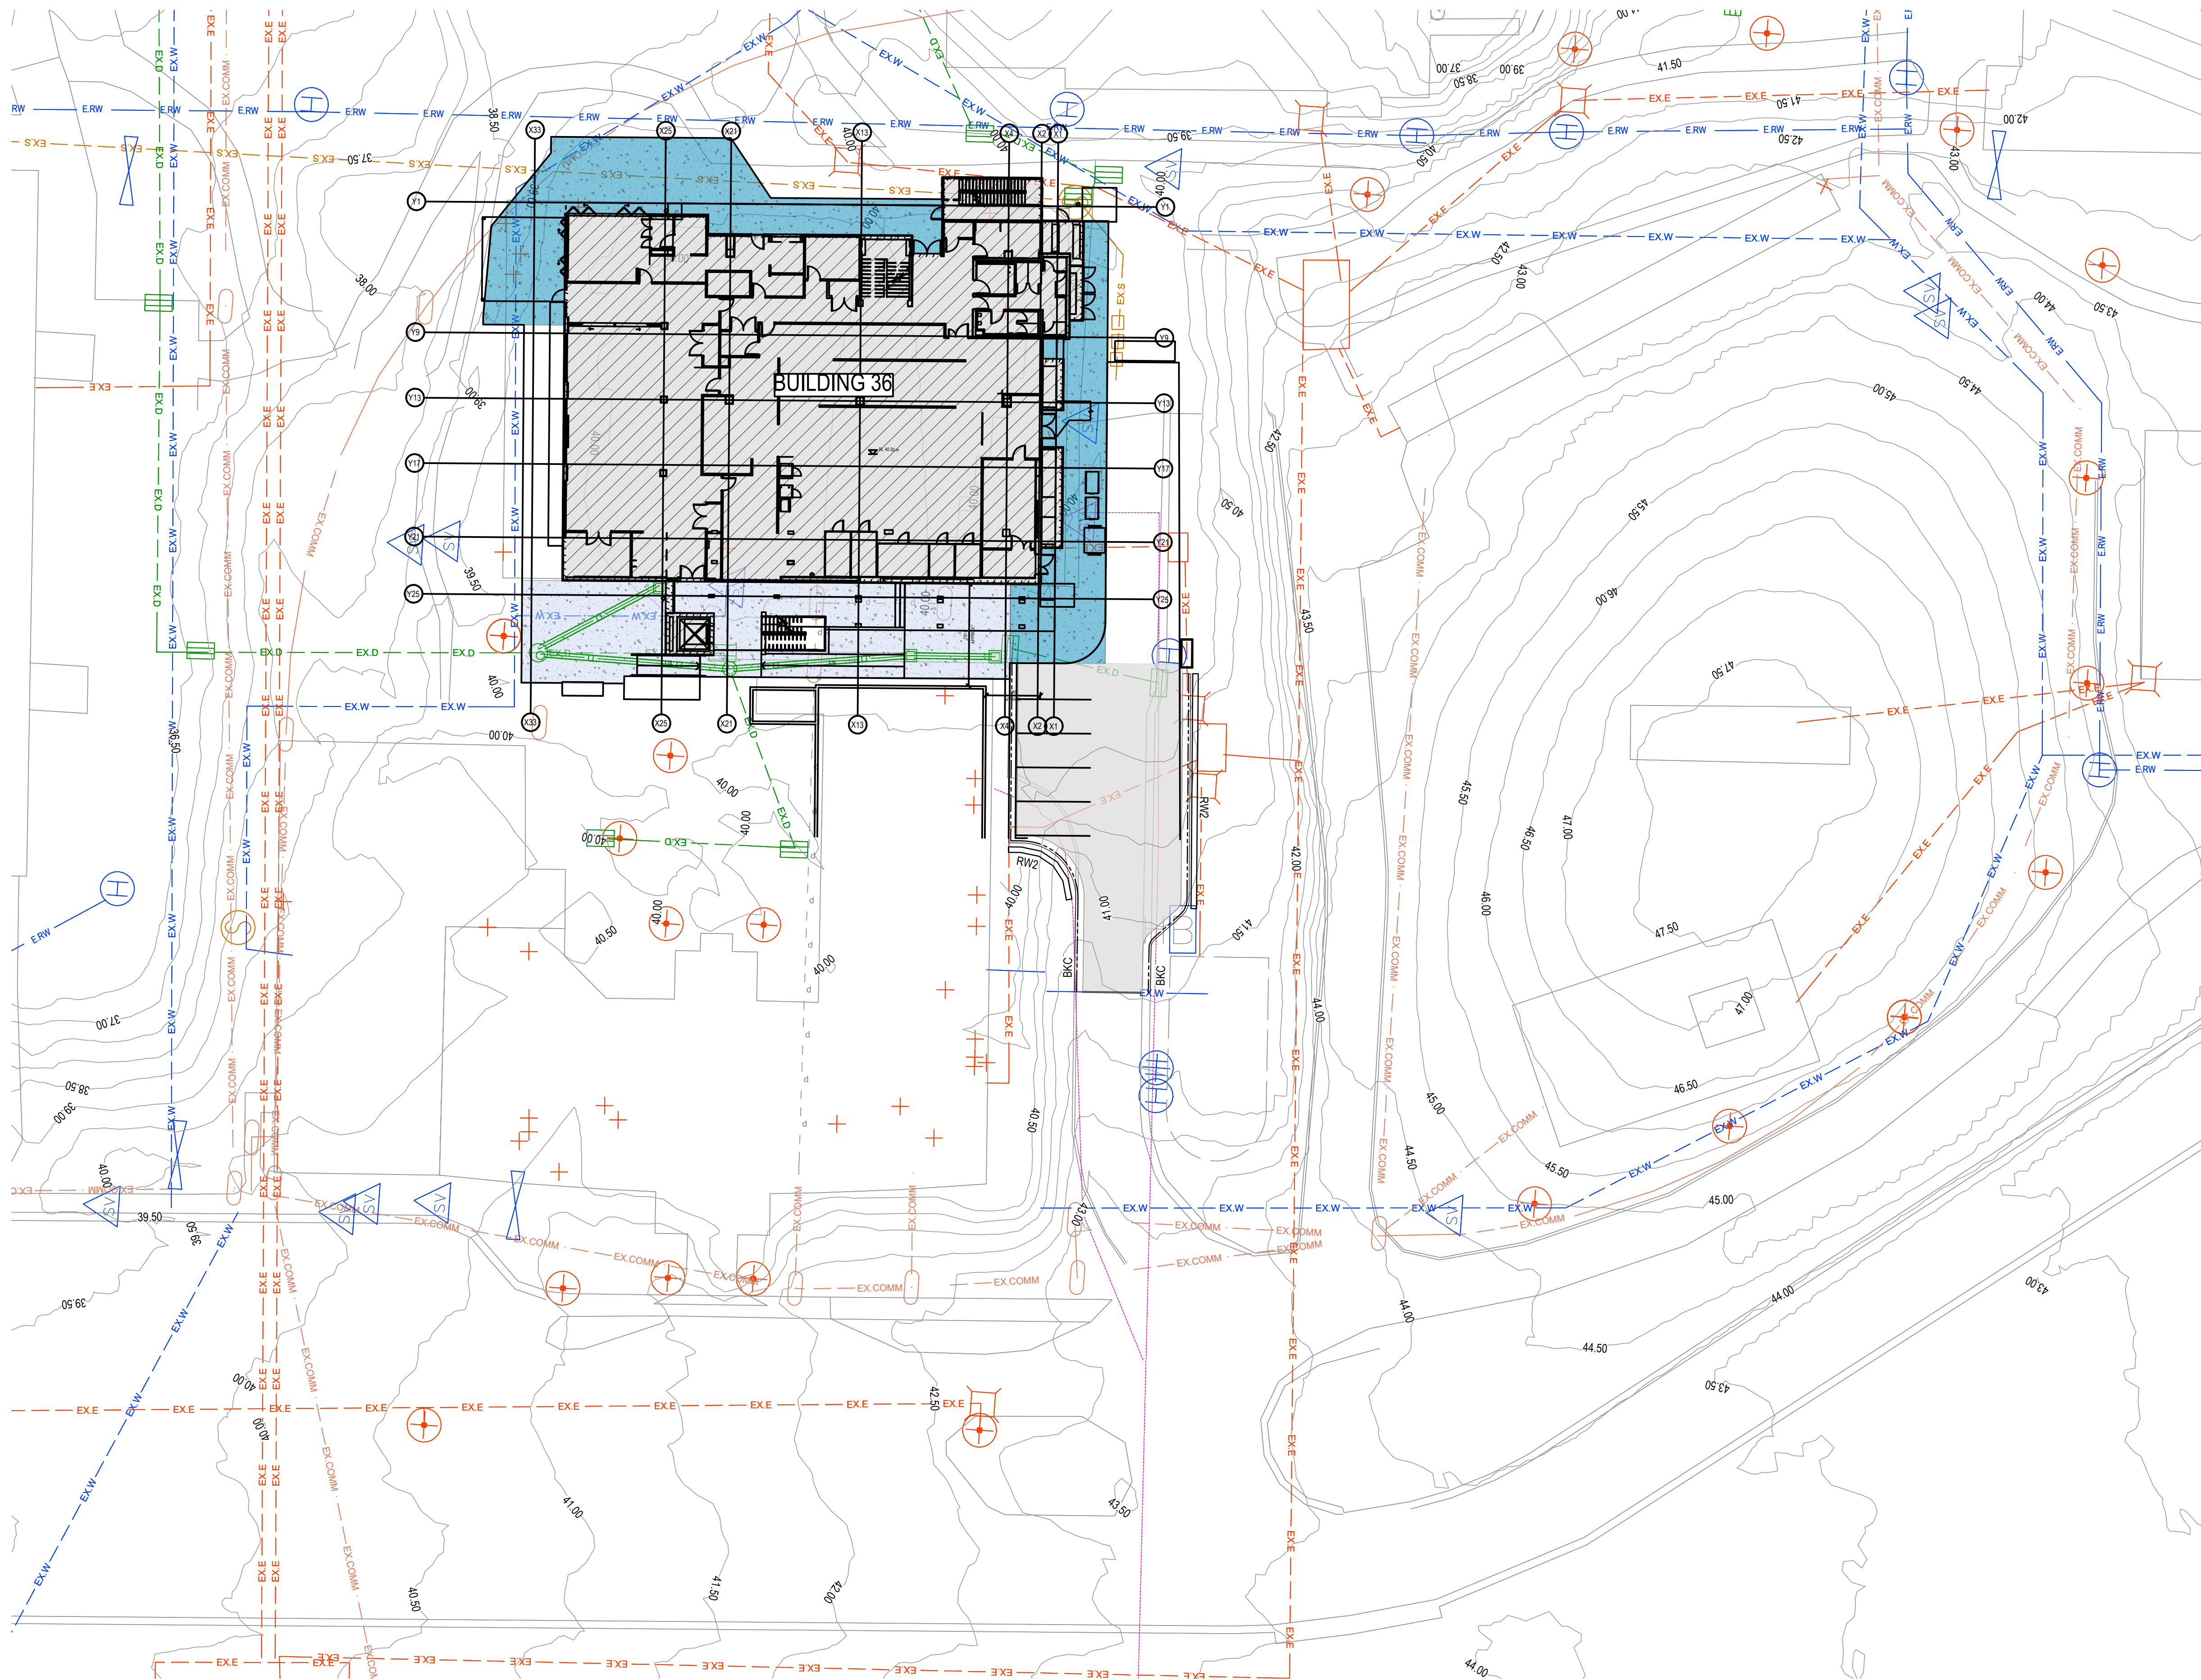

P1	30/01/2026	RO	DRAFT 60% DESIGN DEVELOPMENT	JC	JC
REV	DATE	BY	DESCRIPTION	CHK	APP
DRAWING STATUS:			PRELIMINARY		



<http://www.wsp.com>

CLIENT:



ARCHITECT:



PROJECT:

CQU ROCKHAMPTON TAFE

TITLE:

BUILDING 36 EARTHWORKS LAYOUT PLAN

SCALE @ A1:

1:250

CHECKED:

JC

APPROVED:

JC

PROJECT NUMBER:

PS229518

DRAWN:

RO

DATE:

1/30/2026

DRAWING No:

C200

REV:

P1

© WSP Australia Pty Ltd