


FOR CONTINUATION REFER TO INSET A

DO NOT SCALE

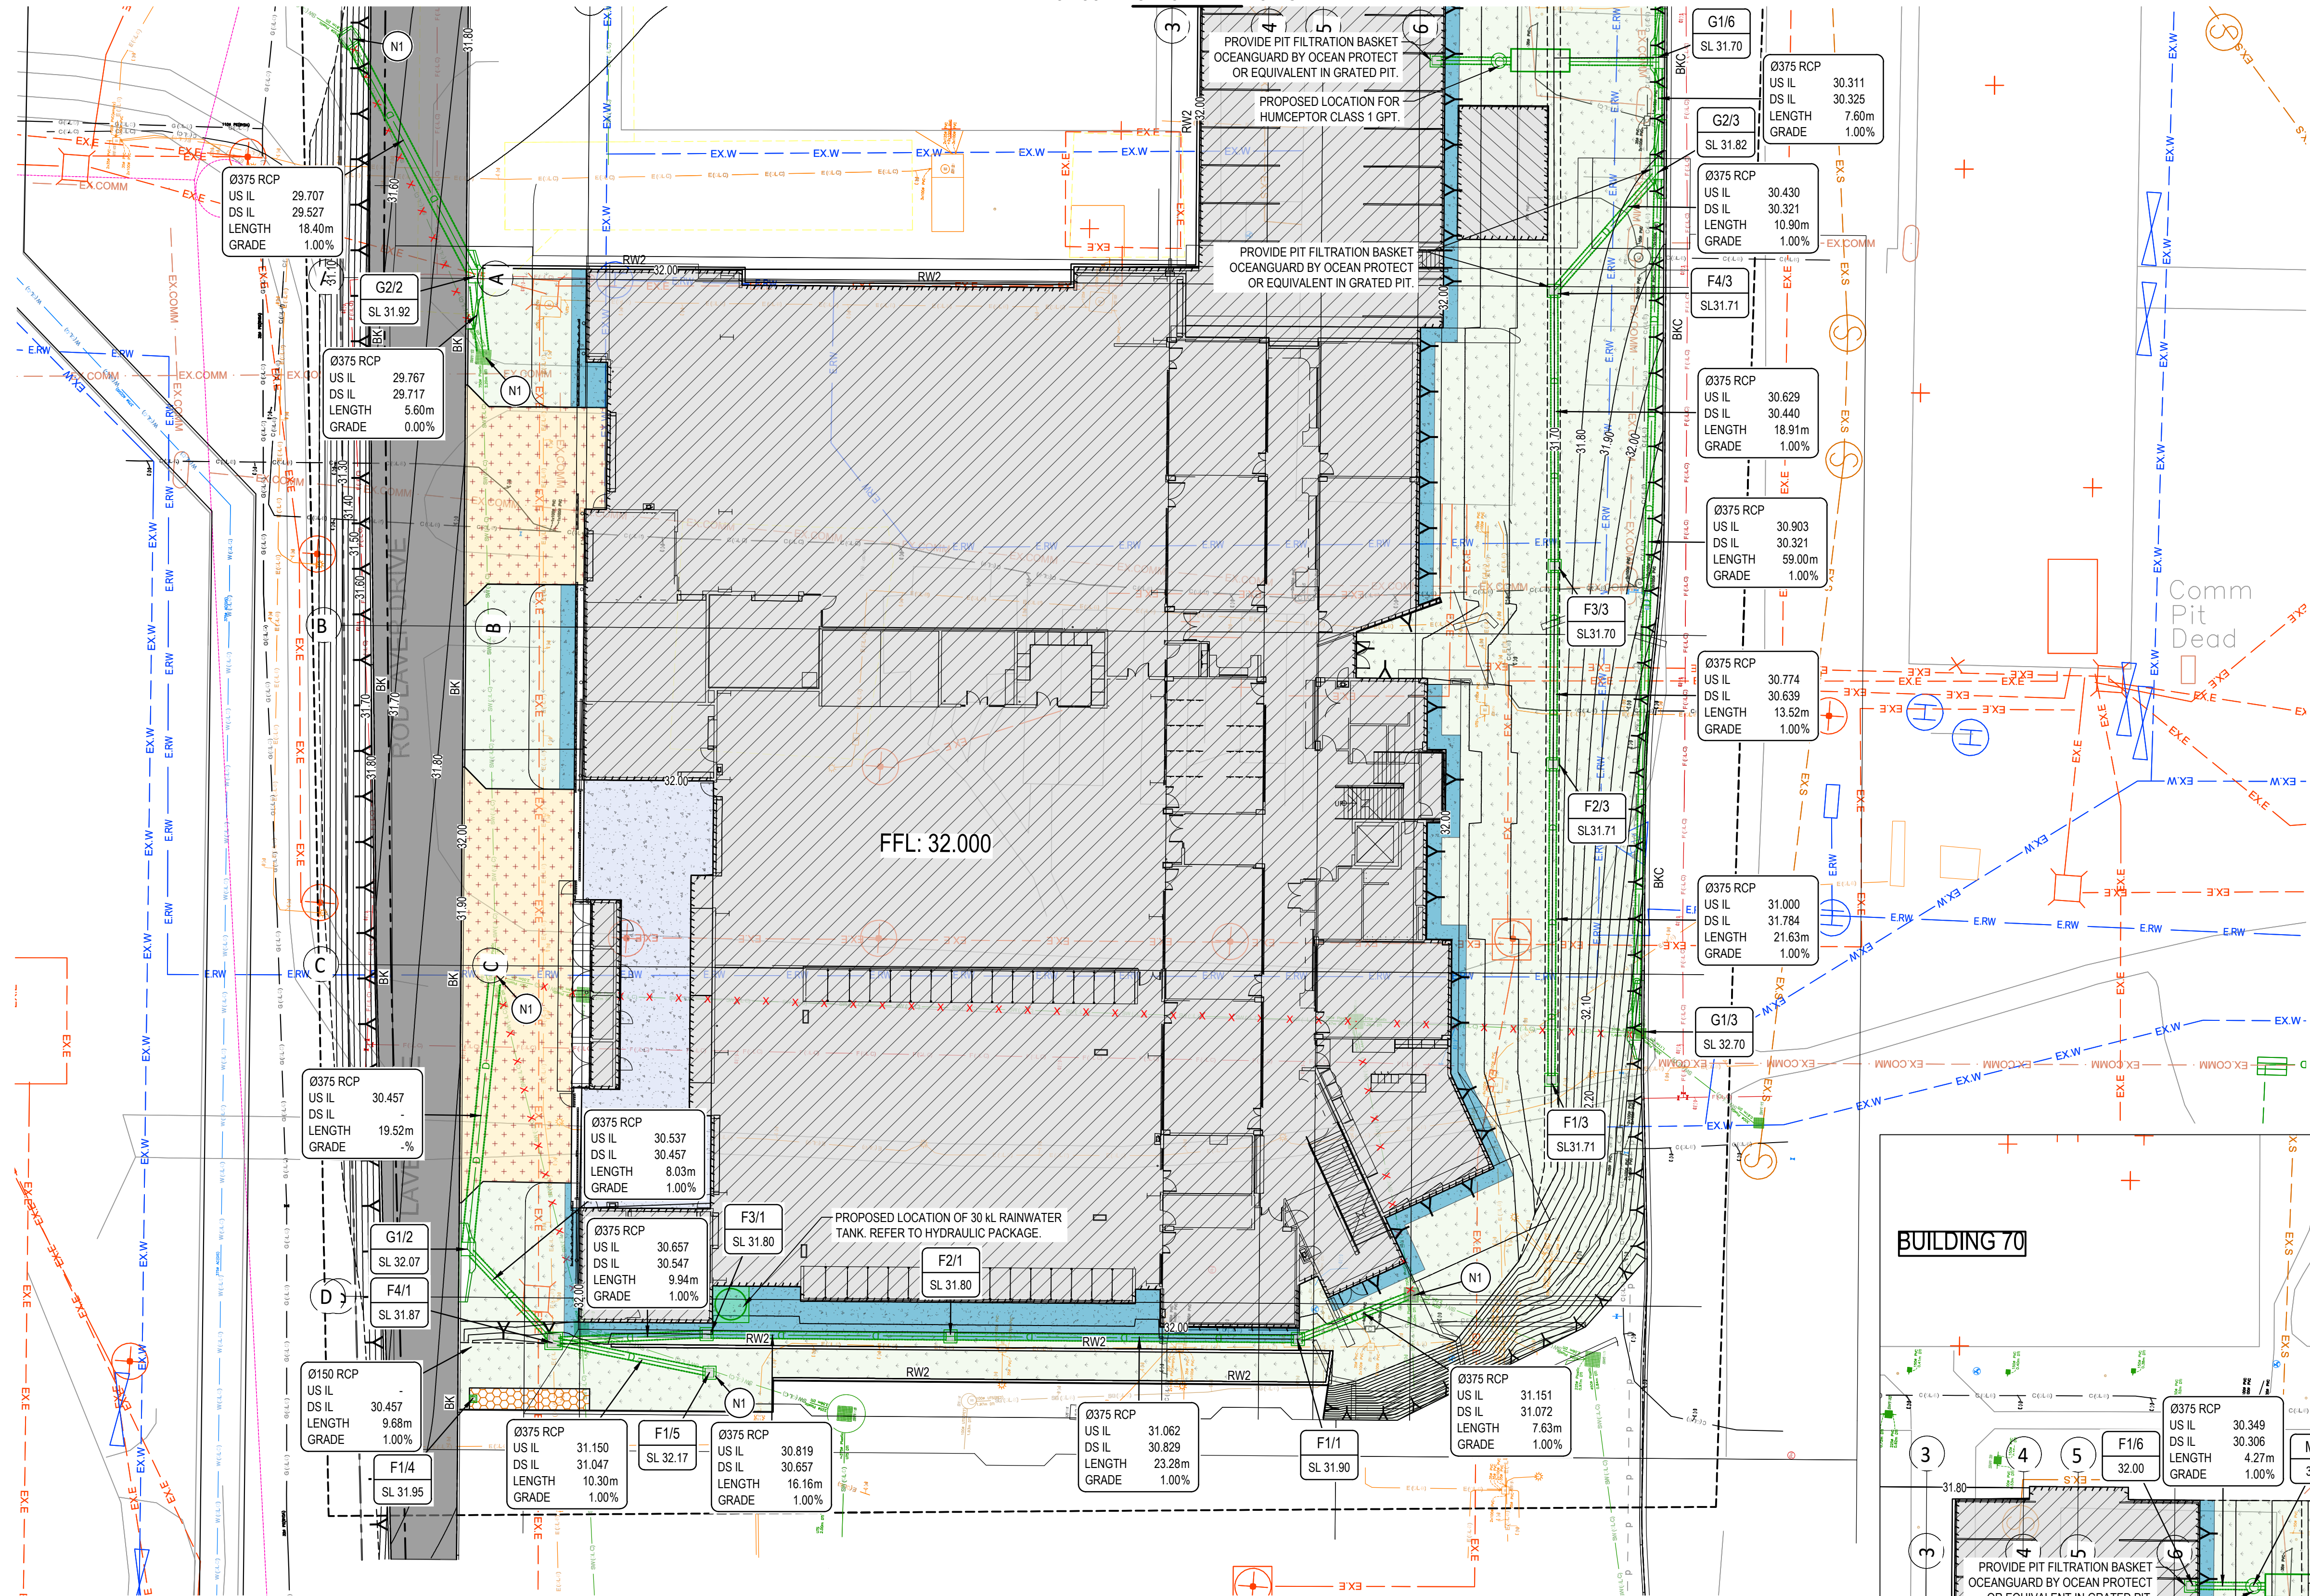


LEGEND EXISTING	
	EX.D EXISTING STORMWATER DRAINAGE
	EX.W EXISTING WATERMAIN
	EX.E EXISTING ELECTRICAL CONDUITS
	ER.W EXISTING FIREMAIN
	EX.COMM EXISTING COMMUNICATIONS
	EX.S EXISTING SEWER MAIN
	444.50 EXISTING CONTOURS

LEGEND	
	PROPOSED BUILDING AREA
	PROPOSED ROOFWATER DRAINAGE PIPE
	PROPOSED STORMWATER DRAINAGE PIPE AND MANHOLE
	PROPOSED HEADWALL AND ROCK OUTLET PROTECTION
	OVERLAND FLOW PATH
	STORMWATER STRUCTURE DETAILS
	STORMWATER PIPE DETAILS
	PROPOSED MOUNTABLE KERB AND CHANNEL
	PROPOSED BARRIER KERB AND CHANNEL
	ITEMS / SERVICES TO BE REMOVED
	PROPOSED WATER PIPE
	PROPOSED SEWERAGE RETICULATION PIPE
	PROPOSED ELECTRICAL CONDUIT
	REFER NOTE 1 FOR DETAILS

NOTES	
1. CONTRACTOR TO INVESTIGATE EXISTING STORMWATER SYSTEM. CONFIRM CONNECTION POINT PRIOR TO COMMENCEMENT OF WORKS AND FLUSH AND CLEAN EXISTING SYSTEM.	

STRUCTURE SCHEDULE				
STRUCTURE TYPE	COVER TYPE	COVER DIM	STRUCTURE TYPE/DIMENSION	STRUCTURE No.
SURFACE INLET	CLASS D GALVANISED MILD STEEL GRATE HINGED TO FRAME	300 x 300	PRECAST	F1/4
SURFACE INLET	CLASS D GALVANISED MILD STEEL GRATE HINGED TO FRAME	600 x 600	PRECAST	F1/1, F2/1, F3/1, F1/3, F2/3, F3/3, F4/3, F1/5, F1/6
SURFACE INLET	CLASS D GALVANISED MILD STEEL GRATE HINGED TO FRAME	900 x 900	PRECAST	F4/1
GULLY PIT	ON GRADE, LIP IN LINE	-	PRECAST	G1/2, G2/2, G1/3, G2/3, G1/6
GPT	AS PER MANUFACTURES SPECIFICATIONS	AS PER MANUFACTURES SPECIFICATIONS	HUMCEPTOR CLASS 1 GPT.	M1/6

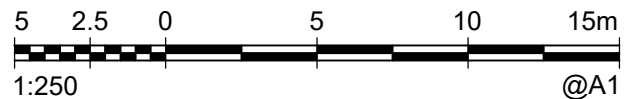

P2	12/02/2026	RO	60% DESIGN DEVELOPMENT	JC	JC
P1	30/01/2026	RO	DRAFT 60% DESIGN DEVELOPMENT	JC	JC
REV	DATE	BY	DESCRIPTION	CHK	APP
DRAWING STATUS: PRELIMINARY					



http://www.wsp.com

CLIENT:



ARCHITECT:



PROJECT:

CQU ROCKHAMPTON TAFE

TITLE:

TRADES BUILDING STORMWATER LAYOUT PLAN

SCALE @ A1:

1:250

CHECKED:

JC

APPROVED:

JC

PROJECT NUMBER:

PS229518

DRAWN:

RO

DATE:

12/02/2026


DRAWING No:

C120

REV:

P2

© WSP Australia Pty Ltd

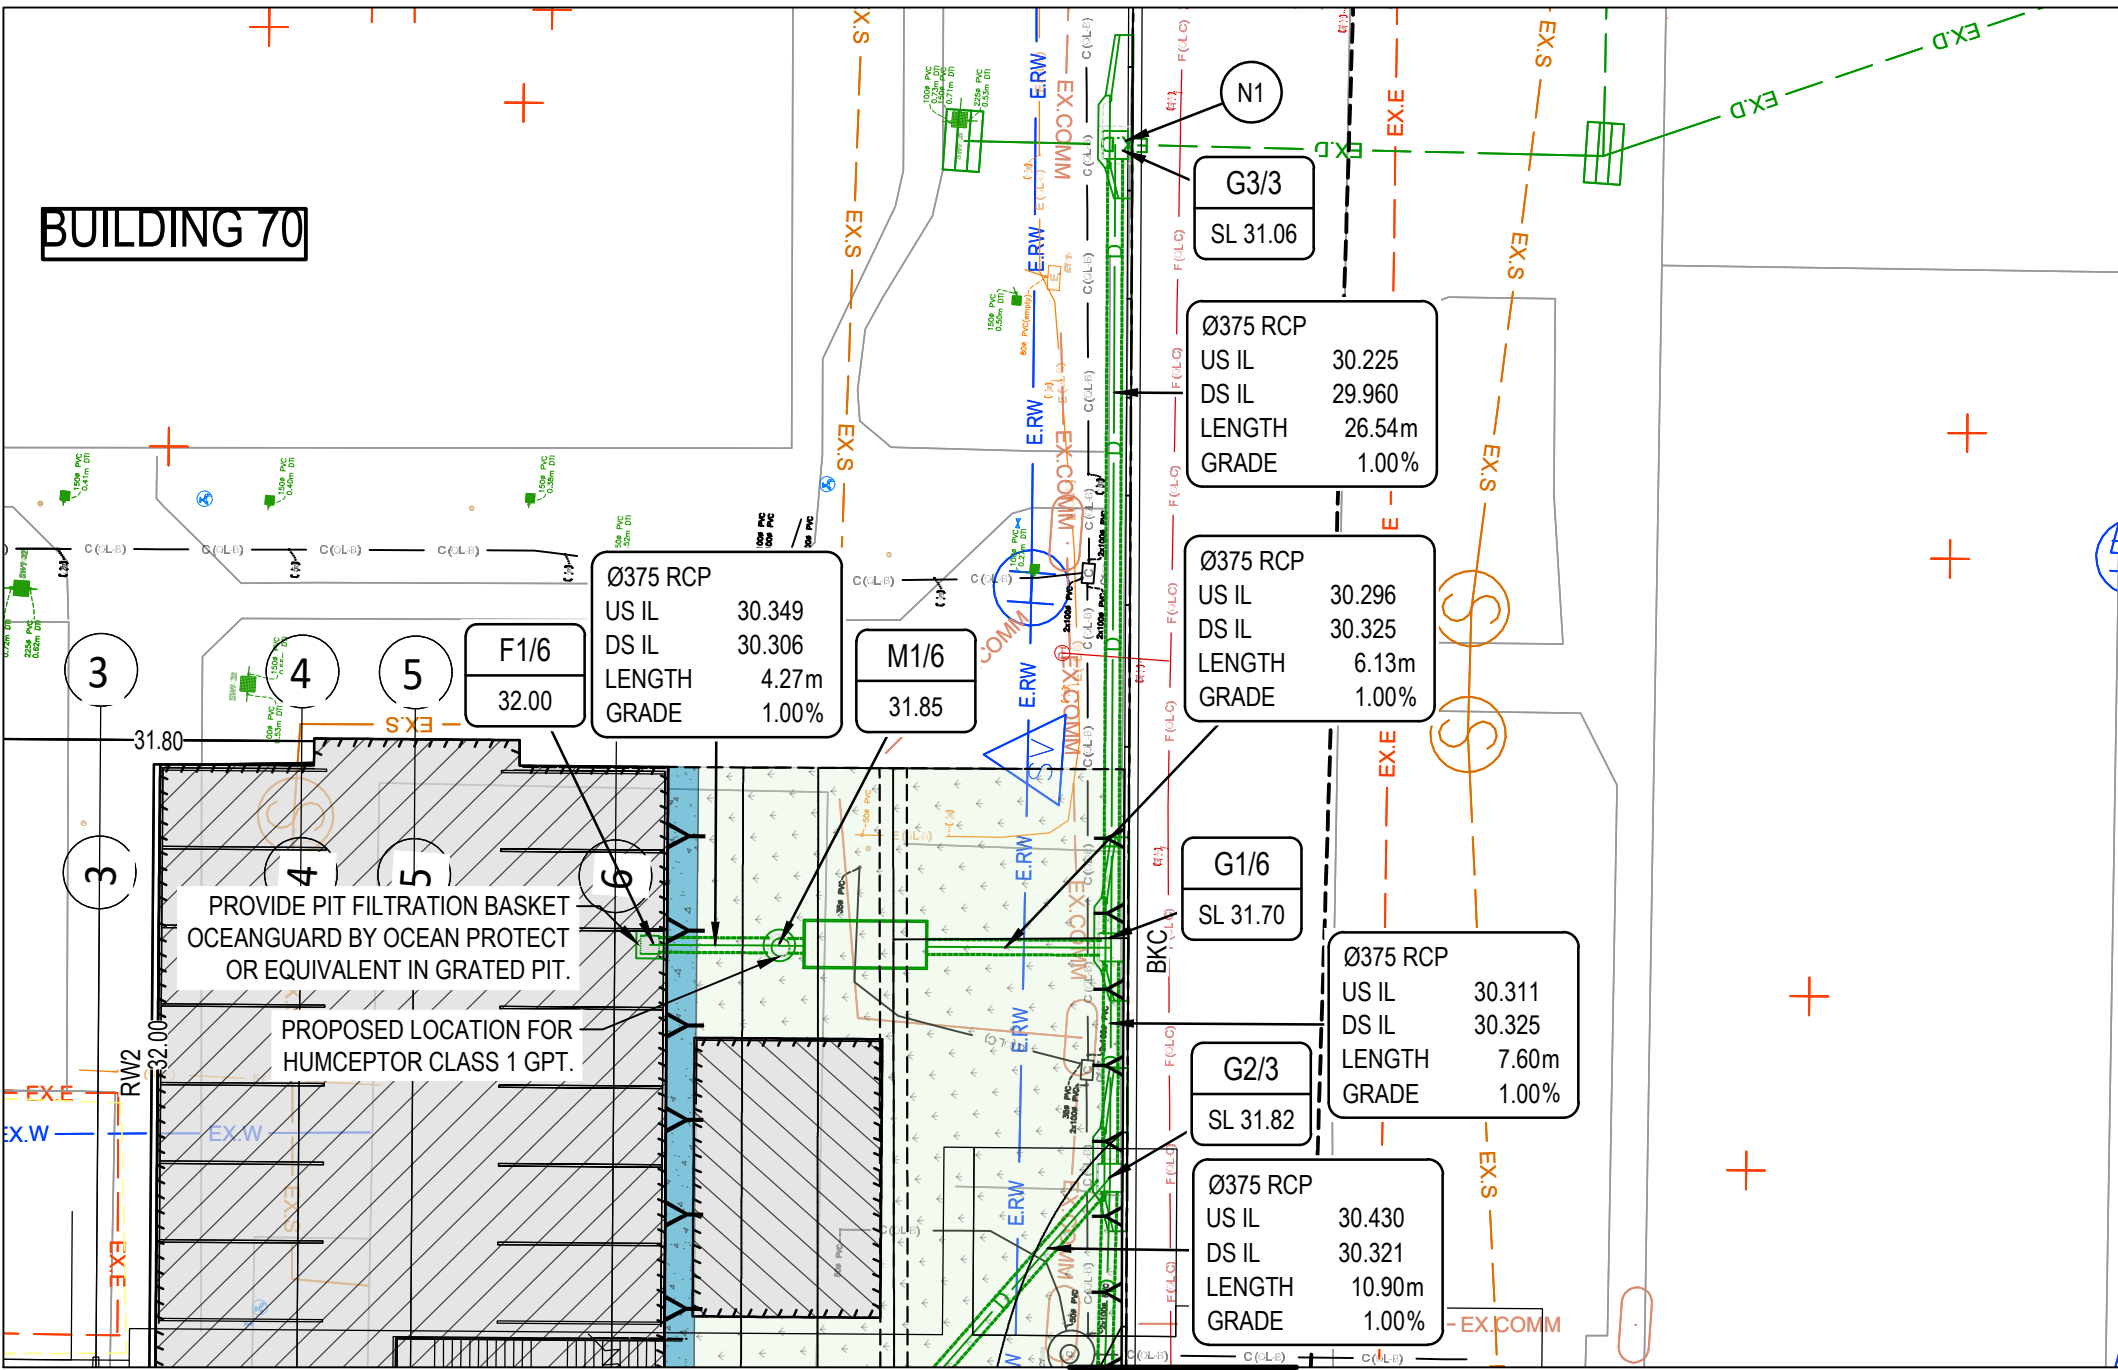

INSET A