


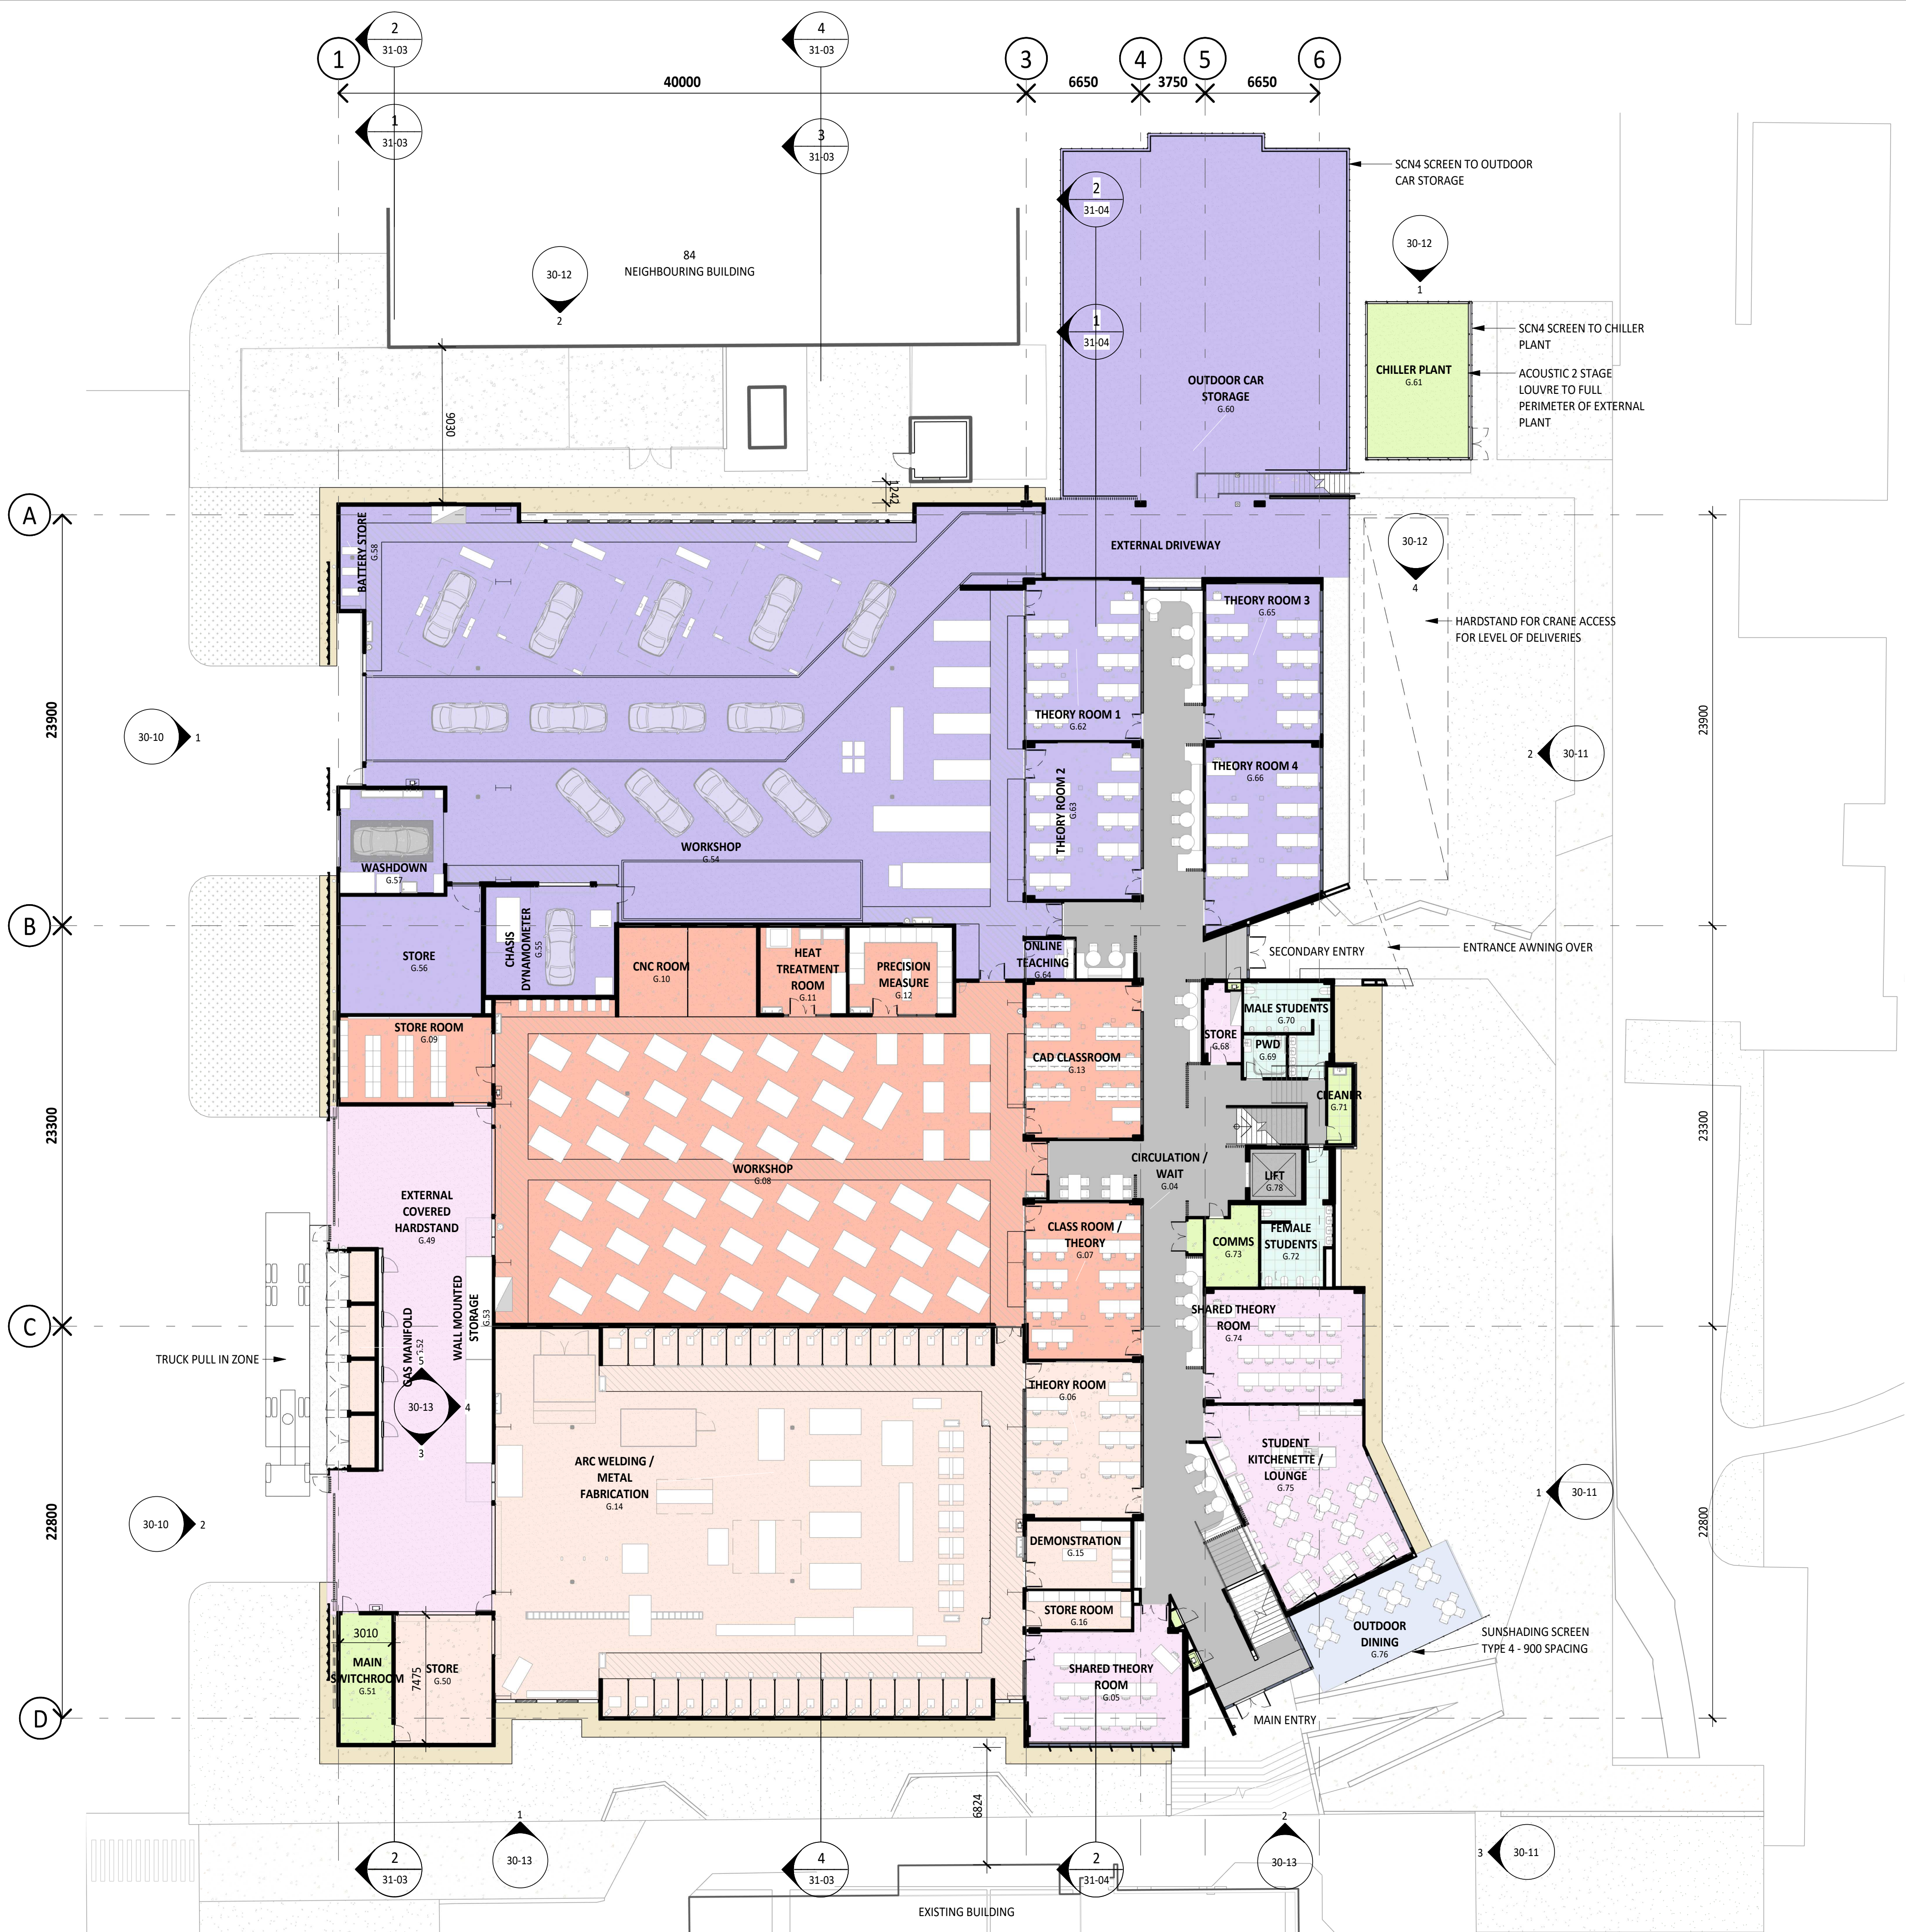

DEPARTMENT COLOUR LEGEND

- AMENITIES
- CIRCULATION
- FITTING & MACHINING
- LIGHT AUTOMOTIVE + AUTO ELECTRICS
- METAL FABRICATION
- OUTDOOR
- SERVICES
- SHARED

thomson
adsett

PEDDLE THORP
architecture | interiors | health | planning

Telephone +61 7 3840 9999
bne@thomsonadsett.com
Level 9, 470 St Pauls Terrace
Fortitude Valley
Qld 4006 Australia
thomsonadsett.com

© Copyright
These drawings and designs and the copyright thereof are the property of Thomson Adsett Pty Ltd and must not be used, retained or copied without written permission of Thomson Adsett Pty Ltd. ABN 76 105 314 654 Trading as ThomsonAdsett. Dimensions take precedence over scaling. Do not measure off drawings as print sizes may vary

**CQU ROCKHAMPTON
TAFE
CONSOLIDATION -
STAGE 2**

554/700 Yaamba Rd, Norman
Gardens QLD 4701



A	12/02/26	ISSUED FOR TENDER	BS
8	30/01/26	DRAFT 60% ISSUE	BS
7	23/01/26	COORDINATION ISSUE FOR CONSULTANTS	BS
6	19/12/25	ISSUE FOR COORDINATION	BS
5	24/11/25	50% COSTING ISSUE	BS
4	18/11/25	USER GROUP PRESENTATION	SG
3	14/11/25	USER GROUP PRESENTATION	SG
2	13/11/25	USER GROUP PRESENTATION	SG
1	12/11/25	USER GROUP PRESENTATION	SG

rev	date	details	init.
-----	------	---------	-------

drawn	date
PT	19/12/25
checked	date
use 'Approved By' only	19/12/25
verified	date
BS	19/12/25

scale

GA PLAN GROUND LEVEL

scale	project no.
1 : 200 @ A1	260018
revision	
A	
sheet no.	
CQU-ROK-092-GN-ARC-21-00	

ISSUED FOR TENDER