

**CQU ROCKHAMPTON
TAFE
CONSOLIDATION -
STAGE 2**554/700 Yaamba Rd, Norman
Gardens QLD 4701

for



B	05/03/26	ISSUED FOR TENDER	BS
A	12/02/26	ISSUED FOR TENDER	BS
3	30/01/26	DRAFT 60% ISSUE	BS
2	23/01/26	COORDINATION ISSUE FOR CONSULTANTS	BS
1	19/12/25	ISSUE FOR COORDINATION	BS
rev	date	details	init.

drawn	date
PT	19/12/25
checked	date
use 'Approved By' only	19/12/25
verified	date
BS	19/12/25

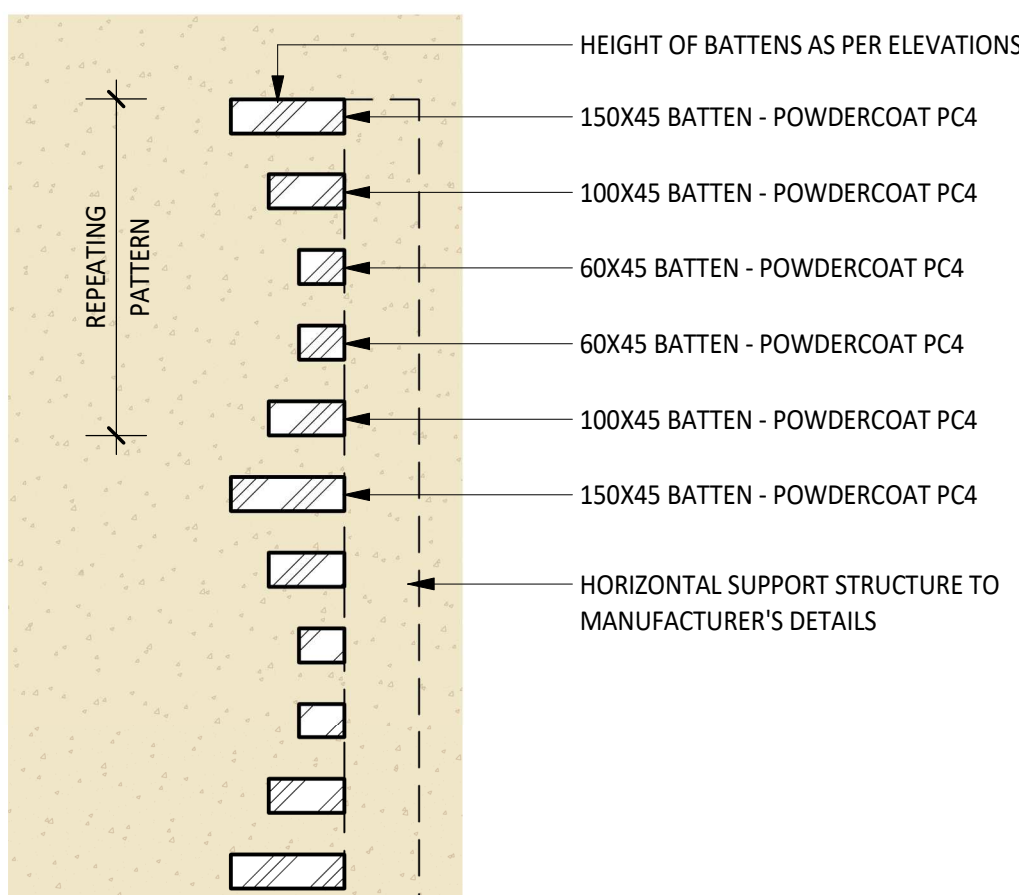
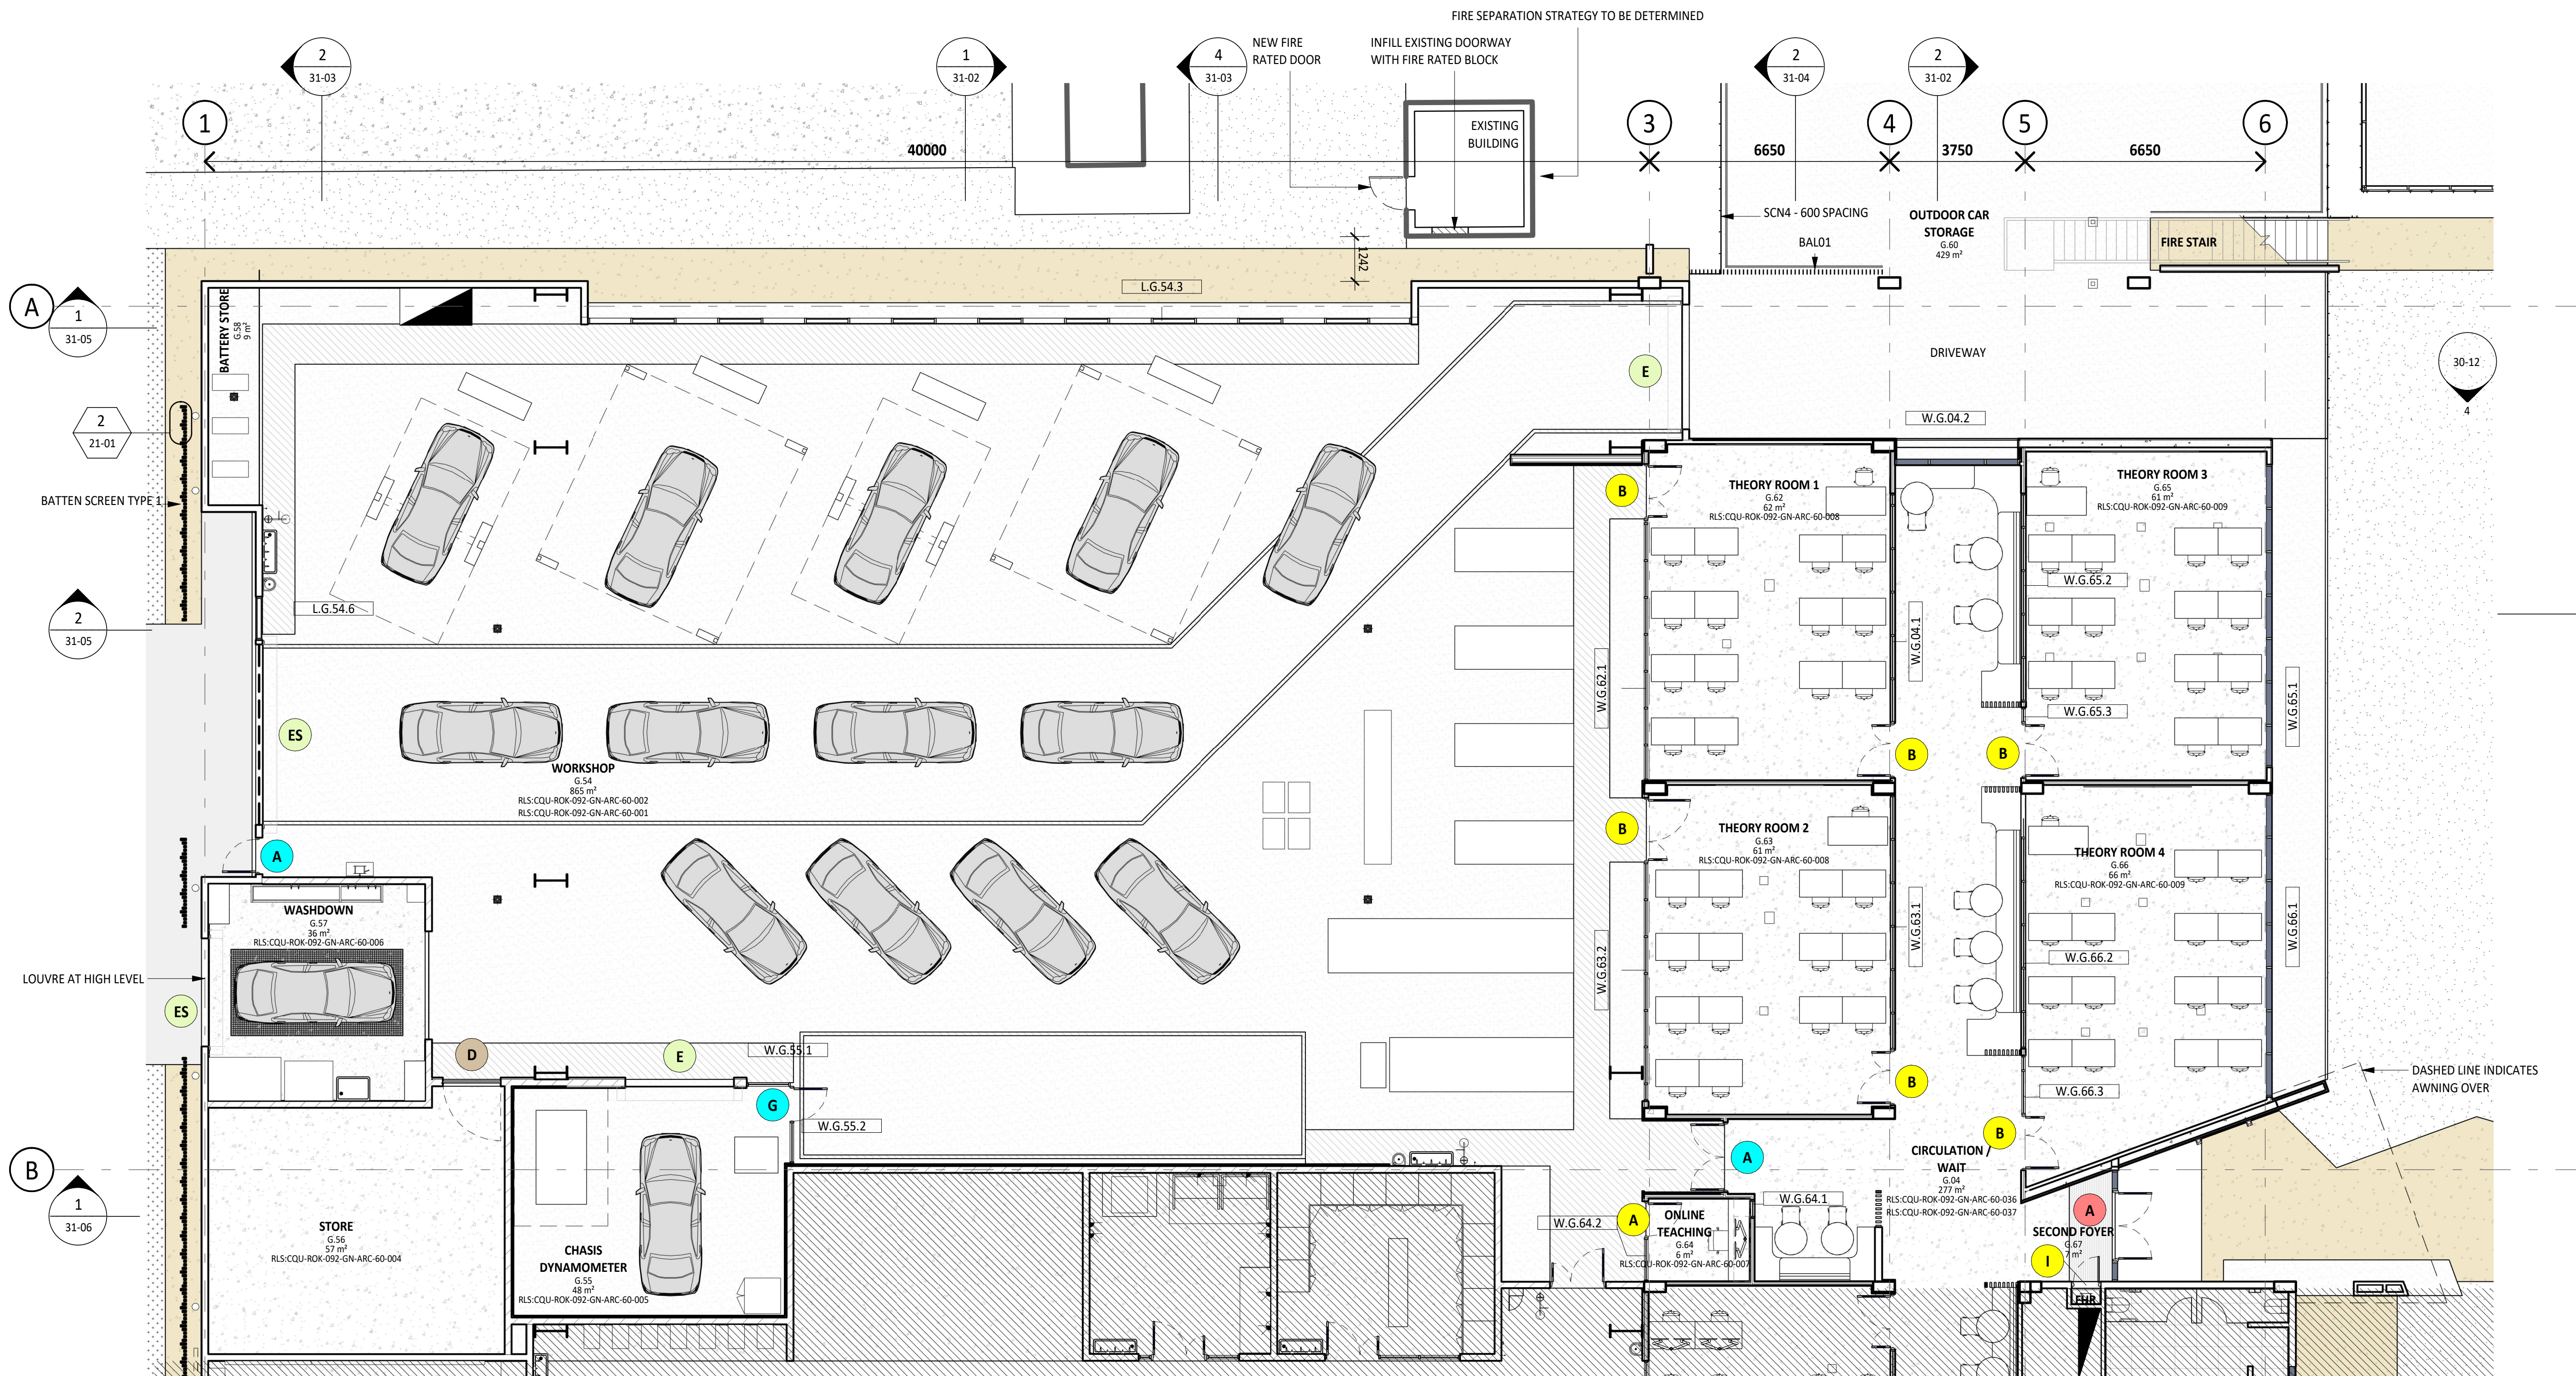
scale

**FLOOR PLAN GROUND
LEVEL - ZONE 1**

scale	project no.
As indicated @ A1	260018
revision	
B	
sheet no.	
CQU-ROK-092-GN-ARC-21-01	

original sheet size - A1 (594mm x 841mm)

ISSUED FOR TENDER

**2 PLAN DETAIL - BATTEN SCREEN TYPE 1 - BST 1**
21-01 1 : 10

ACCESS TYPE	
A	CARD READER ACCESS
B	TURN SNIB (NO KEY)
C	PRIVACY SET & TURN SNIB
D	MORTICE LOCK & KEY CYLINDER
E	ROLLER DOOR LOCK
F	LEVER WITH COMPRESSION LOCKING MECHANISM
G	FREE LEVER ACCESS
H	PUSH & PULL ACCESS
I	ROLLER LATCH
J	FREE LEVER EGRESS
S	ROLLER SHUTTER INCLUDES SAFETY CHAIN TO BE HUNG WHEN SHUTTER IS HELD OPEN

ICON LEGEND	
XX	ACCESS TYPE (TYPE MARK)
XX	DOOR TYPE (COLOUR SHADE)

DOOR TYPE

XX	SOLID CORE DOOR
XX	GLAZED SLIDER DOOR
XX	SOLID CORE DOOR WITH 600W x 900H VISION PANEL
XX	AUTO-SLIDER DOOR
XX	GLAZED STACKER DOOR
XX	BIFOLD DOOR
XX	ROLLER SHUTTER
XX	ACOUSTIC STACKER DOOR
XX	GLAZED SWING DOOR
XX	SWING GATE - ALUMINIUM BATTEN
XX	SLIDING GATE - AUTOMATIC OPERATION

GENERAL NOTE

- ALL DOORS IN WORKSHOP AREA TO HAVE 900 HIGH STAINLESS STEEL TROLLEY PLATE TO BOTH SIDES
- REFER TO MECHANICAL DRAWINGS FOR GRILLE AND UNDERCUT
- ALL SERVICE DOORS TO HAVE SMOKE SEALS
- FOR GLAZED DOORS REFER TO ROOM LAYOUT SHEET FOR EXTENT, WHICH NOTES SAFETY VISUAL GLAZING / PRIVACY SCREENING.
- DOOR FUNCTION AND HARDWARE TO BE IN ACCORDANCE TO CQU GUIDELINES.
- ANY DOOR ACCESS TO BATHROOM TO HAVE STAINLESS STEEL KICKPLATE
- ALLOW FOR DOOR CLOSERS AND DOOR STOPS TO DOORS
- EXTERNAL DOORS TO BE MANUALLY OPERATED, OPENING OUTWARDS. ENSURE THIS COMPLIES WITH AS 1428.1
- FIRE RATED DOORS TO HAVE PUSH BAR FOR EXIT.
- SINGLE SWING DOORS FOR CIRCULATION ACCESS TO BE 920MM WIDE, UNLESS SPECIFIED
- ALL EXTERNAL DOORS, LECTURE THEATRE DOORS, PLANT ROOMS, TOILET DOORS, FIRES DOORS AND EMERGENCY EXIT TO HAVE AUTO-CLOSER DOORS
- CQU TO CONFIRM ACCESS REQUIREMENT TO OFFICES AND CLASSROOMS
- EXTERNALLY LOCKED DOORS TO HAVE STRIKER PLATE PROTECTION INSTALLED
- REFER TO CQU DESIGN GUIDELINES FOR DESIGN AND CONSTRUCTION REQUIREMENTS.
- REFER TO ROOM LAYOUT SHEET FOR EXTENT OF WORK.
- DRAWINGS TO BE READ IN CONJUNCTION WITH SERVICES, CIVIL AND STRUCTURAL DRAWINGS.
- ALL EXTERNAL DOORS TO HAVE REED SWITCH
- ALL DOORS TO HAVE **MONITORED** ELECTRIC STRIKE SWIPE CARD ACCESS, PLUS MASTERKEY LOCK AND CYLINDER. EXCEPTIONS ARE - MEETING ROOM DOORS - INCLUDE MASTERKEY LOCK AND CYLINDER, PLUS SNIB - NO SWIPE. ELECTRICAL CUPBOARDS - INCLUDE MASTERKEY LOCK AND CYLINDER - NO SWIPE OR SNIB
- CONTRACTOR TO ALLOW FOR POWER AND DATA TO ALL DOORS WITH SWIPE ACCESS

FIRE MANAGEMENT LEGEND

	FIRE RATED WALL - REFER TO PARTITION DETAILS FOR MORE INFO
	SMOKE COMPARTMENT WALL
PLANS TO BE PRINTED IN COLOUR	