

**CQU ROCKHAMPTON
TAFE
CONSOLIDATION -
STAGE 2**554/700 Yaamba Rd, Norman
Gardens QLD 4701

for



A	12/02/26	ISSUED FOR TENDER	BS
3	30/01/26	DRAFT 60% ISSUE	BS
2	23/01/26	COORDINATION ISSUE FOR CONSULTANTS	BS
1	19/12/25	ISSUE FOR COORDINATION	BS
rev/	date	details	init.

drawn	date
PT	19/12/25
checked	date
use 'Approved By' only	19/12/25
verified	date
BS	19/12/25

scale

**FLOOR PLAN GROUND
LEVEL - ZONE 2**

scale	project no.
1 : 100 @ A1	260018

revision

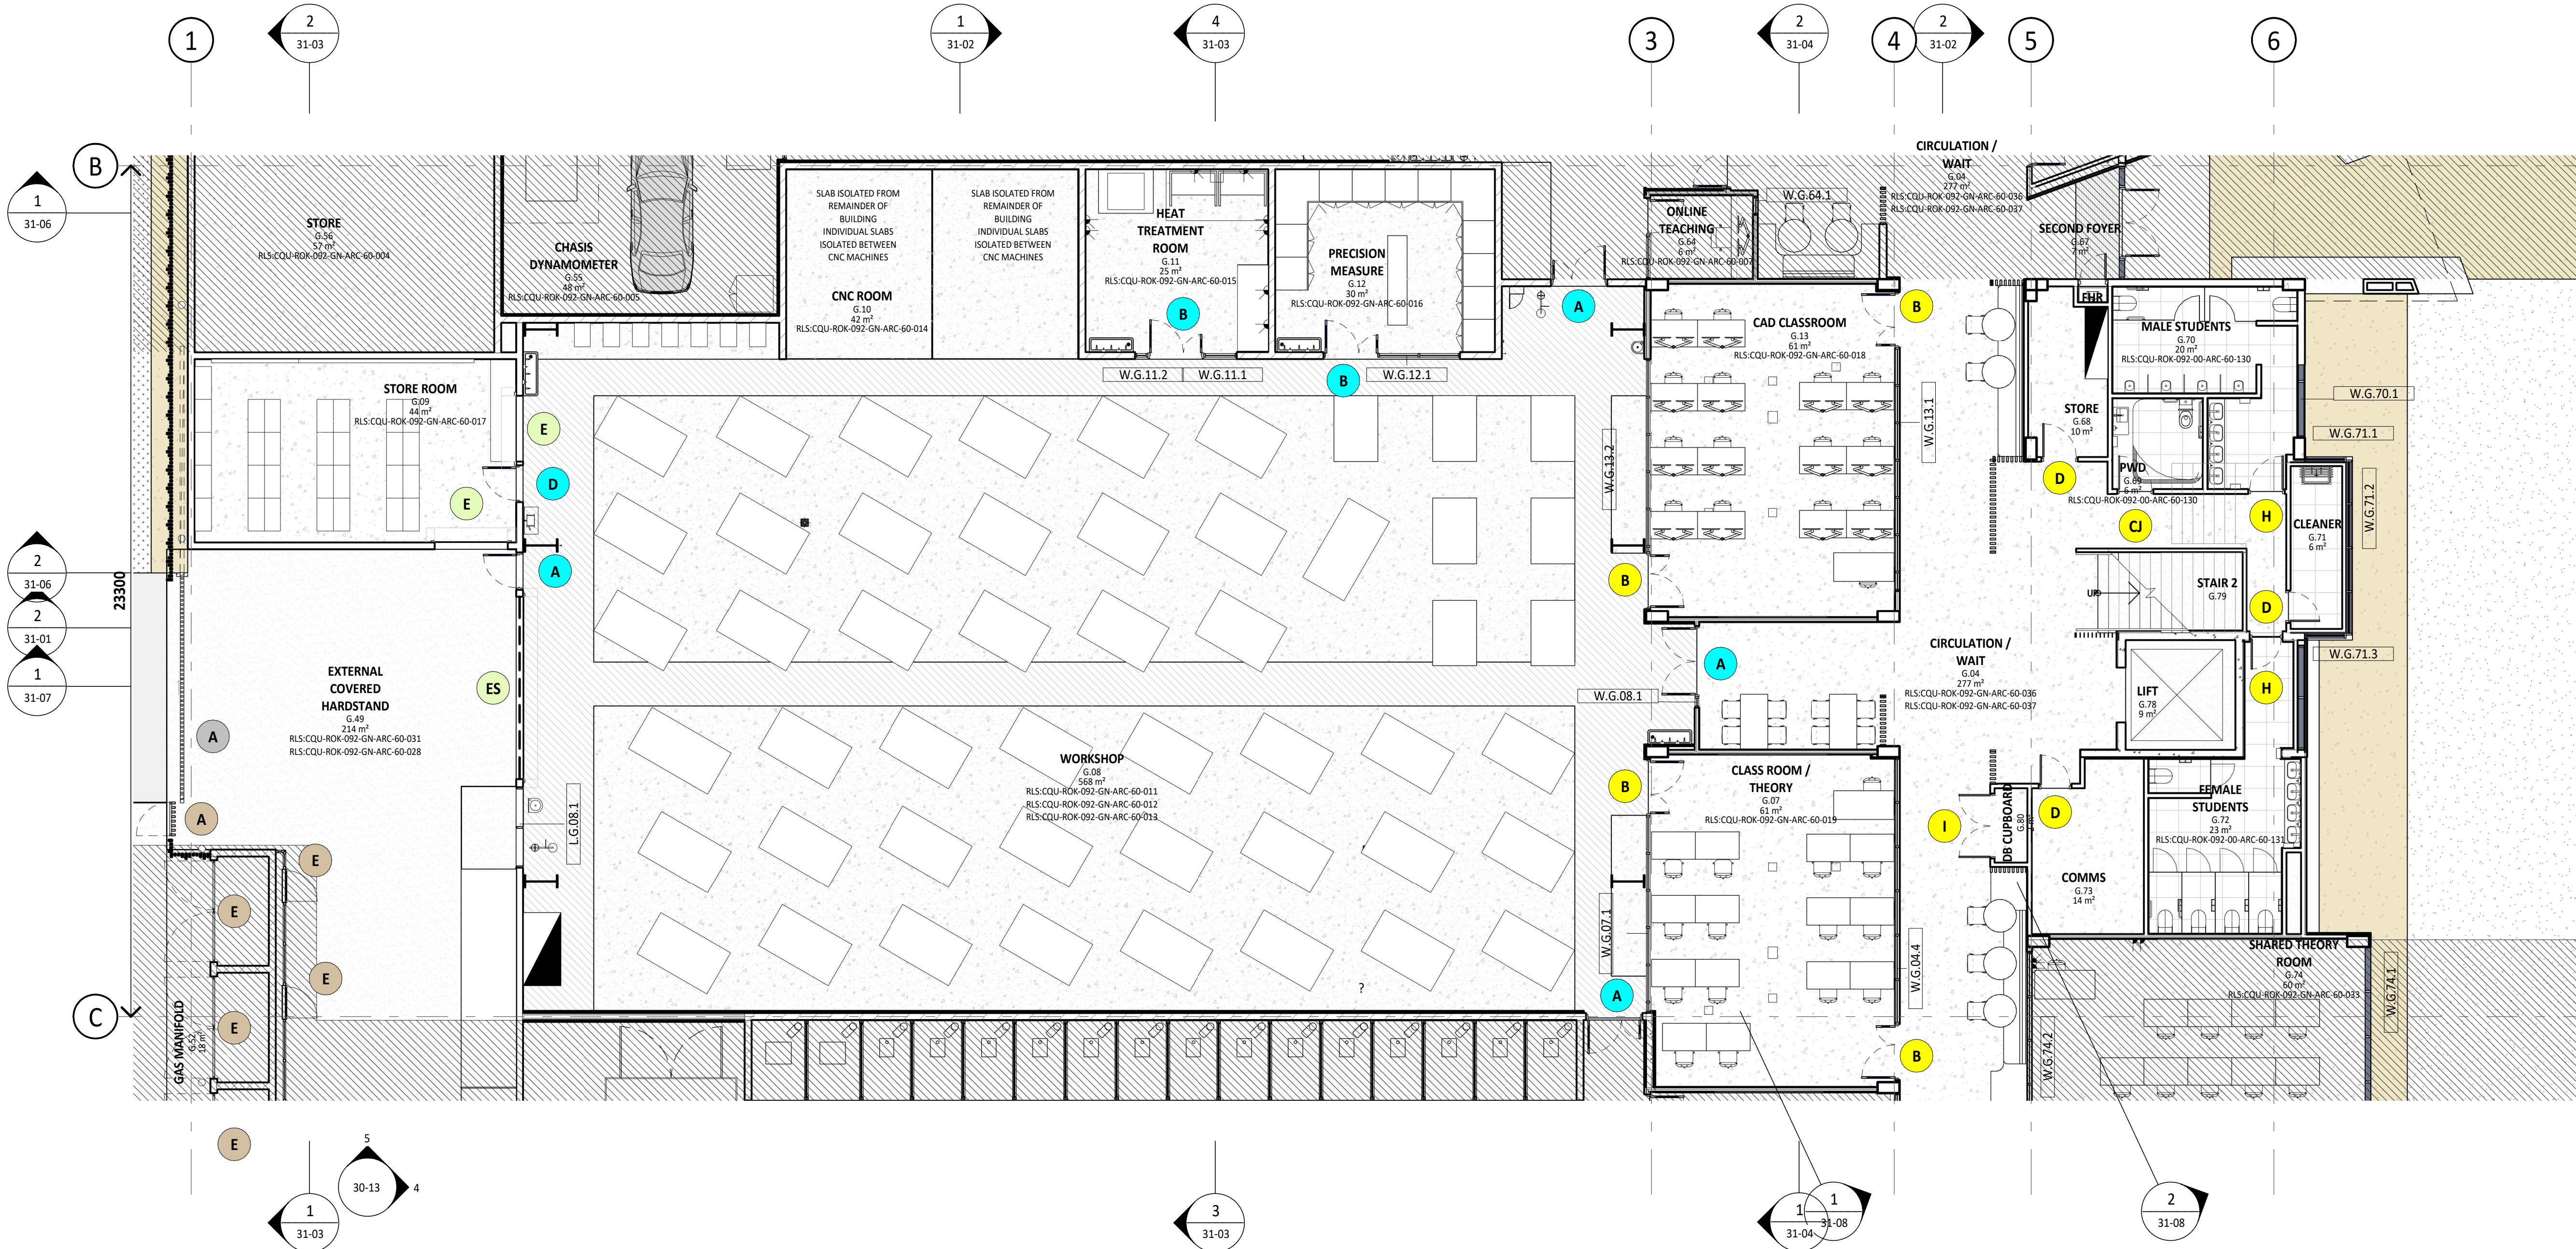
A

sheet no.

CQU-ROK-092-GN-ARC-21-02

original sheet size - A1 (594mm x 841mm)

ISSUED FOR TENDER

**GENERAL NOTE**

- ALL DOORS IN WORKSHOP AREA TO HAVE 900 HIGH STAINLESS STEEL TROLLEY PLATE TO BOTH SIDES
- REFER TO MECHANICAL DRAWINGS FOR GRILLE AND UNDERCUT
- ALL SERVICE DOORS TO HAVE SMOKE SEALS
- FOR GLAZED DOORS REFER TO ROOM LAYOUT SHEET FOR EXTENT, WHICH NOTES SAFETY VISUAL GLAZING / PRIVACY SCREENING.
- DOOR FUNCTION AND HARDWARE TO BE IN ACCORDANCE TO CQU GUIDELINES.
- ANY DOOR ACCESS TO BATHROOM TO HAVE STAINLESS STEEL KICKPLATE
- ALLOW FOR DOOR CLOSERS AND DOOR STOPS TO DOORS
- EXTERNAL DOORS TO BE MANUALLY OPERATED, OPENING OUTWARDS. ENSURE THIS COMPLIES WITH AS 1428.1
- FIRE RATED DOORS TO HAVE PUSH BAR FOR EXIT.
- SINGLE SWING DOORS FOR CIRCULATION ACCESS TO BE 920MM WIDE, UNLESS SPECIFIED
- ALL EXTERNAL DOORS, LECTURE THEATRE DOORS, PLANT ROOMS, TOILET DOORS, FIRES DOORS AND EMERGENCY EXIT TO HAVE AUTO-CLOSER DOORS
- CQU TO CONFIRM ACCESS REQUIREMENT TO OFFICES AND CLASSROOMS
- EXTERNALLY LOCKED DOORS TO HAVE STRIKER PLATE PROTECTION INSTALLED
- REFER TO CQU DESIGN GUIDELINES FOR DESIGN AND CONSTRUCTION REQUIREMENTS.
- REFER TO ROOM LAYOUT SHEET FOR EXTENT OF WORK.
- DRAWINGS TO BE READ IN CONJUNCTION WITH SERVICES, CIVIL AND STRUCTURAL DRAWINGS.
- ALL EXTERNAL DOORS TO HAVE REED SWITCH
- ALL DOORS TO HAVE **MONITORED** ELECTRIC STRIKE SWIPE CARD ACCESS, PLUS MASTERKEY LOCK AND CYLINDER. EXCEPTIONS ARE - MEETING ROOM DOORS - INCLUDE MASTERKEY LOCK AND CYLINDER, PLUS SNIB - NO SWIPE. ELECTRICAL CUPBOARDS - INCLUDE MASTERKEY LOCK AND CYLINDER - NO SWIPE OR SNIB
- CONTRACTOR TO ALLOW FOR POWER AND DATA TO ALL DOORS WITH SWIPE ACCESS

DOOR TYPE

- XX** SOLID CORE DOOR
- XX** GLAZED SLIDER DOOR
- XX** SOLID CORE DOOR WITH 600W x 900H VISION PANEL
- XX** AUTO-SLIDER DOOR
- XX** GLAZED-STACKER DOOR
- XX** BIFOLD DOOR
- XX** ROLLER SHUTTER
- XX** ACOUSTIC STACKER DOOR
- XX** GLAZED SWING DOOR
- XX** SWING GATE - ALUMINIUM BATTEN
- XX** SLIDING GATE - AUTOMATIC OPERATION

ACCESS TYPE

- A** CARD READER ACCESS
- B** TURN SNIB (NO KEY)
- C** PRIVACY SET & TURN SNIB
- D** MORTICE LOCK & KEY CYLINDER
- E** ROLLER DOOR LOCK
- F** LEVER WITH COMPRESSION LOCKING MECHANISM
- G** FREE LEVER ACCESS
- H** PUSH & PULL ACCESS
- I** ROLLER LATCH
- J** FREE LEVER EGRESS
- S** ROLLER SHUTTER INCLUDES SAFETY CHAIN TO BE HUNG WHEN SHUTTER IS HELD OPEN

ICON LEGEND

- XX** ACCESS TYPE (TYPE MARK)
- XX** DOOR TYPE (COLOUR SHADE)

FIRE MANAGEMENT LEGEND

- FIRE RATED WALL - REFER TO PARTITION DETAILS FOR MORE INFO
- SMOKE COMPARTMENT WALL
- PLANS TO BE PRINTED IN COLOUR