


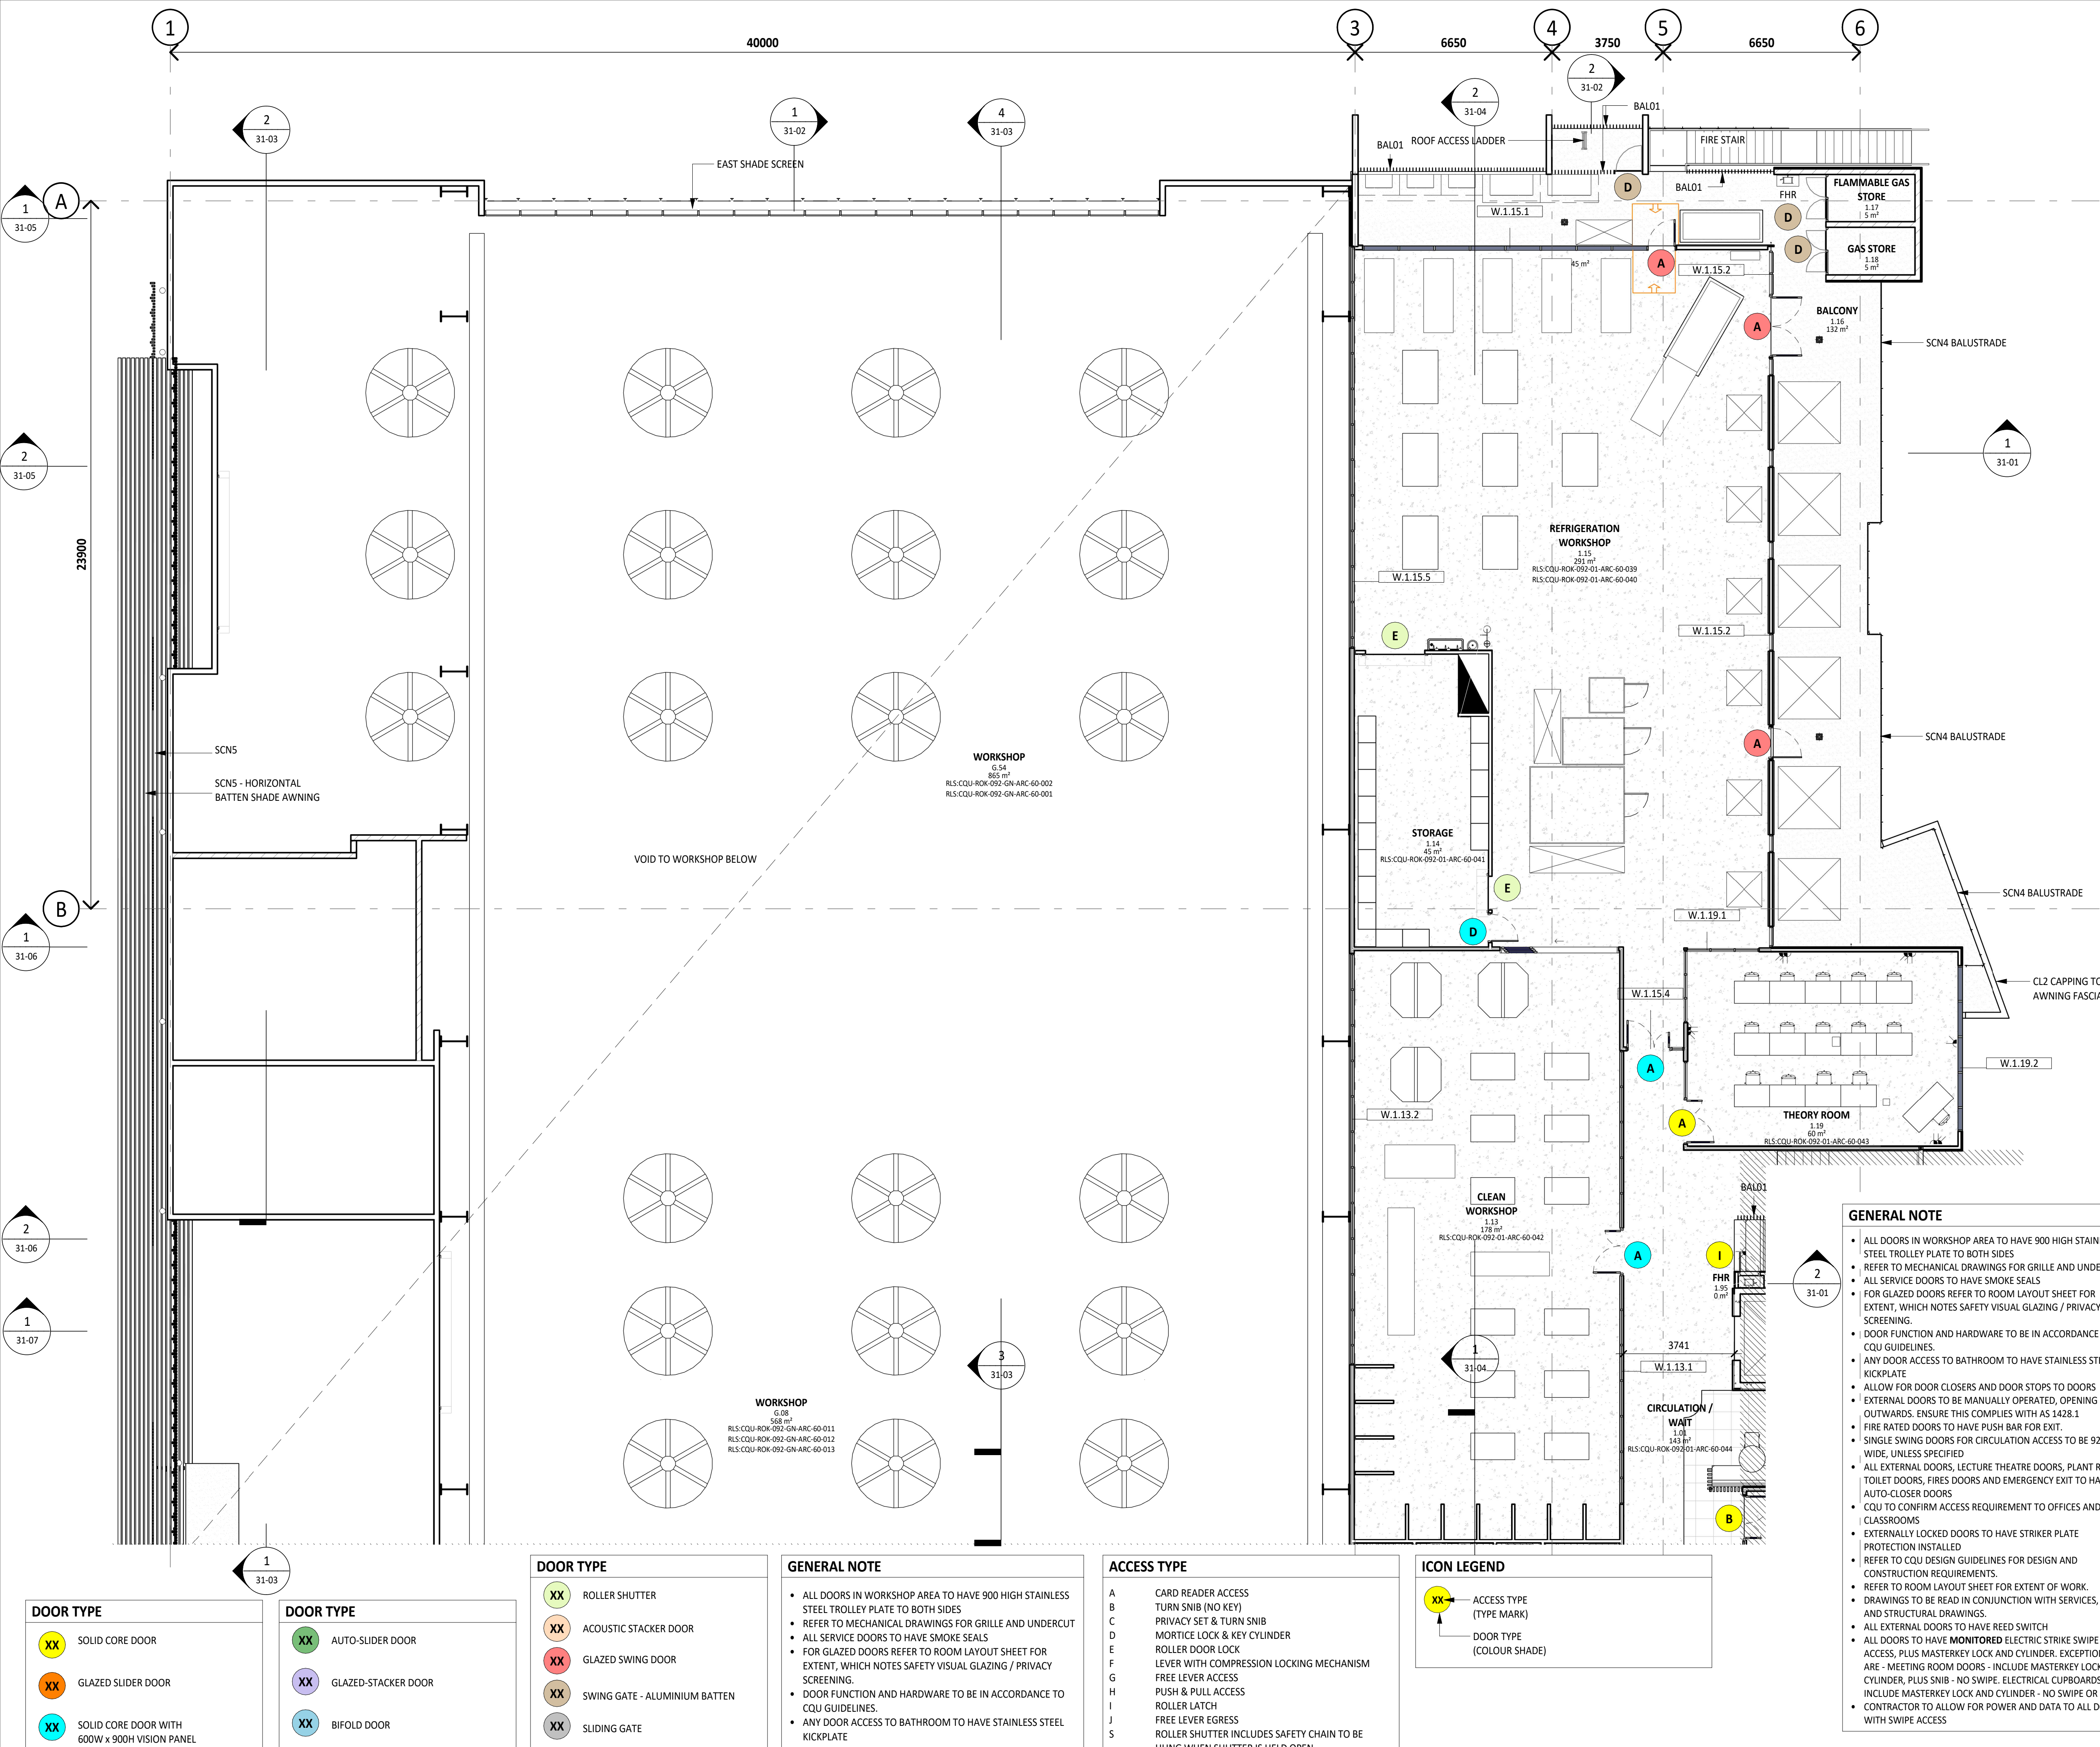

CQU ROCKHAMPTON TAFE CONSOLIDATION - STAGE 2

554/700 Yaamba Rd, Norman
Gardens QLD 4701



A	12/02/26	ISSUED FOR TENDER	BS
3	30/01/26	DRAFT 60% ISSUE	BS
2	23/01/26	COORDINATION ISSUE FOR CONSULTANTS	BS
1	19/12/25	ISSUE FOR COORDINATION	BS
rev	date	details	init.

drawn	date
PT	19/12/25
checked	date
use 'Approved By' only	19/12/25
verified	date
BS	19/12/25

scale	
1 : 100 @ A1	260018
revision	
A	
sheet no.	

FLOOR PLAN LEVEL 01 - ZONE 1

scale	project no.
1 : 100 @ A1	260018
revision	
A	
sheet no.	

CQU-ROK-092-01-ARC-21-11

ISSUED FOR TENDER

