


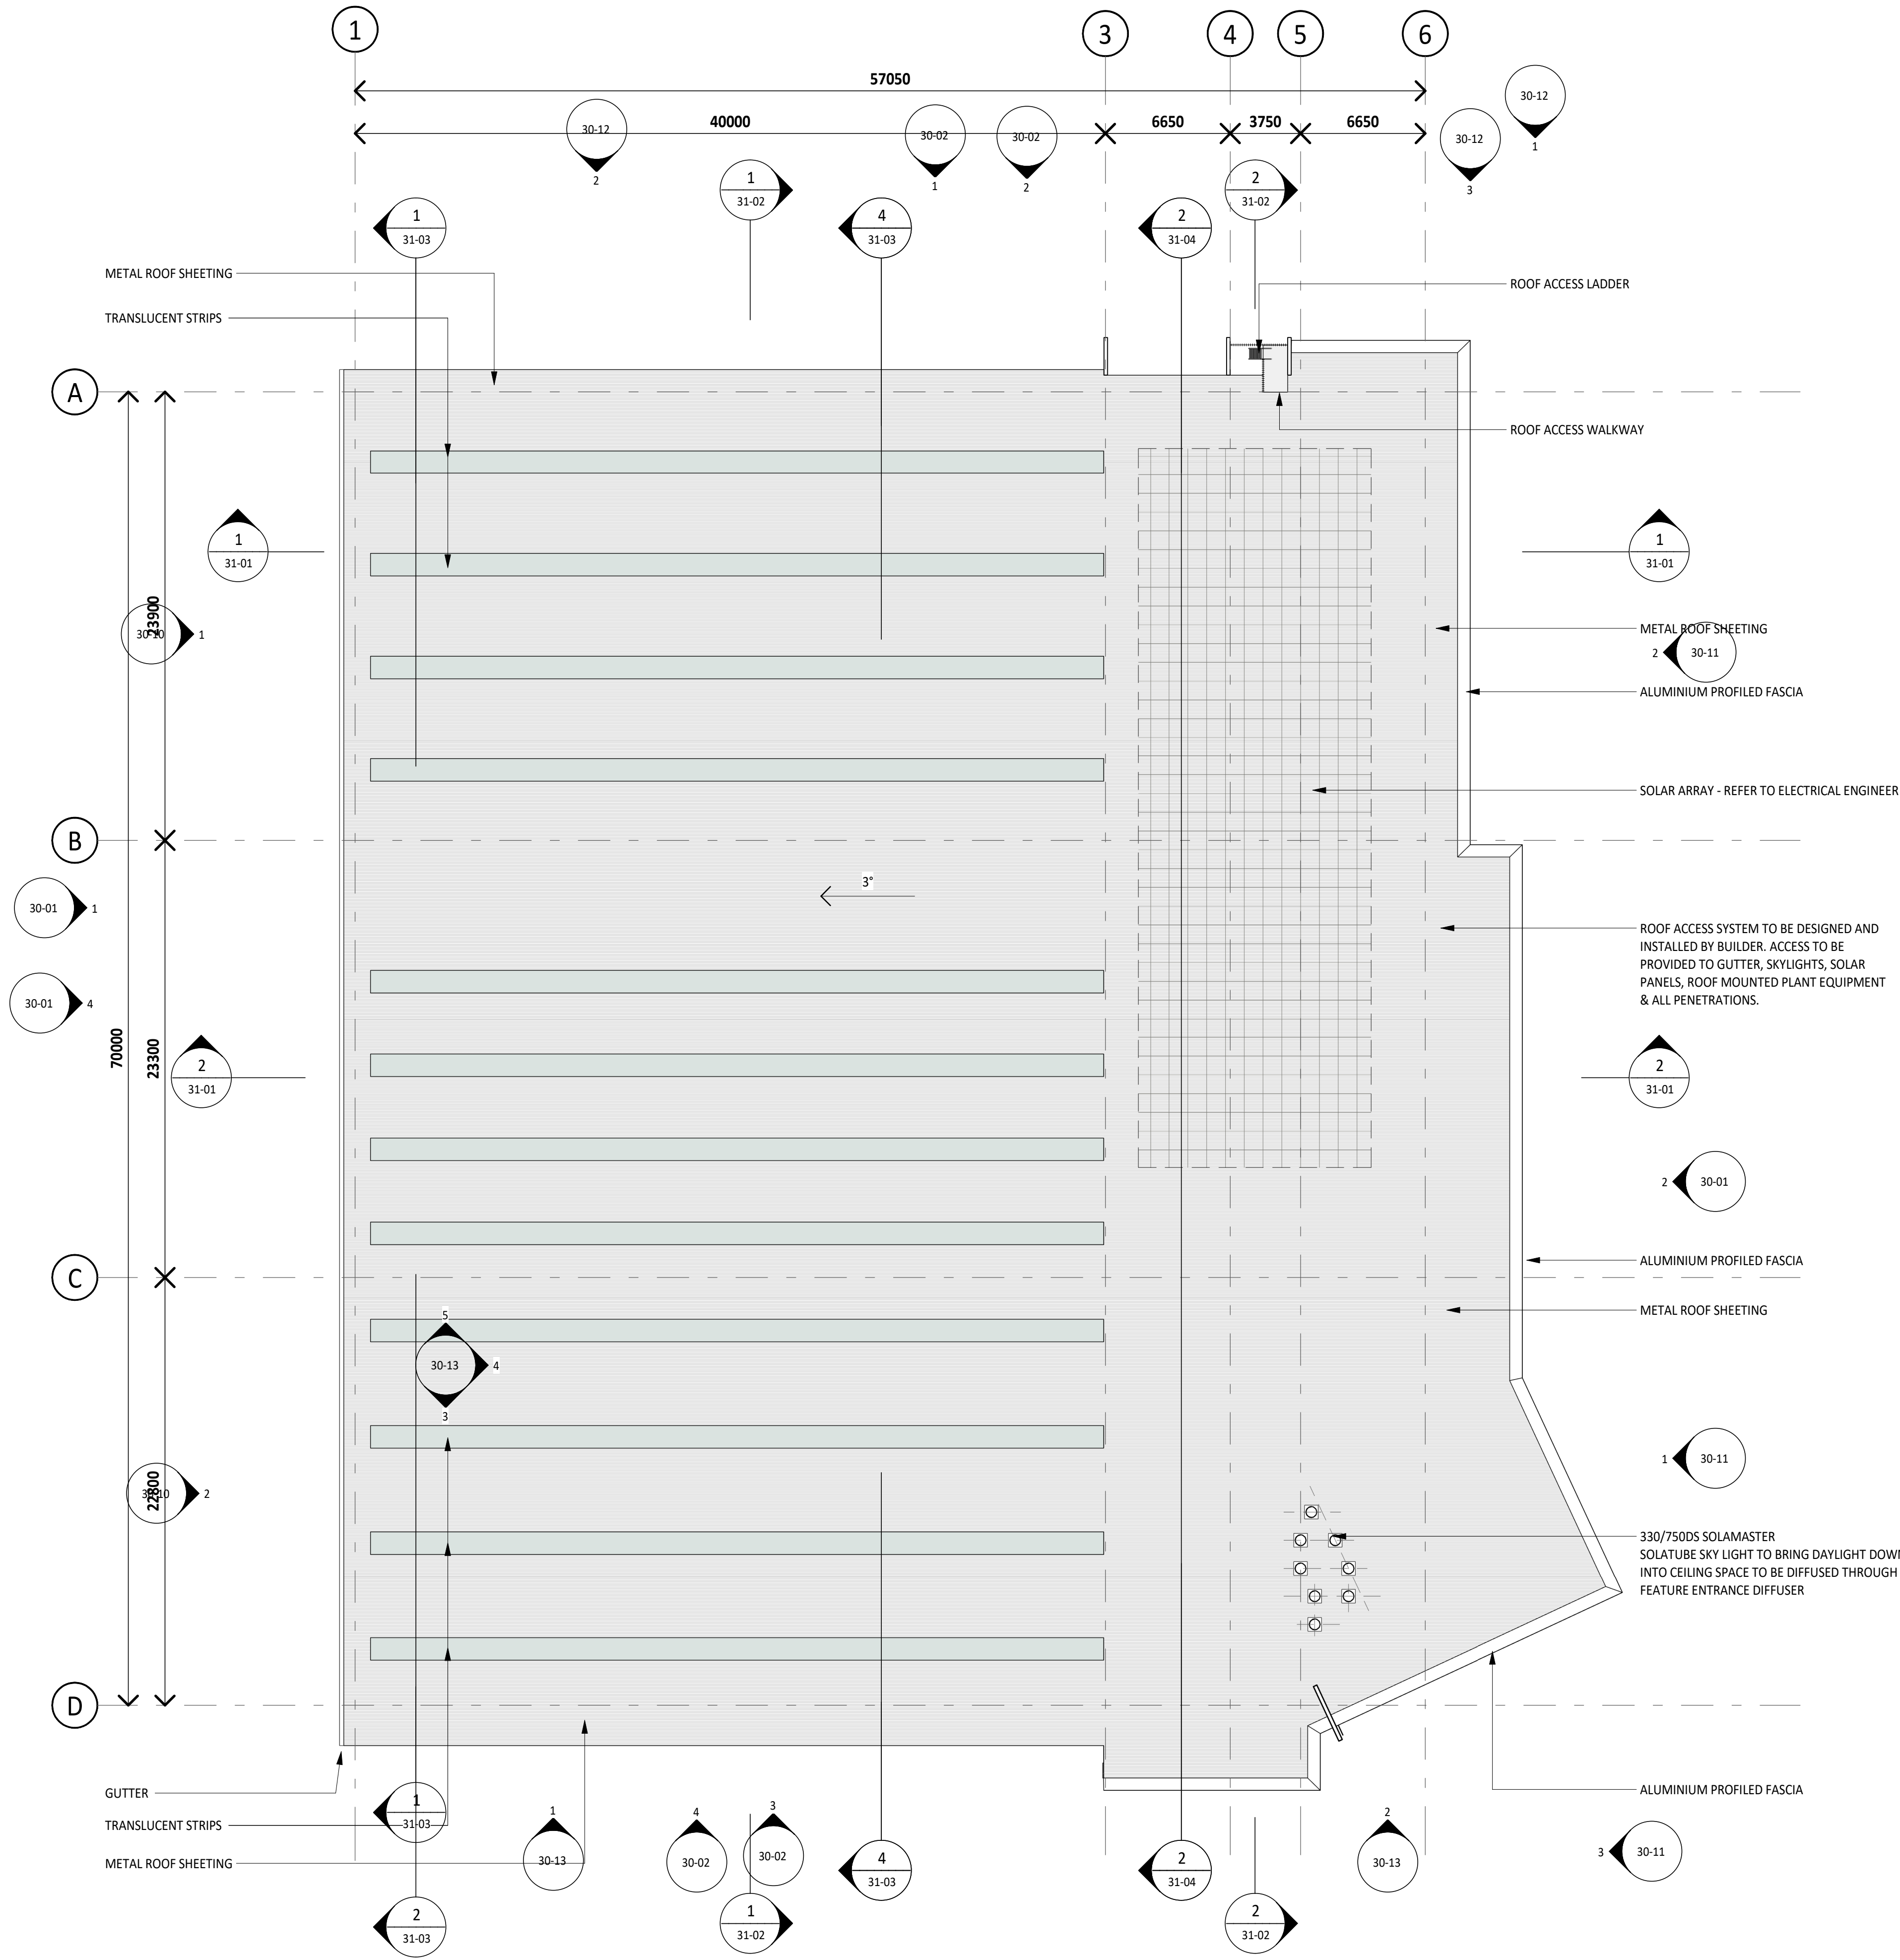

**CQU ROCKHAMPTON
TAFE
CONSOLIDATION -
STAGE 2**

554/700 Yaamba Rd, Norman
Gardens QLD 4701



A	12/02/26	ISSUED FOR TENDER	BS
4	30/01/26	DRAFT 60% ISSUE	BS
3	23/01/26	COORDINATION ISSUE FOR CONSULTANTS	BS
2	19/12/25	ISSUE FOR COORDINATION	BS
1	24/11/25	50% COSTING ISSUE	BS
rev	date	details	init.

drawn	date
PT	19/12/25
checked	date
use 'Approved By' only	19/12/25
verified	date
BS	19/12/25

scale

GA PLAN ROOF LEVEL

scale
1 : 200 @ A1

project no.
260018

revision
A

sheet no.
CQU-ROK-092-RF-ARC-21-20

ISSUED FOR TENDER