


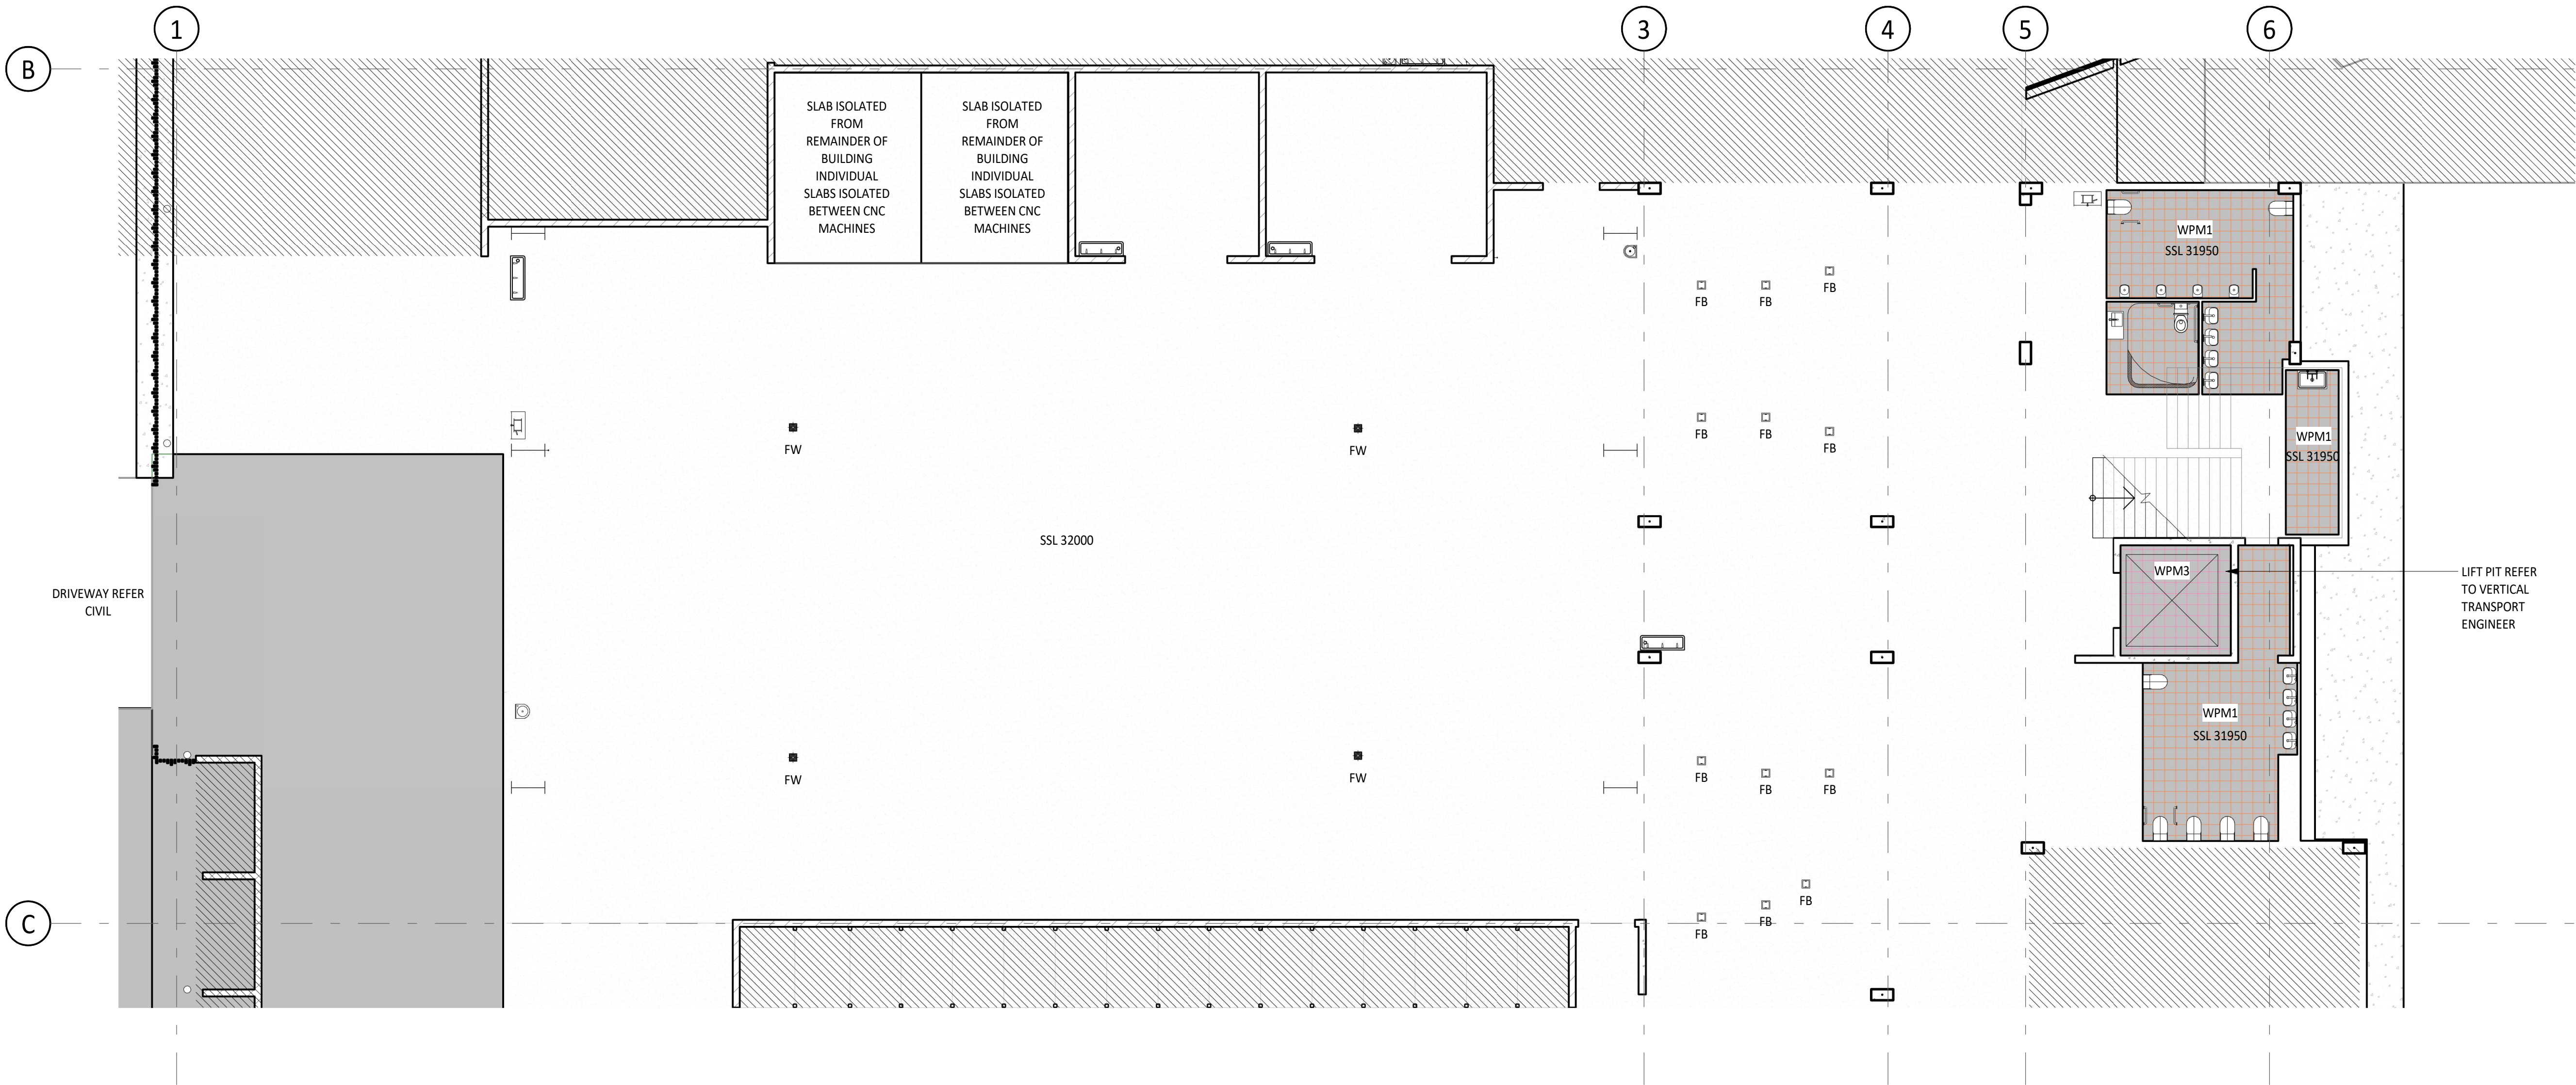

SLAB SETOUT LEGEND

--- JOINTS
REFER TO DETAILS FOR TYPICAL SLAB
EXPANSION JOINTS

[Grey Box] DENOTES SETDOWNS

FB - FLOOR BOX

FW - FLOOR WASTE

PLANS TO BE PRINTED IN COLOUR

WATERPROOFING LEGEND

[Orange Box] **WPM1**
WATERPROOFING TYPE 1

[Blue Box] **WPM2**
WATERPROOFING TYPE 2

[Pink Box] **WPM3**
WATERPROOFING TYPE 3

UNLESS NOTED OTHERWISE FLOORS WITH WATERPROOFING TO
HAVE MEMBRANE COVED TO MINIMUM 150 AFFL

PLANS TO BE PRINTED IN COLOUR

TO BE READ IN CONJUNCTION
WITH STRUCTURAL & SERVICES
ENGINEER'S DOCUMENTS

WALL SETOUTS

1500 ALL CONCRETE/MASONRY WALLS
DIMENSION FROM OUTSIDE / INSIDE
FACE OF WALL TO GRID

1500 ALL PARTITION WALLS DIMENSION
FROM CENTRE OF STUD TO GRID

ISSUED FOR TENDER

**STRUCTURAL SETOUT
GROUND LEVEL - ZONE 2**

scale 1 : 100 @ A1 project no. 260018

revision A sheet no. CQU-ROK-092-GN-ARC-23-02

**thomson
adsett**

PEDDLE THORP
architecture | interiors | health | planning

Telephone +61 7 3840 9999
bne@thomsonadsett.com
Level 9, 470 St Pauls Terrace
Fortitude Valley
Qld 4006 Australia
thomsonadsett.com

© Copyright
These drawings and designs and the copyright
thereof are the property of Thomson Adsett Pty
Ltd and must not be used, retained or copied
without written permission of Thomson Adsett
Pty Ltd. ABN 76 105 314 654 Trading as
ThomsonAdsett. Dimensions take precedence
over scaling. Do not measure off drawings as
print sizes may vary

**CQU ROCKHAMPTON
TAFE
CONSOLIDATION -
STAGE 2**

554/700 Yaamba Rd, Norman
Gardens QLD 4701

for

**CQUniversity
AUSTRALIA**

A	12/02/26	ISSUED FOR TENDER	BS
1	30/01/26	DRAFT 60% ISSUE	BS
rev	date	details	init.

drawn	date
PT	30/01/26
checked	date
BS	30/01/26
verified	date
BS	30/01/26

scale

1