


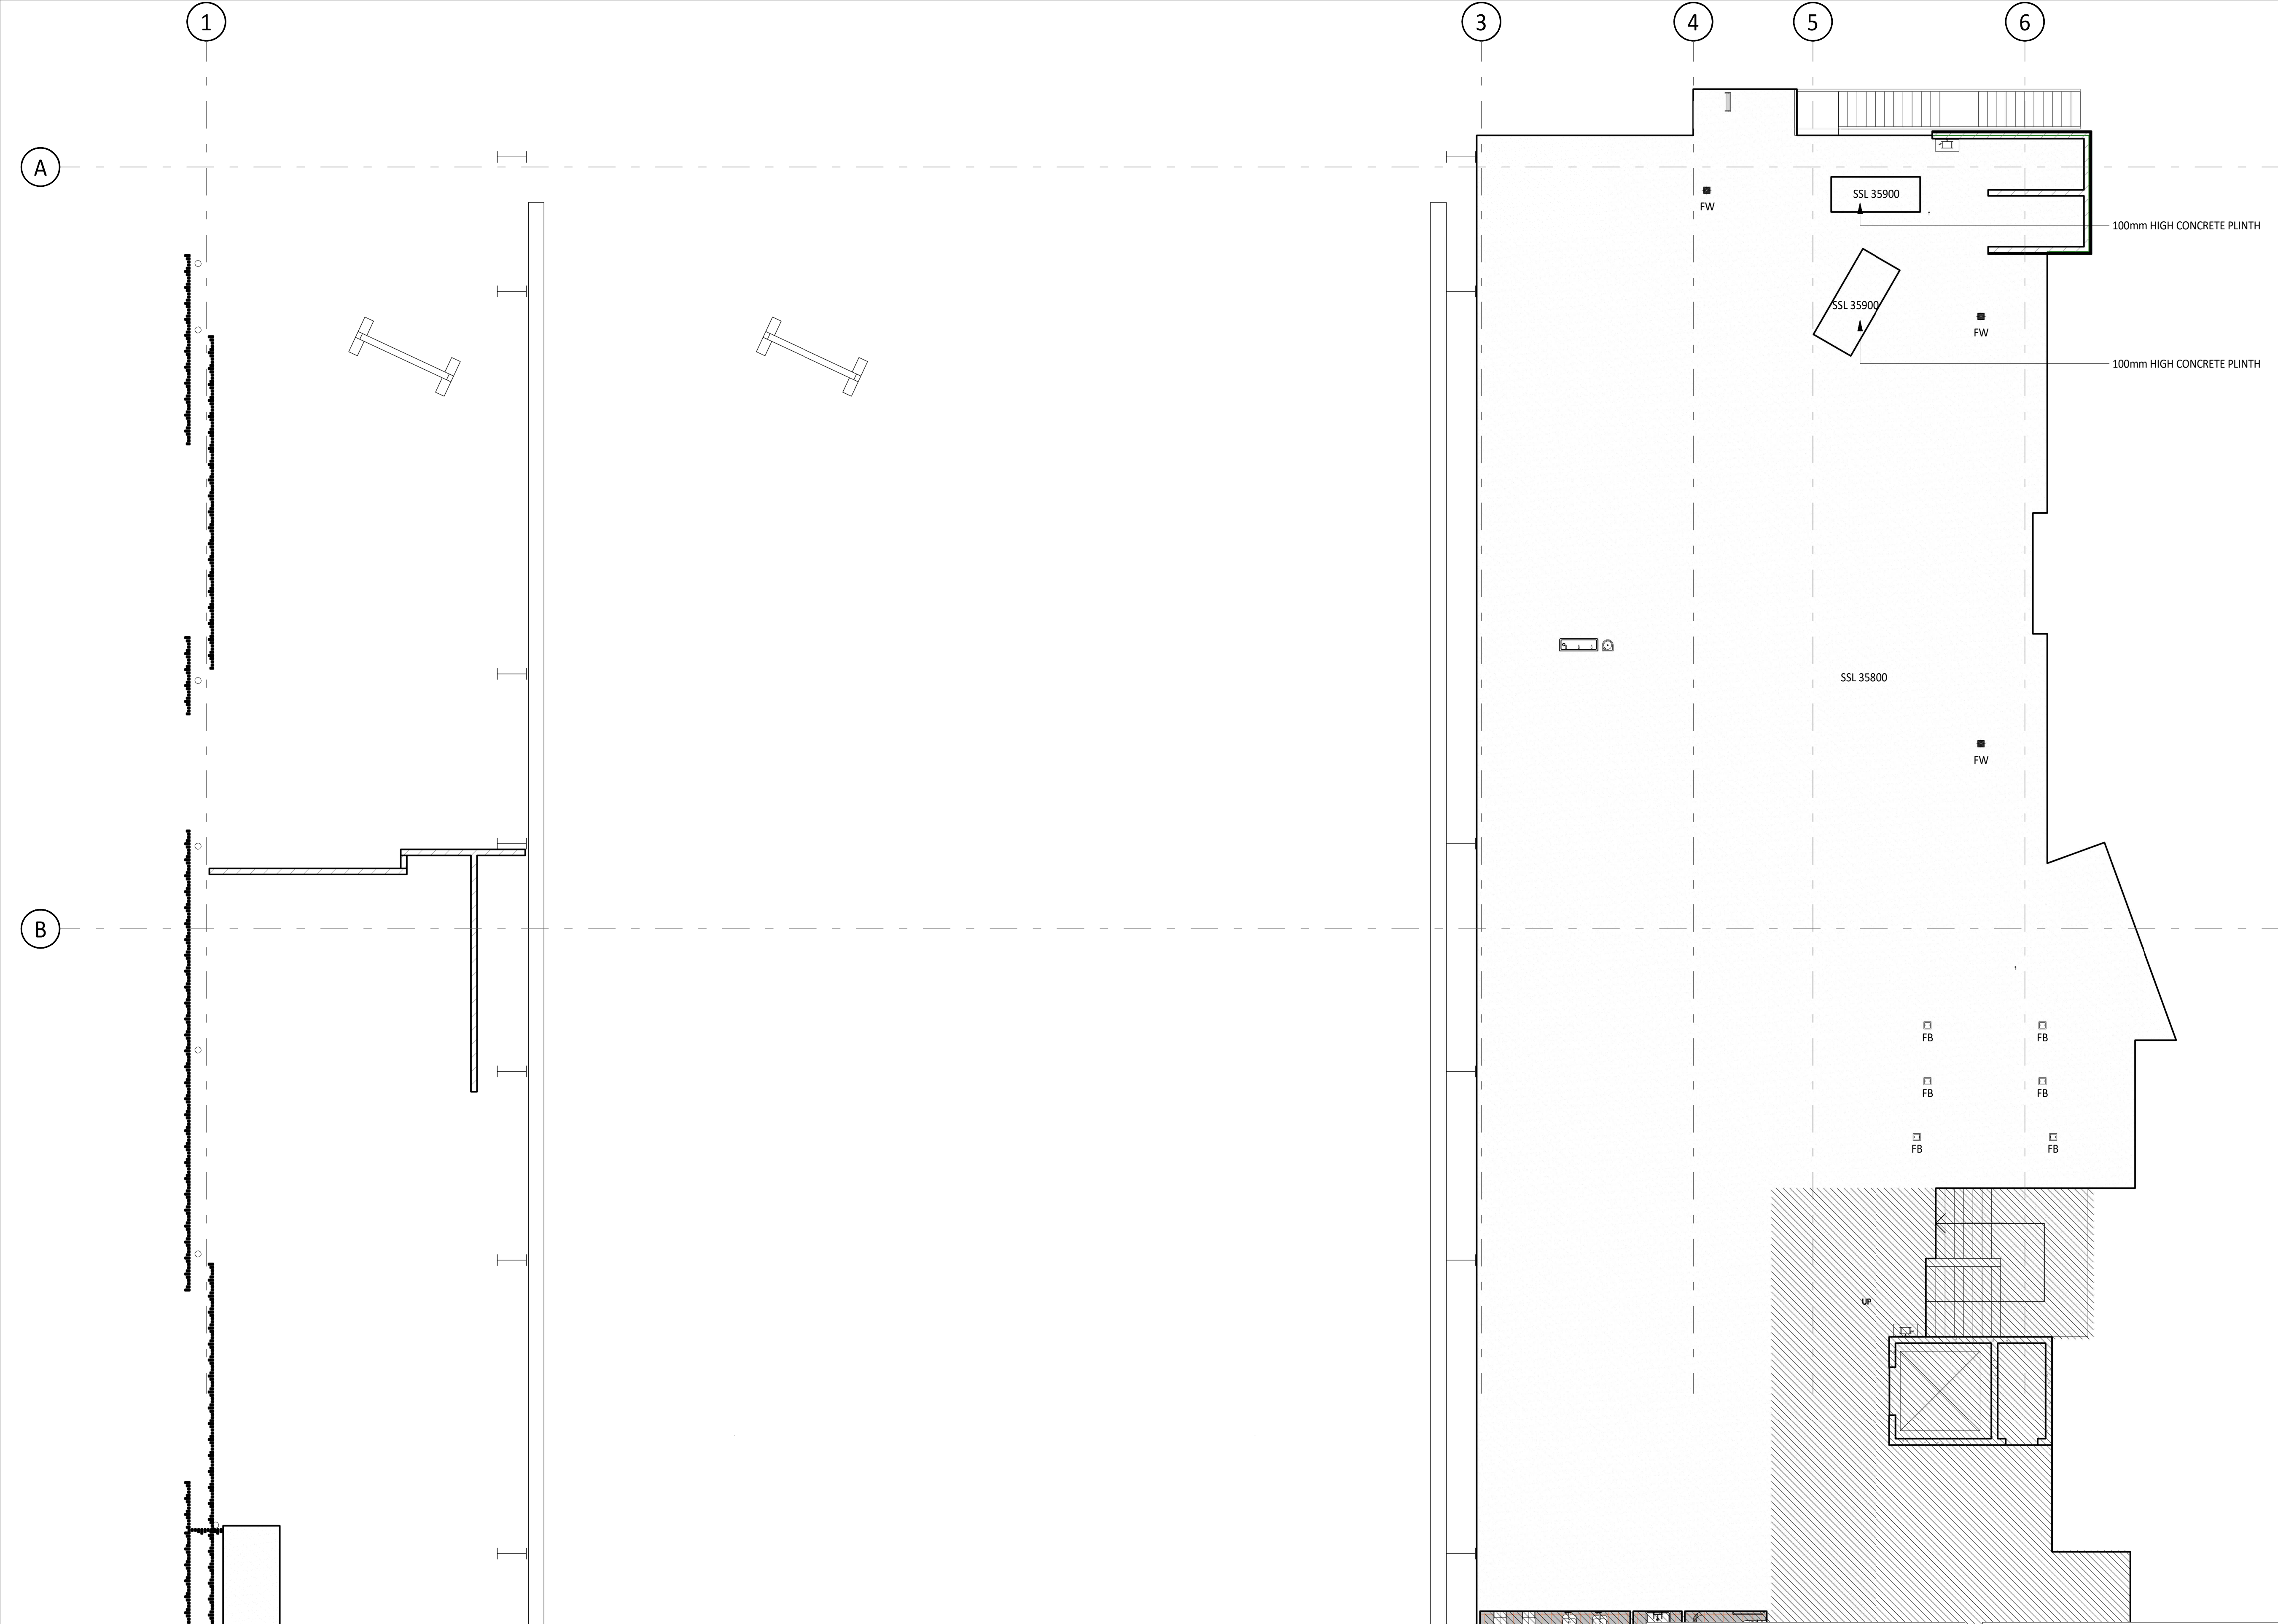

TO BE READ IN CONJUNCTION
WITH STRUCTURAL & SERVICES
ENGINEER'S DOCUMENTS

SLAB SETOUT LEGEND	
	JOINTS REFER TO DETAILS FOR TYPICAL SLAB EXPANSION JOINTS
	DENOTES SETDOWNS
	FB - FLOOR BOX
	FW - FLOOR WASTE
PLANS TO BE PRINTED IN COLOUR	

WATERPROOFING LEGEND	
	WPM1 WATERPROOFING TYPE 1
	WPM2 WATERPROOFING TYPE 2
	WPM3 WATERPROOFING TYPE 3
UNLESS NOTED OTHERWISE FLOORS WITH WATERPROOFING TO HAVE MEMBRANE COVED TO MINIMUM 150 AFFL	
PLANS TO BE PRINTED IN COLOUR	

WALL SETOUTS	
	1500 ALL CONCRETE/MASONRY WALLS DIMENSION FROM OUTSIDE / INSIDE FACE OF WALL TO GRID
	1500 ALL PARTITION WALLS DIMENSION FROM CENTRE OF STUD TO GRID

ISSUED FOR TENDER

STRUCTURAL SETOUT
LEVEL 01 - ZONE 1

scale project no.
1 : 100 @ A1 260018

revision
A
sheet no.
CQU-ROK-092-01-ARC-23-11

original sheet size - A1 (594mm x 841mm)

architecture | interiors | health | planning

Telephone +61 7 3840 9999
bne@thomsonadsett.com
Level 9, 470 St Pauls Terrace
Fortitude Valley
Qld 4006 Australia
thomsonadsett.com

© Copyright
These drawings and designs and the copyright
thereof are the property of Thomson Adsett Pty
Ltd and must not be used, retained or copied
without written permission of Thomson Adsett
Pty Ltd. ABN 76 105 314 654 Trading as
ThomsonAdsett. Dimensions take precedence
over scaling. Do not measure off drawings as
print sizes may vary

CQU ROCKHAMPTON
TAFE
CONSOLIDATION -
STAGE 2
554/700 Yaamba Rd, Norman
Gardens QLD 4701

for

A	12/02/26	ISSUED FOR TENDER	BS
1	30/01/26	DRAFT 60% ISSUE	BS
rev	date	details	init.

drawn	date
PT	30/01/26
checked	date
BS	30/01/26
verified	date
BS	30/01/26

scale

