


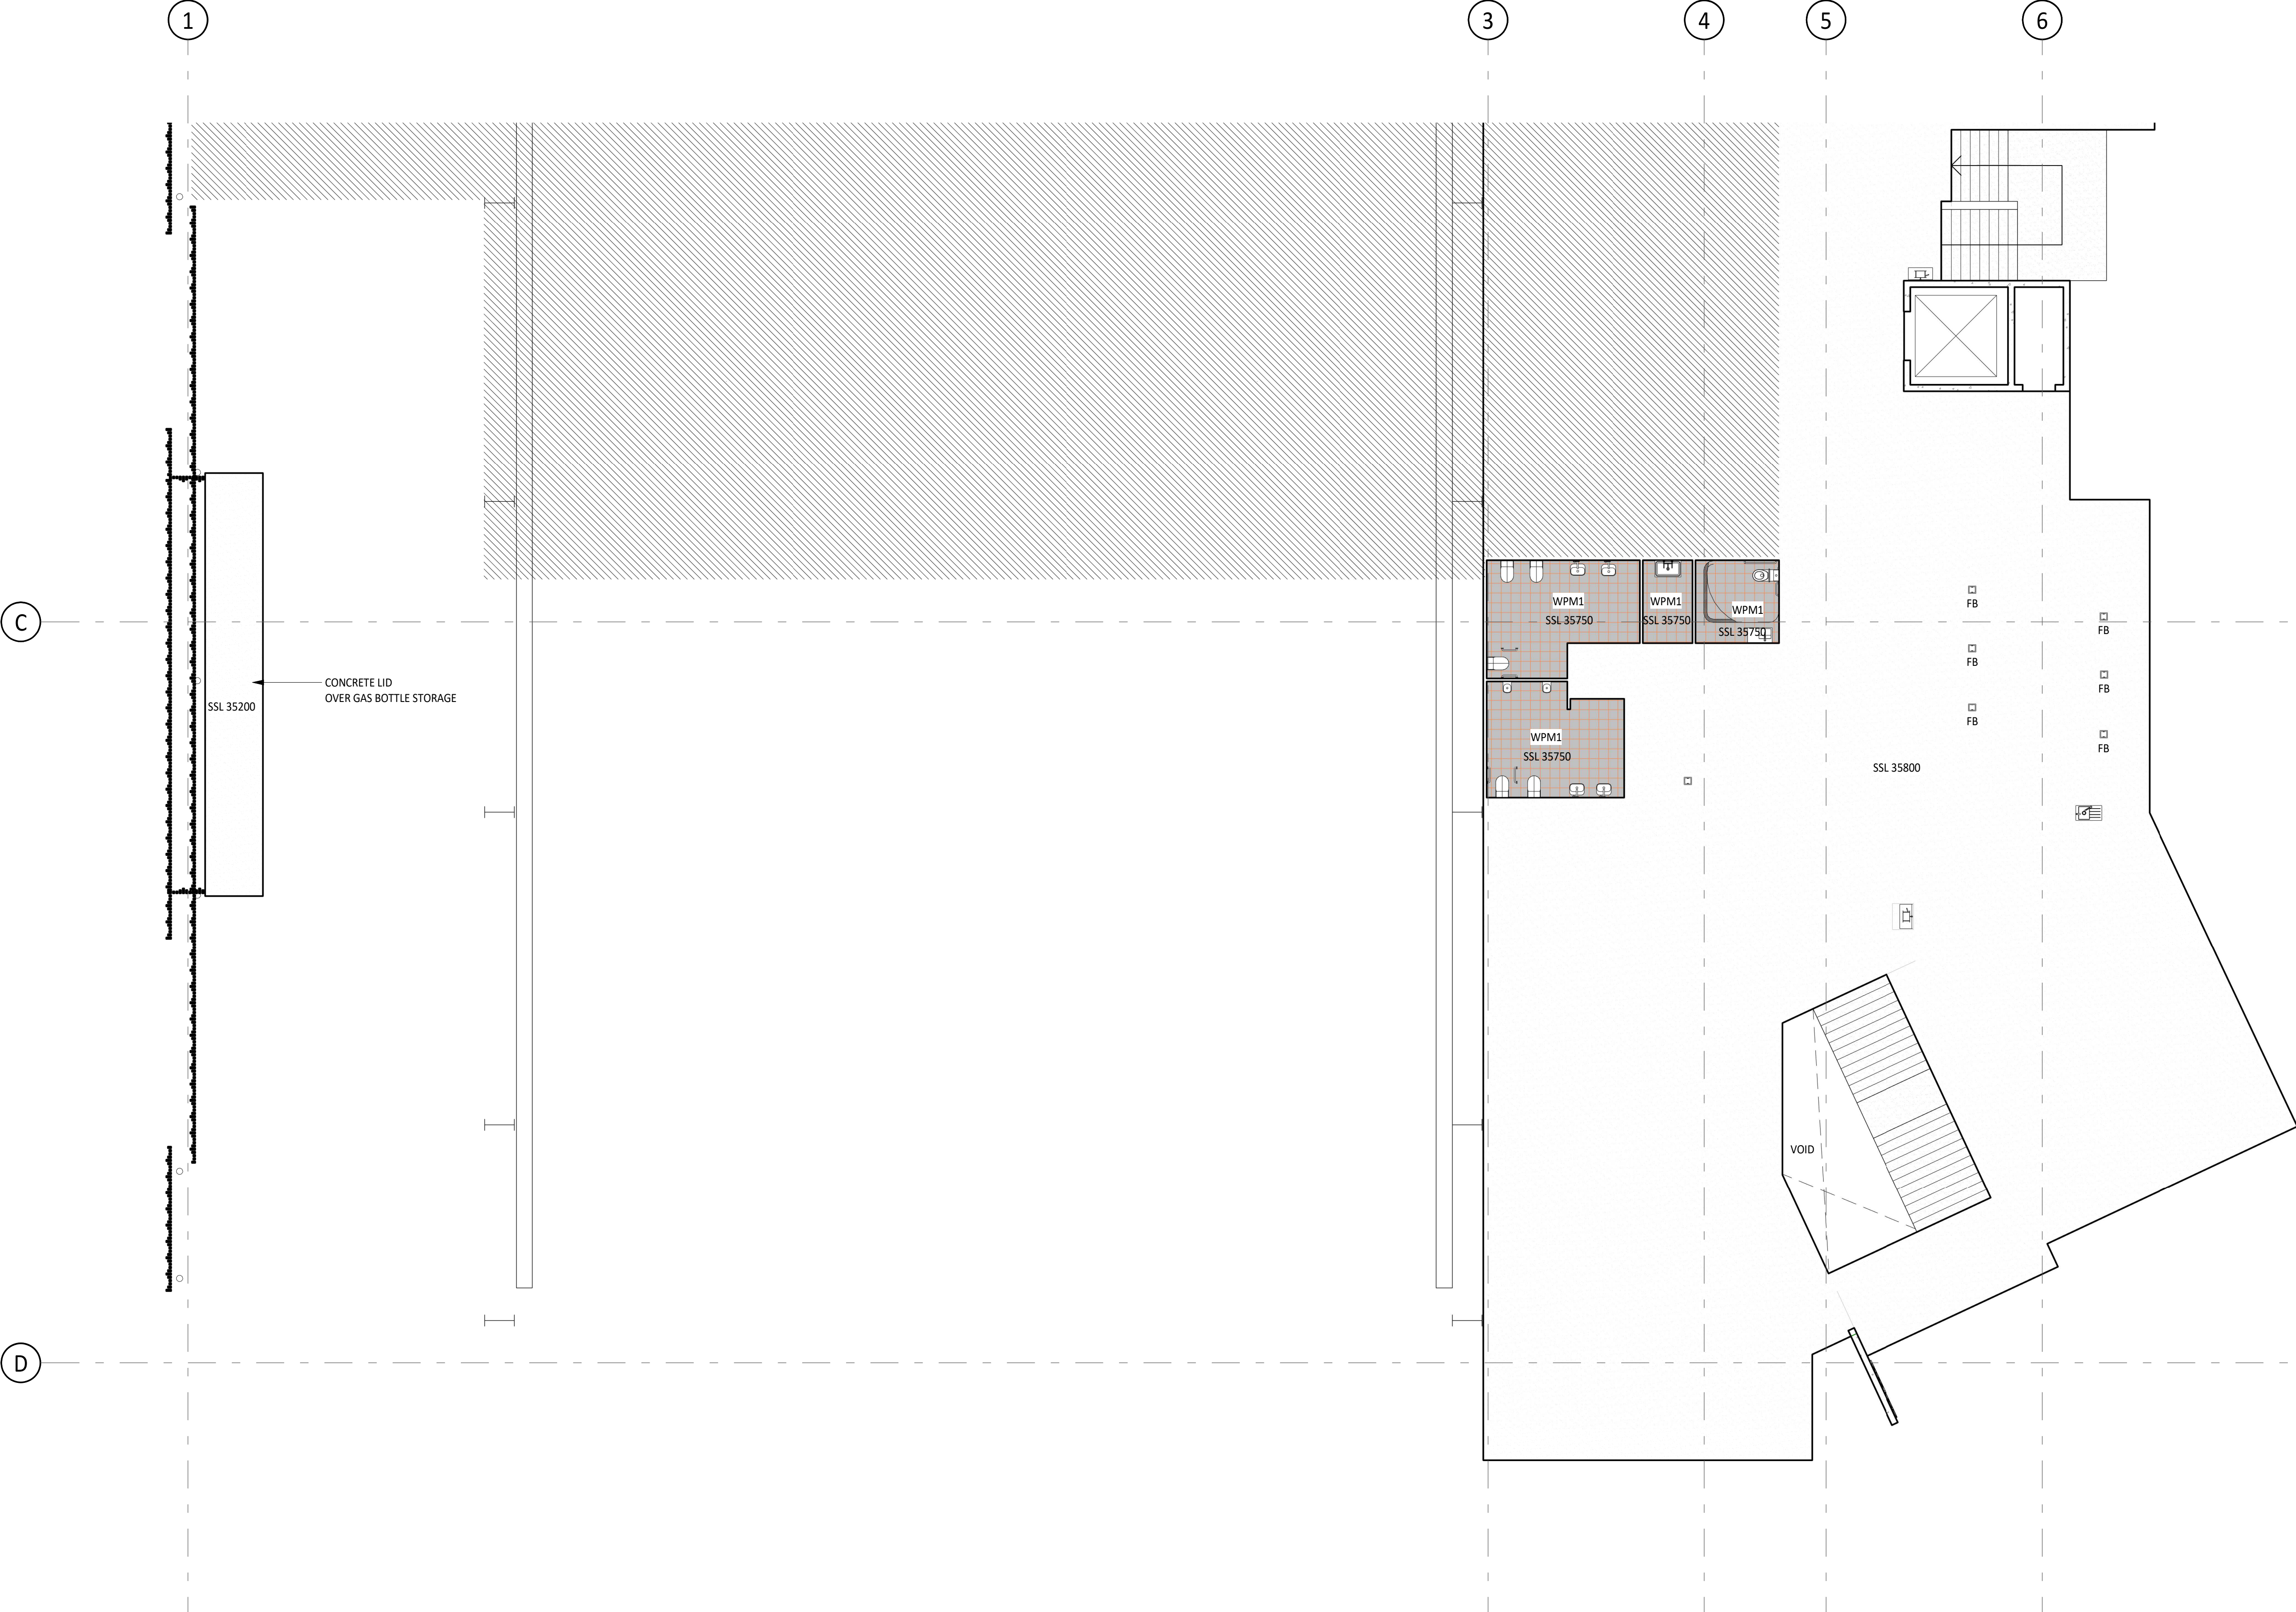

TO BE READ IN CONJUNCTION
WITH STRUCTURAL & SERVICES
ENGINEER'S DOCUMENTS

SLAB SETOUT LEGEND	
---	JOINTS REFER TO DETAILS FOR TYPICAL SLAB EXPANSION JOINTS
■	DENOTES SETDOWNS
FB	FLOOR BOX
FW	FLOOR WASTE
PLANS TO BE PRINTED IN COLOUR	

WATERPROOFING LEGEND	
WPM1	WATERPROOFING TYPE 1
WPM2	WATERPROOFING TYPE 2
WPM3	WATERPROOFING TYPE 3
UNLESS NOTED OTHERWISE FLOORS WITH WATERPROOFING TO HAVE MEMBRANE COVERED TO MINIMUM 150 AFFL	
PLANS TO BE PRINTED IN COLOUR	

WALL SETOUTS	
1500	ALL CONCRETE/MASONRY WALLS DIMENSION FROM OUTSIDE / INSIDE FACE OF WALL TO GRID
1500	ALL PARTITION WALLS DIMENSION FROM CENTRE OF STUD TO GRID

ISSUED FOR TENDER

STRUCTURAL SETOUT LEVEL 01 - ZONE 2

scale 1 : 100 @ A1 project no. 260018

revision A
sheet no. CQU-ROK-092-01-ARC-23-12

original sheet size - A1 (594mm x 841mm)

thomson
adsett

PEDDLE THORP
architecture | interiors | health | planning

Telephone +61 7 3840 9999
bne@thomsonadsett.com
Level 9, 470 St Pauls Terrace
Fortitude Valley
Qld 4006 Australia
thomsonadsett.com

© Copyright
These drawings and designs and the copyright
thereof are the property of Thomson Adsett Pty
Ltd and must not be used, retained or copied
without written permission of Thomson Adsett
Pty Ltd. ABN 76 105 314 654 Trading as
ThomsonAdsett. Dimensions take precedence
over scaling. Do not measure off drawings as
print sizes may vary

CQU ROCKHAMPTON TAFE CONSOLIDATION - STAGE 2

554/700 Yaamba Rd, Norman
Gardens QLD 4701



A	12/02/26	ISSUED FOR TENDER	BS
1	30/01/26	DRAFT 60% ISSUE	BS
rev	date	details	init.

drawn	PT	date	30/01/26
checked	BS	date	30/01/26
verified	BS	date	30/01/26

scale