


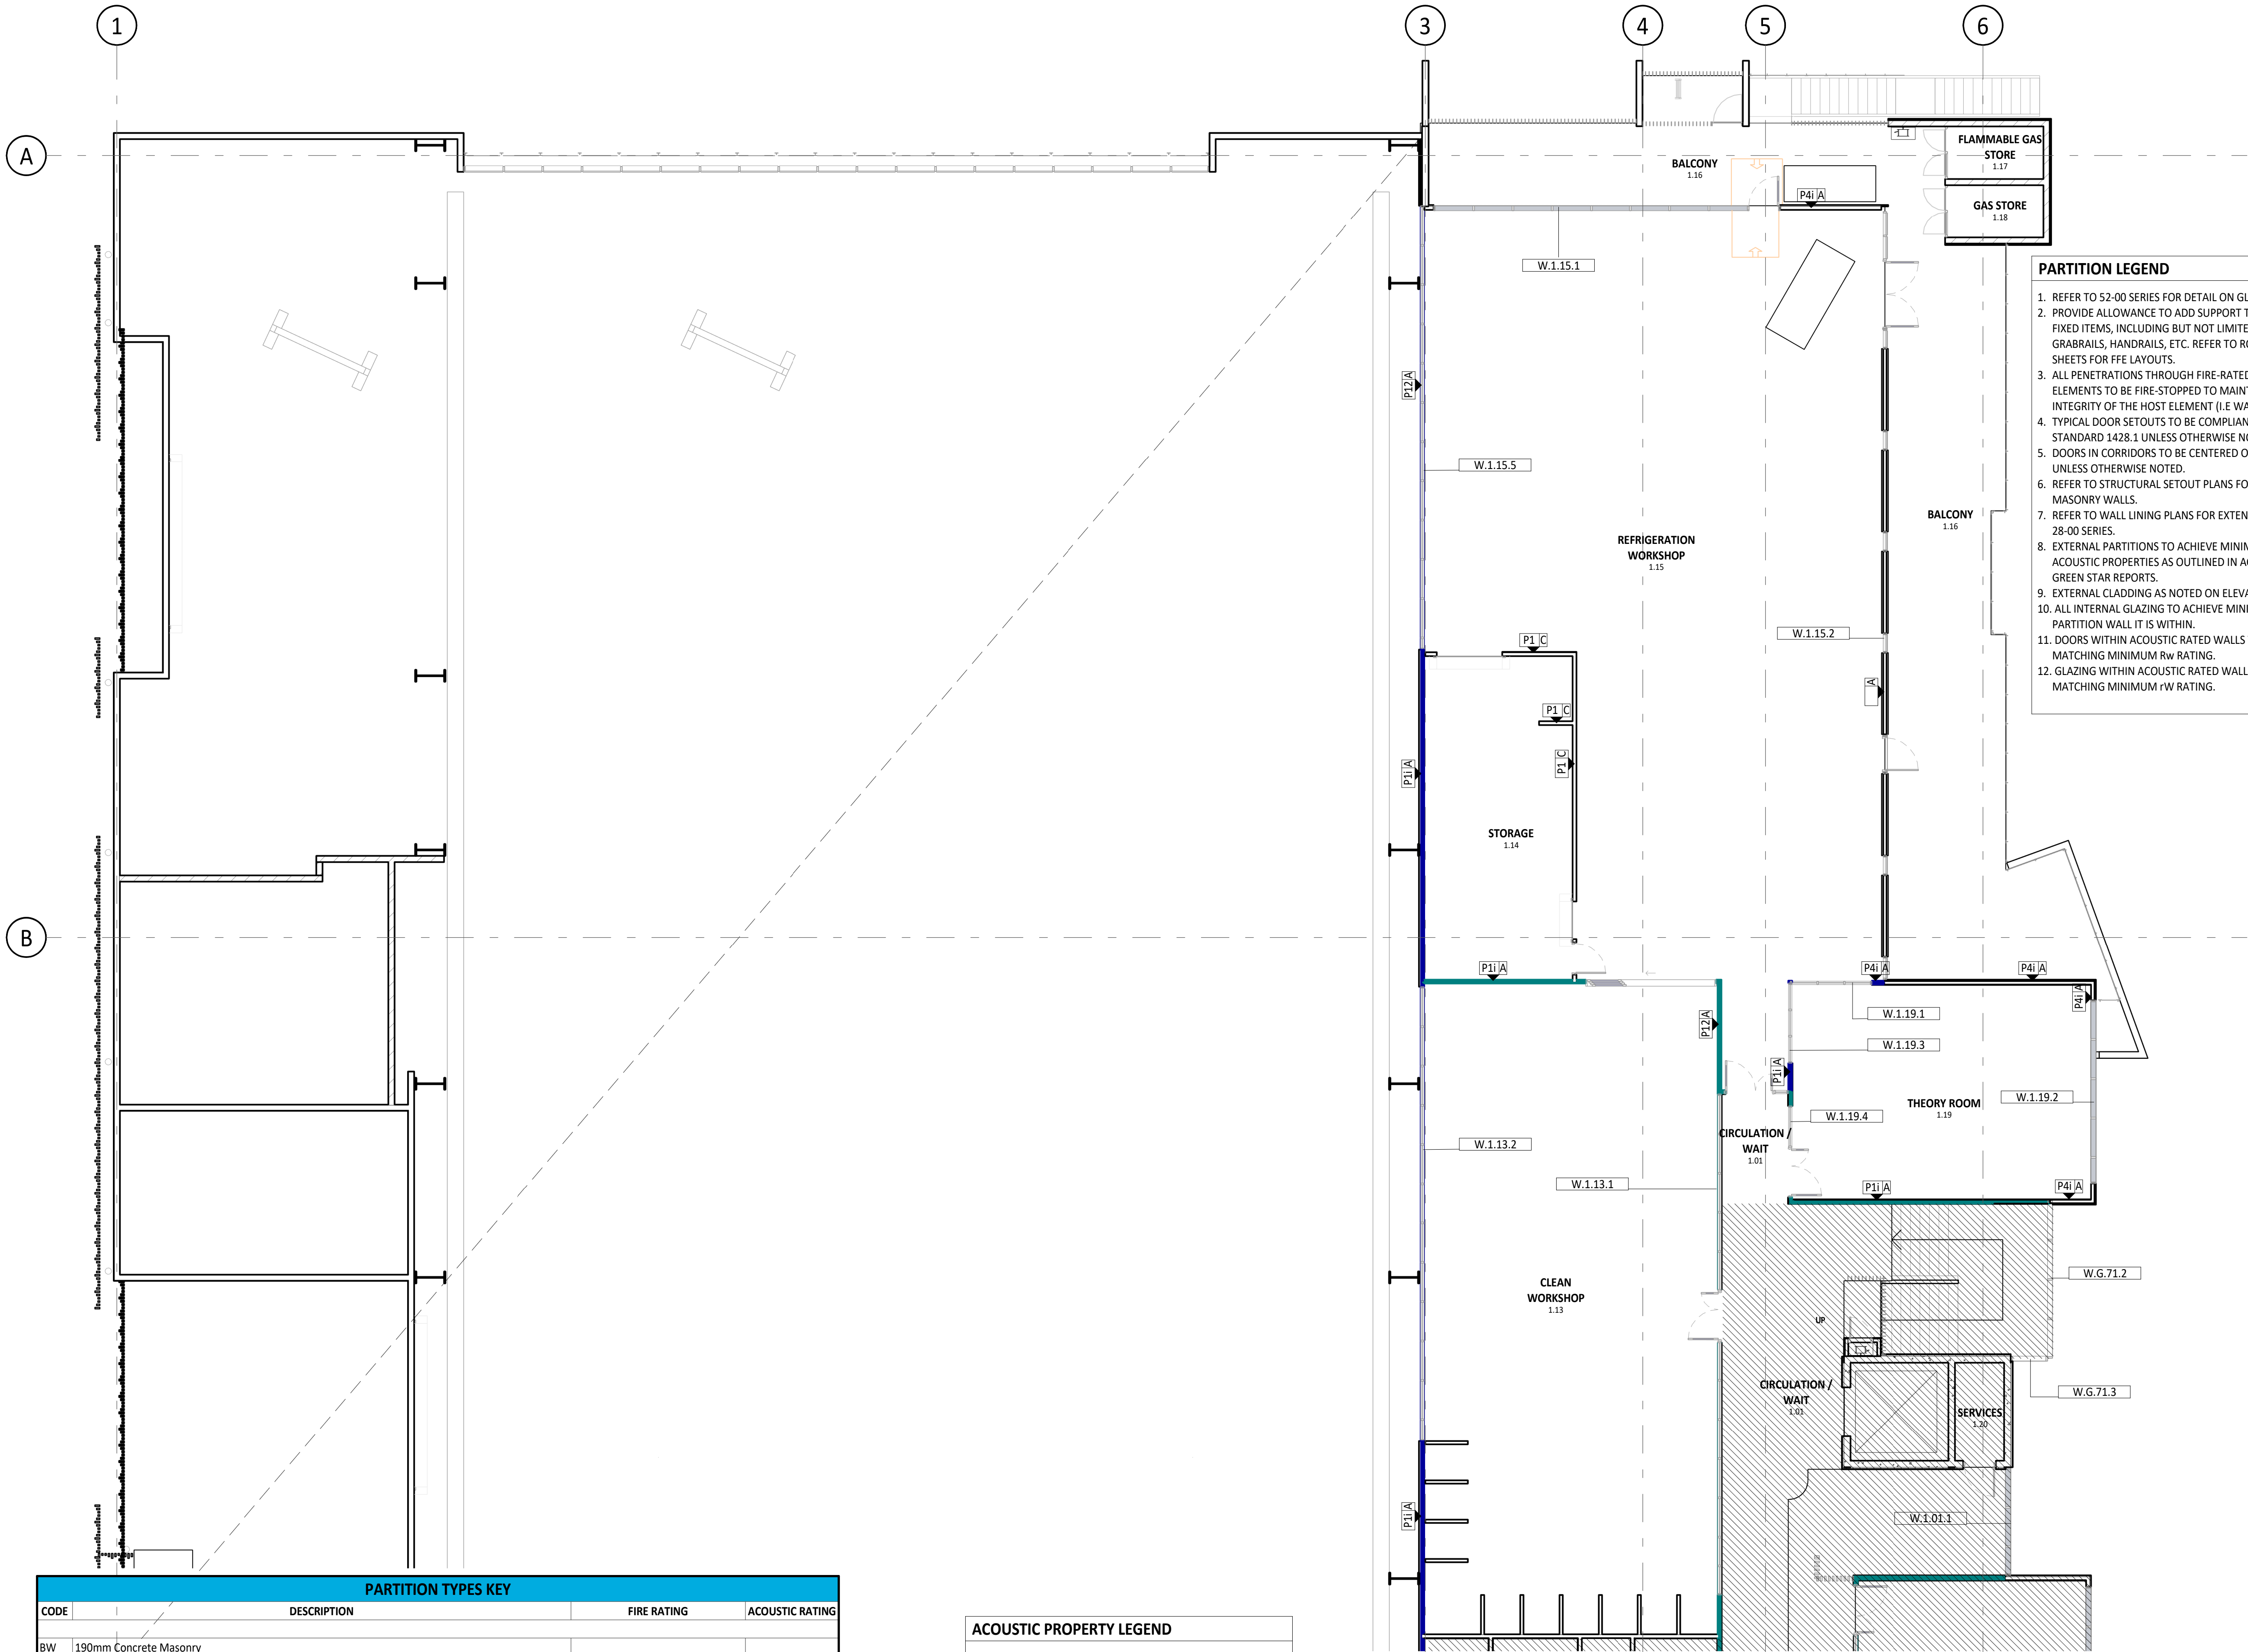

PARTITION TYPES KEY			
CODE	DESCRIPTION	FIRE RATING	ACOUSTIC RATING
BW	190mm Concrete Masonry		
MC1	16mm Cladding + 6mm Rigid Air Barrier + 150 Structure + Thermal & Acoustic Insulation + 16mm Cladding		Refer Acoustic & Green Star Reports
P1	92mm STEEL STUD WITH 1x13mm HIGH PERFORMANCE PLASTERBOARD (TRUROCK) TO BOTH SIDES	WHERE REQUIRED (-/60/60)	38Rw (30Rw+Ctr)
P1i	92mm STEEL STUD WITH 50mm ACOUSTIC INSULATION AND 1x13mm HIGH PERFORMANCE PLASTERBOARD (TRUROCK) TO BOTH SIDES - Rw 40 minimum	WHERE REQUIRED (-/60/60)	40 Rw minimum
P1i	92mm STEEL STUD WITH 50mm ACOUSTIC INSULATION AND 1x13mm HIGH PERFORMANCE PLASTERBOARD (TRUROCK) TO BOTH SIDES - Rw 45 minimum	WHERE REQUIRED (-/60/60)	45 Rw minimum
P2i	92mm STEEL STUD WITH 70mm ACOUSTIC INSULATION AND 2x13mm GYPROCK SOUNDCHECK PLASTERBOARD TO BOTH SIDES - Rw 55 minimum	N/A	55 Rw minimum
P4i	92mm STEEL STUD + INSULATION AS DOCUMENTED WITH 1x13mm HIGH PERFORMANCE PLASTERBOARD (TRUROCK) TO ONE SIDE ONLY	N/A	<varies>
P5	28mm FURRING CHANNEL WITH 1x13mm HIGH PERFORMANCE PLASTERBOARD	N/A	-
P6	WA15 + 92 STUD + WA15		

ACOUSTIC PROPERTY LEGEND

RW 40

RW 45

RW 50

RW 55

LEGEND IDENTIFIES MINIMUM RW PARTITION WALL IS TO ACHIEVE

PLANS TO BE PRINTED IN COLOUR

FIRE MANAGEMENT LEGEND

FIRE RATED WALL - REFER TO PARTITION DETAILS FOR MORE INFO

SMOKE COMPARTMENT WALL

PLANS TO BE PRINTED IN COLOUR

PARTITION HEAD TYPE LEGEND

A = ACOUSTIC/SMOKE (FULL HEIGHT STUD TO U/S SLAB)
B = FIRE RATED (FULL HEIGHT STUD TO U/S SLAB)
C = 100mm ABOVE CEILING
D = TO UNDERSIDE OF CEILING
E = LOW WALL

PARTITION TAG LEGEND

P2i

B

PARTITION TYPE NO. (i) DENOTES INSULATION (REFER TO PARTITION TYPES 44-XX)

PARTITION HEAD DETAIL TYPE (REFER TO PARTITION DETAILS 44-XX)

PARTITION LEGEND

1. REFER TO 52-00 SERIES FOR DETAIL ON GLAZING PARTITIONS.

2. PROVIDE ALLOWANCE TO ADD SUPPORT TO WALLS FOR ALL FIXED ITEMS, INCLUDING BUT NOT LIMITED TO HANDBASINS, GRABRAILS, HANDRAILS, ETC. REFER TO ROOM LAYOUT SHEETS FOR FFE LAYOUTS.

3. ALL PENETRATIONS THROUGH FIRE-RATED BUILDING ELEMENTS TO BE FIRE-STOPPED TO MAINTAIN THE LEVEL OF INTEGRITY OF THE HOST ELEMENT (I.E WALL, FLOOR, CEILING).

4. TYPICAL DOOR SETOUTS TO BE COMPLIANT WITH AUSTRALIAN STANDARD 1428.1 UNLESS OTHERWISE NOTED.

5. DOORS IN CORRIDORS TO BE CENTERED ON CORRIDOR WIDTH UNLESS OTHERWISE NOTED.

6. REFER TO STRUCTURAL SETOUT PLANS FOR SETOUT OF ALL MASONRY WALLS.

7. REFER TO WALL LINING PLANS FOR EXTENT OF WALL LININGS 28-00 SERIES.

8. EXTERNAL PARTITIONS TO ACHIEVE MINIMUM THERMAL & ACOUSTIC PROPERTIES AS OUTLINED IN ACOUSTIC & JV3 / GREEN STAR REPORTS.

9. EXTERNAL CLADDING AS NOTED ON ELEVATIONS.

10. ALL INTERNAL GLAZING TO ACHIEVE MINIMUM RW OF PARTITION WALL IT IS WITHIN.

11. DOORS WITHIN ACOUSTIC RATED WALLS TO ACHIEVE MATCHING MINIMUM Rw RATING.

12. GLAZING WITHIN ACOUSTIC RATED WALLS TO ACHIEVE MATCHING MINIMUM rW RATING.

ISSUED FOR TENDER

thomson
adsett

PEDDLE THORP
architecture | interiors | health | planning

Telephone +61 7 3840 9999
bne@thomsonadsett.com
Level 9, 470 St Pauls Terrace
Fortitude Valley
Qld 4006 Australia
thomsonadsett.com

© Copyright
These drawings and designs and the copyright thereof are the property of Thomson Adsett Pty Ltd and must not be used, retained or copied without written permission of Thomson Adsett Pty Ltd. ABN 76 105 314 654 Trading as ThomsonAdsett. Dimensions take precedence over scaling. Do not measure off drawings as print sizes may vary

CQU ROCKHAMPTON
TAFE
CONSOLIDATION -
STAGE 2

554/700 Yaamba Rd, Norman
Gardens QLD 4701



A	12/02/26	ISSUED FOR TENDER	BS
1	30/01/26	DRAFT 60% ISSUE	BS
rev/	date	details	init.

drawn	date
PT	30/01/26
checked	date
BS	30/01/26
verified	date
BS	30/01/26

scale

1

PARTITION PLAN LEVEL 01 -
ZONE 1

scale

1 : 100 @ A1

project no.

260018

revision

A

sheet no.

CQU-ROK-092-01-ARC-26-11

original sheet size - A1 (594mm x 841mm)