

CQU ROCKHAMPTON TAFE CONSOLIDATION - STAGE 2

554/700 Yaamba Rd, Norman
Gardens QLD 4701



A	12/02/26	ISSUED FOR TENDER	BS
4	30/01/26	DRAFT 60% ISSUE	BS
3	23/01/26	COORDINATION ISSUE FOR CONSULTANTS	BS
2	19/12/25	ISSUE FOR COORDINATION	BS
1	24/11/25	50% COSTING ISSUE	BS

rev	date	details	init.
-----	------	---------	-------

drawn	date
PT	19/12/25
checked	date
BS	19/12/25
verified	date
BS	19/12/25

scale

REFLECTED CEILING PLAN GROUND LEVEL - ZONE 1

scale
1 : 100 @ A1


project no.
260018

revision
A

sheet no.
CQU-ROK-092-GN-ARC-27-01

original sheet size - A1 (594mm x 841mm)

ISSUED FOR TENDER

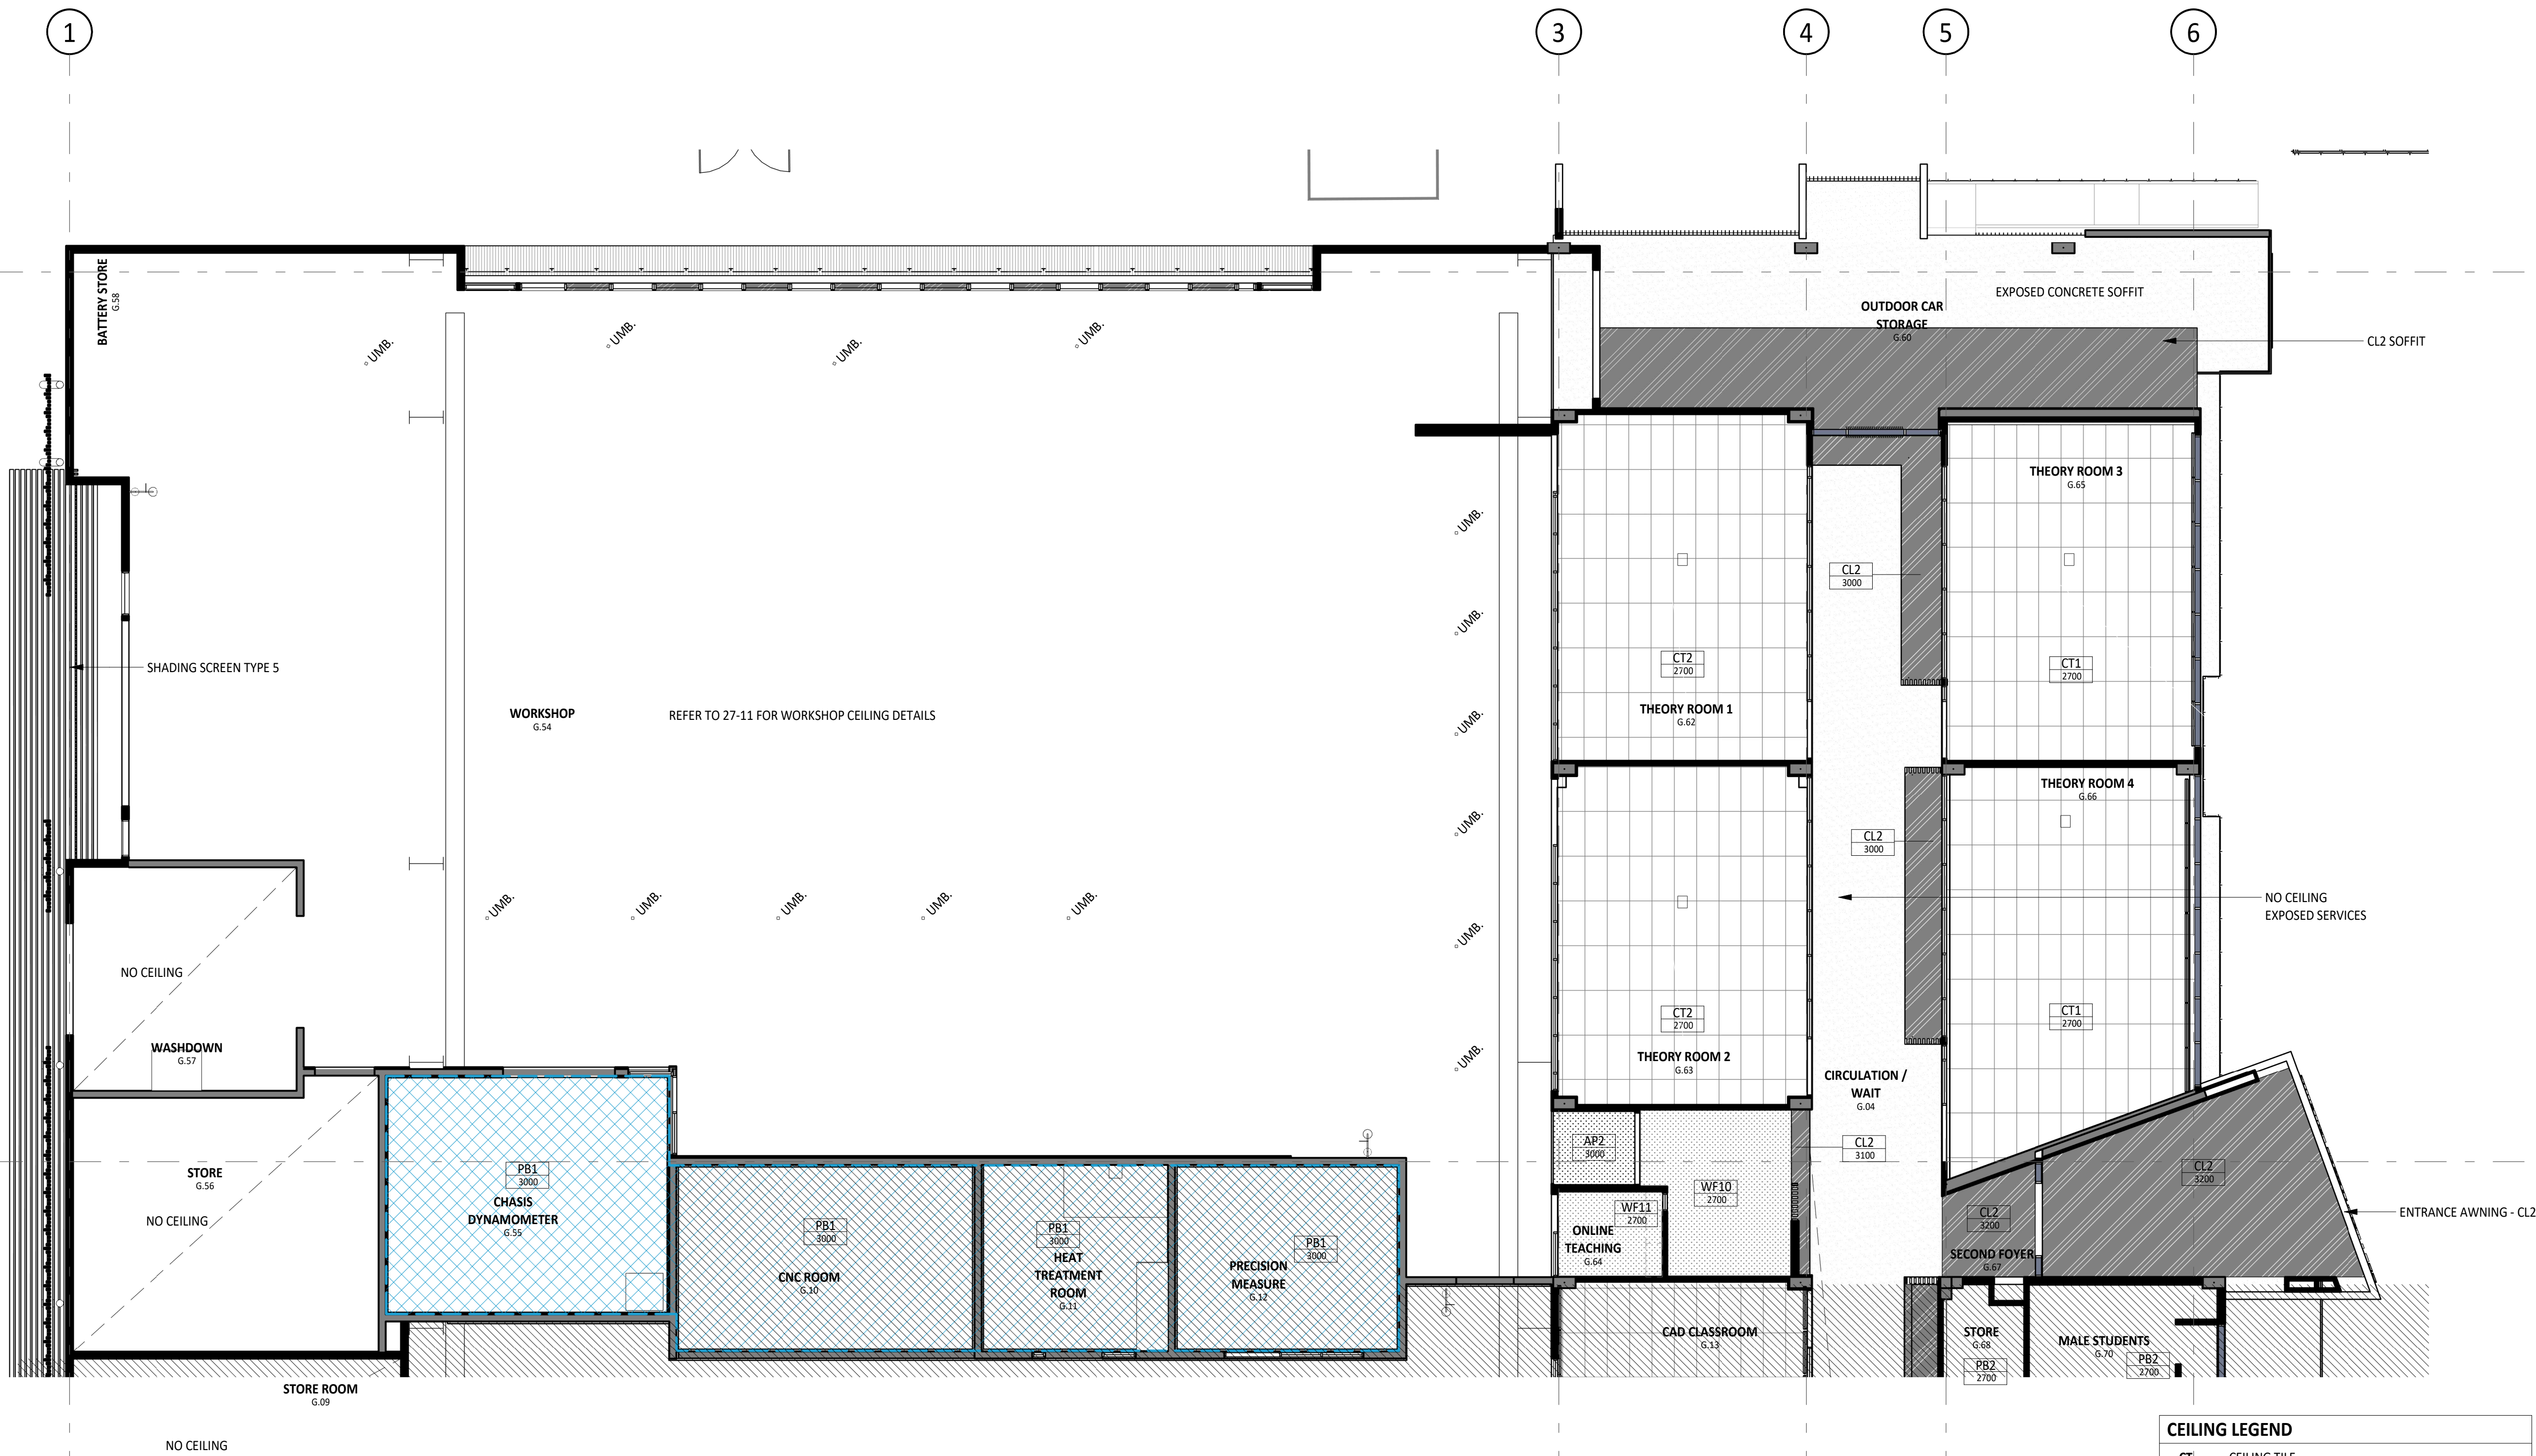

CEILING LEGEND

CT	CEILING TILE
PB	FLUSH SET PLASTERBOARD SHEETING
FC	FLUSH SET FIBRE CEMENT SHEETING
UMB.	UMBILICAL
SP	SERVICE POLE

NOTE: REFER TO SERVICES DOCUMENTATION FOR ACCESS PANEL QUANTITIES FINAL LOCATIONS TO SETOUT BY ARCHITECT

	ROOF INSULATION
	UNDERSLAB INSULATION
	GREY HATCH INDICATES EXISTING CEILING
	GREY HATCH INDICATES EXISTING WALL
	ACOUSTIC INSULATION
	CEILING TAG- FINISH (REFER TO FINISHES SCHEDULE) HEIGHT ABOVE FFL

FIRE MANAGEMENT LEGEND

	FIRE RATED WALL - REFER TO PARTITION DETAILS FOR MORE INFO
	SMOKE COMPARTMENT WALL
	FIRE RATED CEILING

PLANS TO BE PRINTED IN COLOUR