

CQU ROCKHAMPTON TAFE CONSOLIDATION - STAGE 2

554/700 Yaamba Rd, Norman
Gardens QLD 4701


for



A	12/02/26	ISSUED FOR TENDER	BS
3	30/01/26	DRAFT 60% ISSUE	BS
2	23/01/26	COORDINATION ISSUE FOR CONSULTANTS	BS
1	19/12/25	ISSUE FOR COORDINATION	BS
rev/	date	details	init.

drawn	date
PT	19/12/25
checked	date
Checker	19/12/25
verified	date
BS	19/12/25

scale

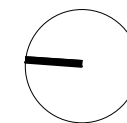


REFLECTED CEILING PLAN GROUND LEVEL - ZONE 3

scale	project no.
1 : 100 @ A1	260018
revision	
A	
sheet no.	
CQU-ROK-092-GN-ARC-27-03	

original sheet size - A1 (594mm x 841mm)

ISSUED FOR TENDER

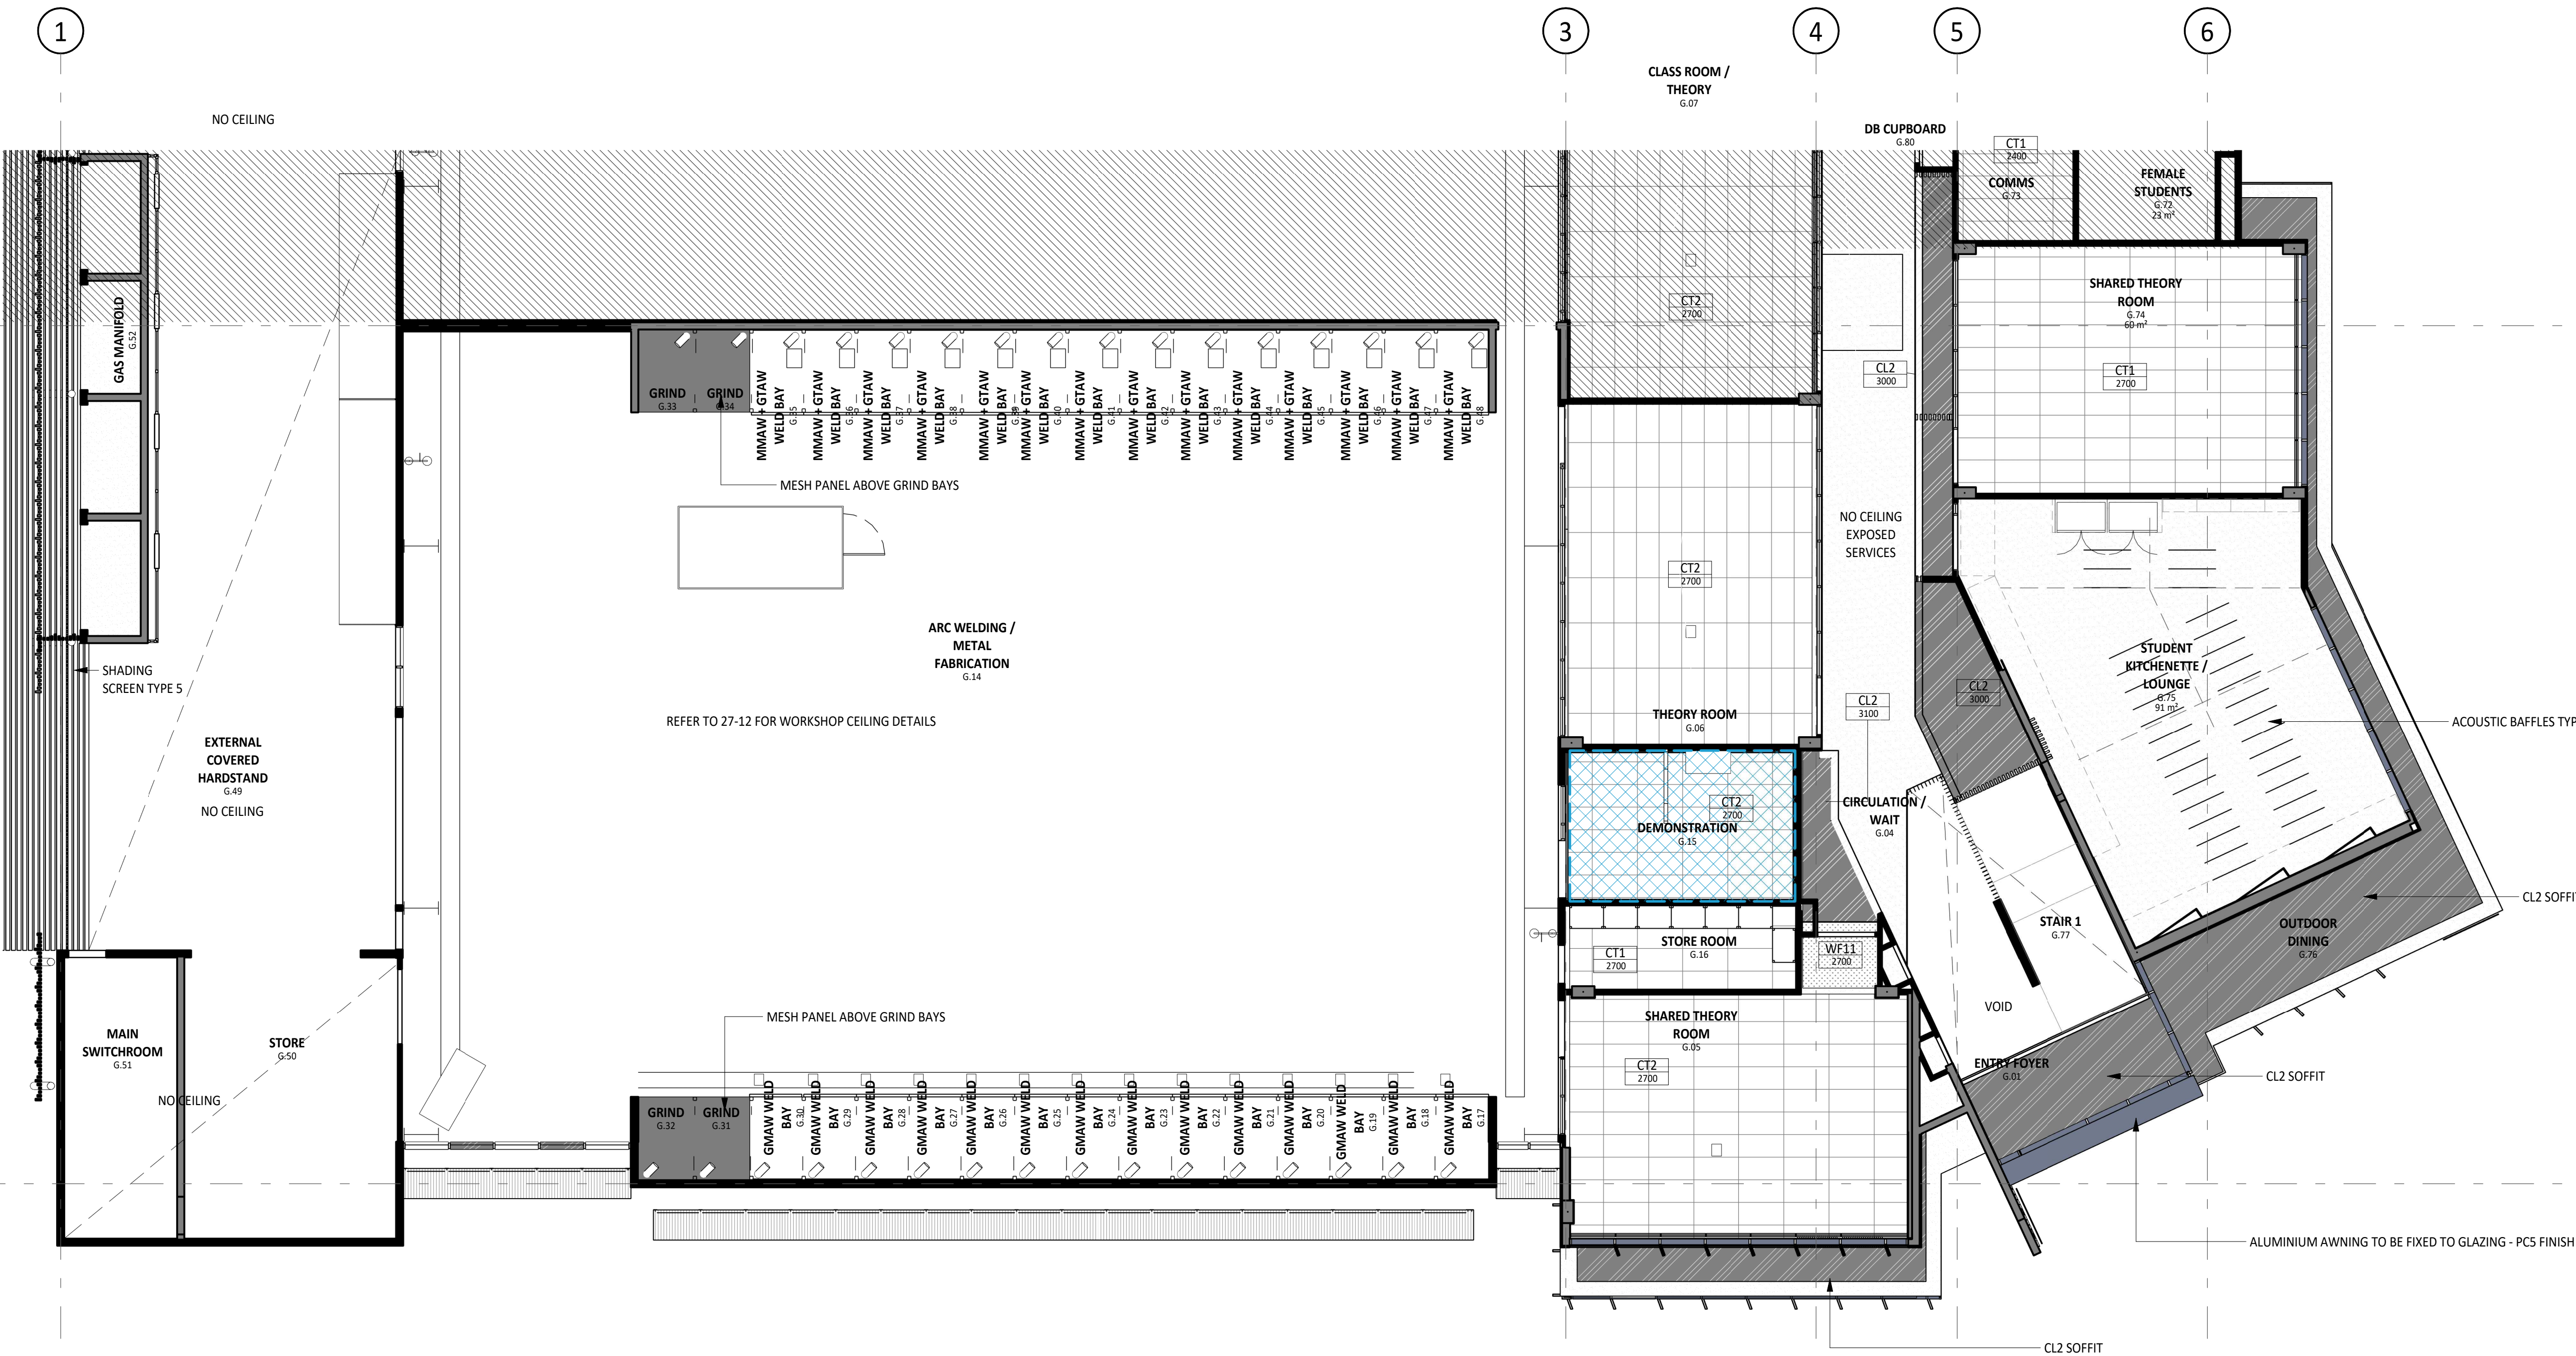

CEILING LEGEND	
CT	CEILING TILE
PB	FLUSH SET PLASTERBOARD SHEETING
FC	FLUSH SET FIBRE CEMENT SHEETING
UMB.	UMBILICAL
SP	SERVICE POLE
NOTE: REFER TO SERVICES DOCUMENTATION FOR ACCESS PANEL QUANTITIES FINAL LOCATIONS TO SETOUT BY ARCHITECT	
	ROOF INSULATION
	UNDERSLAB INSULATION
	GREY HATCH INDICATES EXISTING CEILING
	GREY HATCH INDICATES EXISTING WALL
	ACOUSTIC INSULATION
	CEILING TAG- FINISH (REFER TO FINISHES SCHEDULE) HEIGHT ABOVE FFL

FIRE MANAGEMENT LEGEND	
	FIRE RATED WALL - REFER TO PARTITION DETAILS FOR MORE INFO
	SMOKE COMPARTMENT WALL
	FIRE RATED CEILING
PLANS TO BE PRINTED IN COLOUR	