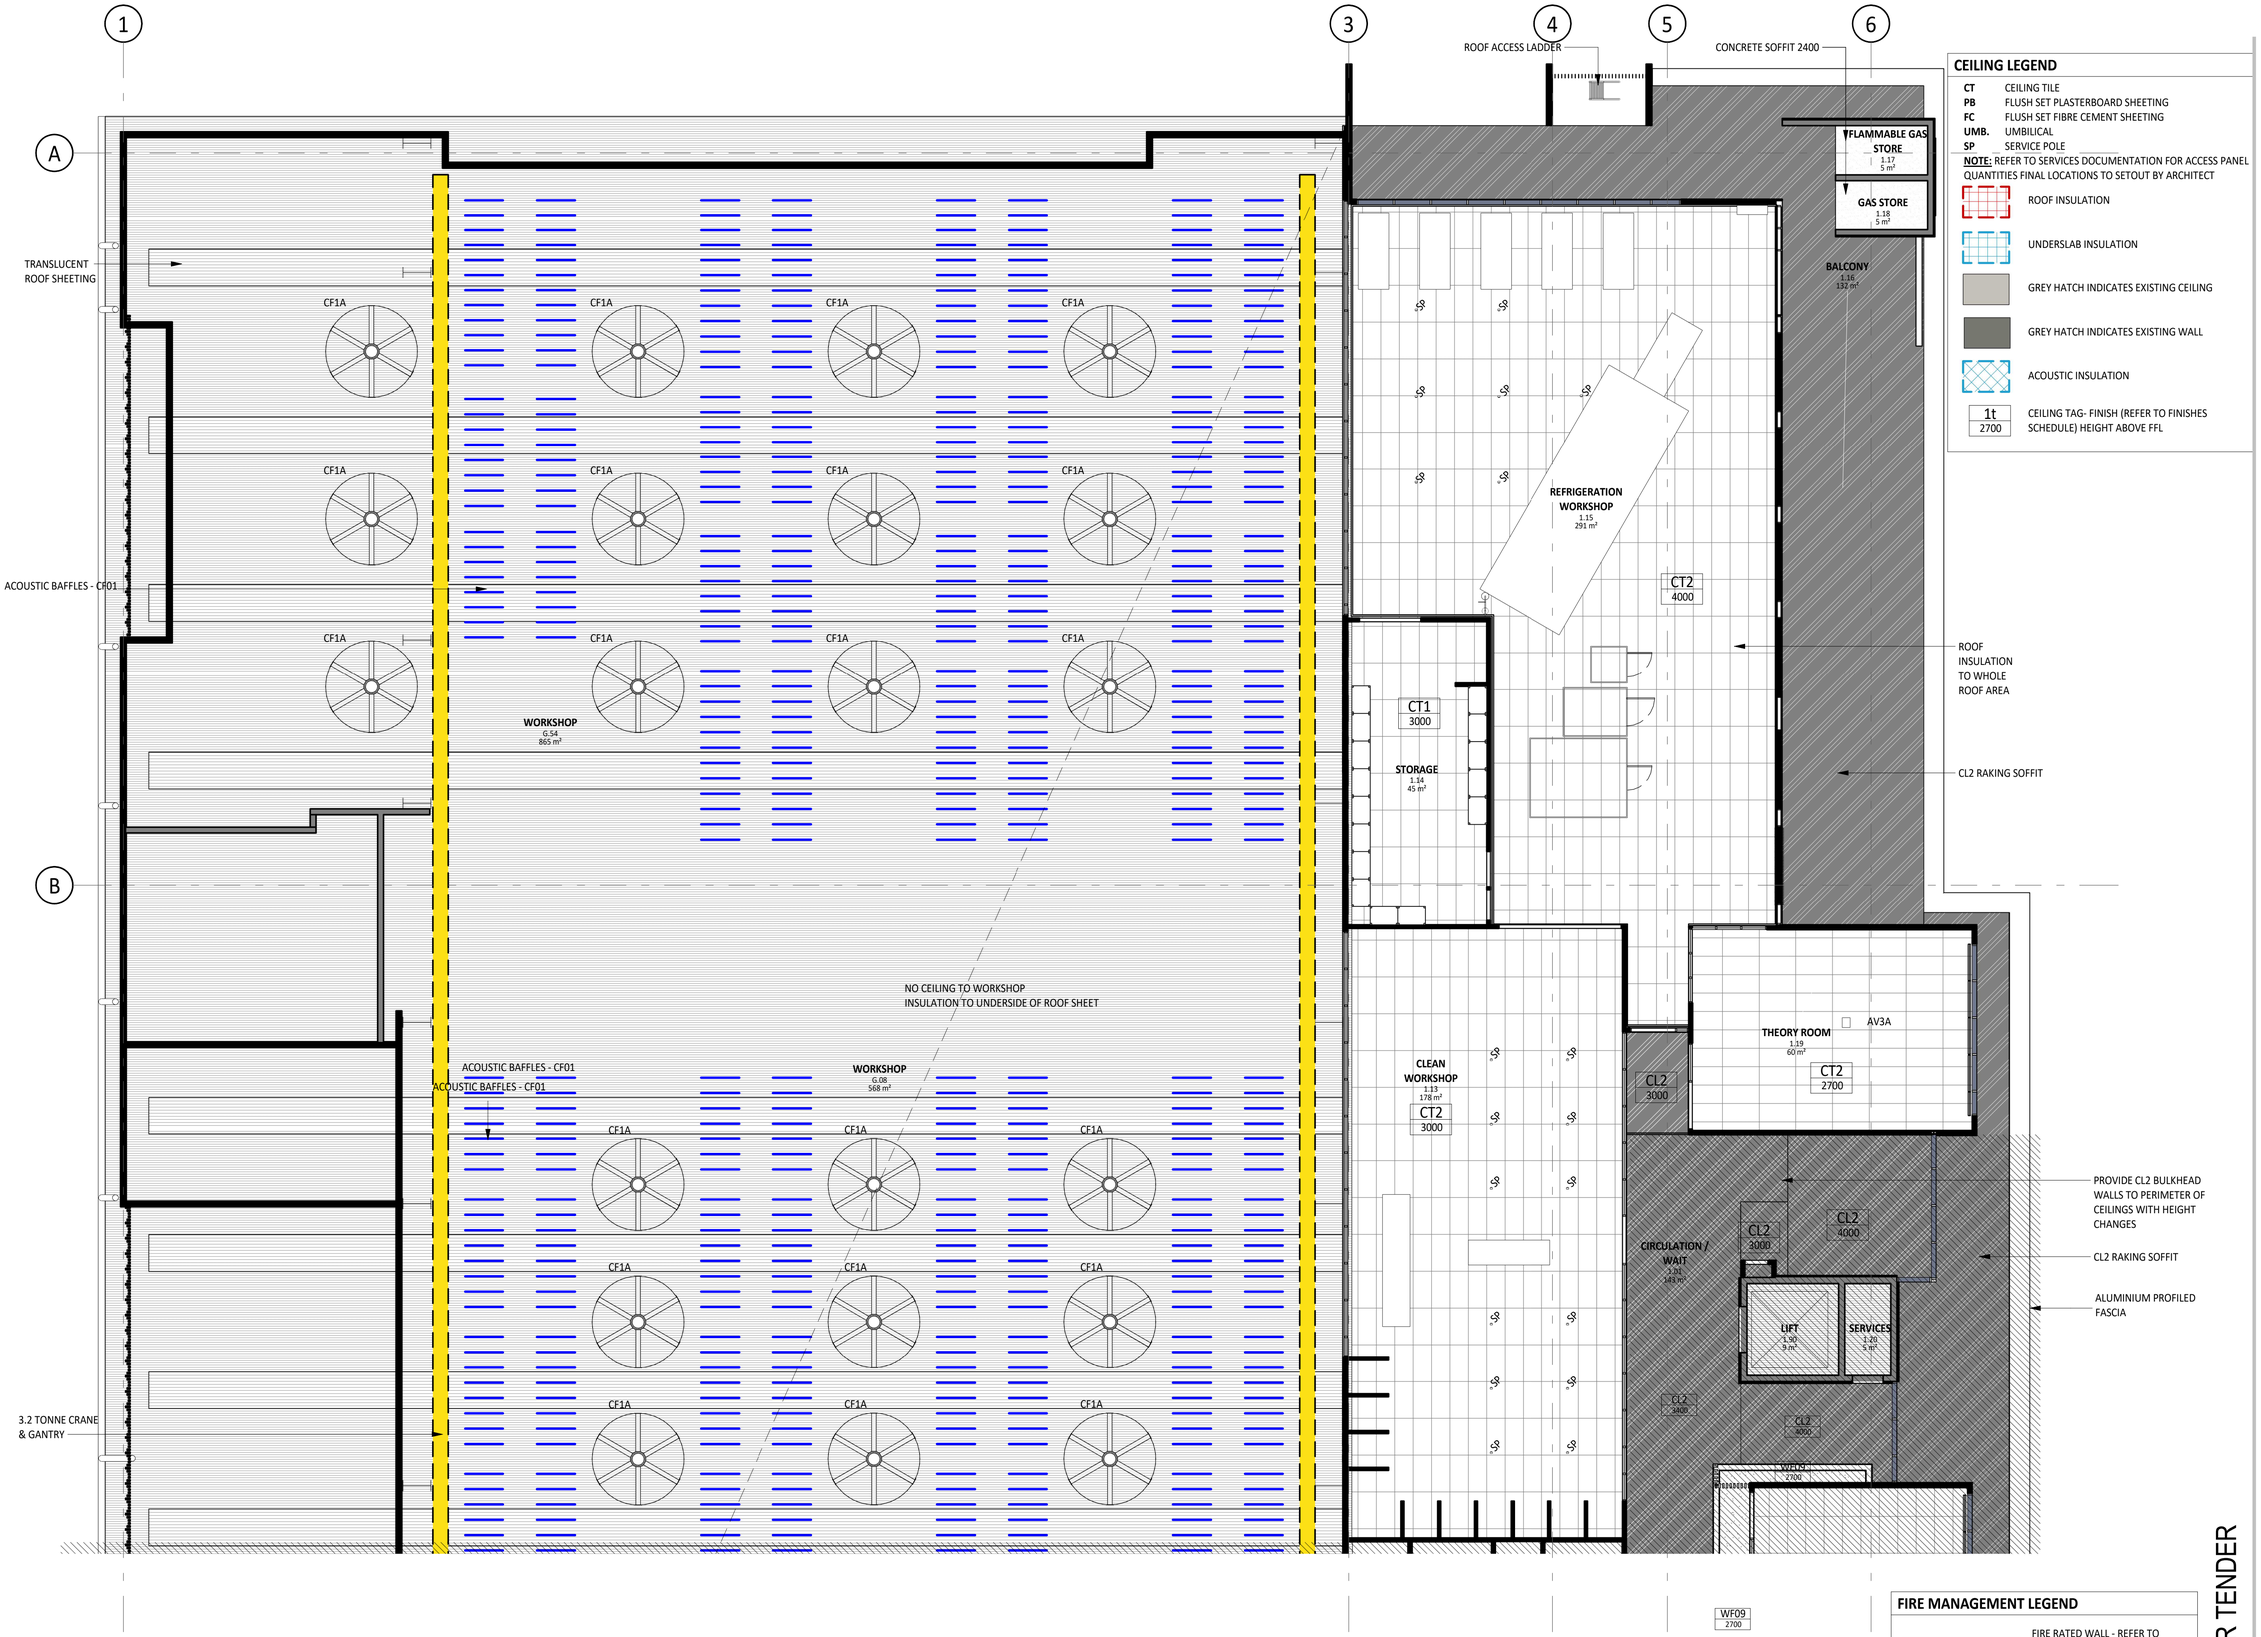

CEILING LEGEND

CT	CEILING TILE
PB	FLUSH SET PLASTERBOARD SHEETING
FC	FLUSH SET FIBRE CEMENT SHEETING
UMB.	UMBILICAL
SP	SERVICE POLE

NOTE: REFER TO SERVICES DOCUMENTATION FOR ACCESS PANEL QUANTITIES FINAL LOCATIONS TO SETOUT BY ARCHITECT

- ROOF INSULATION
- UNDERSLAB INSULATION
- GREY HATCH INDICATES EXISTING CEILING
- GREY HATCH INDICATES EXISTING WALL
- ACOUSTIC INSULATION
- 1t / 2700 — CEILING TAG- FINISH (REFER TO FINISHES SCHEDULE) HEIGHT ABOVE FFL

FIRE MANAGEMENT LEGEND

- FIRE RATED WALL - REFER TO PARTITION DETAILS FOR MORE INFO
- SMOKE COMPARTMENT WALL
- FIRE RATED CEILING

PLANS TO BE PRINTED IN COLOUR

ISSUED FOR TENDER

thomson adsett

PEDDLE THORP
architecture | interiors | health | planning

Telephone +61 7 3840 9999
bne@thomsonadsett.com
Level 9, 470 St Pauls Terrace
Fortitude Valley
Qld 4006 Australia
thomsonadsett.com

© Copyright
These drawings and designs and the copyright thereof are the property of Thomson Adsett Pty Ltd and must not be used, retained or copied without written permission of Thomson Adsett Pty Ltd. ABN 76 105 314 654 Trading as ThomsonAdsett. Dimensions take precedence over scaling. Do not measure off drawings as print sizes may vary

CQU ROCKHAMPTON TAFE CONSOLIDATION - STAGE 2

554/700 Yaamba Rd, Norman Gardens QLD 4701

for CQUniversity AUSTRALIA

rev	date	details	init
A	12/02/26	ISSUED FOR TENDER	BS
4	30/01/26	DRAFT 60% ISSUE	BS
3	23/01/26	COORDINATION ISSUE FOR CONSULTANTS	BS
2	19/12/25	ISSUE FOR COORDINATION	BS
1	24/11/25	50% COSTING ISSUE	BS

drawn PT — date 19/12/25
checked BS — date 19/12/25
verified BS — date 19/12/25

scale

REFLECTED CEILING PLAN LEVEL 01 - ZONE 1

scale: 1 : 100 @ A1
project no.: 260018
revision: A
sheet no.: CQU-ROK-092-01-ARC-27-11

original sheet size - A1 (594mm x 841mm)

12/02/2026 4:34:29 PM Autodesk Docs://CQU ROK TAFE/260018_A_CQ-UNIVERSITY_BLD-TRADES_R25.rvt