


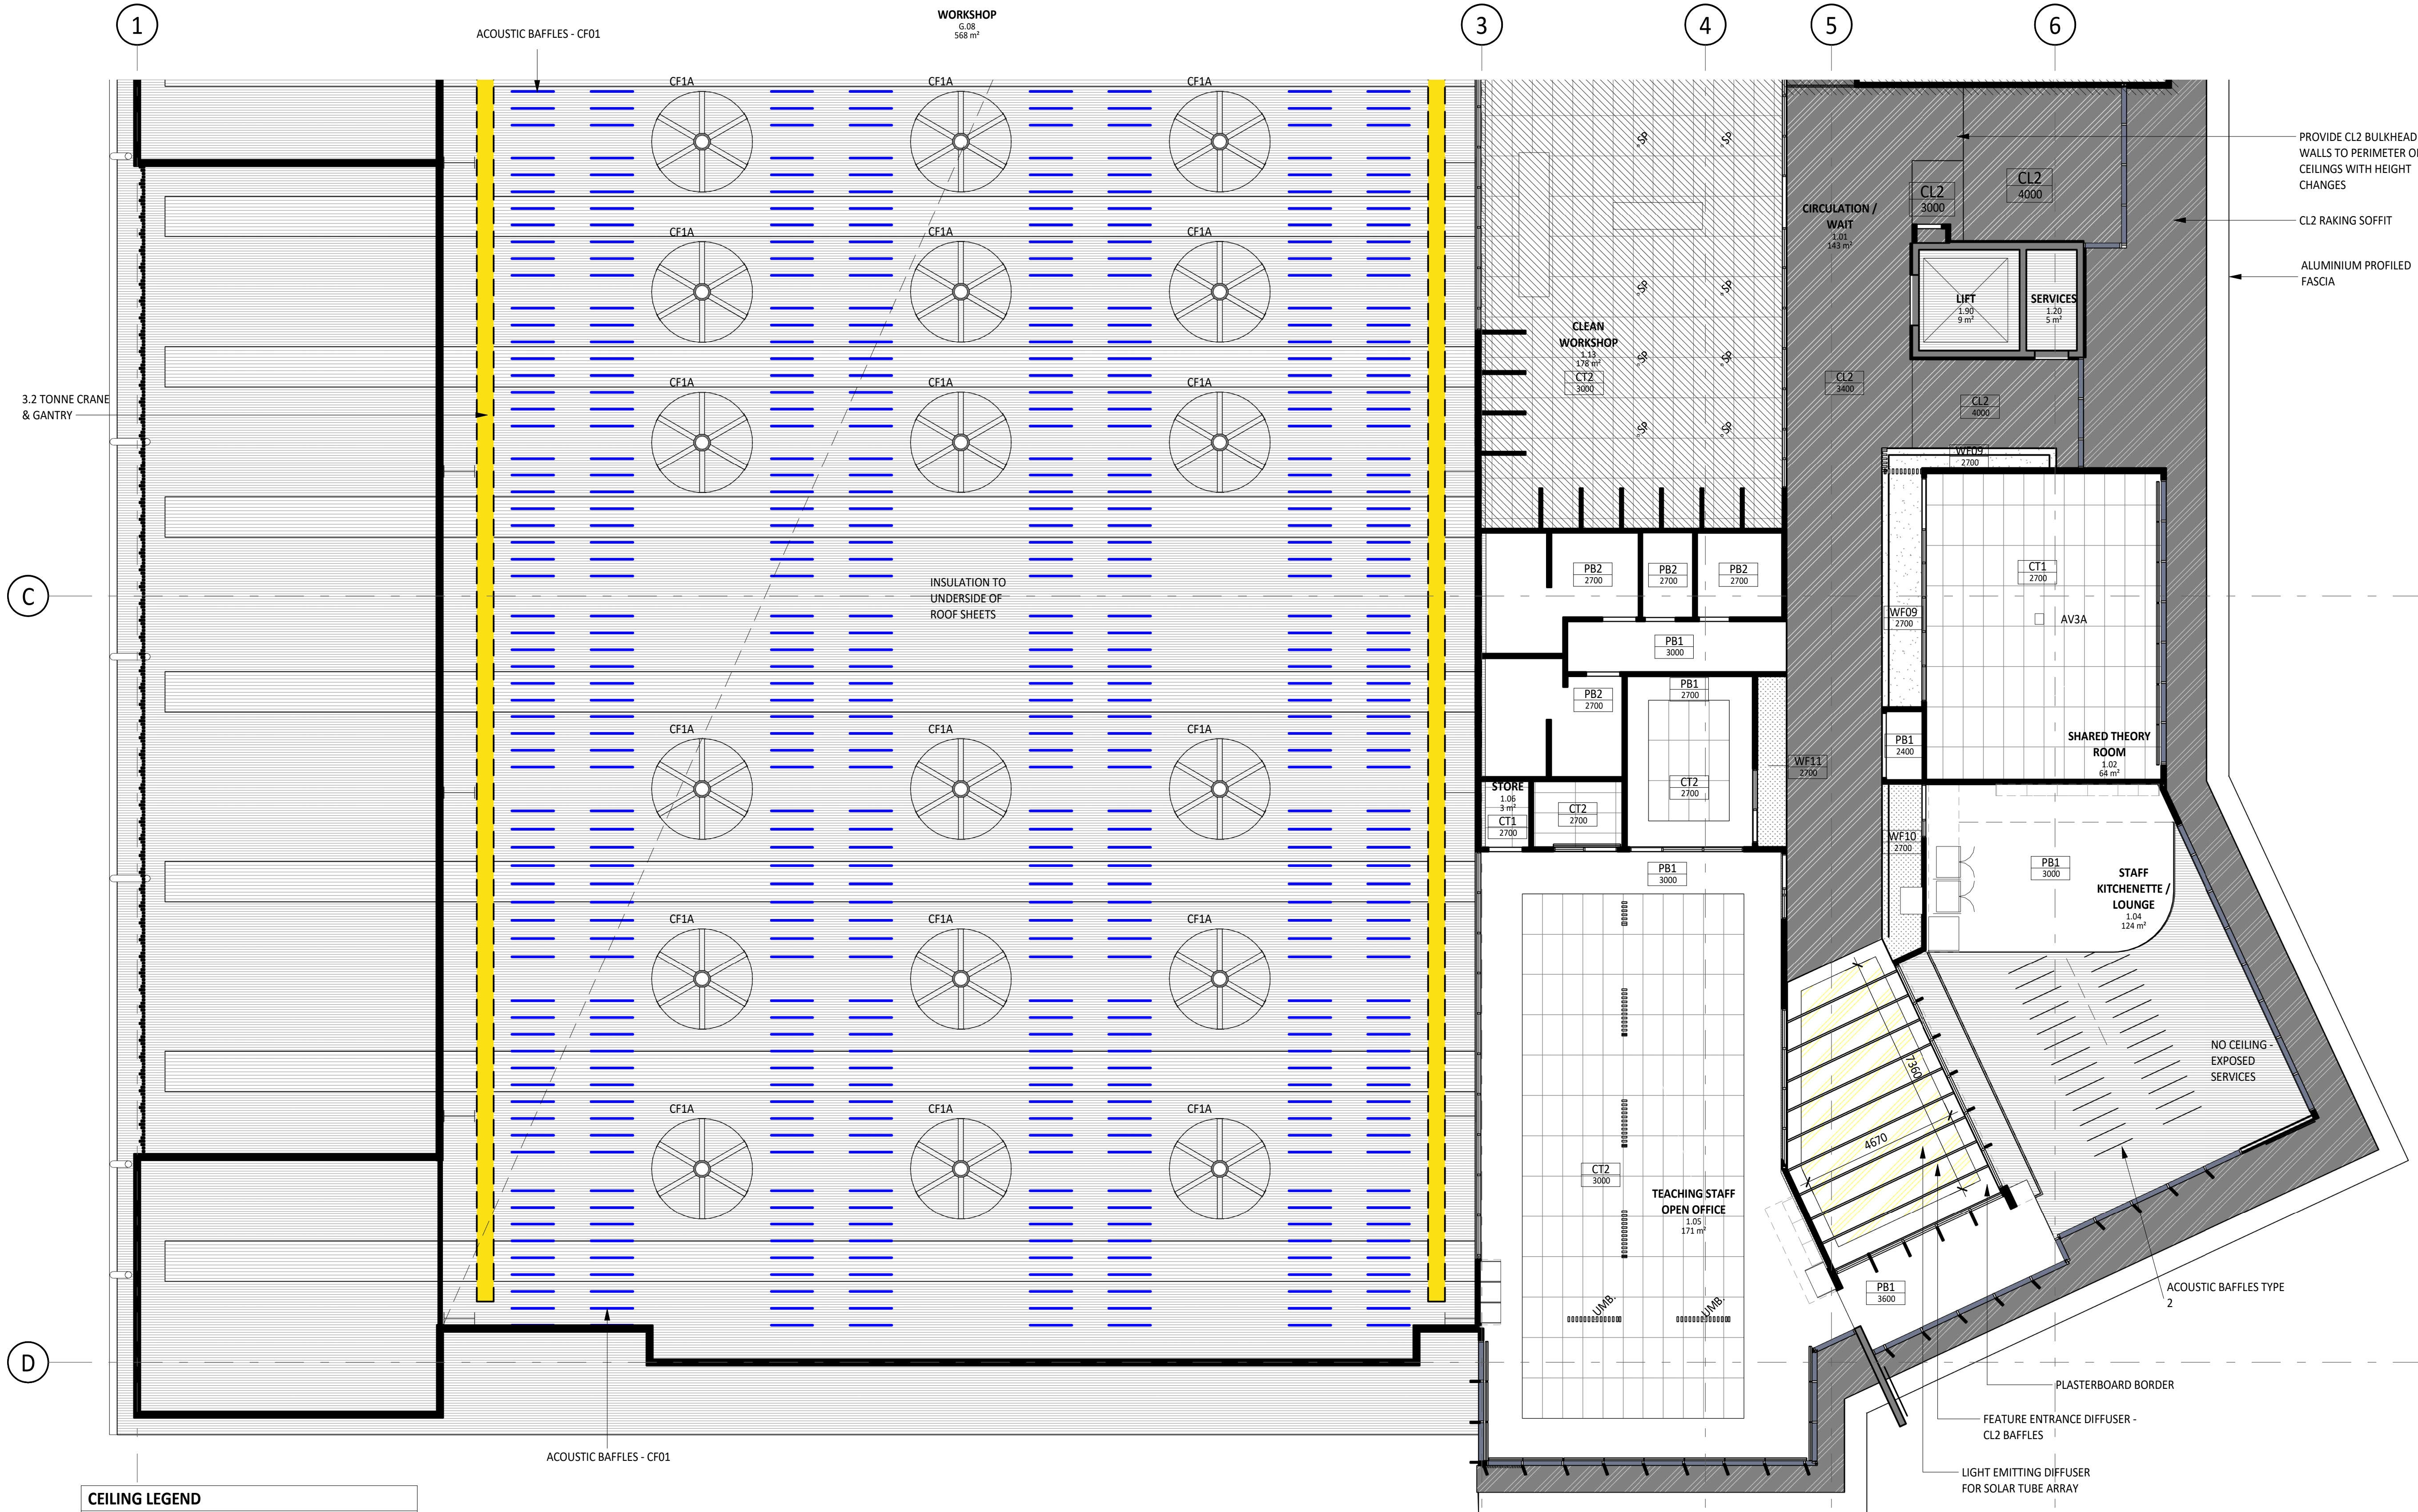

thomson
adsett

**PEDDLE THORP**
architecture | interiors | health | planning

Telephone +61 7 3840 9999
bne@thomsonadsett.com
Level 9, 470 St Pauls Terrace
Fortitude Valley
Qld 4006 Australia
thomsonadsett.com

© Copyright
These drawings and designs and the copyright thereof are the property of Thomson Adsett Pty Ltd and must not be used, retained or copied without written permission of Thomson Adsett Pty Ltd. A.B.N 76 105 314 654 Trading as ThomsonAdsett. Dimensions take precedence over scaling. Do not measure off drawings as print sizes may vary

CQU ROCKHAMPTON TAFE CONSOLIDATION - STAGE 2


554/700 Yaamba Rd, Norman Gardens QLD 4701



A	12/02/26	ISSUED FOR TENDER	BS
3	30/01/26	DRAFT 60% ISSUE	BS
2	23/01/26	COORDINATION ISSUE FOR CONSULTANTS	BS
1	19/12/25	ISSUE FOR COORDINATION	BS
rev/	date	details	init.

drawn	date
PT	19/12/25
checked	date
BS	19/12/25
verified	date
BS	19/12/25

scale

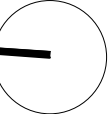

REFLECTED CEILING PLAN LEVEL 01 - ZONE 2

scale project no.
1 : 100 @ A1 260018
revision
A
sheet no.
CQU-ROK-092-01-ARC-27-12

original sheet size - A1 (594mm x 841mm)

ISSUED FOR TENDER

FIRE MANAGEMENT LEGEND

 FIRE RATED WALL - REFER TO PARTITION DETAILS FOR MORE INFO

 SMOKE COMPARTMENT WALL

 FIRE RATED CEILING

PLANS TO BE PRINTED IN COLOUR

CEILING LEGEND

CT CEILING TILE

PB FLUSH SET PLASTERBOARD SHEETING

FC FLUSH SET FIBRE CEMENT SHEETING

UMB. UMBILICAL

SP SERVICE POLE

NOTE: REFER TO SERVICES DOCUMENTATION FOR ACCESS PANEL QUANTITIES FINAL LOCATIONS TO SETOUT BY ARCHITECT


 ROOF INSULATION

 UNDERSLAB INSULATION

 GREY HATCH INDICATES EXISTING CEILING

 GREY HATCH INDICATES EXISTING WALL

 ACOUSTIC INSULATION

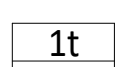 **1t** 2700 CEILING TAG- FINISH (REFER TO FINISHES SCHEDULE) HEIGHT ABOVE FFL