

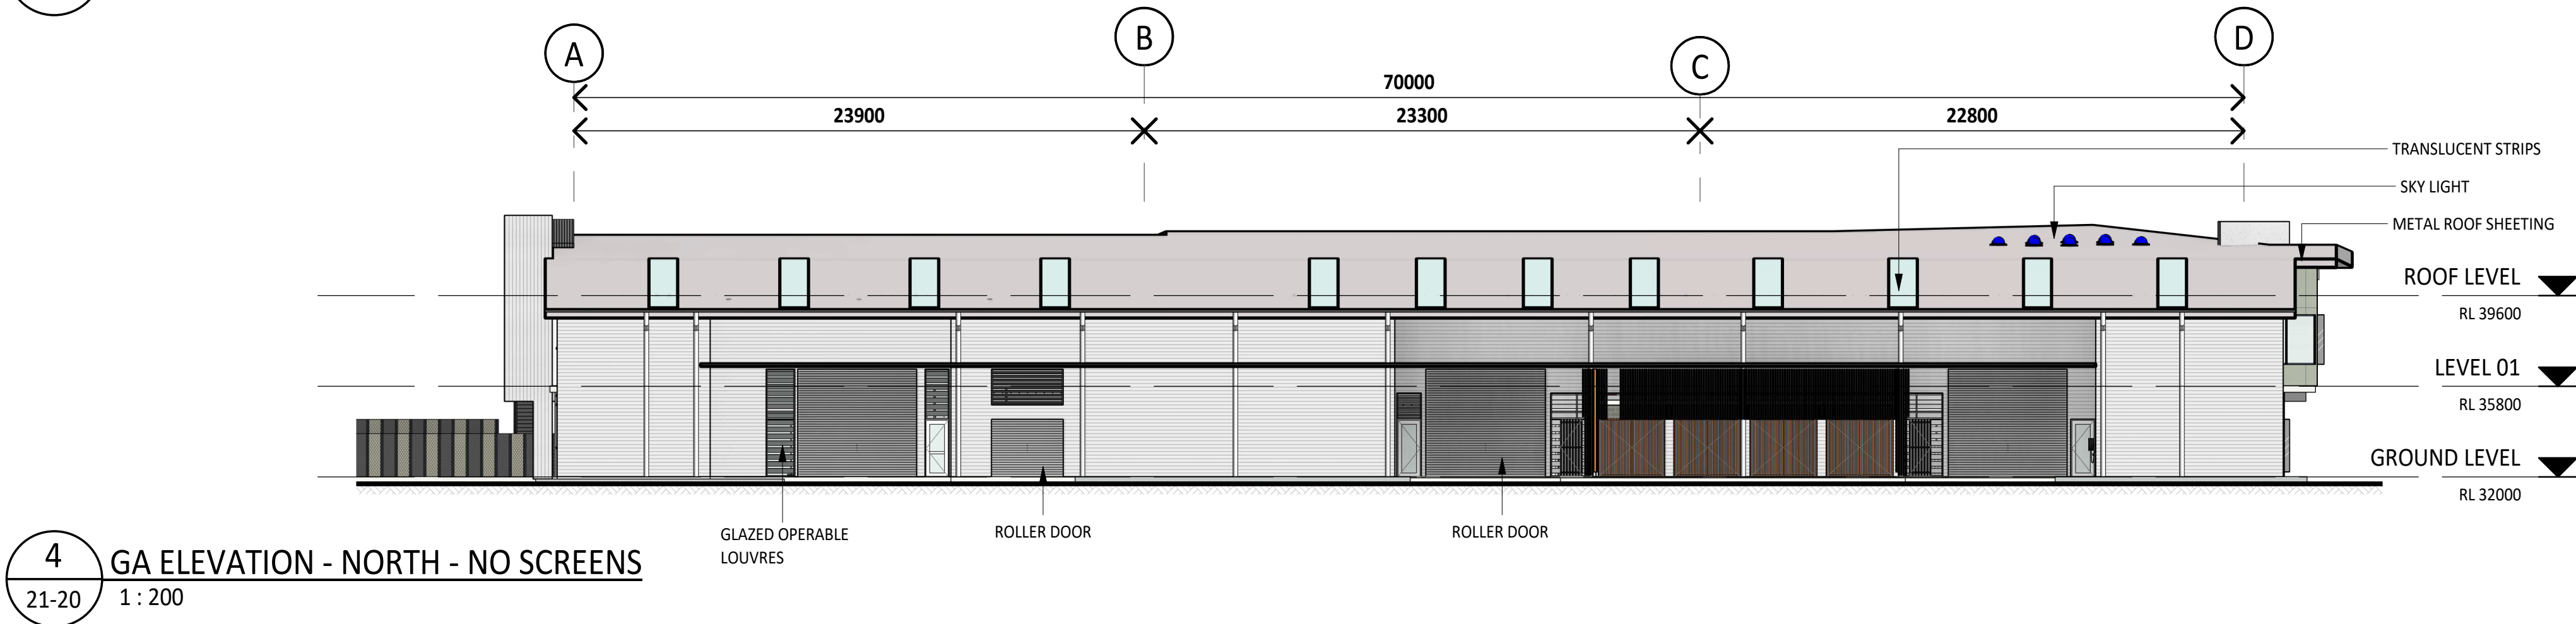
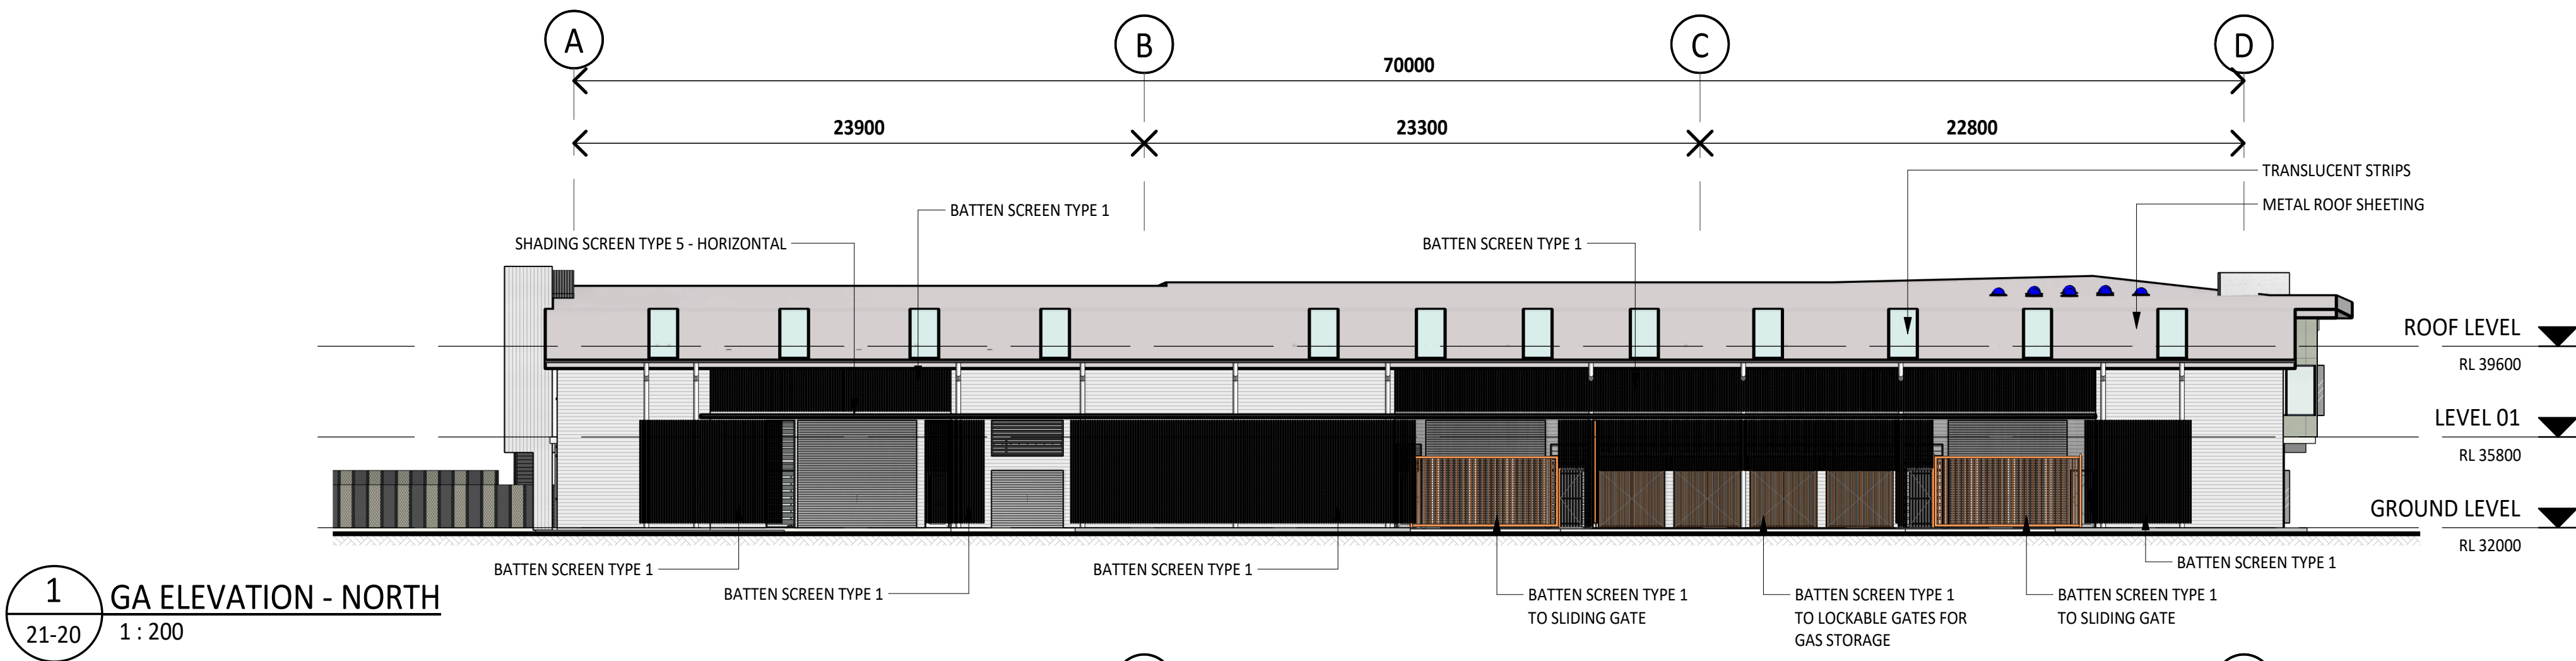


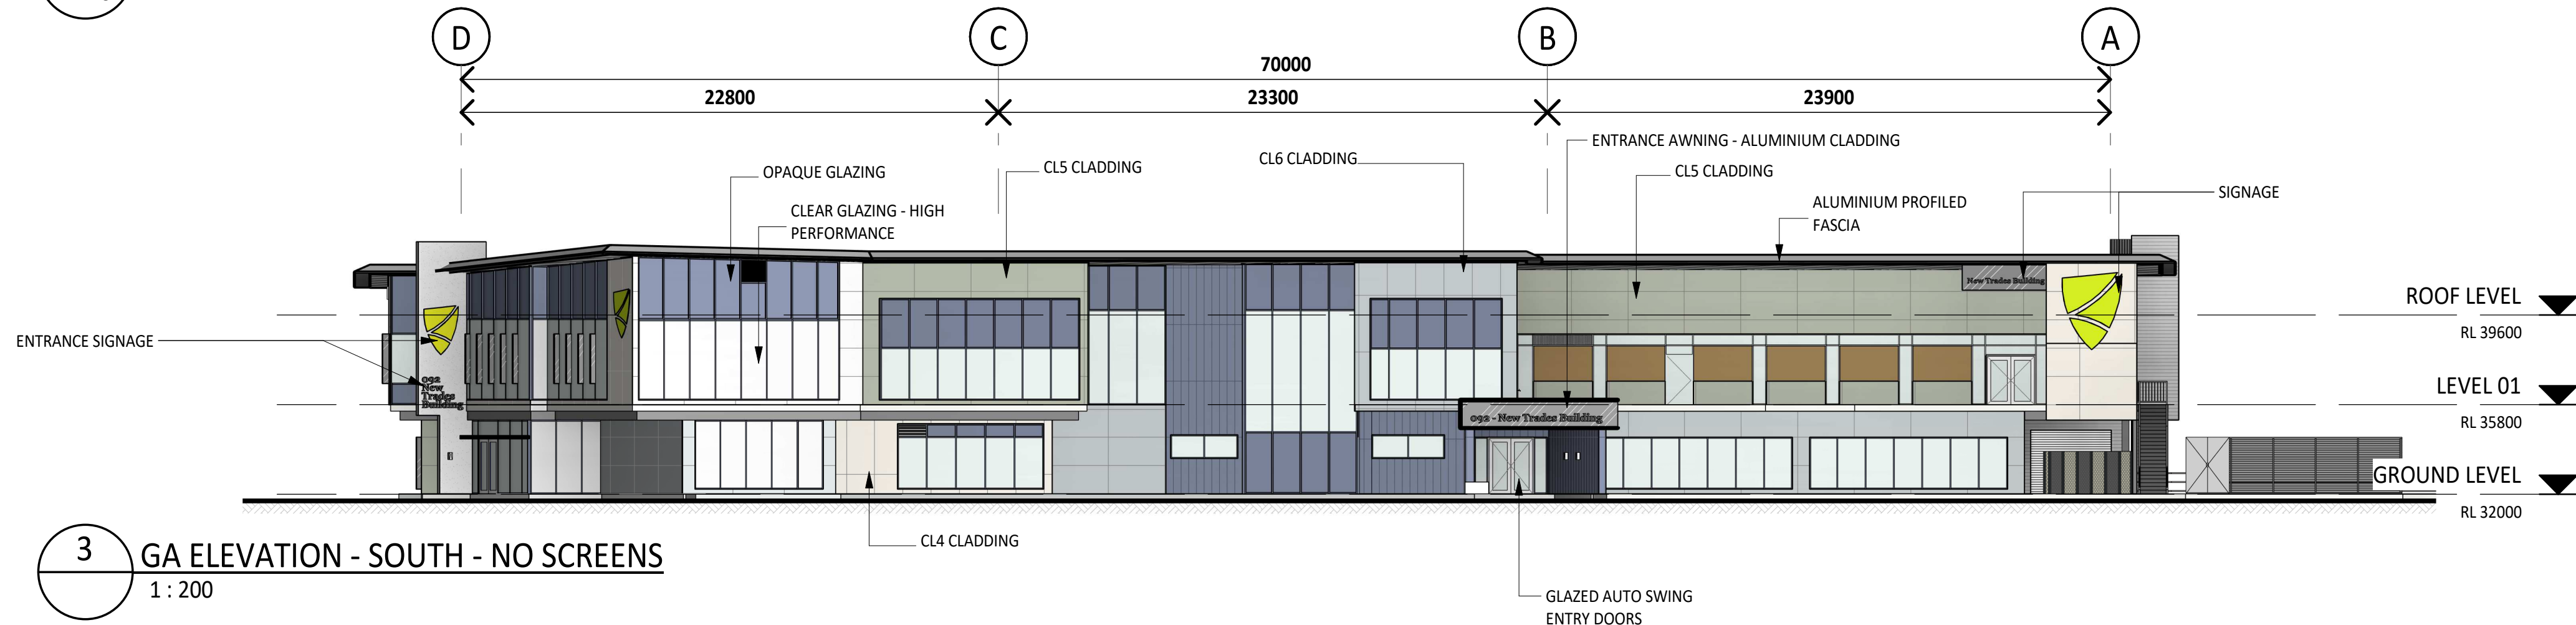

SCREENS HIDDEN FOR CLARITY

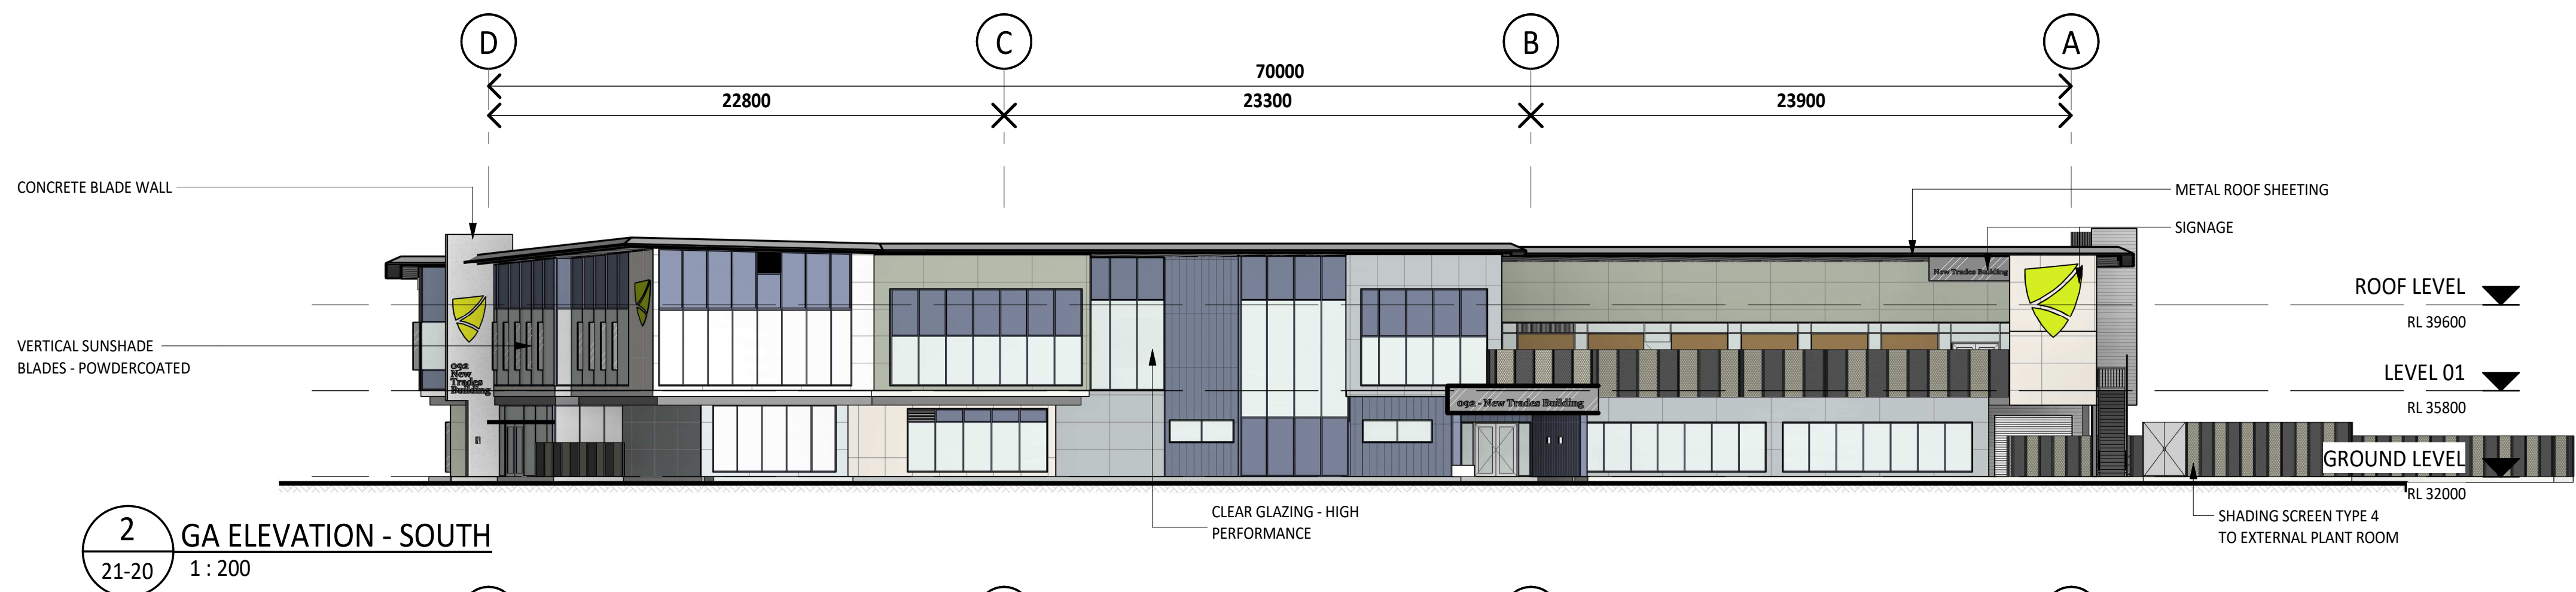

SCREENS HIDDEN FOR CLARITY

thomson
adsett

PEDDLE THORP
architecture | interiors | health | planning

Telephone +61 7 3840 9999
bne@thomsonadsett.com
Level 9, 470 St Pauls Terrace
Fortitude Valley
Qld 4006 Australia
thomsonadsett.com

© Copyright
These drawings and designs and the copyright thereof are the property of Thomson Adsett Pty Ltd and must not be used, retained or copied without written permission of Thomson Adsett Pty Ltd. A.B.N 76 105 314 654 Trading as ThomsonAdsett. Dimensions take precedence over scaling. Do not measure off drawings as print sizes may vary

CQU ROCKHAMPTON TAFE CONSOLIDATION - STAGE 2

554/700 Yaamba Rd, Norman
Gardens QLD 4701

for



A	12/02/26	ISSUED FOR TENDER	BS
3	30/01/26	DRAFT 60% ISSUE	BS
2	20/01/25	DRAFT ISSUE FOR SUSTAINABILITY CONSULTANT	BS
1	24/11/25	50% COSTING ISSUE	BS
rev	date	details	init.

drawn	date
PT	19/12/25
checked	date
BS	19/12/25
verified	date
BS	19/12/25

scale

GA ELEVATIONS SHEET 1

scale project no.
1 : 200 @ A1 260018
revision
A
sheet no.
CQU-ROK-092-00-ARC-30-01

original sheet size - A1 (594mm x 841mm)

ISSUED FOR TENDER

12/02/2026 4:35:45 PM Autodesk Docs:JCQU ROK TAFE/260018_A_CQU-UNIVERSITY_BLD-TRADES_R25.rvt