

CQU ROCKHAMPTON TAFE CONSOLIDATION - STAGE 2

554/700 Yaamba Rd, Norman
Gardens QLD 4701

for



A	12/02/26	ISSUED FOR TENDER	BS
1	30/01/26	DRAFT 60% ISSUE	BS
rev	date	details	init.

drawn	date
PT	30/01/26
checked	date
BS	30/01/26
verified	date
BS	30/01/26


scale

BUILDING ELEVATIONS - NORTH


scale project no.
1 : 100 @ A1 260018

A
sheet no.
CQU-ROK-092-00-ARC-30-10

original sheet size - A1 (594mm x 841mm)

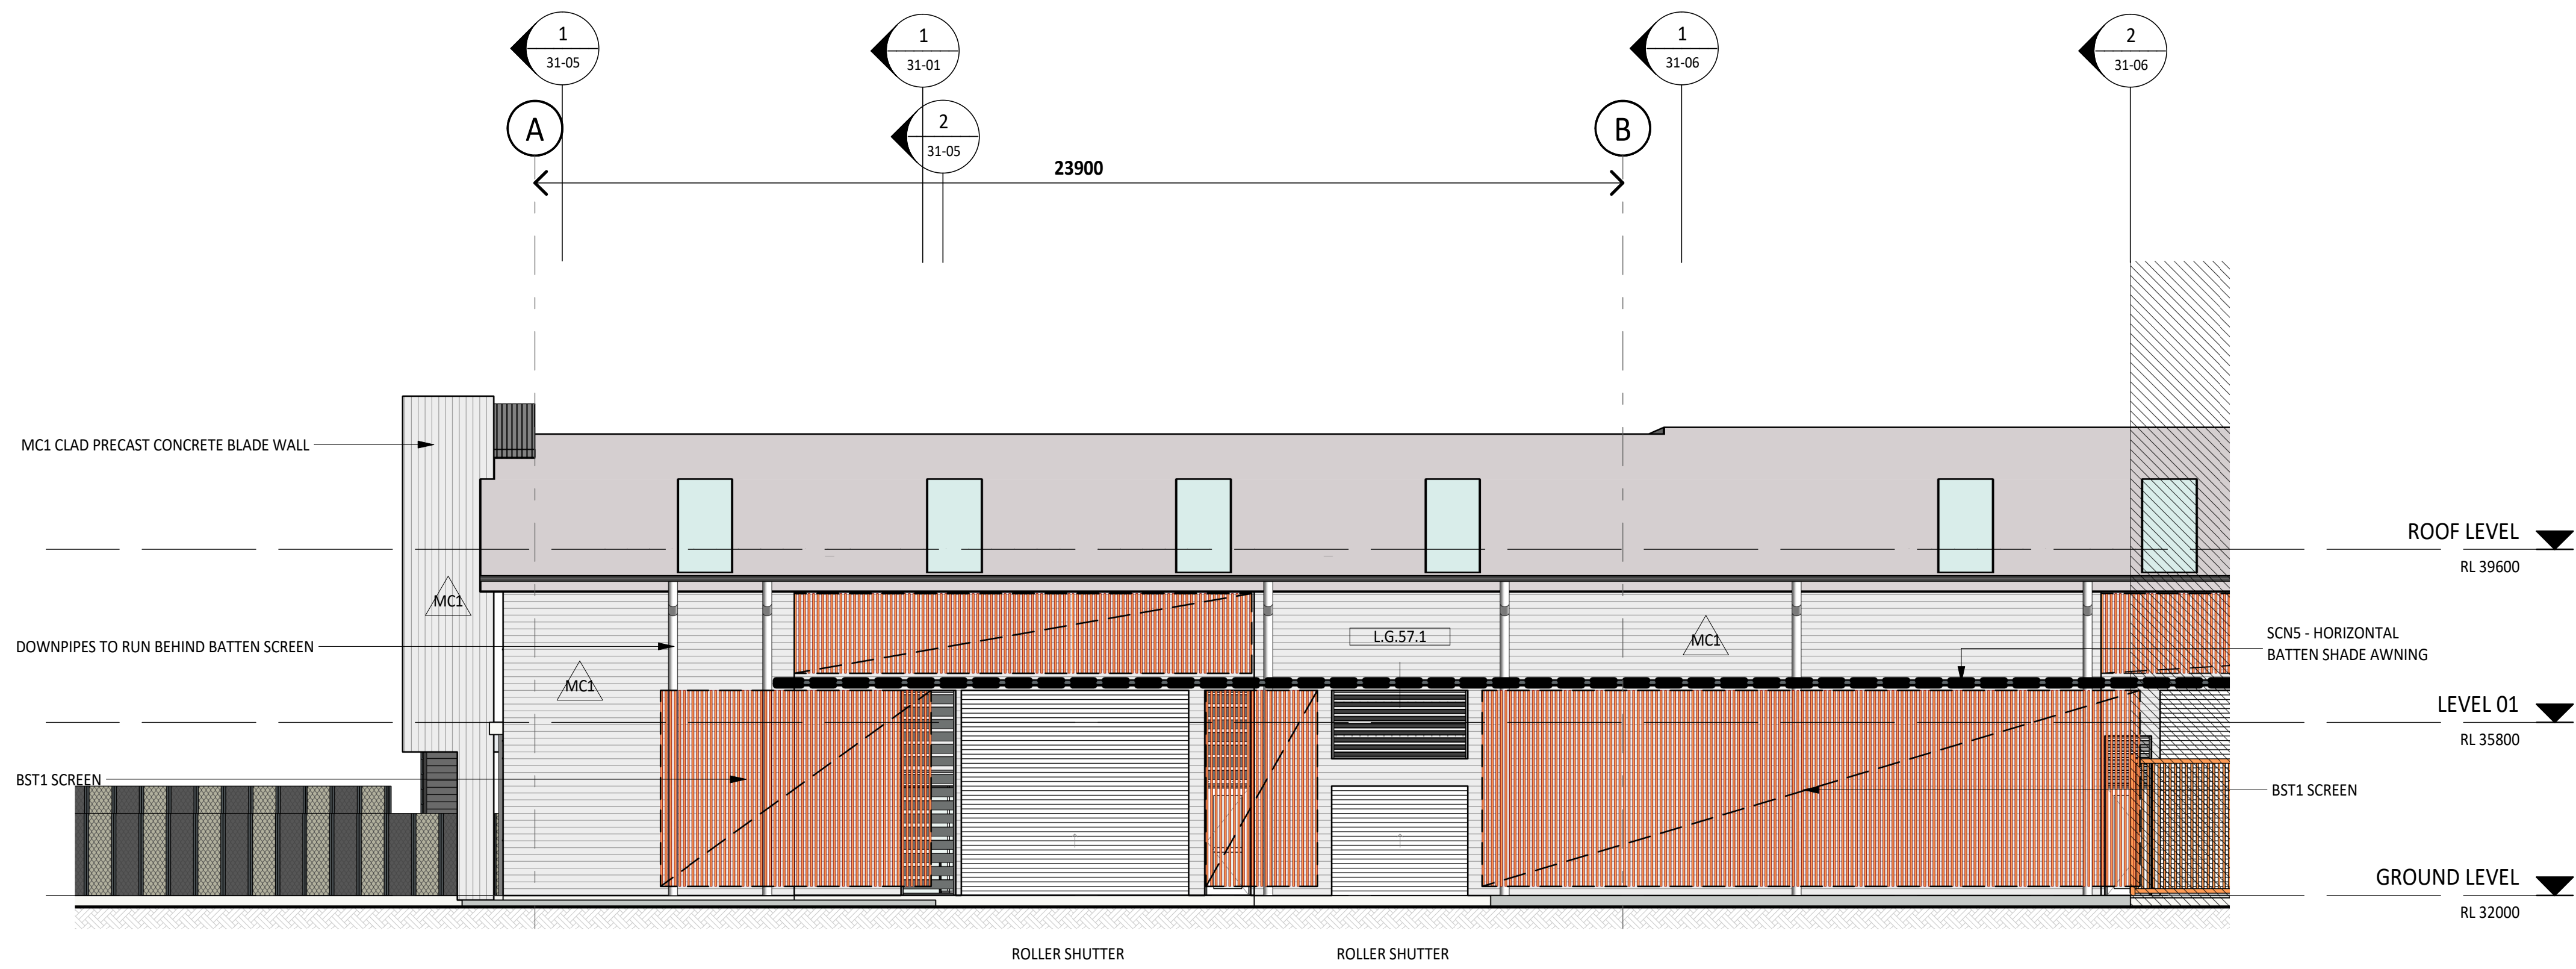

1 BUILDING ELEVATION - NORTH - 1
21-00 1 : 100

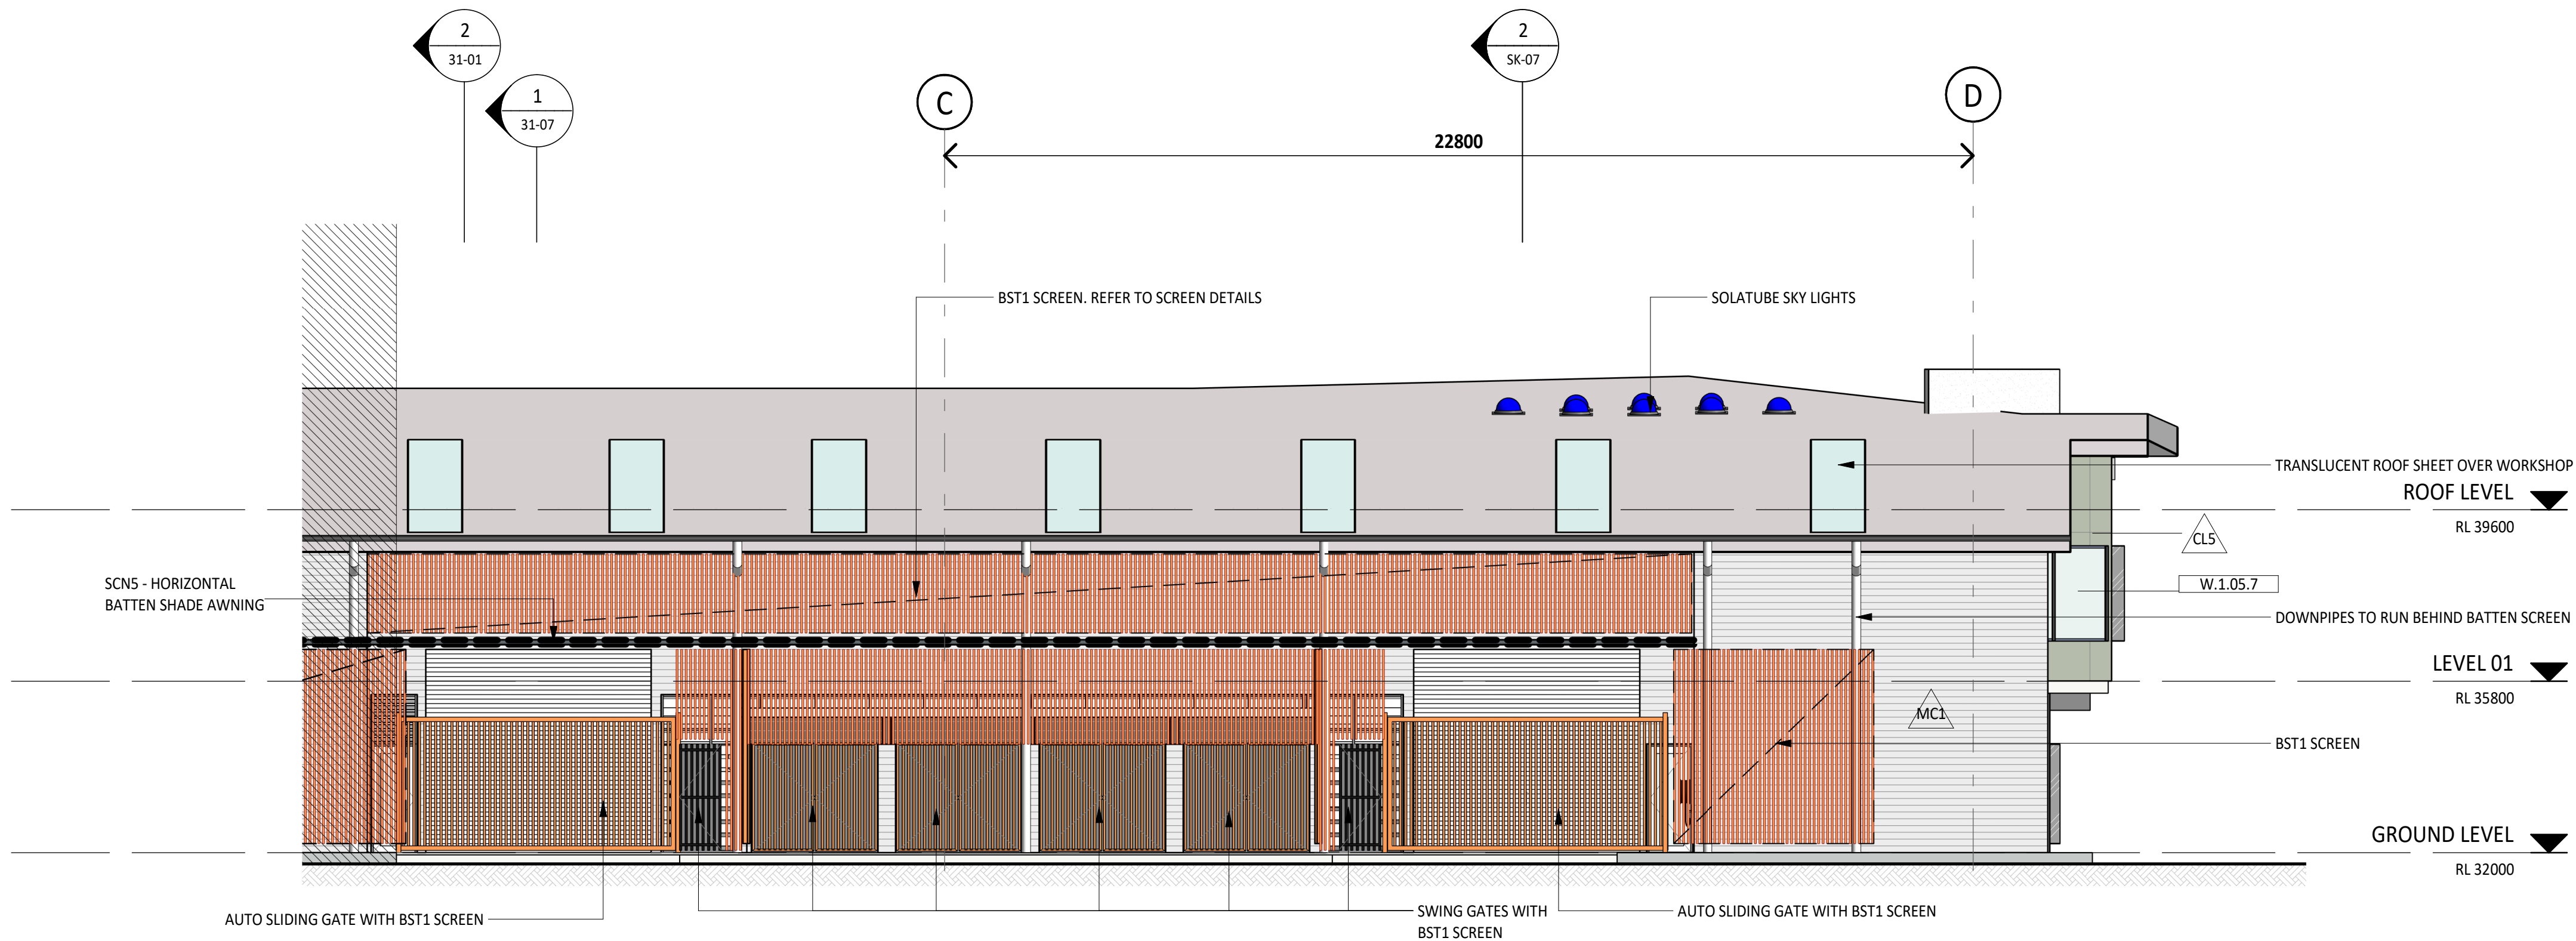

2 BUILDING ELEVATION - NORTH - 2
21-00 1 : 100

EXTERNAL FINISHES SCHEDULE

- CL1 - COMPRESSED FIBRE CEMENT CLADDING - CONCRETE LOOK
- CL2 - SOLID ALUMINIUM CLADDING - BRUSHED ALUMINIUM
- CL3 - NOT USED ON NEW TRADES BUILDING
- CL4 - THROUGH COLOURED FIBRE CEMENT CLADDING - LINEN
- CL5 - THROUGH COLOURED FIBRE CEMENT CLADDING - ASH GREY
- CL6 - THROUGH COLOURED FIBRE CEMENT CLADDING - LIGHT SLATE
- MC1 - PRE-FINISHED METAL PROFILE SHEET CLADDING - CORRUGATED ZINCALUME
- MC2 - PRE-FINISHED METAL PROFILE SHEET CLADDING - CORRUGATED ZINCALUME - MINI PROFILE
- MC3 - PRE-FINISHED METAL PROFILE SHEET CLADDING - STANDING SEAM - COLORBOND DEEP OCEAN
- BS1 - ALUMINIUM BATTEN SCREEN - 3X BATTEN PROFILES - REFER PLAN FOR SET OUT DETAILS
- DP - DOWNPIPE - REFER TO SPECIFICATION FOR SIZE & FINISHES

BUILDING ELEVATION NOTES



FINISHES TAG

1. CLADDING CL4, CL5, AND CL6 HAS A NON TYPICAL PANEL BREAK UP. REFER TO DETAIL ELEVATION FOR SET OUT
2. SHADE SCREENS HIDDEN FOR CLARITY. REFER TO GENERAL ARRANGEMENT ELEVATIONS FOR EXTENT, AND SCREEN DETAILS ON 44-00 SERIES

PLANS TO BE PRINTED IN COLOUR

ISSUED FOR TENDER