




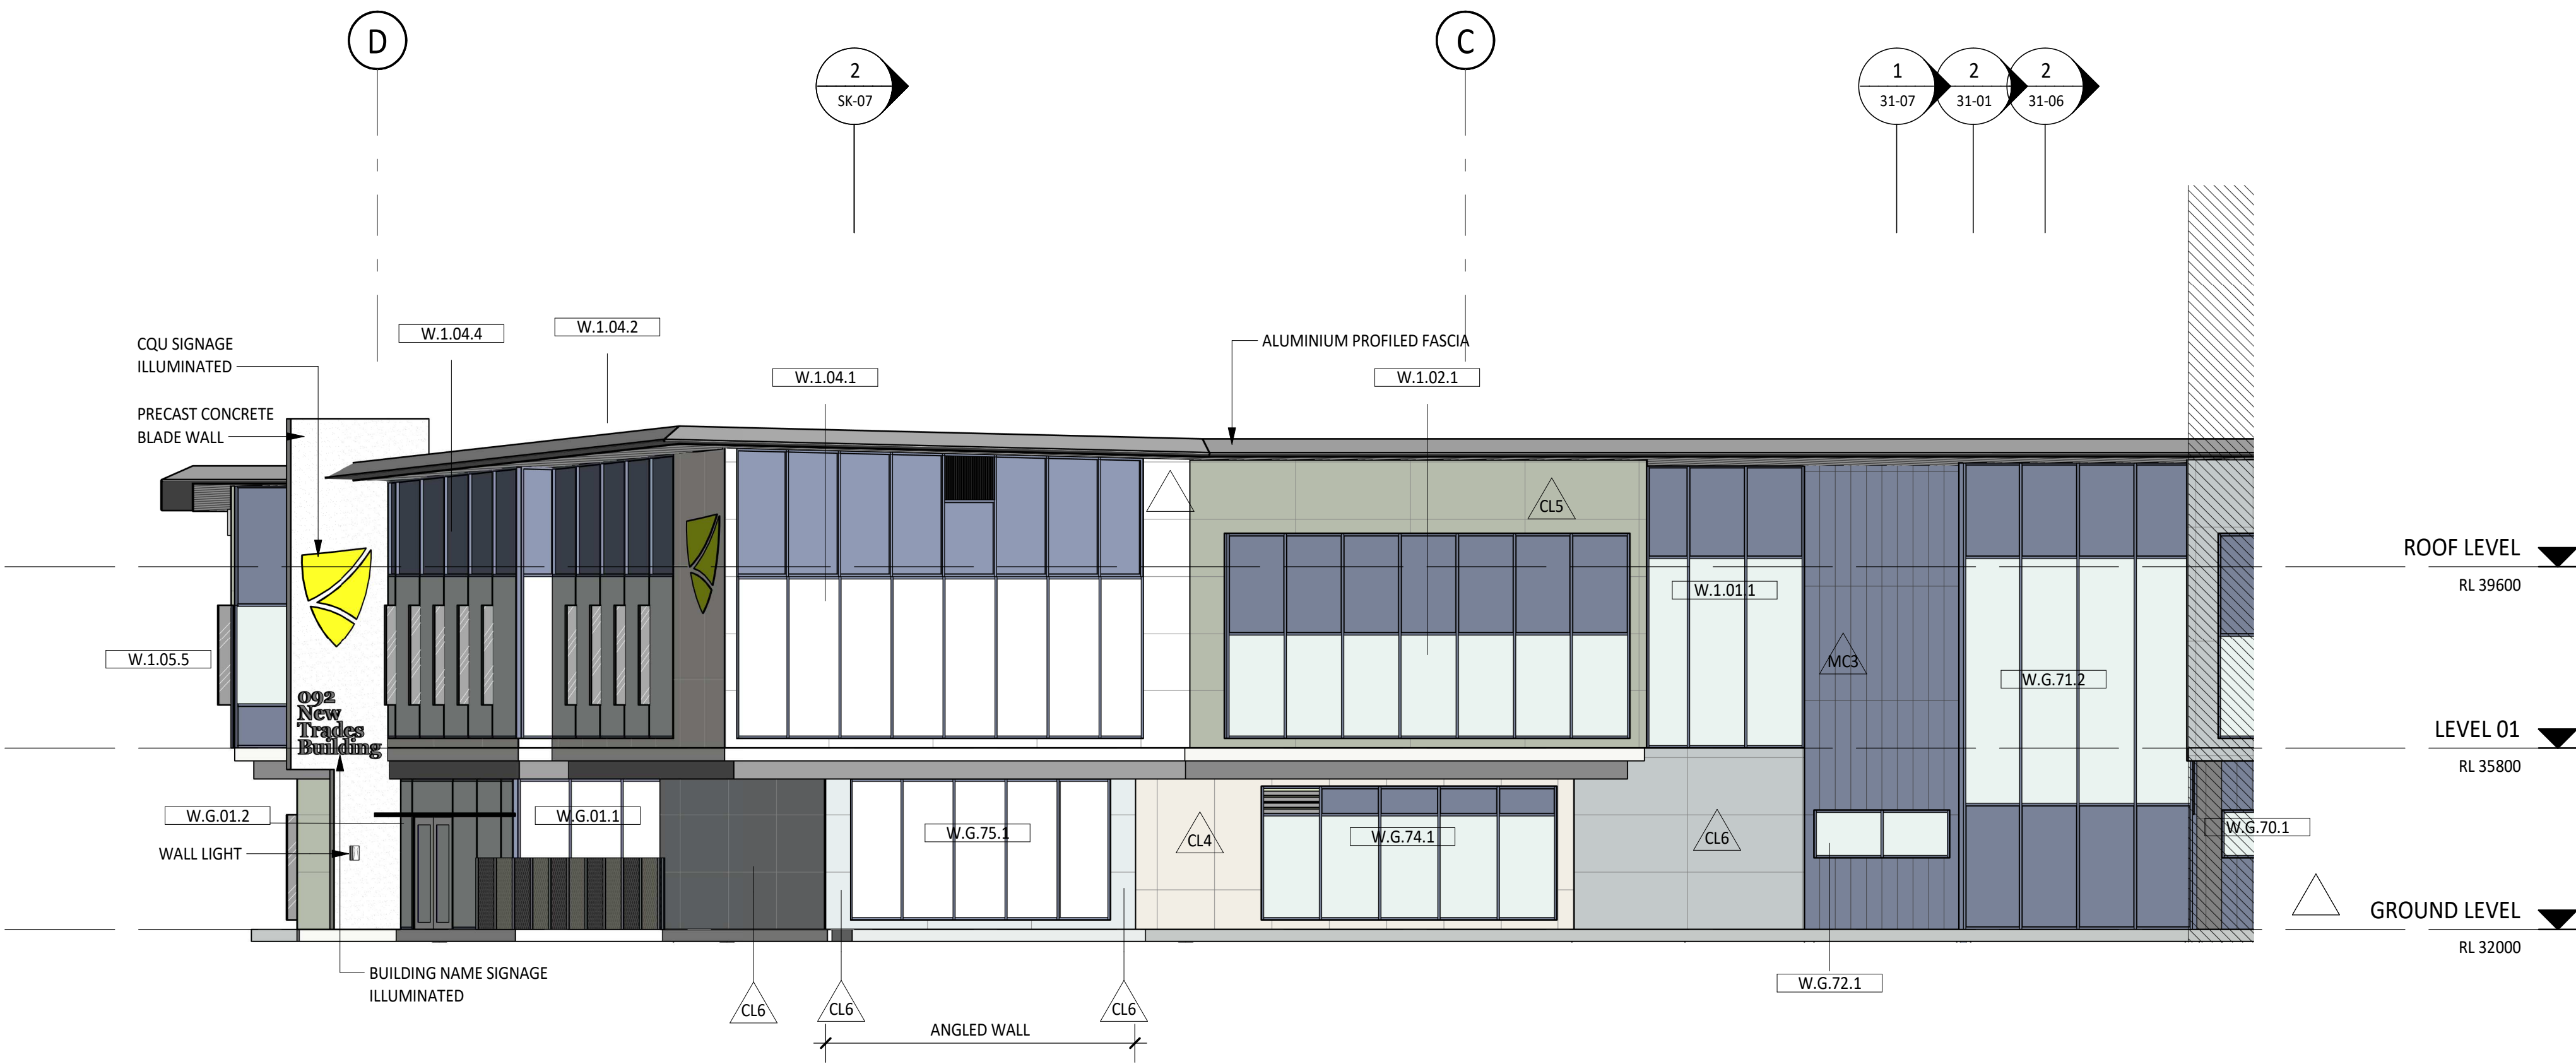


1 BUILDING ELEVATION - SOUTH - 1
21-00 1 : 100

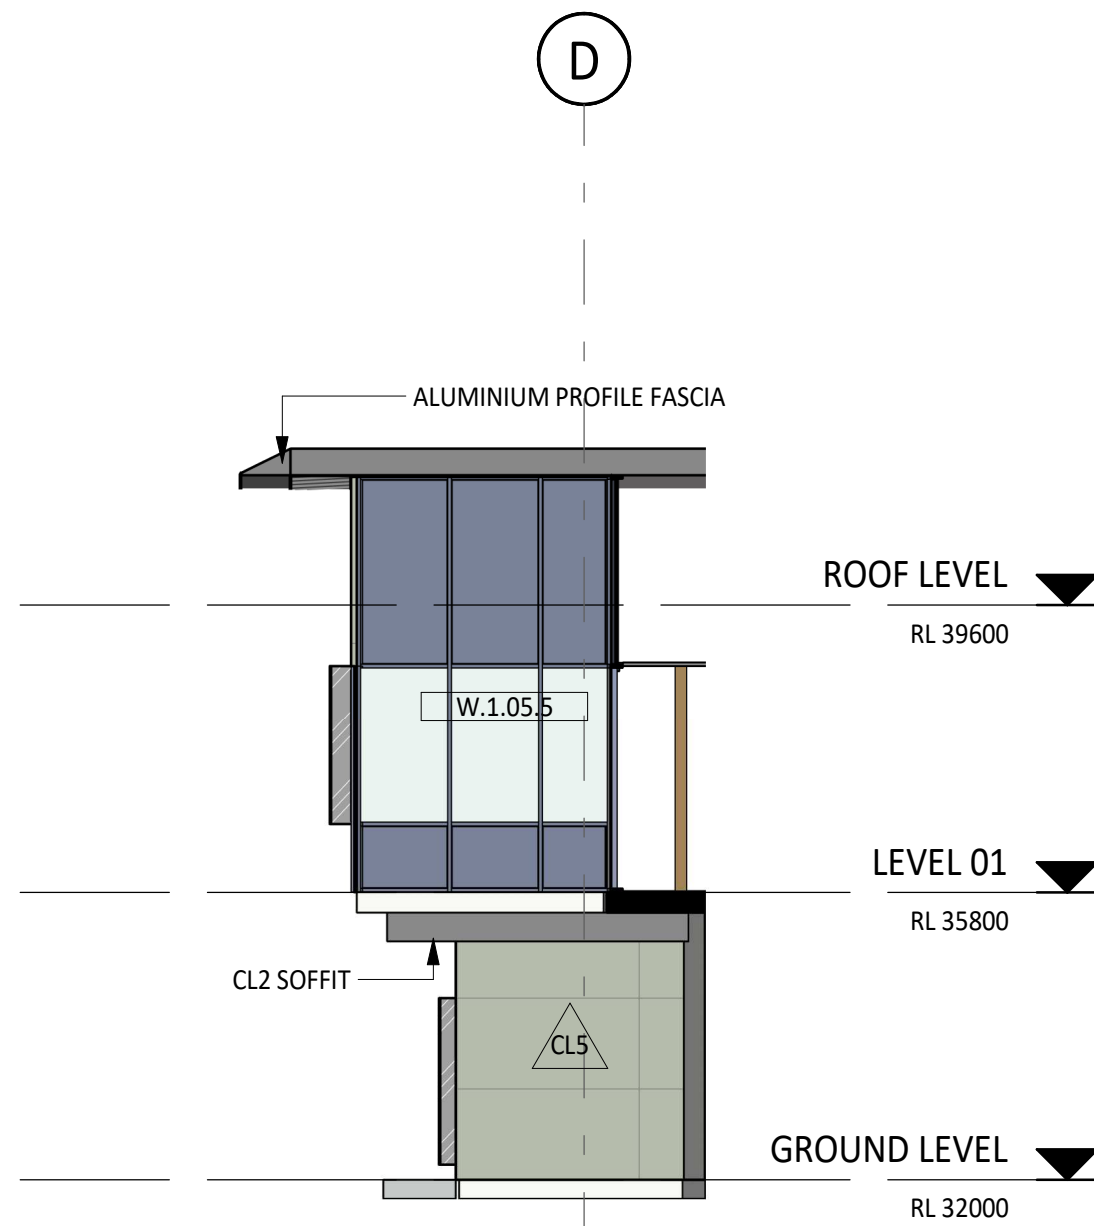

3 BUILDING ELEVATION - SOUTH - 3
21-00 1 : 100

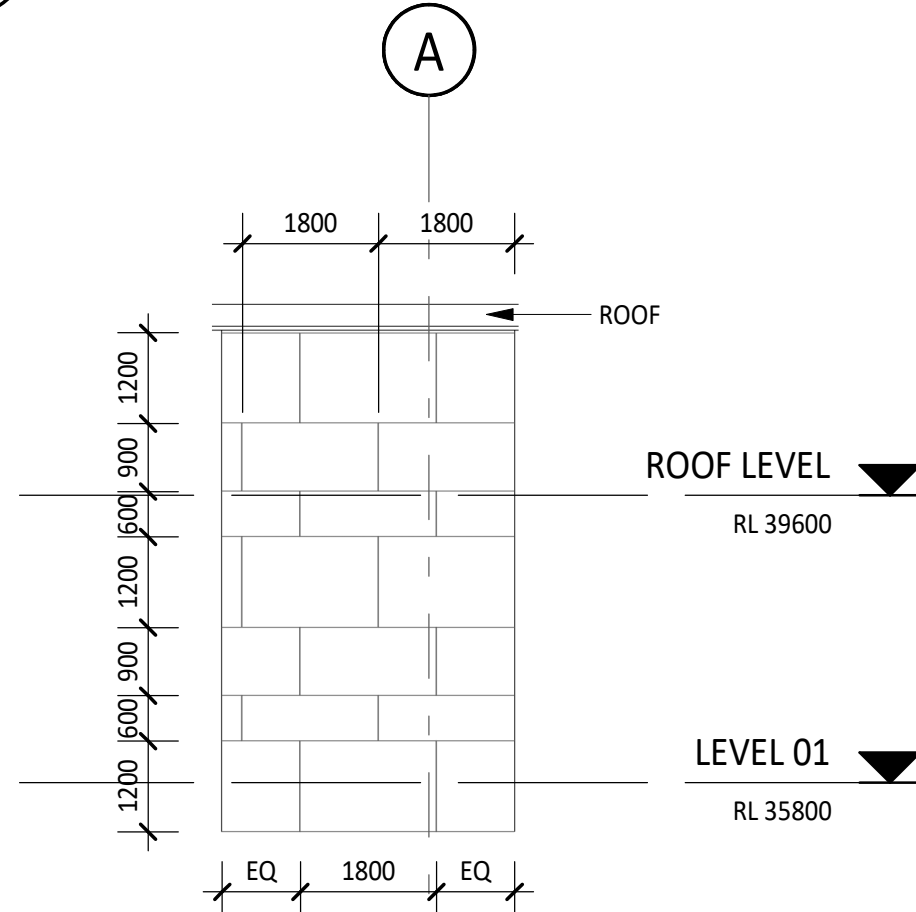

4 BUILDING ELEVATION - TYPICAL CFC PATTERN
30-11 1 : 100

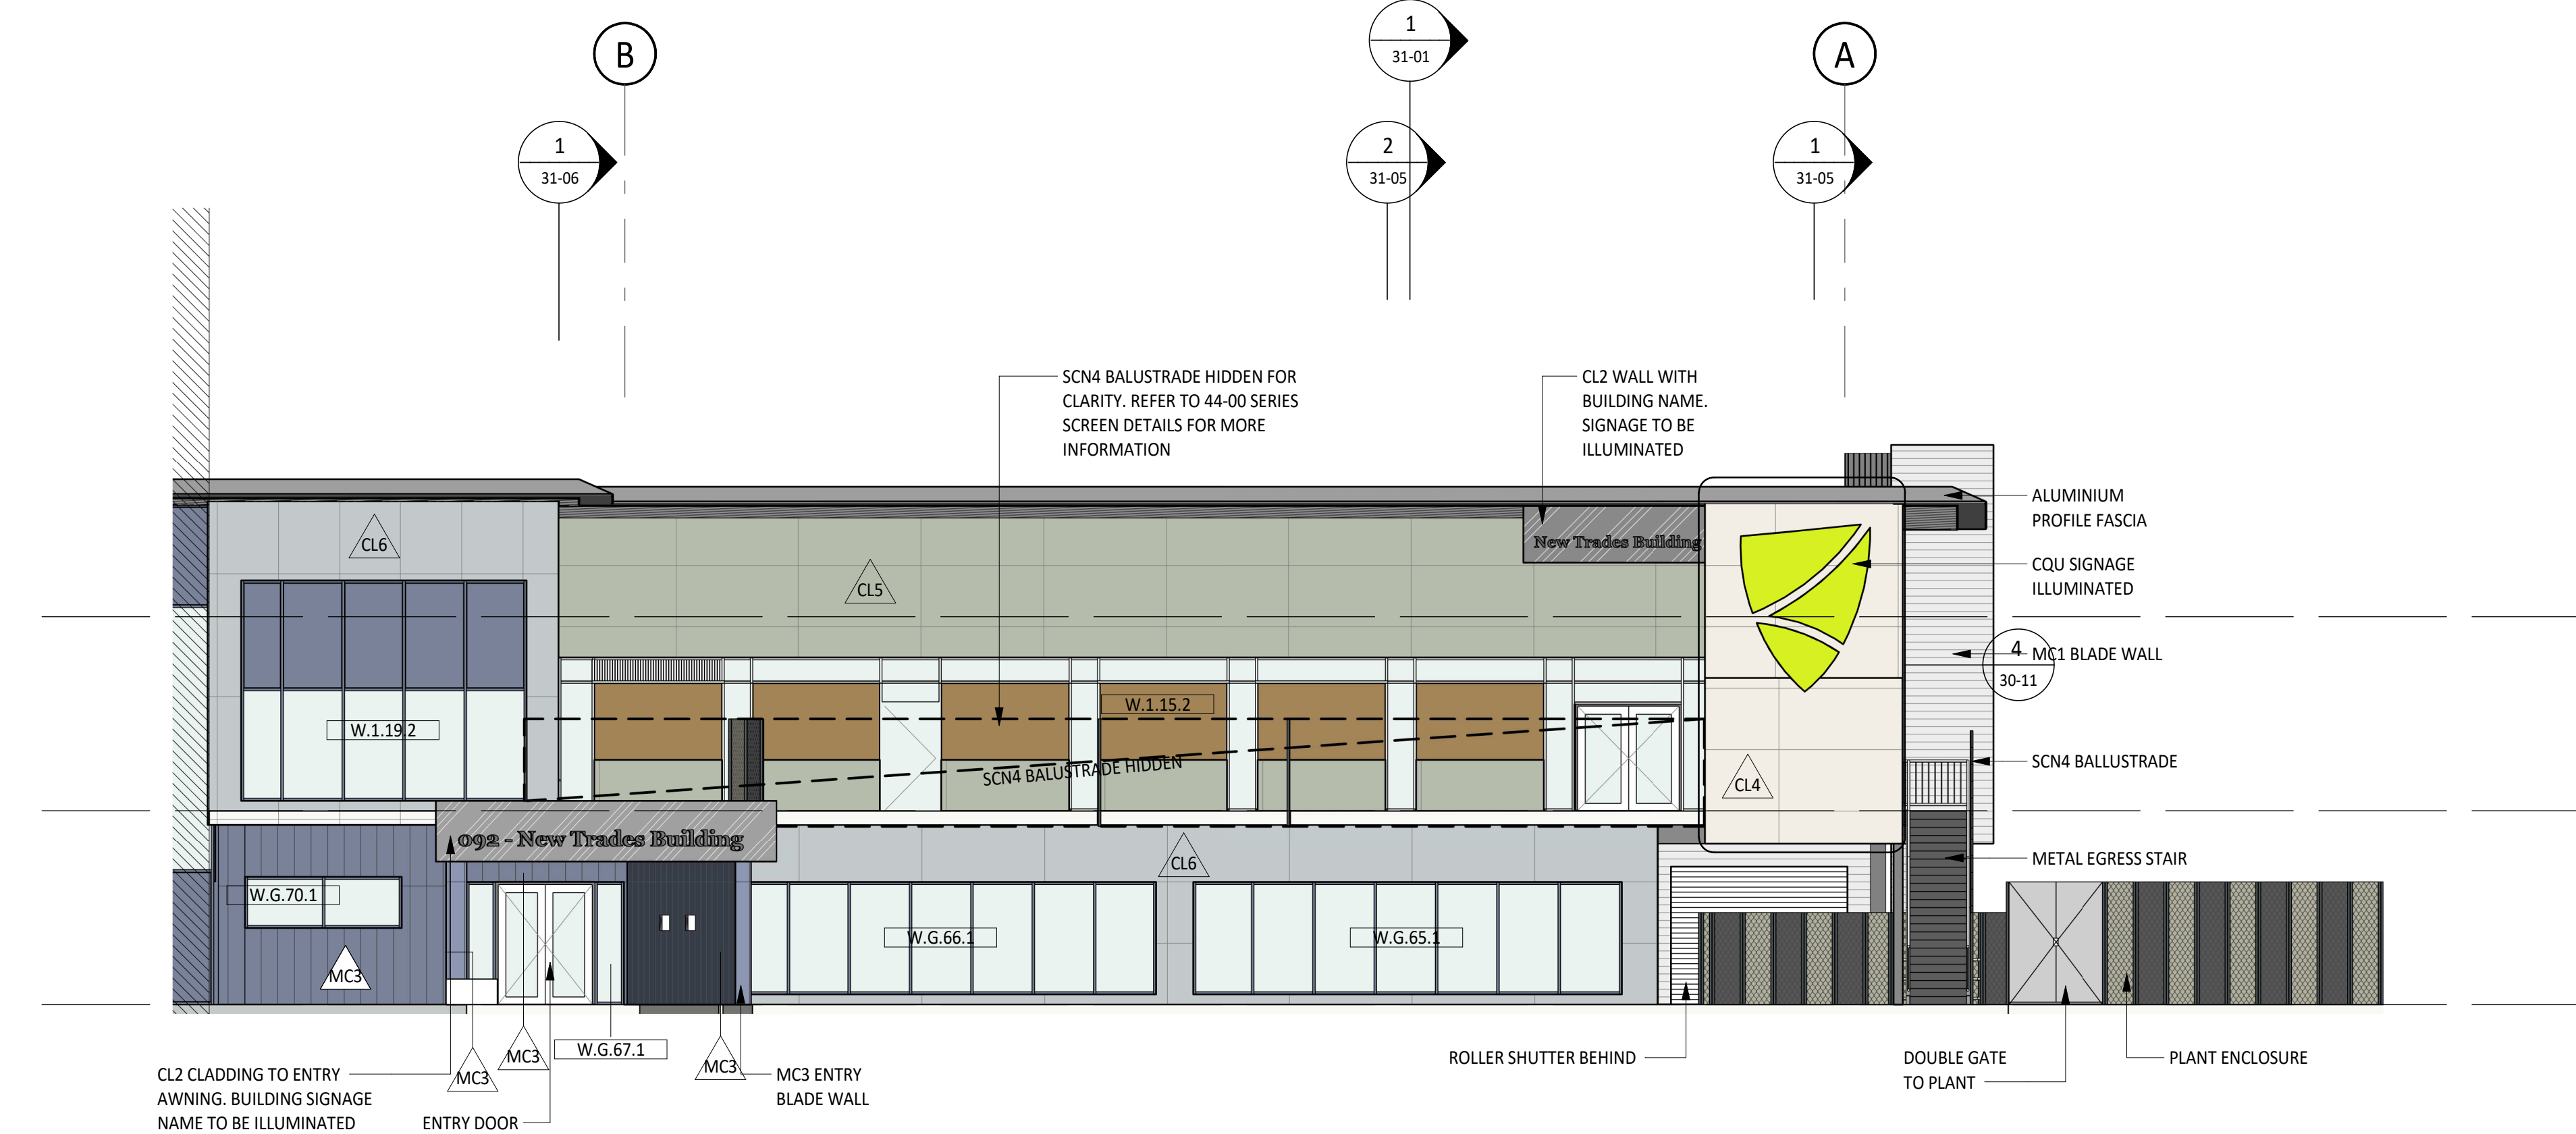

2 BUILDING ELEVATION - SOUTH - 2
21-00 1 : 100

EXTERNAL FINISHES SCHEDULE			
CL1 - COMPRESSED FIBRE CEMENT CLADDING - CONCRETE LOOK			
CL2 - SOLID ALUMINIUM CLADDING - BRUSHED ALUMINIUM			
CL3 - NOT USED ON NEW TRADES BUILDING			
CL4 - THROUGH COLOURED FIBRE CEMENT CLADDING - LINEN			
CL5 - THROUGH COLOURED FIBRE CEMENT CLADDING - ASH GREY			
CL6 - THROUGH COLOURED FIBRE CEMENT CLADDING - LIGHT SLATE			
MC1 - PRE-FINISHED METAL PROFILE SHEET CLADDING - CORRUGATED ZINCALUME			
MC2 - PRE-FINISHED METAL PROFILE SHEET CLADDING - CORRUGATED ZINCALUME - MINI PROFILE			
MC3 - PRE-FINISHED METAL PROFILE SHEET CLADDING - STANDING SEAM - COLORBOND DEEP OCEAN			
BST1 - ALUMINIUM BATTEN SCREEN - 3X BATTEN PROFILES - REFER PLAN FOR SET OUT DETAILS			
DP - DOWNPIPE - REFER TO SPECIFICATION FOR SIZE & FINISHES			

BUILDING ELEVATION NOTES	
△	FINISHES TAG
1. CLADDING CL4, CL5, AND CL6 HAS A NON TYPICAL PANEL BREAK UP. REFER TO DETAIL ELEVATION FOR SET OUT	
2. SHADE SCREENS HIDDEN FOR CLARITY. REFER TO GENERAL ARRANGEMENT ELEVATIONS FOR EXTENT, AND SCREEN DETAILS ON 44-00 SERIES	

PLANS TO BE PRINTED IN COLOUR

© Copyright
These drawings and designs and the copyright thereof are the property of Thomson Adsett Pty Ltd and must not be used, retained or copied without written permission of Thomson Adsett Pty Ltd. ABN 76 105 314 654 Trading as ThomsonAdsett. Dimensions take precedence over scaling. Do not measure off drawings as print sizes may vary

CQU ROCKHAMPTON TAFE CONSOLIDATION - STAGE 2

554/700 Yaamba Rd, Norman
Gardens QLD 4701



A	12/02/26	ISSUED FOR TENDER	BS
1	30/01/26	DRAFT 60% ISSUE	BS
rev	date	details	init.

scale

BUILDING ELEVATIONS - SOUTH

scale 1 : 100 @ A1 project no. 260018

revision A sheet no. CQU-ROK-092-00-ARC-30-11

ISSUED FOR TENDER