




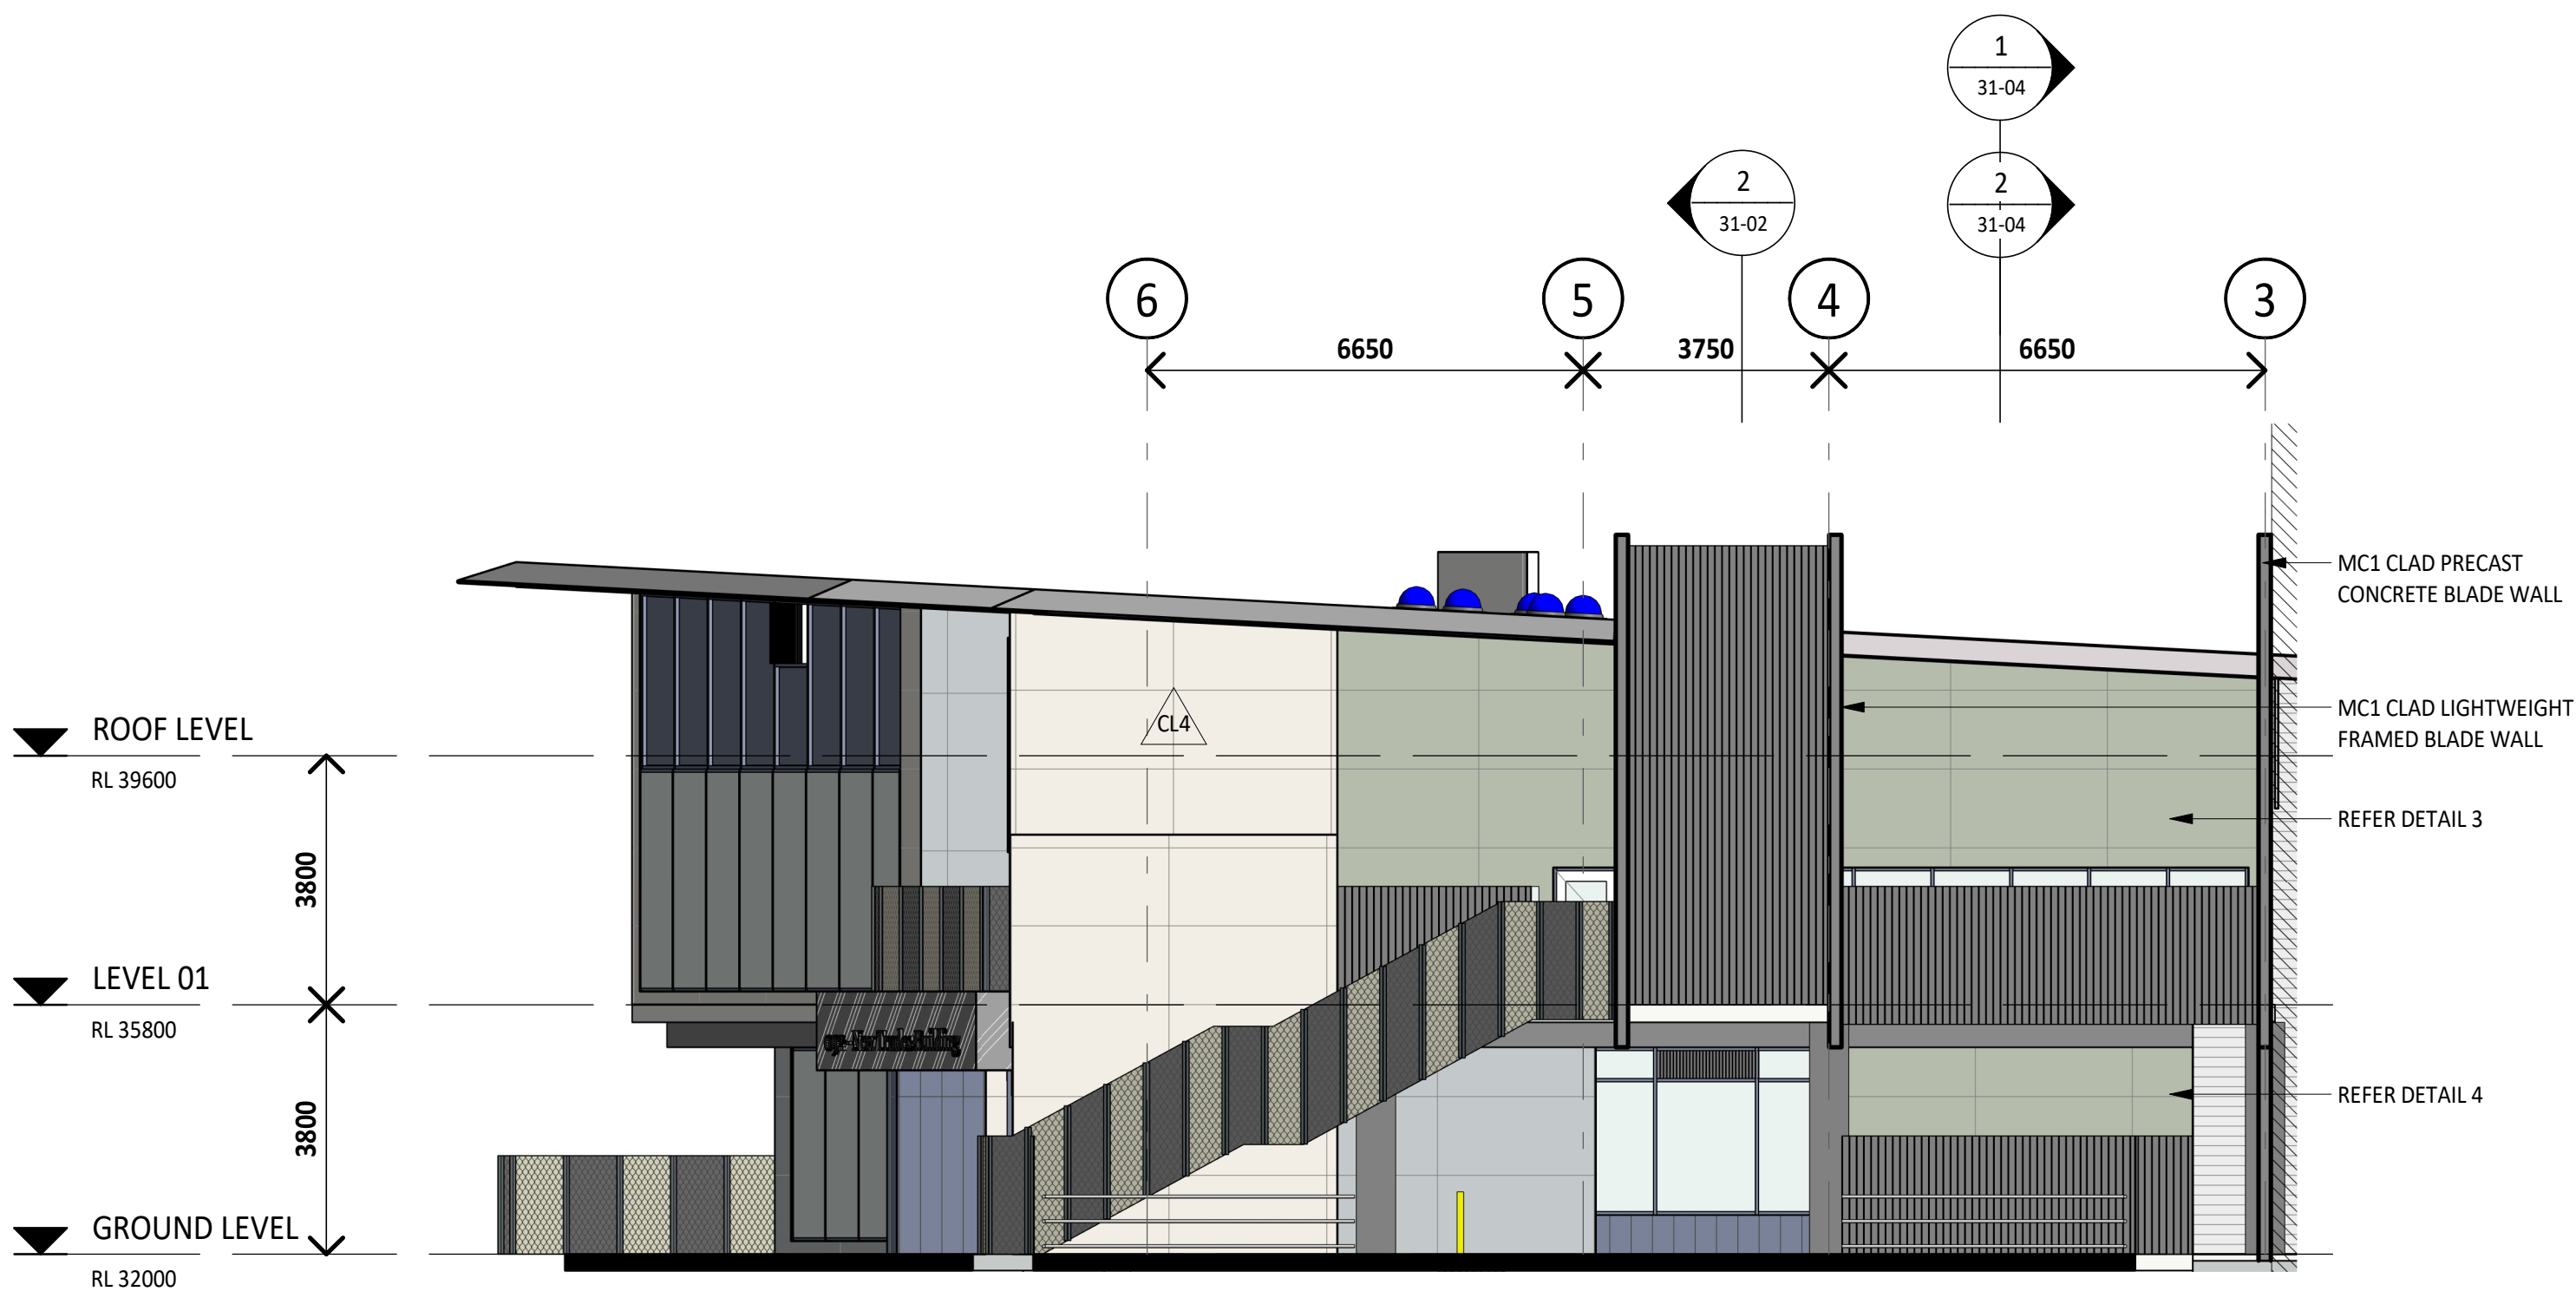


1 BUILDING ELEVATION - EAST - 1
21-00 1 : 100

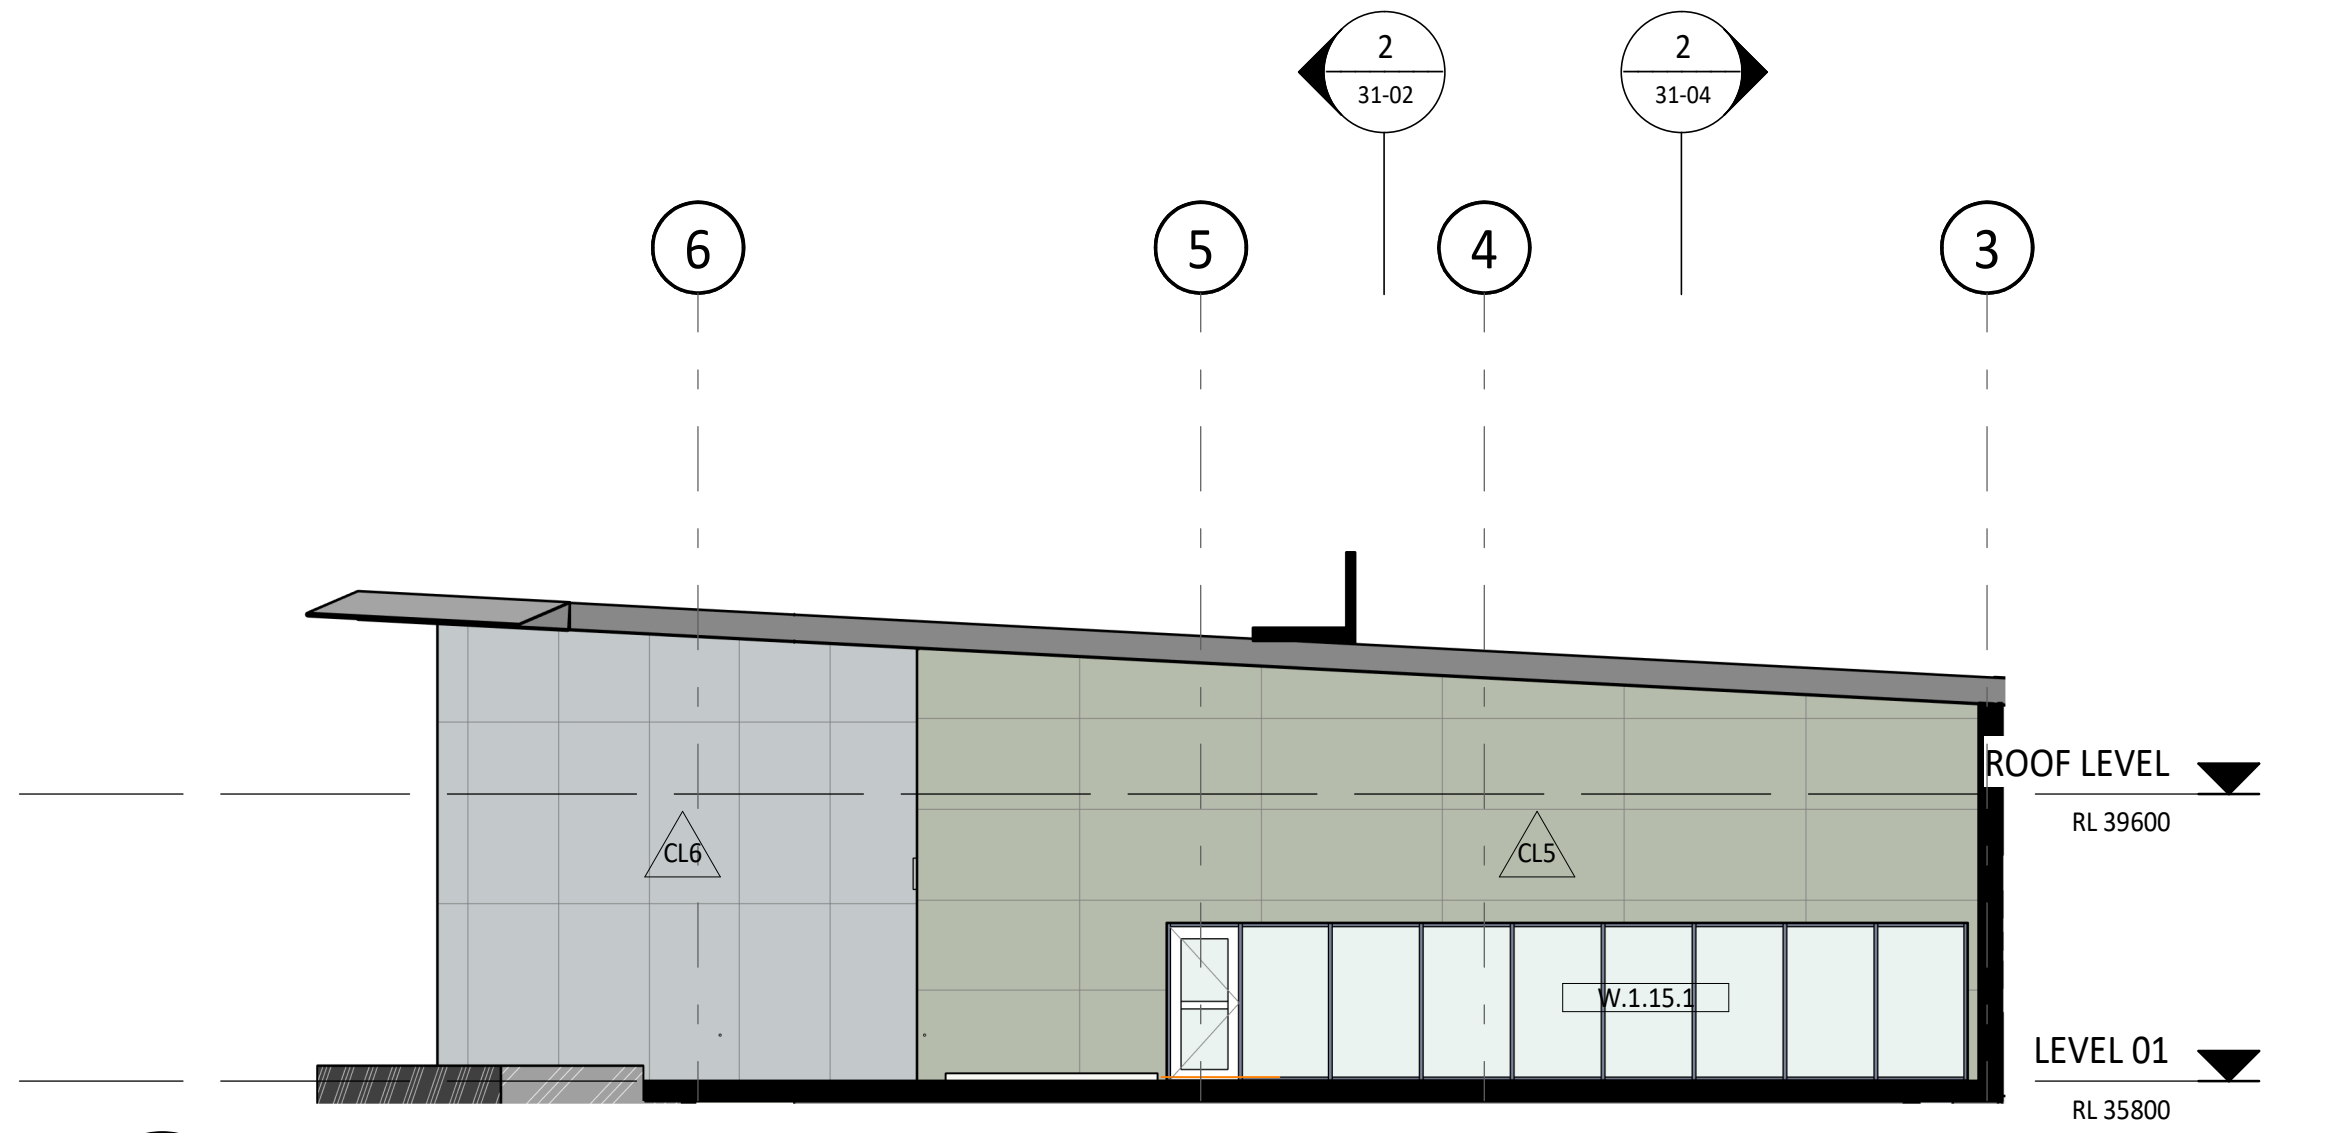

3 EAST ELEVATION 2
21-10 1 : 100

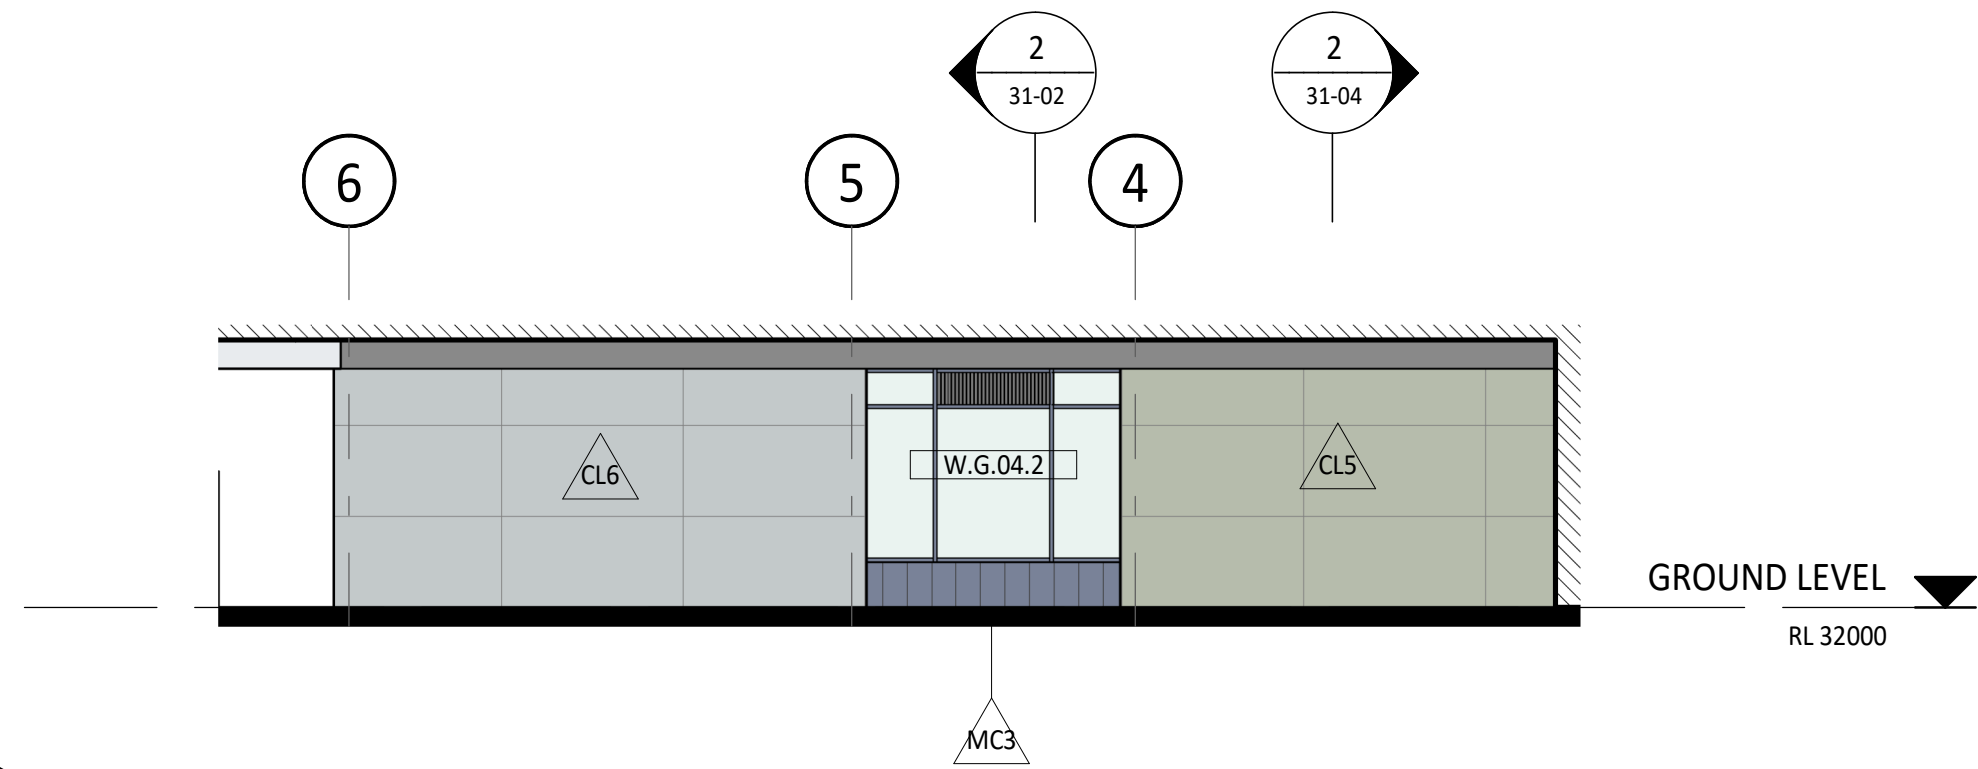

4 EAST ELEVATION 3
21-00 1 : 100

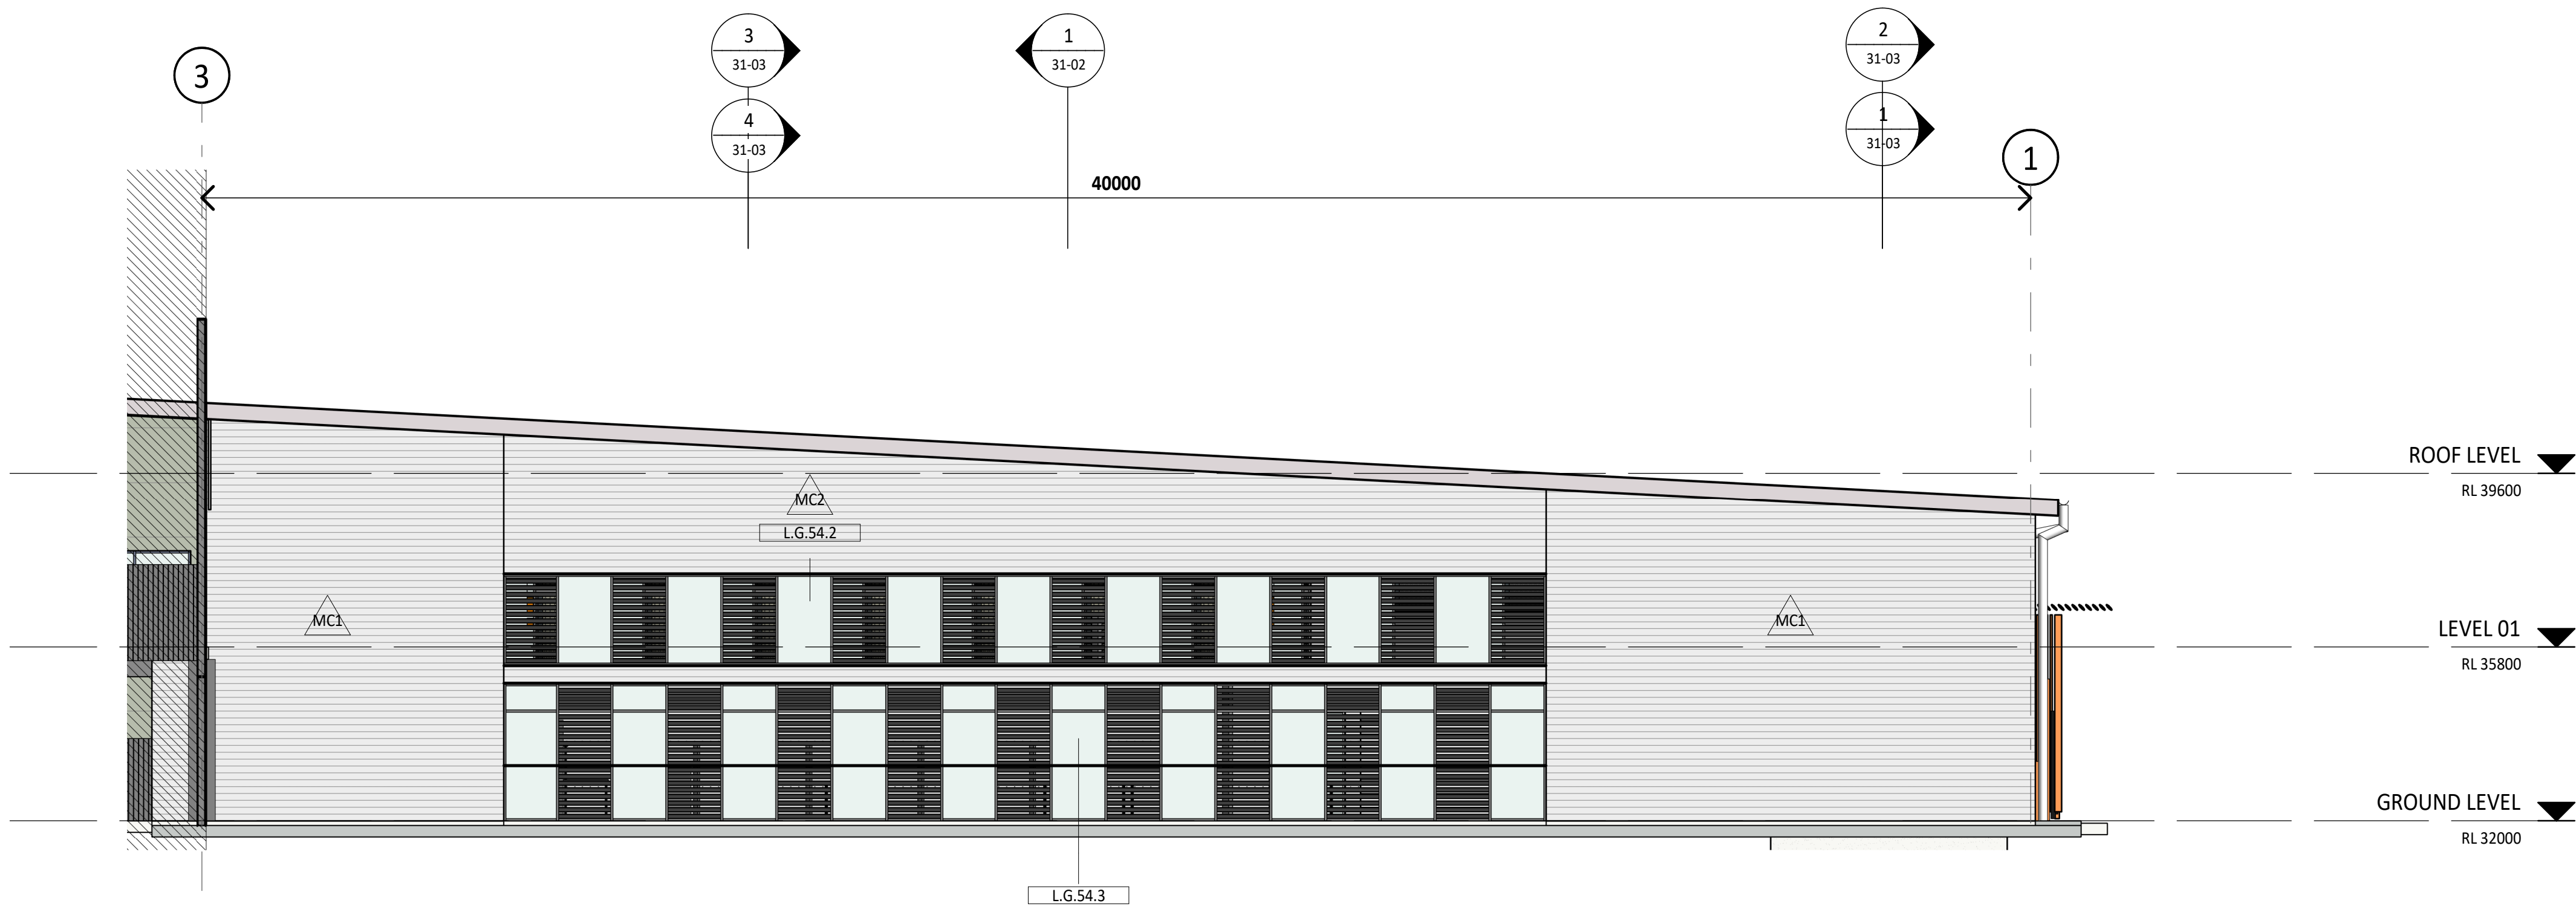

2 BUILDING ELEVATION - EAST - 2
21-00 1 : 100

EXTERNAL FINISHES SCHEDULE			
CL1 - COMPRESSED FIBRE CEMENT CLADDING - CONCRETE LOOK			
CL2 - SOLID ALUMINIUM CLADDING - BRUSHED ALUMINIUM			
CL3 - NOT USED ON NEW TRADES BUILDING			
CL4 - THROUGH COLOURED FIBRE CEMENT CLADDING - LINEN			
CL5 - THROUGH COLOURED FIBRE CEMENT CLADDING - ASH GREY			
CL6 - THROUGH COLOURED FIBRE CEMENT CLADDING - LIGHT SLATE			
MC1 - PRE-FINISHED METAL PROFILE SHEET CLADDING - CORRUGATED ZINCALUME			
MC2 - PRE-FINISHED METAL PROFILE SHEET CLADDING - CORRUGATED ZINCALUME - MINI PROFILE			
MC3 - PRE-FINISHED METAL PROFILE SHEET CLADDING - STANDING SEAM - COLORBOND DEEP OCEAN			
BS1 - ALUMINIUM BATTEN SCREEN - 3X BATTEN PROFILES - REFER PLAN FOR SET OUT DETAILS			
DP - DOWNPIPE - REFER TO SPECIFICATION FOR SIZE & FINISHES			
BUILDING ELEVATION NOTES			
1. CLADDING CL4, CL5, AND CL6 HAS A NON TYPICAL PANEL BREAK UP. REFER TO DETAIL ELEVATION FOR SET OUT			
2. SHADE SCREENS HIDDEN FOR CLARITY. REFER TO GENERAL ARRANGEMENT ELEVATIONS FOR EXTENT, AND SCREEN DETAILS ON 44-00 SERIES			
PLANS TO BE PRINTED IN COLOUR			

B	05/03/26	ISSUED FOR TENDER	BS
A	12/02/26	ISSUED FOR TENDER	BS
1	30/01/26	DRAFT 60% ISSUE	BS
rev	date	details	init.

drawn	date
PT	30/01/26
checked	date
BS	30/01/26
verified	date
BS	30/01/26

scale

BUILDING ELEVATIONS - EAST

scale project no.
1 : 100 @ A1 260018

revision
B
sheet no.
CQU-ROK-092-00-ARC-30-12

ISSUED FOR TENDER