




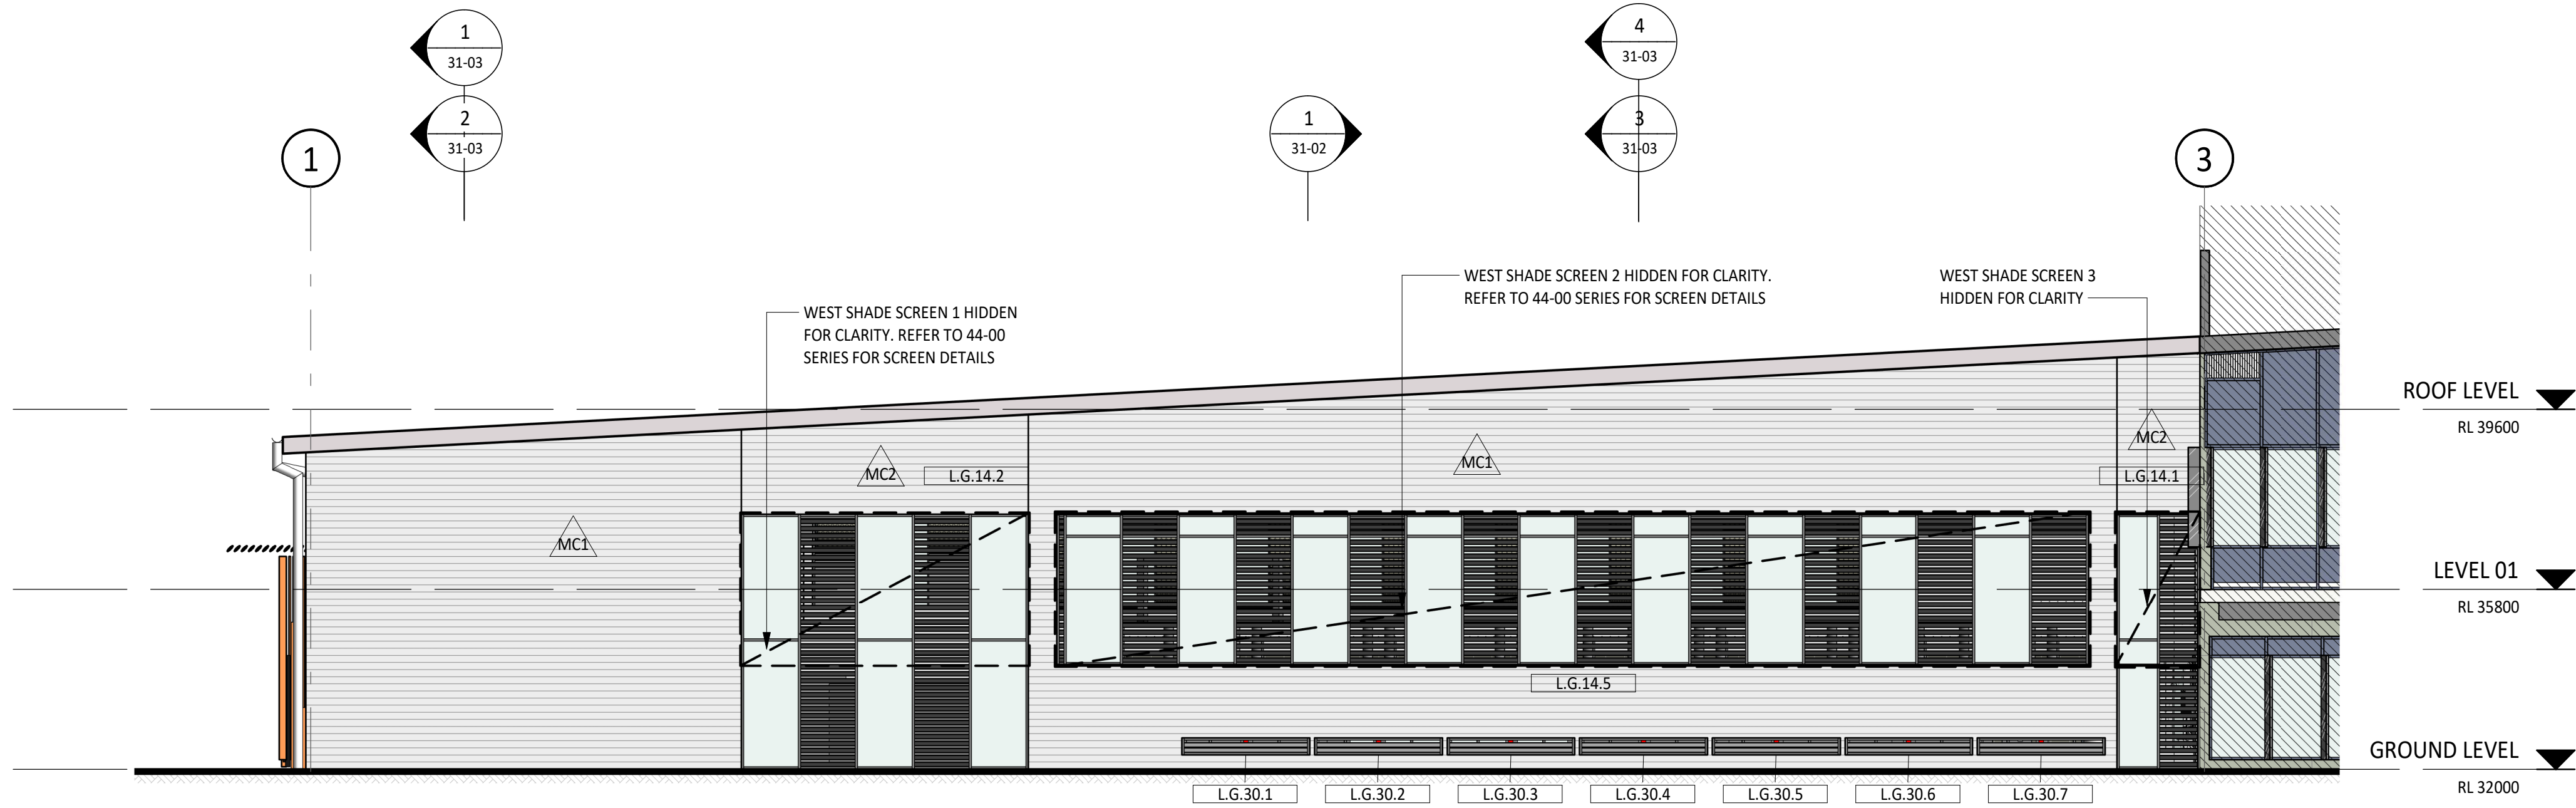

1 BUILDING ELEVATION - WEST - 1
21-00 1 : 100

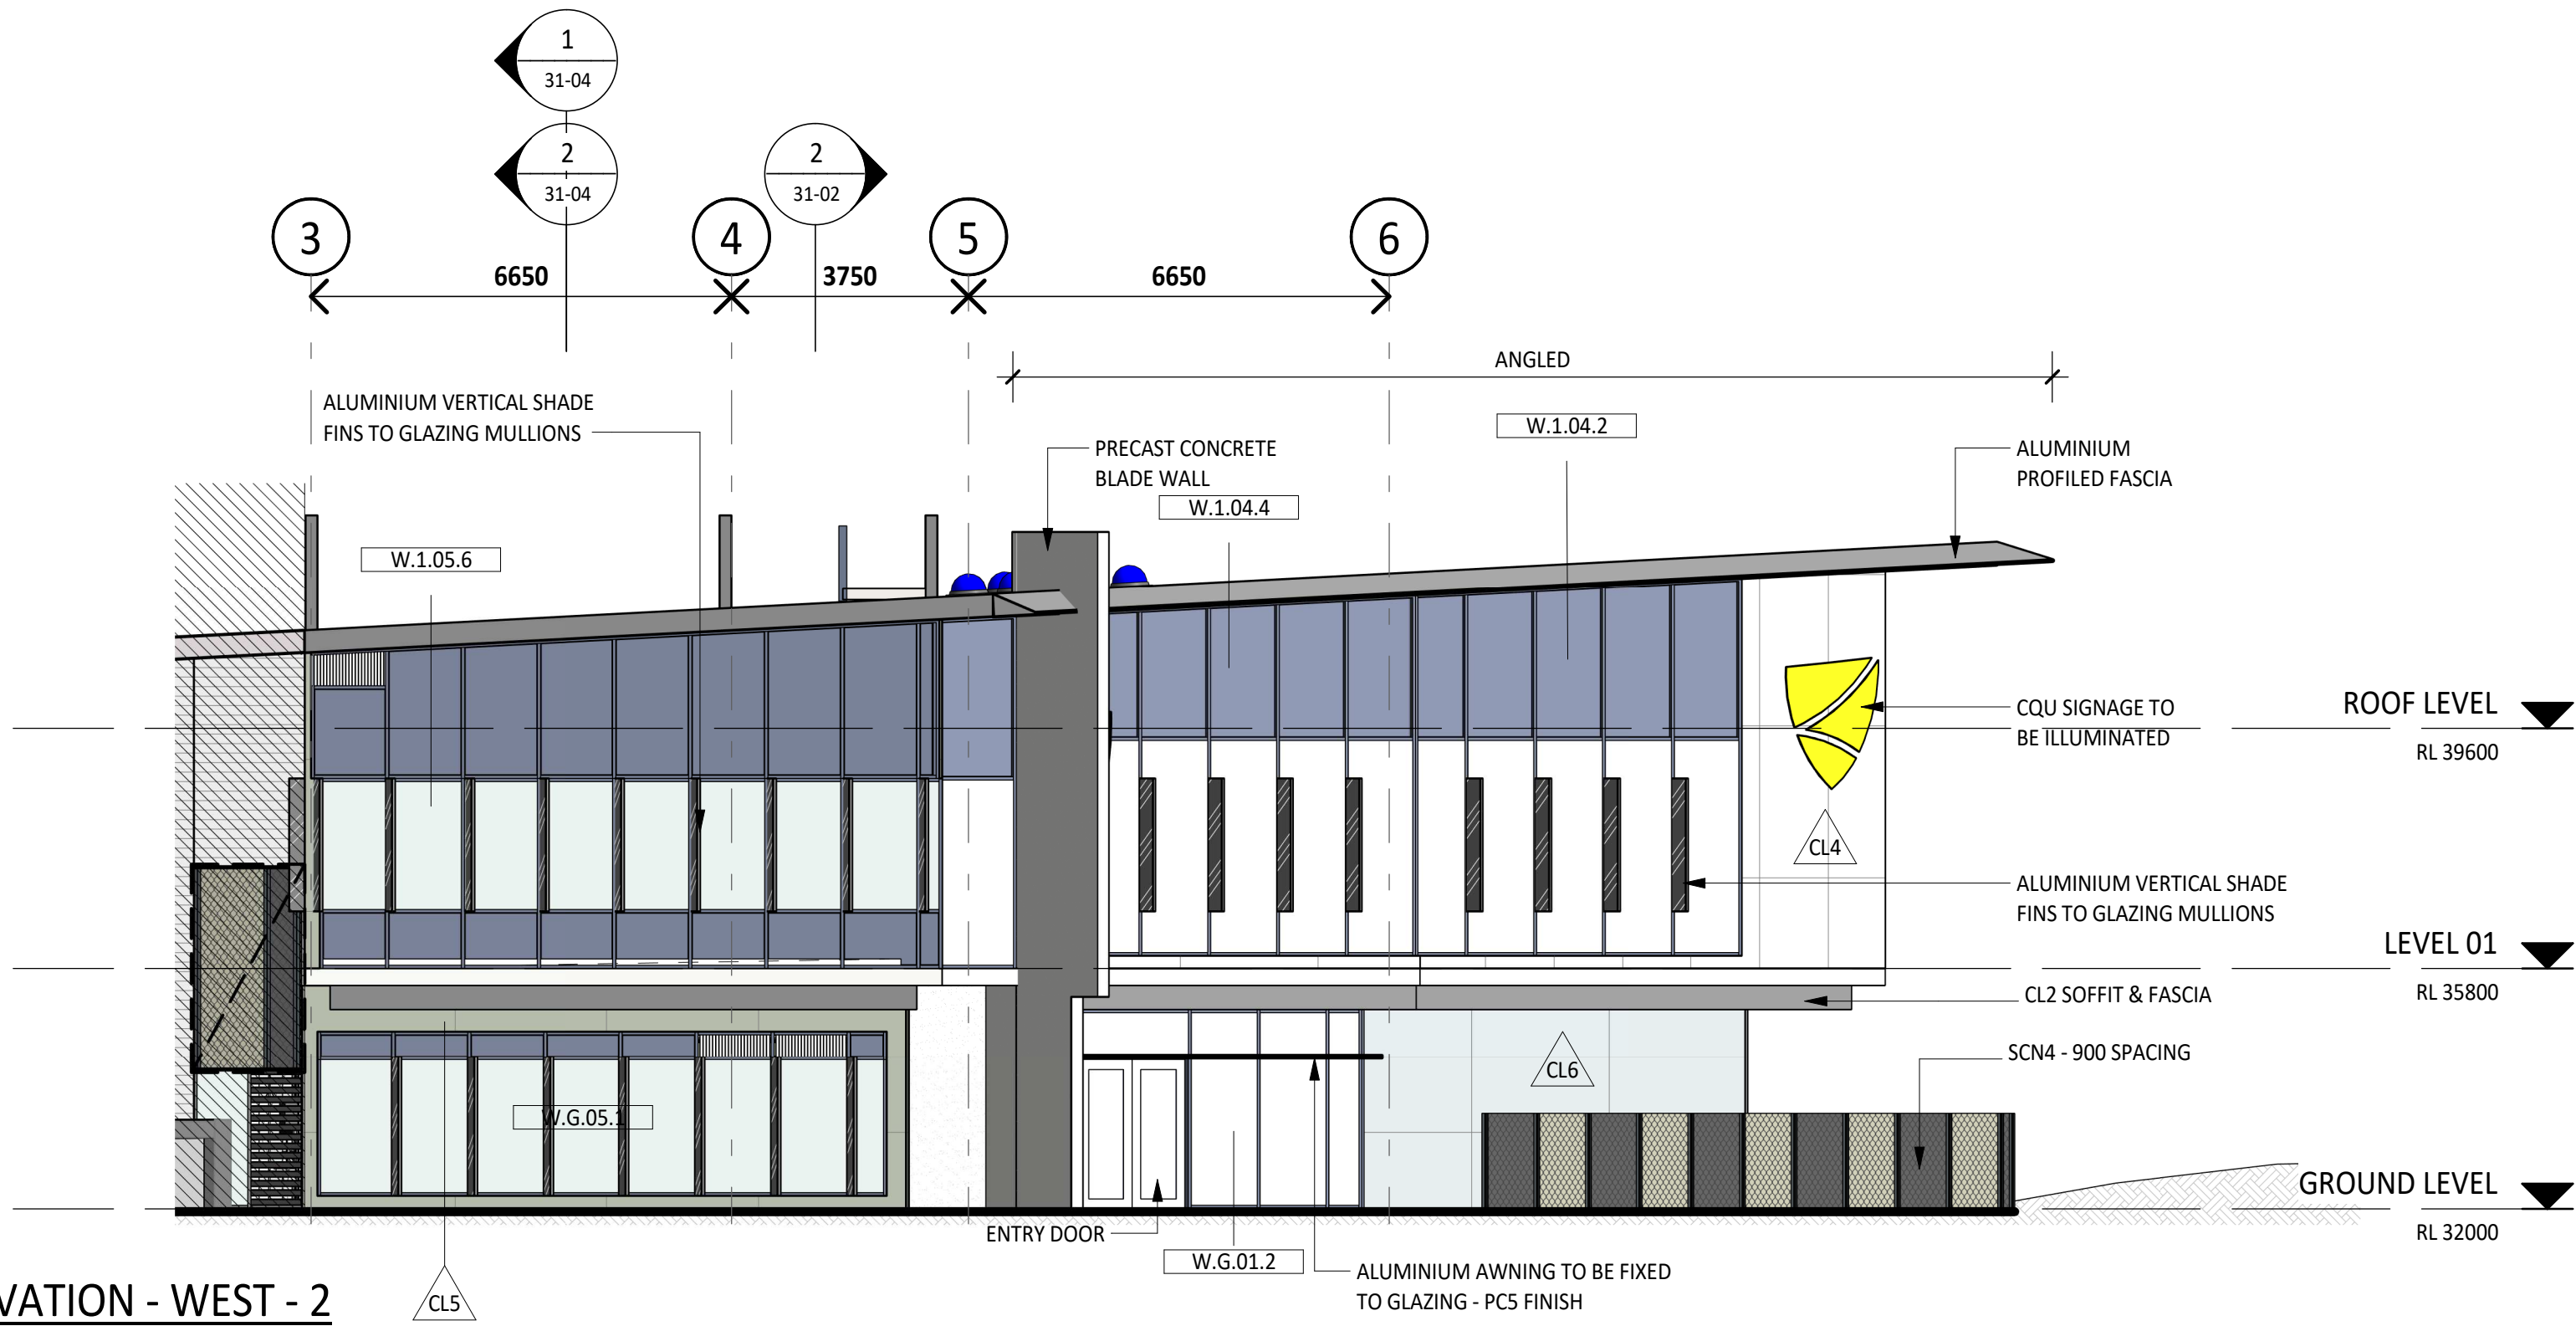

2 BUILDING ELEVATION - WEST - 2
21-00 1 : 100

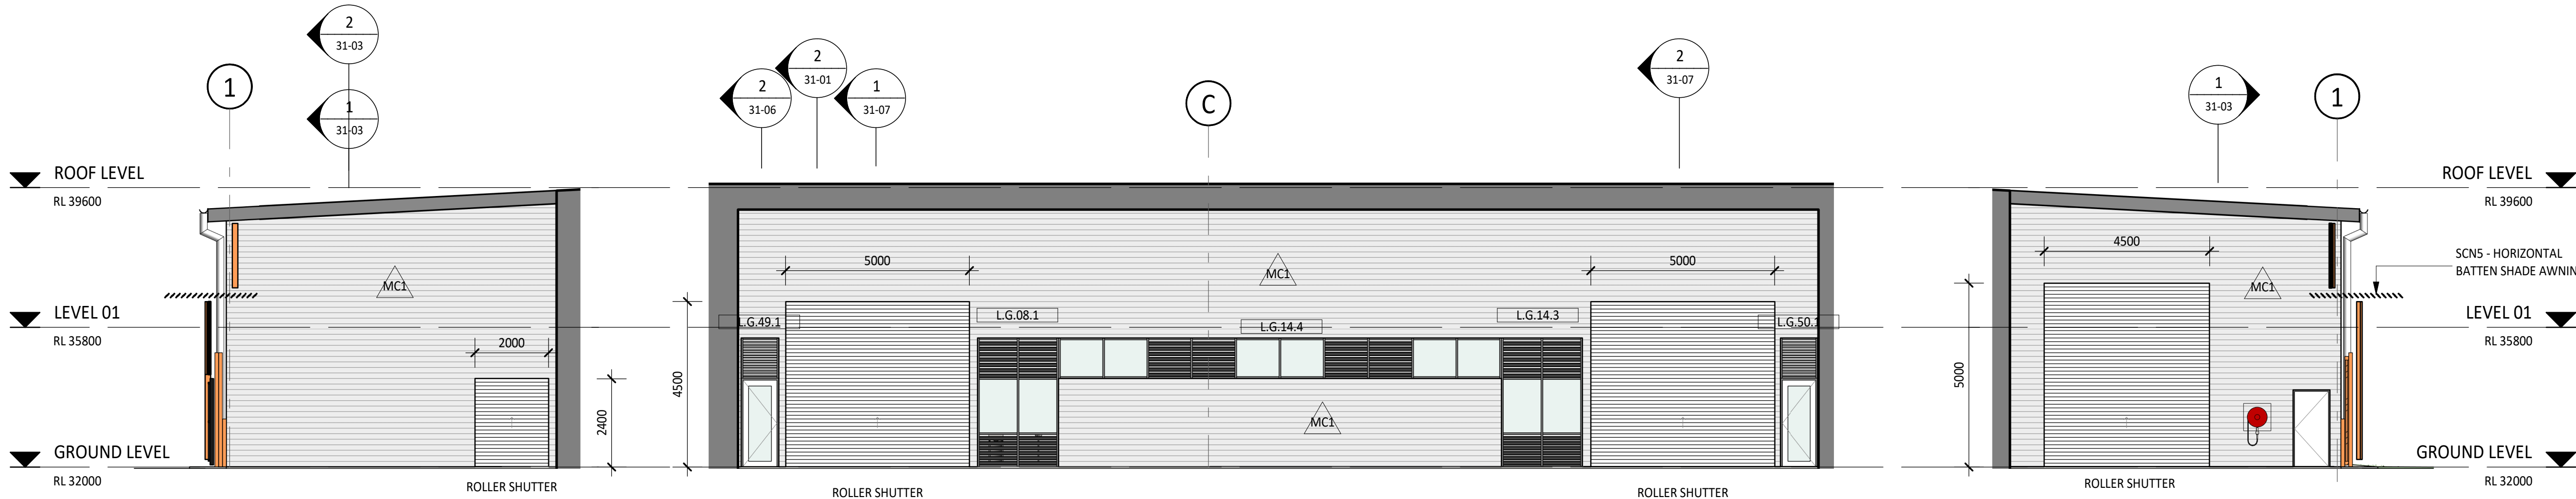

5 EXTERNAL HARDSTAND WEST ELEVATION
21-00 1 : 100

4 EXTERNAL HARDSTAND NORTH ELEVATION
21-00 1 : 100

3 EXTERNAL HARDSTAND EAST ELEVATION
21-00 1 : 100

EXTERNAL FINISHES SCHEDULE

CL1 - COMPRESSED FIBRE CEMENT CLADDING - CONCRETE LOOK
CL2 - SOLID ALUMINIUM CLADDING - BRUSHED ALUMINIUM
CL3 - NOT USED ON NEW TRADES BUILDING
CL4 - THROUGH COLOURED FIBRE CEMENT CLADDING - LINEN
CL5 - THROUGH COLOURED FIBRE CEMENT CLADDING - ASH GREY
CL6 - THROUGH COLOURED FIBRE CEMENT CLADDING - LIGHT SLATE
MC1 - PRE-FINISHED METAL PROFILE SHEET CLADDING - CORRUGATED ZINCALUME
MC2 - PRE-FINISHED METAL PROFILE SHEET CLADDING - CORRUGATED ZINCALUME - MINI PROFILE
MC3 - PRE-FINISHED METAL PROFILE SHEET CLADDING - STANDING SEAM - COLORBOND DEEP OCEAN
BST1 - ALUMINIUM BATTEN SCREEN - 3X BATTEN PROFILES - REFER PLAN FOR SET OUT DETAILS
DP - DOWNPIPE - REFER TO SPECIFICATION FOR SIZE & FINISHES

BUILDING ELEVATION NOTES

FINISHES TAG

- CLADDING CL4, CL5, AND CL6 HAS A NON TYPICAL PANEL BREAK UP. REFER TO DETAIL ELEVATION FOR SET OUT
- SHADE SCREENS HIDDEN FOR CLARITY. REFER TO GENERAL ARRANGEMENT ELEVATIONS FOR EXTENT, AND SCREEN DETAILS ON 44-00 SERIES

PLANS TO BE PRINTED IN COLOUR

CQU ROCKHAMPTON TAFE CONSOLIDATION - STAGE 2

554/700 Yaamba Rd, Norman
Gardens QLD 4701

B	05/03/26	ISSUED FOR TENDER	BS
A	12/02/26	ISSUED FOR TENDER	BS
1	30/01/26	DRAFT 60% ISSUE	BS

rev	date	details	init.
-----	------	---------	-------

drawn	date
PT	30/01/26
checked	date
BS	30/01/26
verified	date
BS	30/01/26

scale

BUILDING ELEVATIONS - WEST

scale
1 : 100 @ A1

project no.
260018

revision
B

sheet no.
CQU-ROK-092-00-ARC-30-13

ISSUED FOR TENDER