

**CQU ROCKHAMPTON
TAFE
CONSOLIDATION -
STAGE 2**

554/700 Yaamba Rd, Norman
Gardens QLD 4701



A	12/02/26	ISSUED FOR TENDER	BS
2	30/01/26	DRAFT 60% ISSUE	BS
1	24/11/25	50% COSTING ISSUE	BS


rev	date	details	init.
-----	------	---------	-------

drawn	date
PT	21/11/25
checked	date
BS	21/11/25
verified	date
BS	21/11/25


scale

GA SECTIONS SHEET 1

scale	project no.
1 : 200 @ A1	260018
revision	
A	
sheet no.	
CQU-ROK-092-00-ARC-31-01	

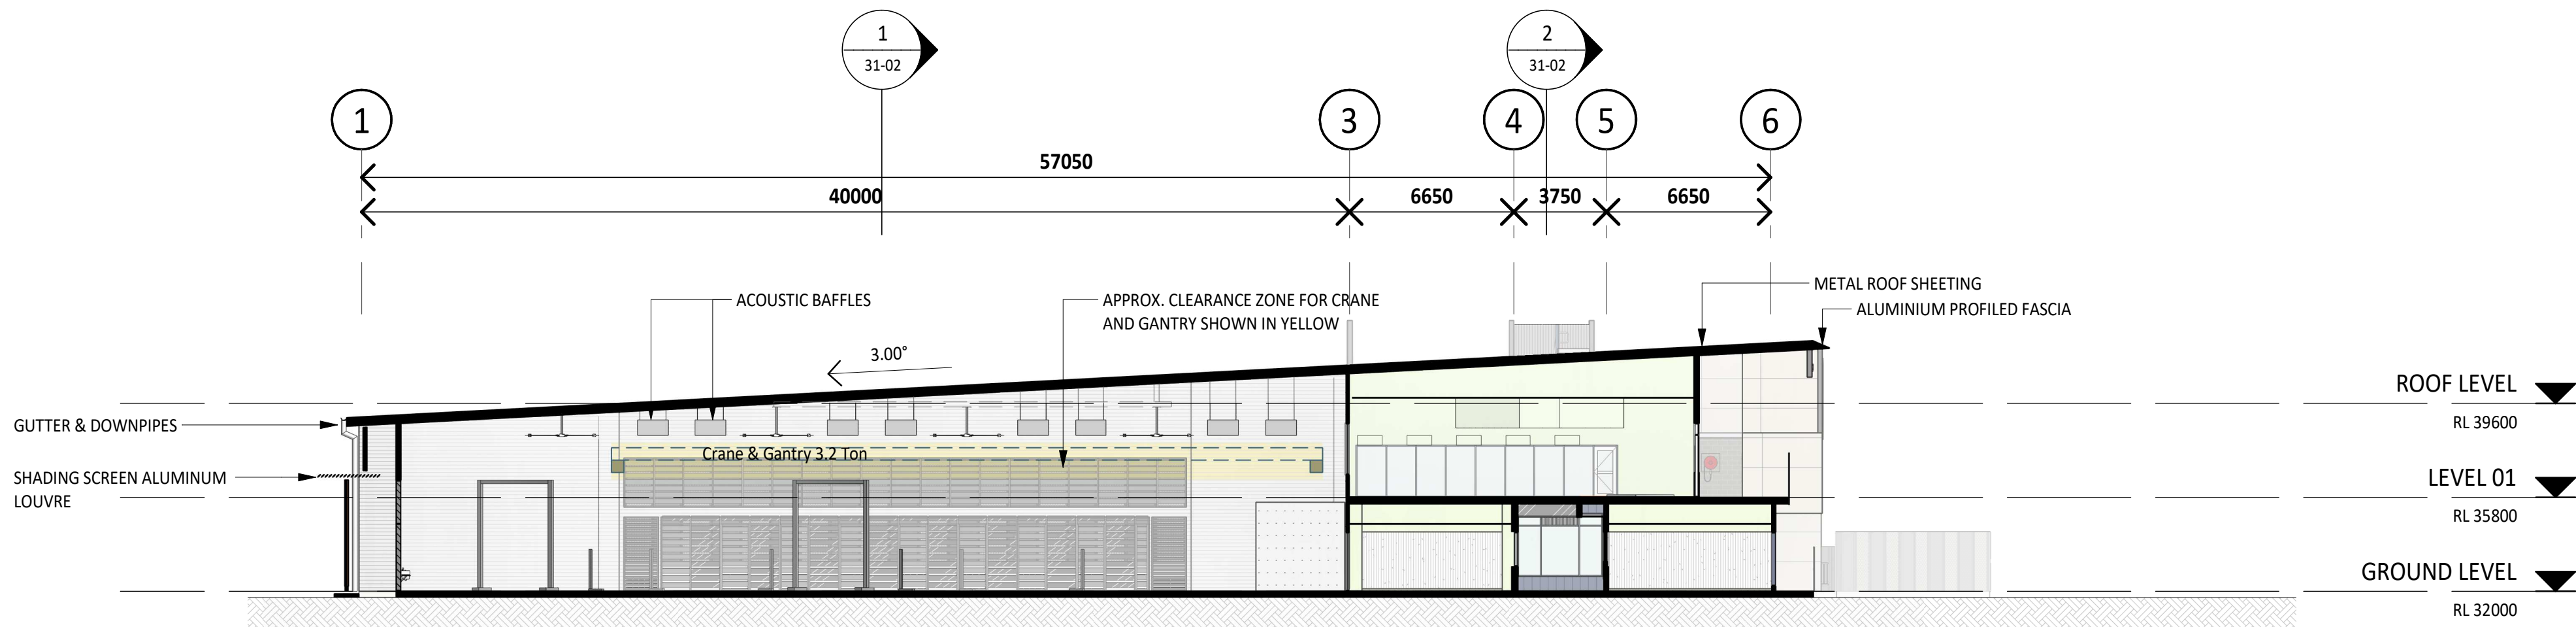

1
21-01
GA SECTION 01
1 : 200

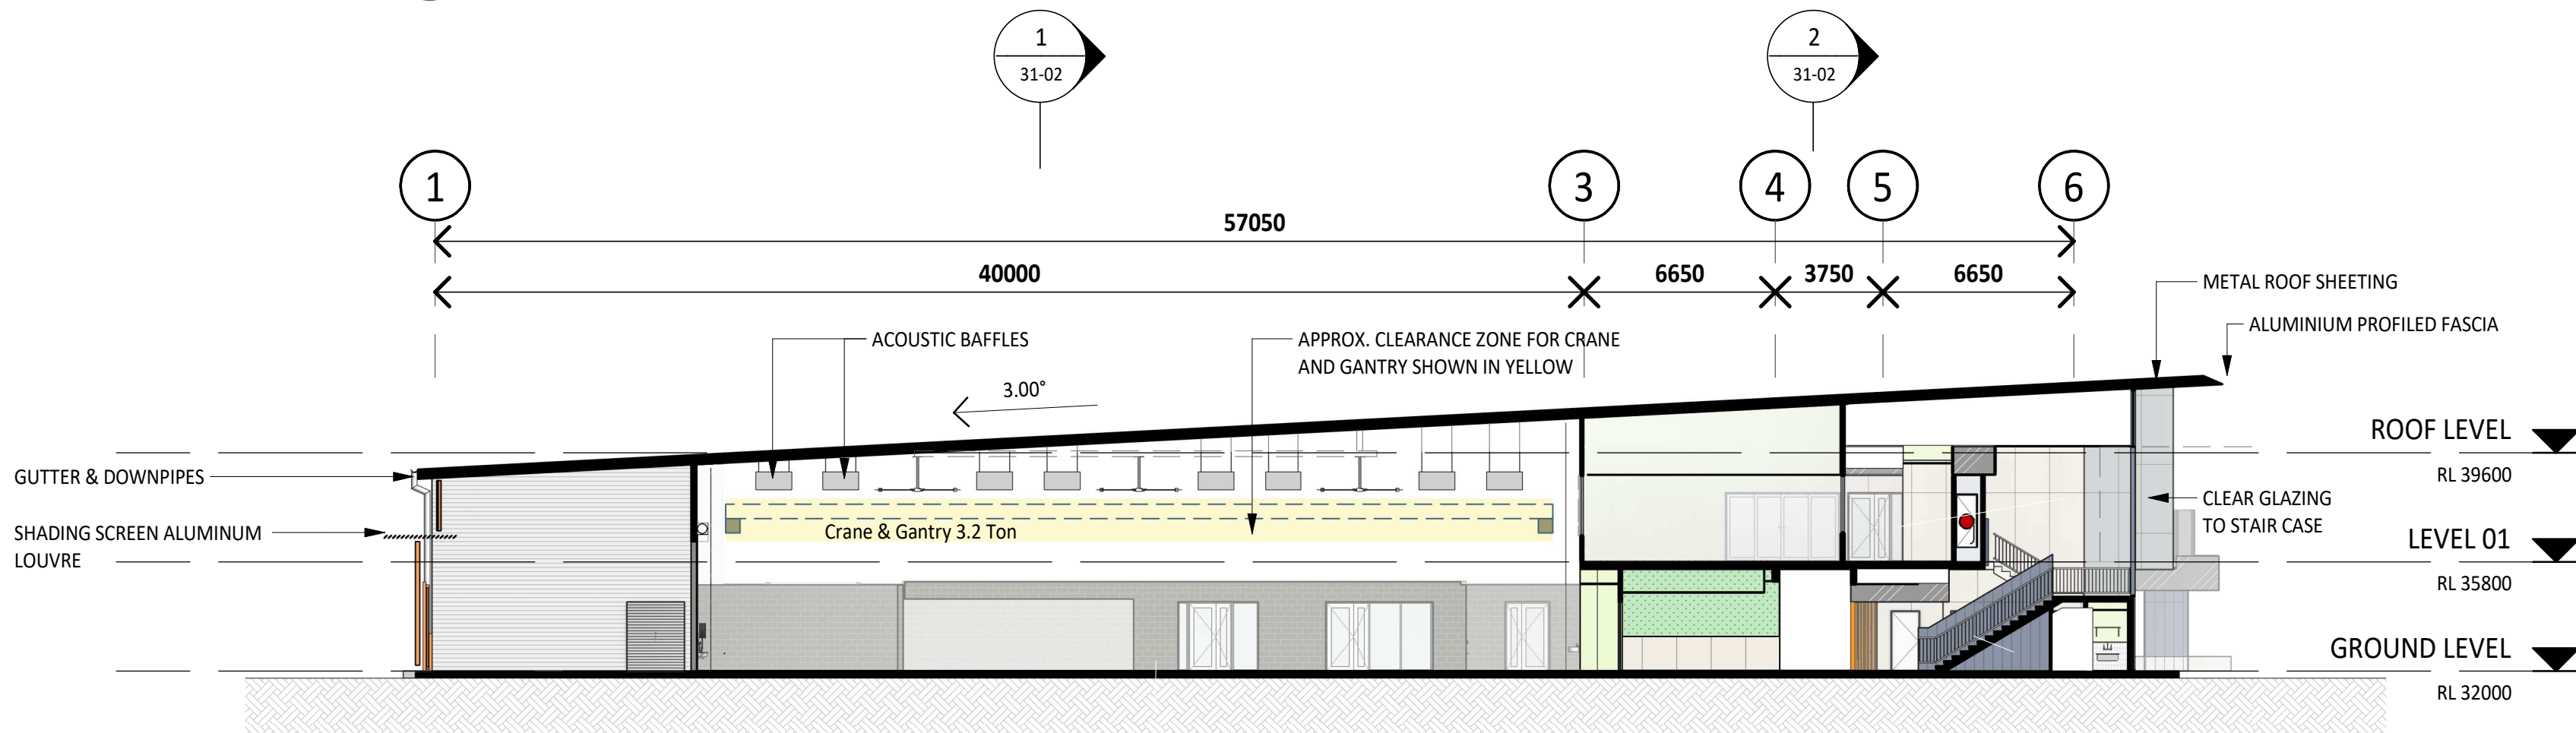

2
21-02
GA SECTION 02
1 : 200

ISSUED FOR TENDER