



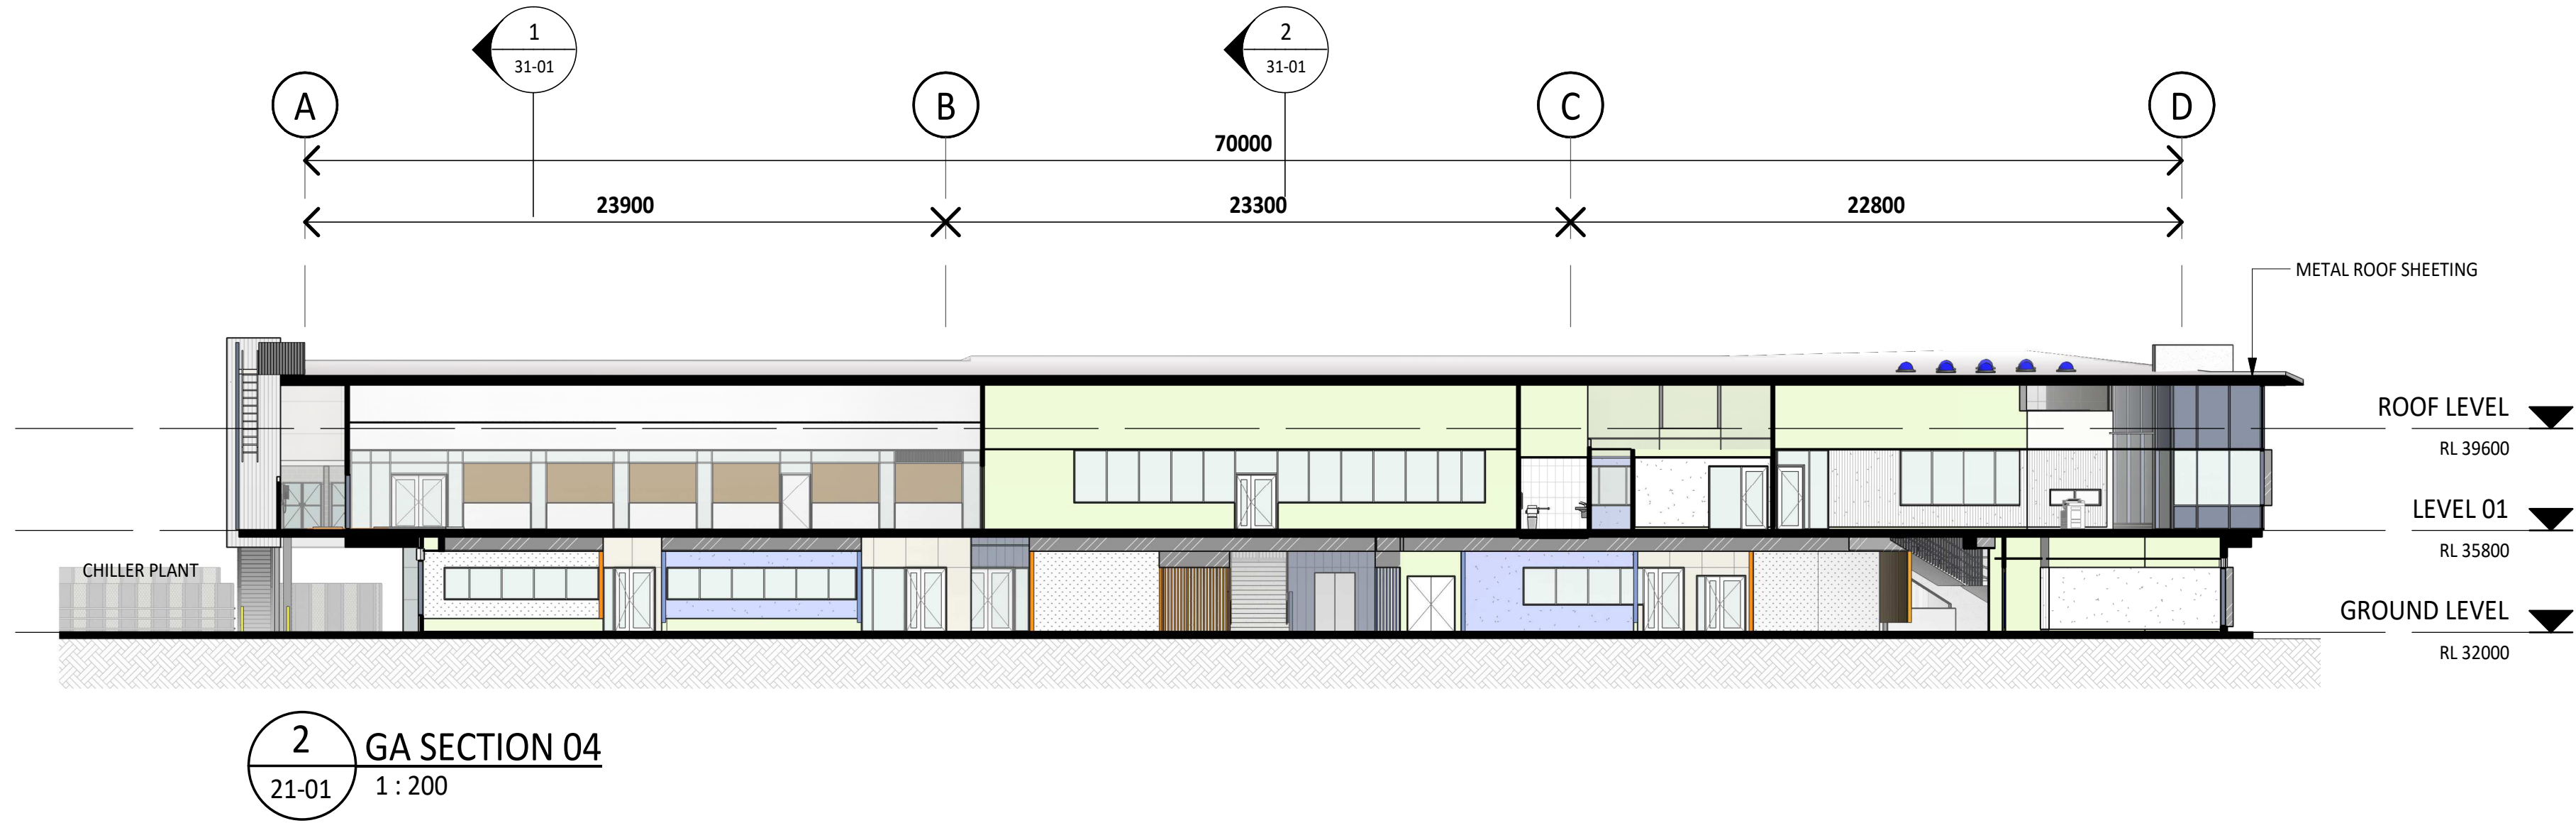

**CQU ROCKHAMPTON
TAFE
CONSOLIDATION -
STAGE 2**

554/700 Yaamba Rd, Norman
Gardens QLD 4701

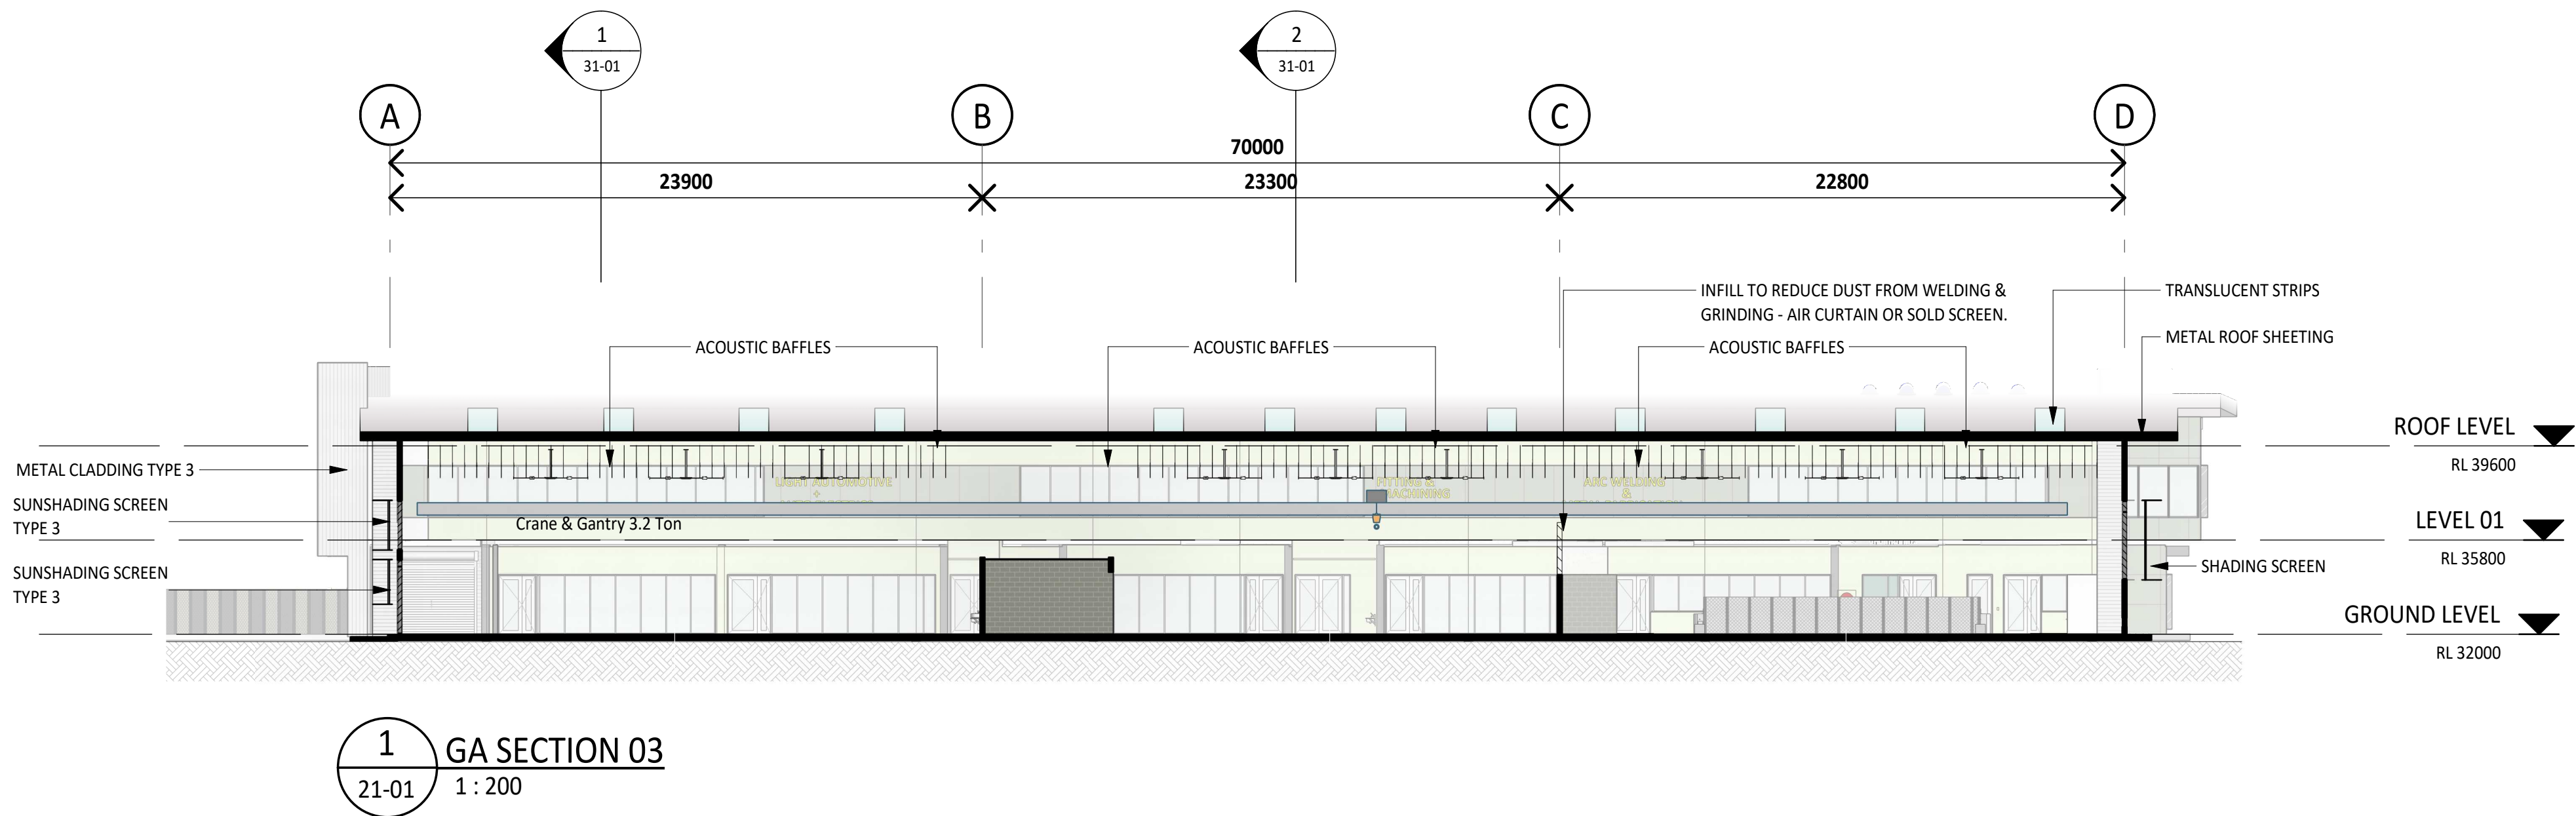

A	12/02/26	ISSUED FOR TENDER	BS
2	30/01/26	DRAFT 60% ISSUE	BS
1	24/11/25	50% COSTING ISSUE	BS
rev	date	details	init.

drawn	date
PT	21/11/26
checked	date
BS	21/11/26
verified	date
BS	21/11/26

scale

GA SECTIONS SHEET 2

scale
1 : 200 @ A1
revision
A
sheet no.
CQU-ROK-092-00-ARC-31-02

project no.
260018

ISSUED FOR TENDER