

**CQU ROCKHAMPTON
TAFE
CONSOLIDATION -
STAGE 2**

554/700 Yaamba Rd, Norman
Gardens QLD 4701



B	05/03/26	ISSUED FOR TENDER	BS
A	12/02/26	ISSUED FOR TENDER	BS
1	30/01/26	DRAFT 60% ISSUE	BS
rev\	date	details	init.

drawn	date
PT	30/01/26
checked	date
BS	30/01/26
verified	date
BS	30/01/26

scale


**BUILDING SECTIONS -
SHEET 1**

scale
1 : 100 @ A1

project no.
260018

revision
B

sheet no.
CQU-ROK-092-00-ARC-31-03

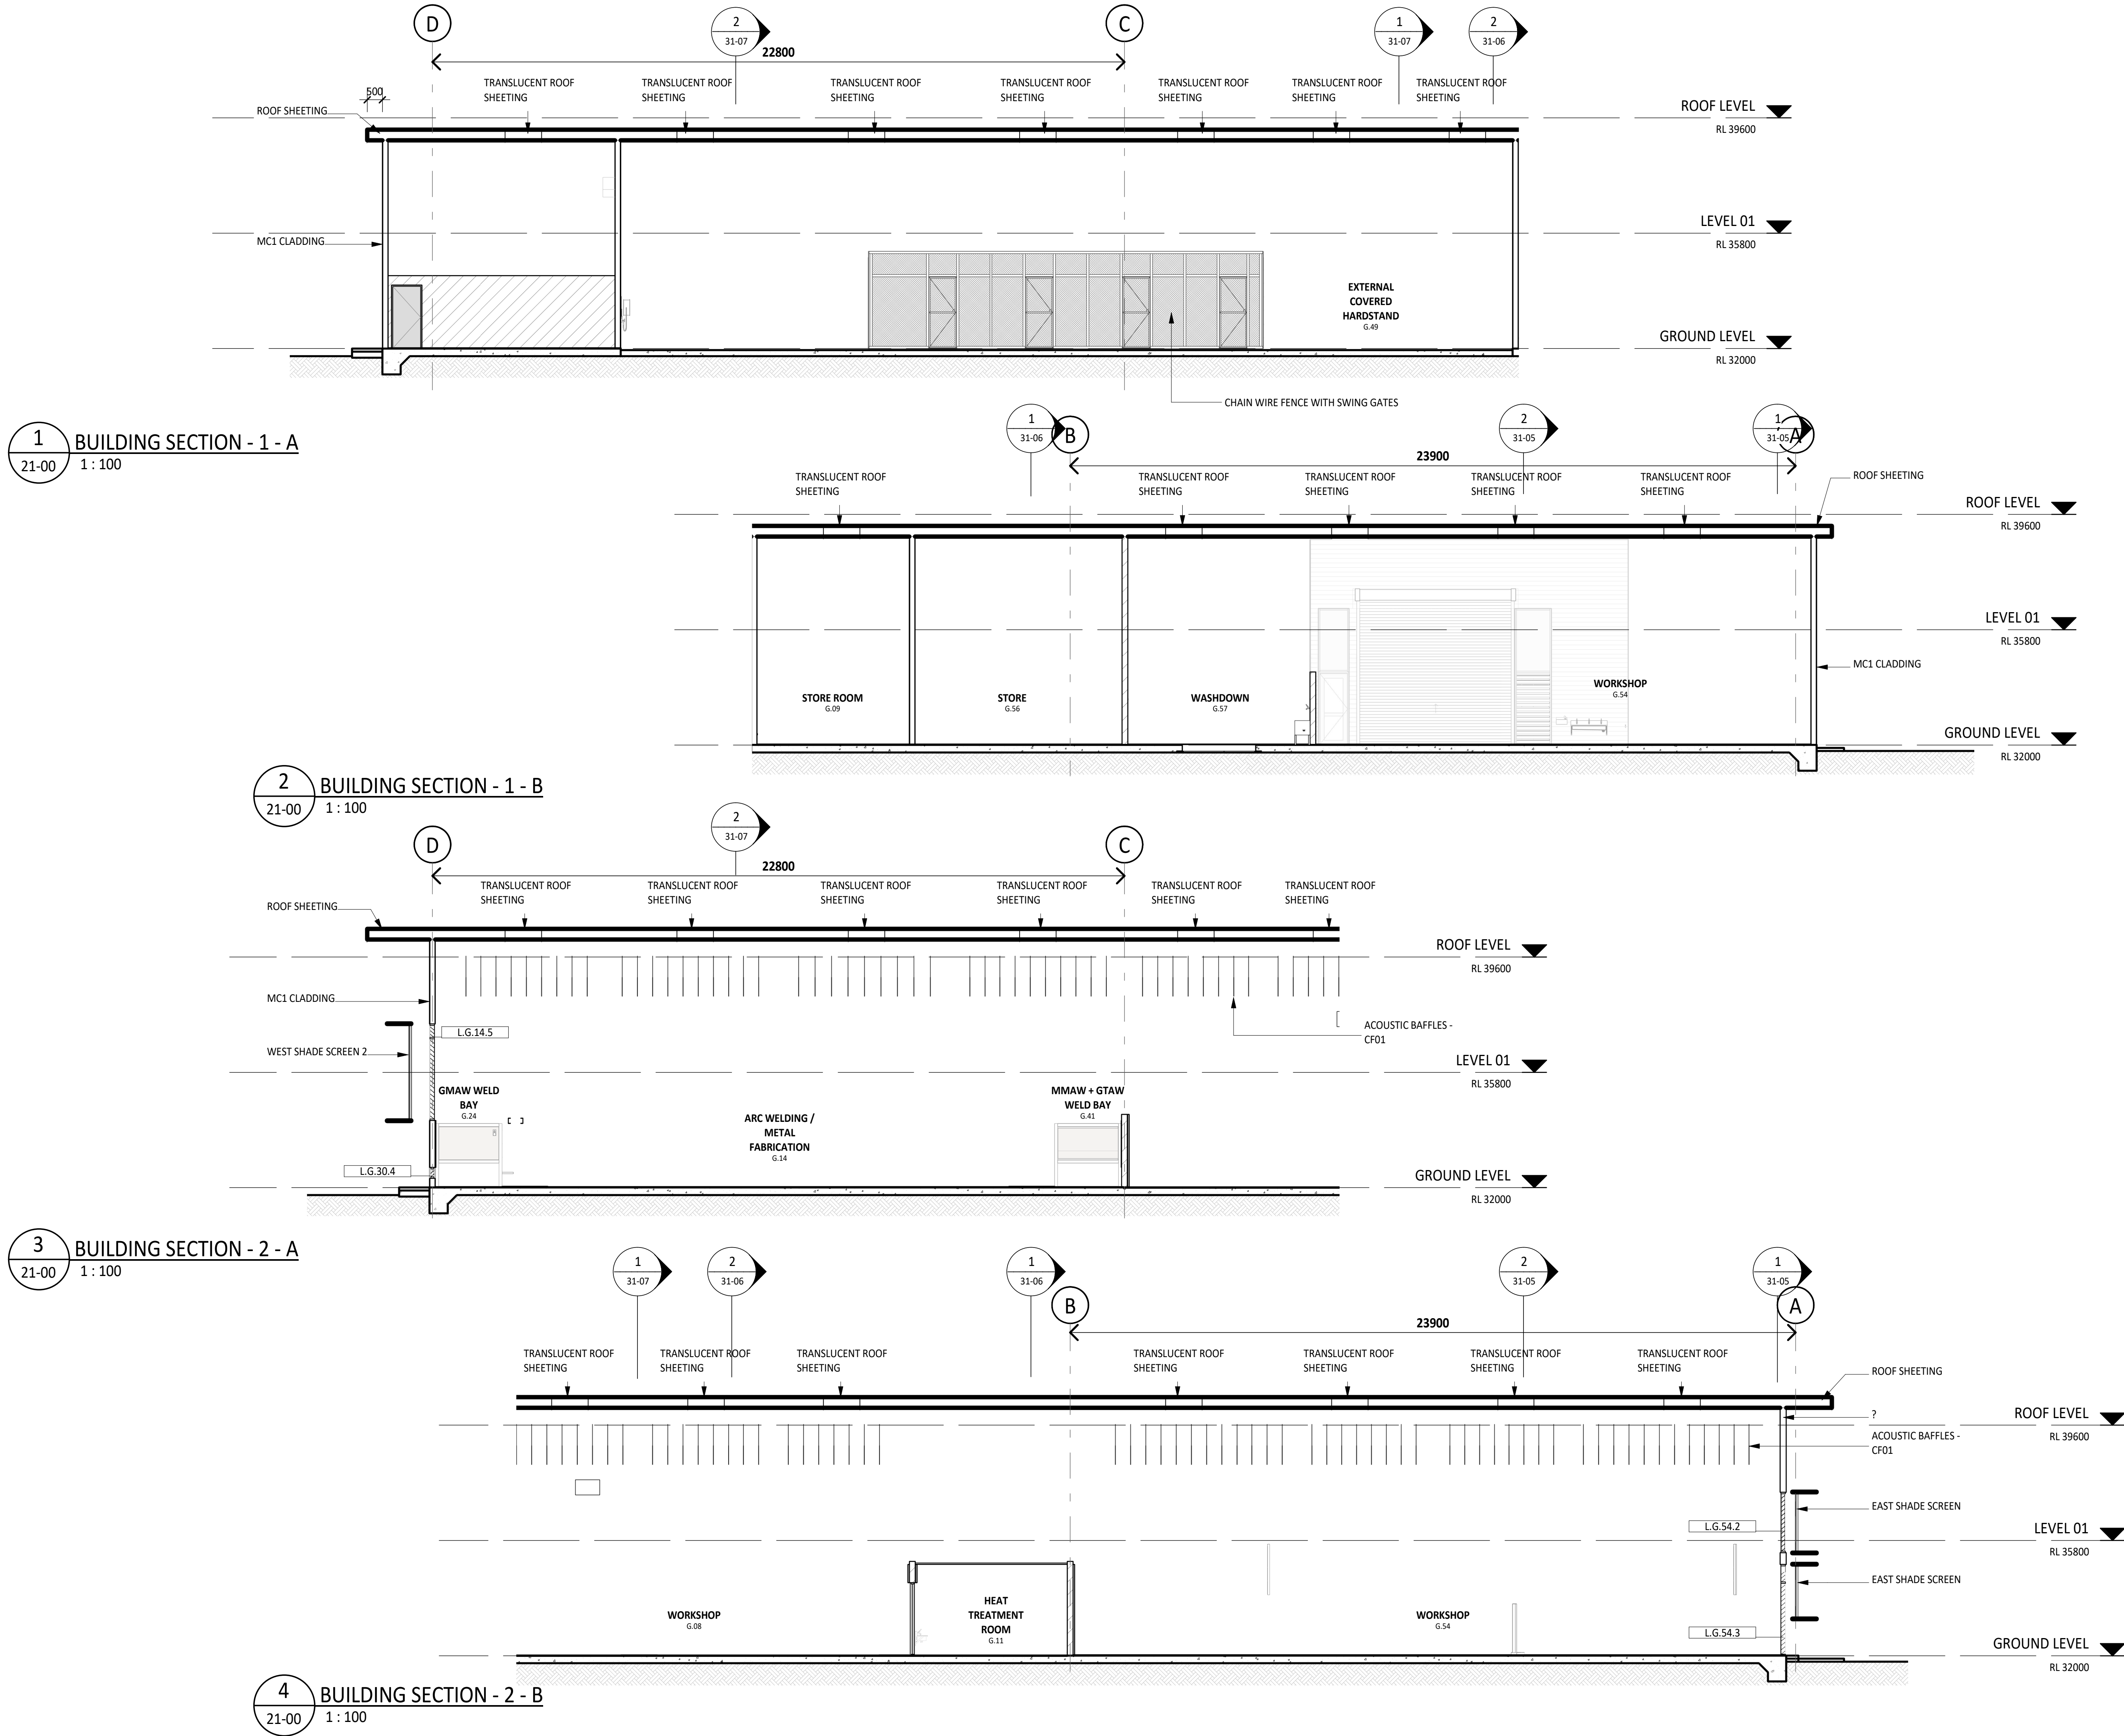

ISSUED FOR TENDER