

**CQU ROCKHAMPTON
TAFE
CONSOLIDATION -
STAGE 2**

554/700 Yaamba Rd, Norman
Gardens QLD 4701




B	05/03/26	ISSUED FOR TENDER	BS
A	12/02/26	ISSUED FOR TENDER	BS
1	30/01/26	DRAFT 60% ISSUE	BS
rev	date	details	init.

drawn	date
PT	30/01/26
checked	date
BS	30/01/26
verified	date
BS	30/01/26


scale

**BUILDING SECTIONS -
SHEET 3**


scale project no.
As indicated @ A1 260018
revision
B
sheet no.
CQU-ROK-092-00-ARC-31-05

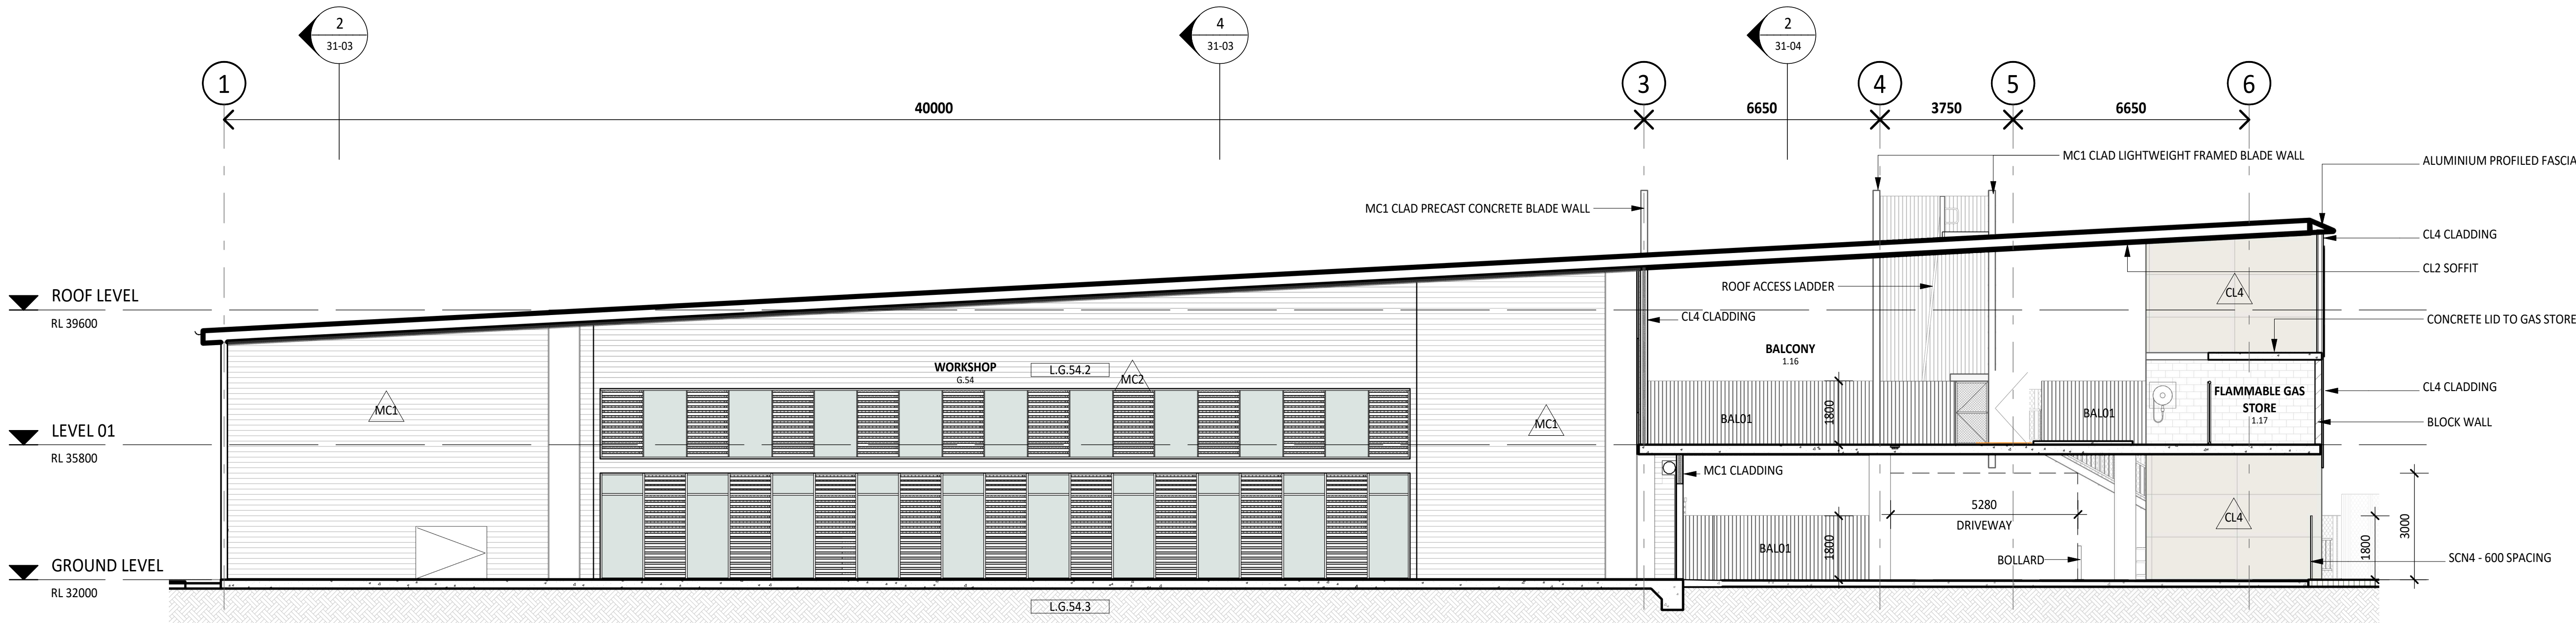

1 BUILDING SECTION - 4
21-01 1 : 100

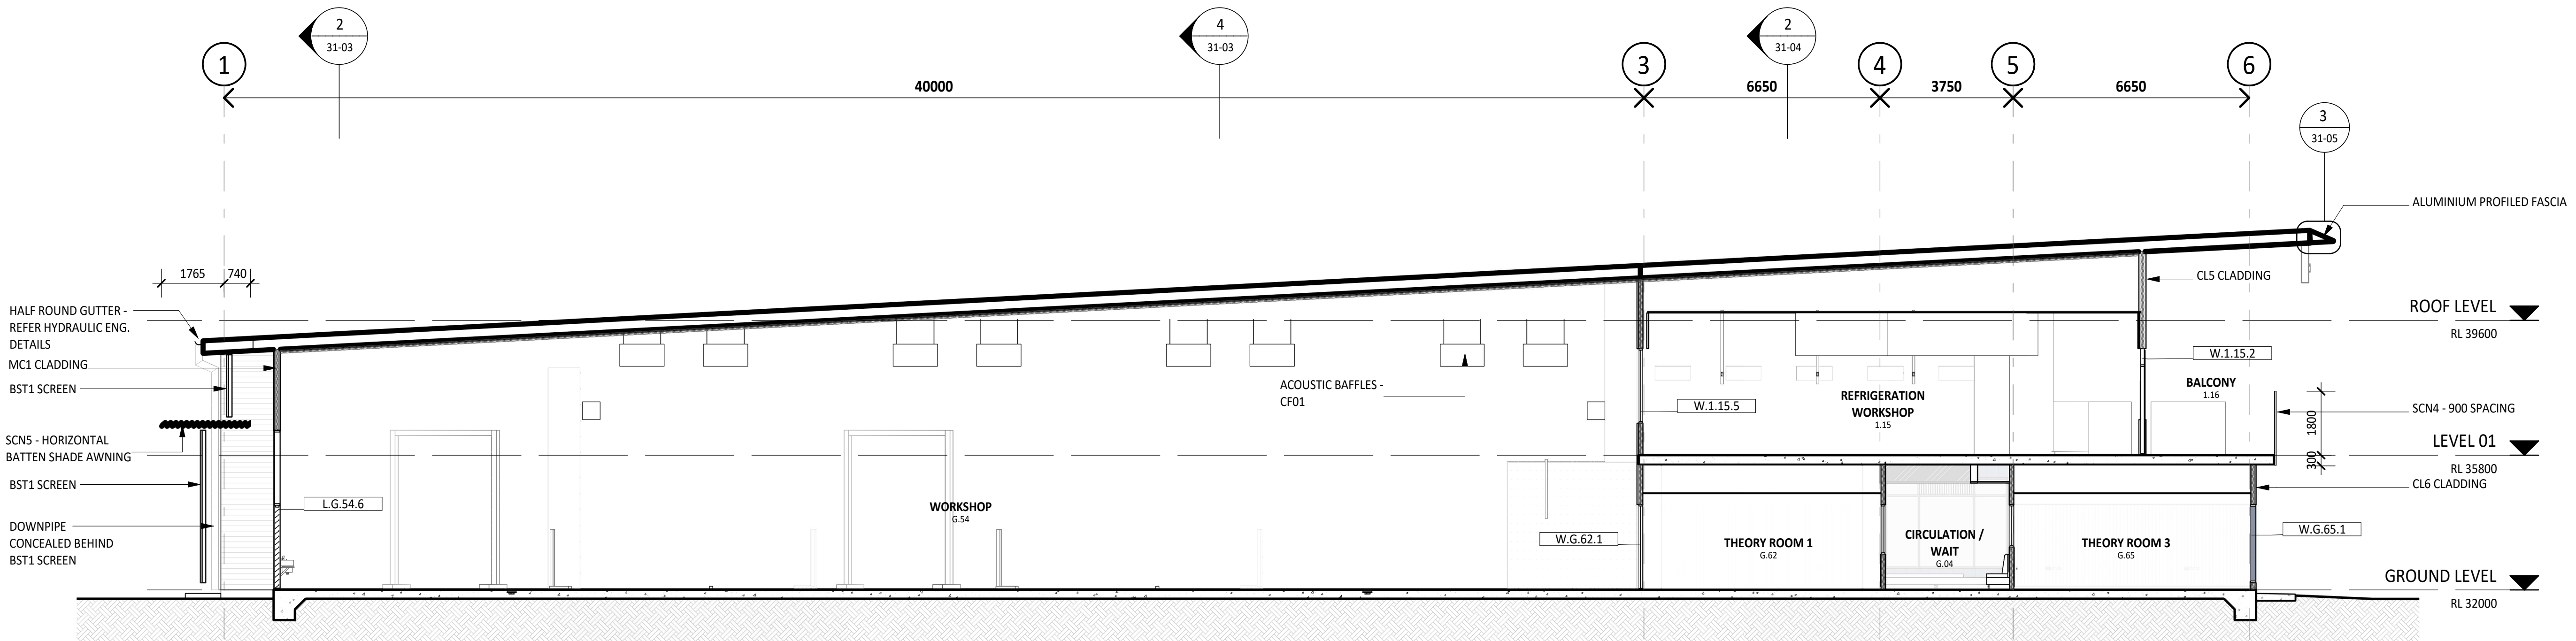

2 BUILDING SECTION - 5
21-01 1 : 100

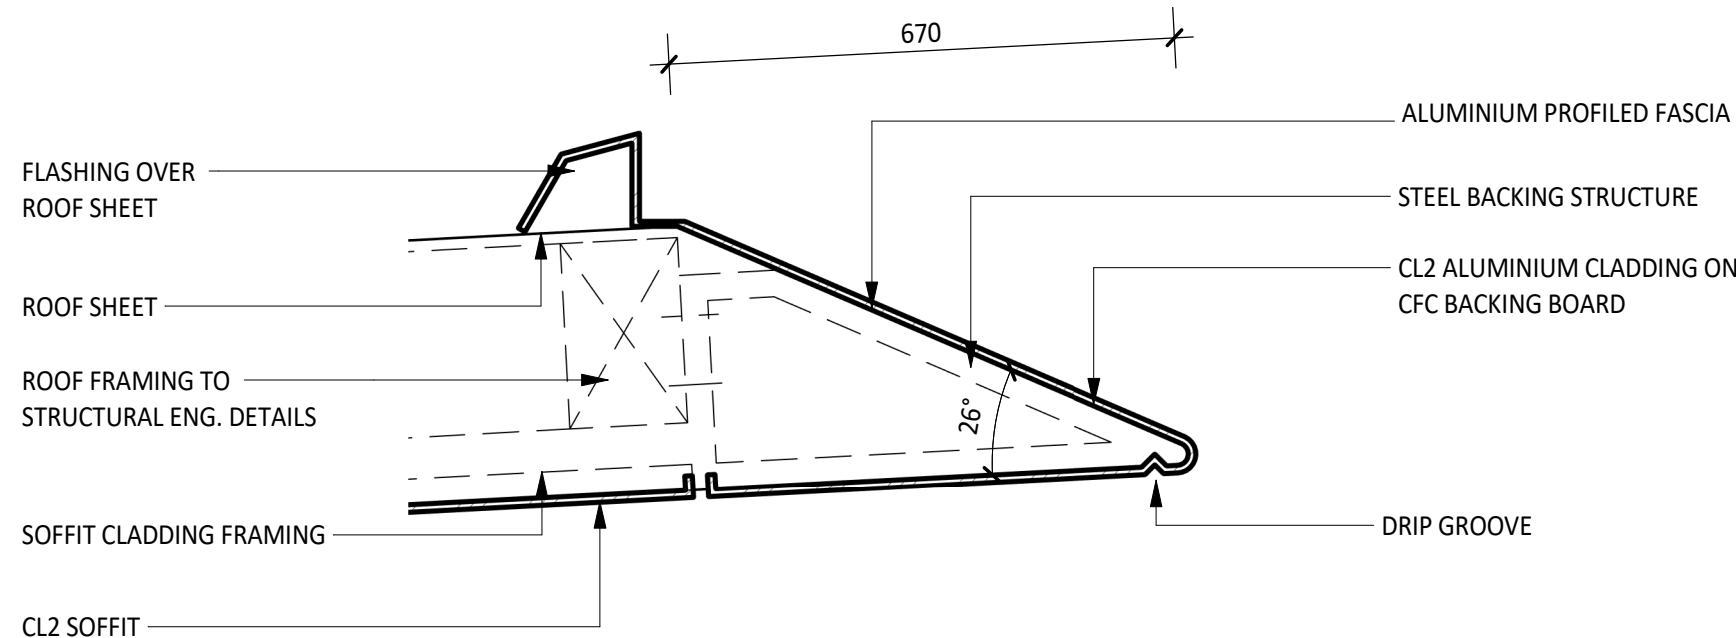

3 DETAIL - ALUMINIUM PROFILED FASCIA
31-05 1 : 10