

**CQU ROCKHAMPTON
TAFE
CONSOLIDATION -
STAGE 2**

554/700 Yaamba Rd, Norman
Gardens QLD 4701



A	12/02/26	ISSUED FOR TENDER	BS
1	30/01/26	DRAFT 60% ISSUE	BS
rev/	date	details	init.

drawn	date
PT	30/01/26
checked	date
use 'Approved By' only	30/01/26
verified	date
BS	30/01/26


scale

**BUILDING SECTIONS -
SHEET 4**


scale project no.
1 : 100 @ A1 260018

revision
A
sheet no.
CQU-ROK-092-00-ARC-31-06

ISSUED FOR TENDER

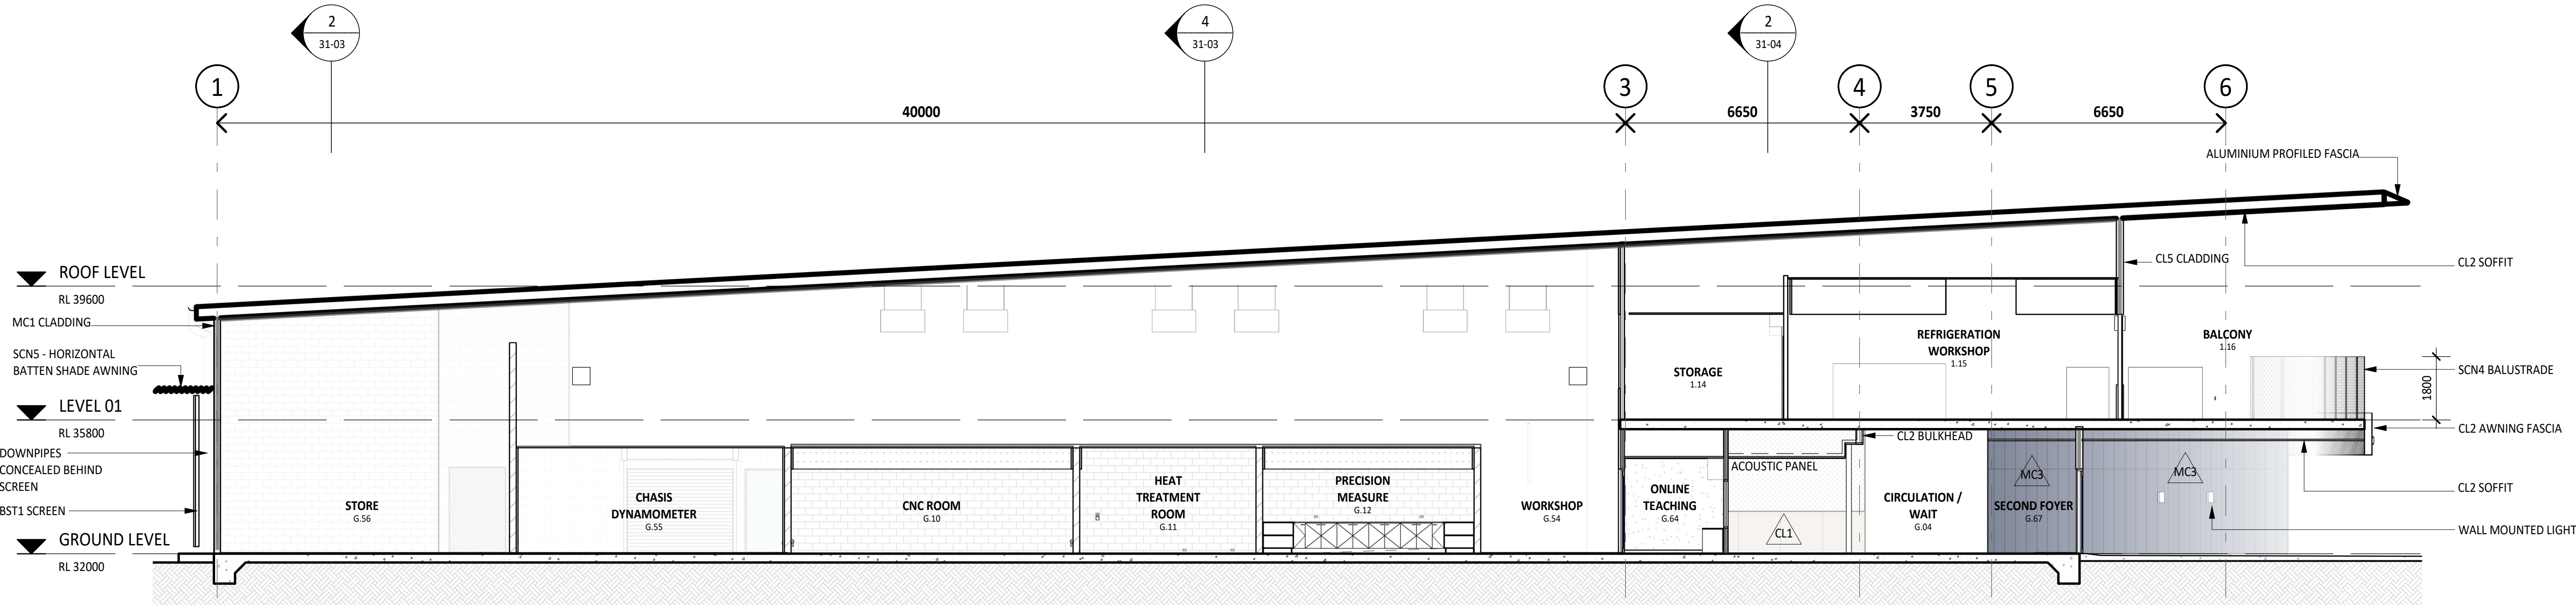

1 BUILDING SECTION - 6
21-01 1 : 100

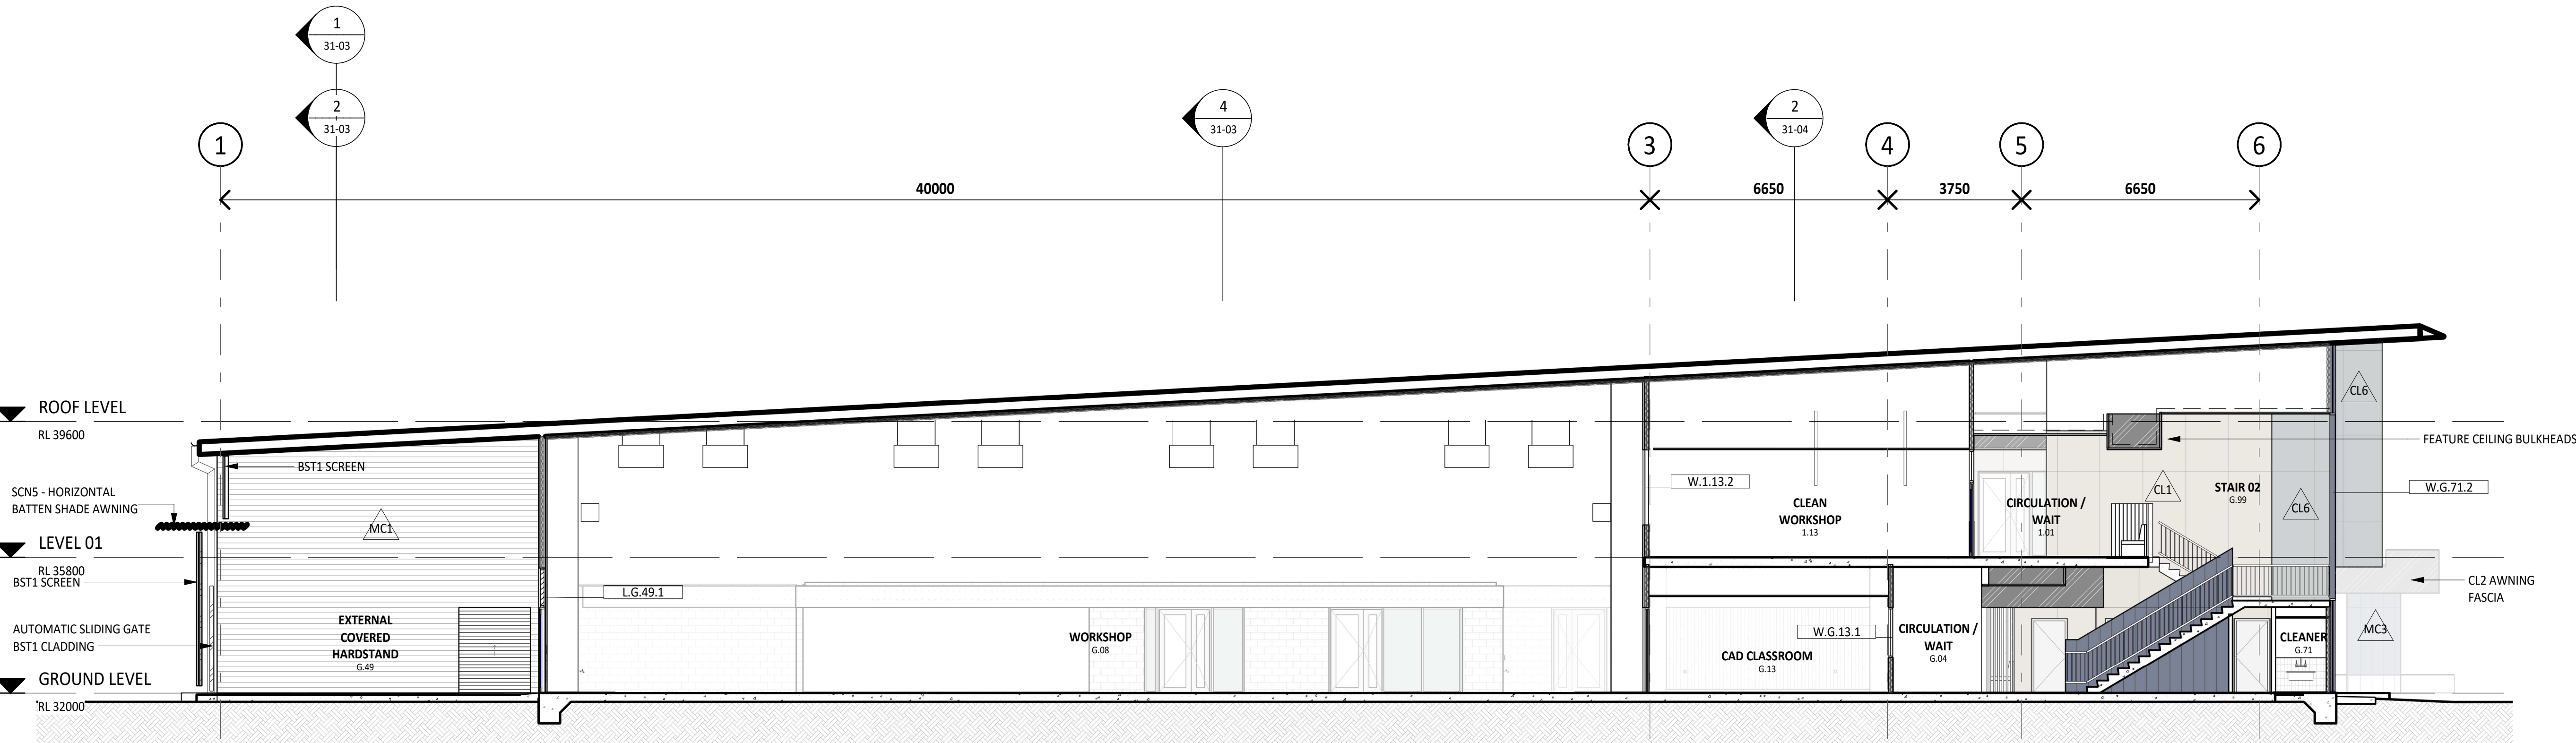

2 BUILDING SECTION - 7
21-02 1 : 100