

**CQU ROCKHAMPTON
TAFE
CONSOLIDATION -
STAGE 2**

554/700 Yaamba Rd, Norman
Gardens QLD 4701




A	12/02/26	ISSUED FOR TENDER	BS
1	30/01/26	DRAFT 60% ISSUE	BS
rev	date	details	init.

drawn	date
PT	30/01/26
checked	date
BS	30/01/26
verified	date
BS	30/01/26


scale

**BUILDING SECTIONS -
SHEET 6**


scale project no.
As indicated @ A1 260018
revision
A
sheet no.
CQU-ROK-092-00-ARC-31-08

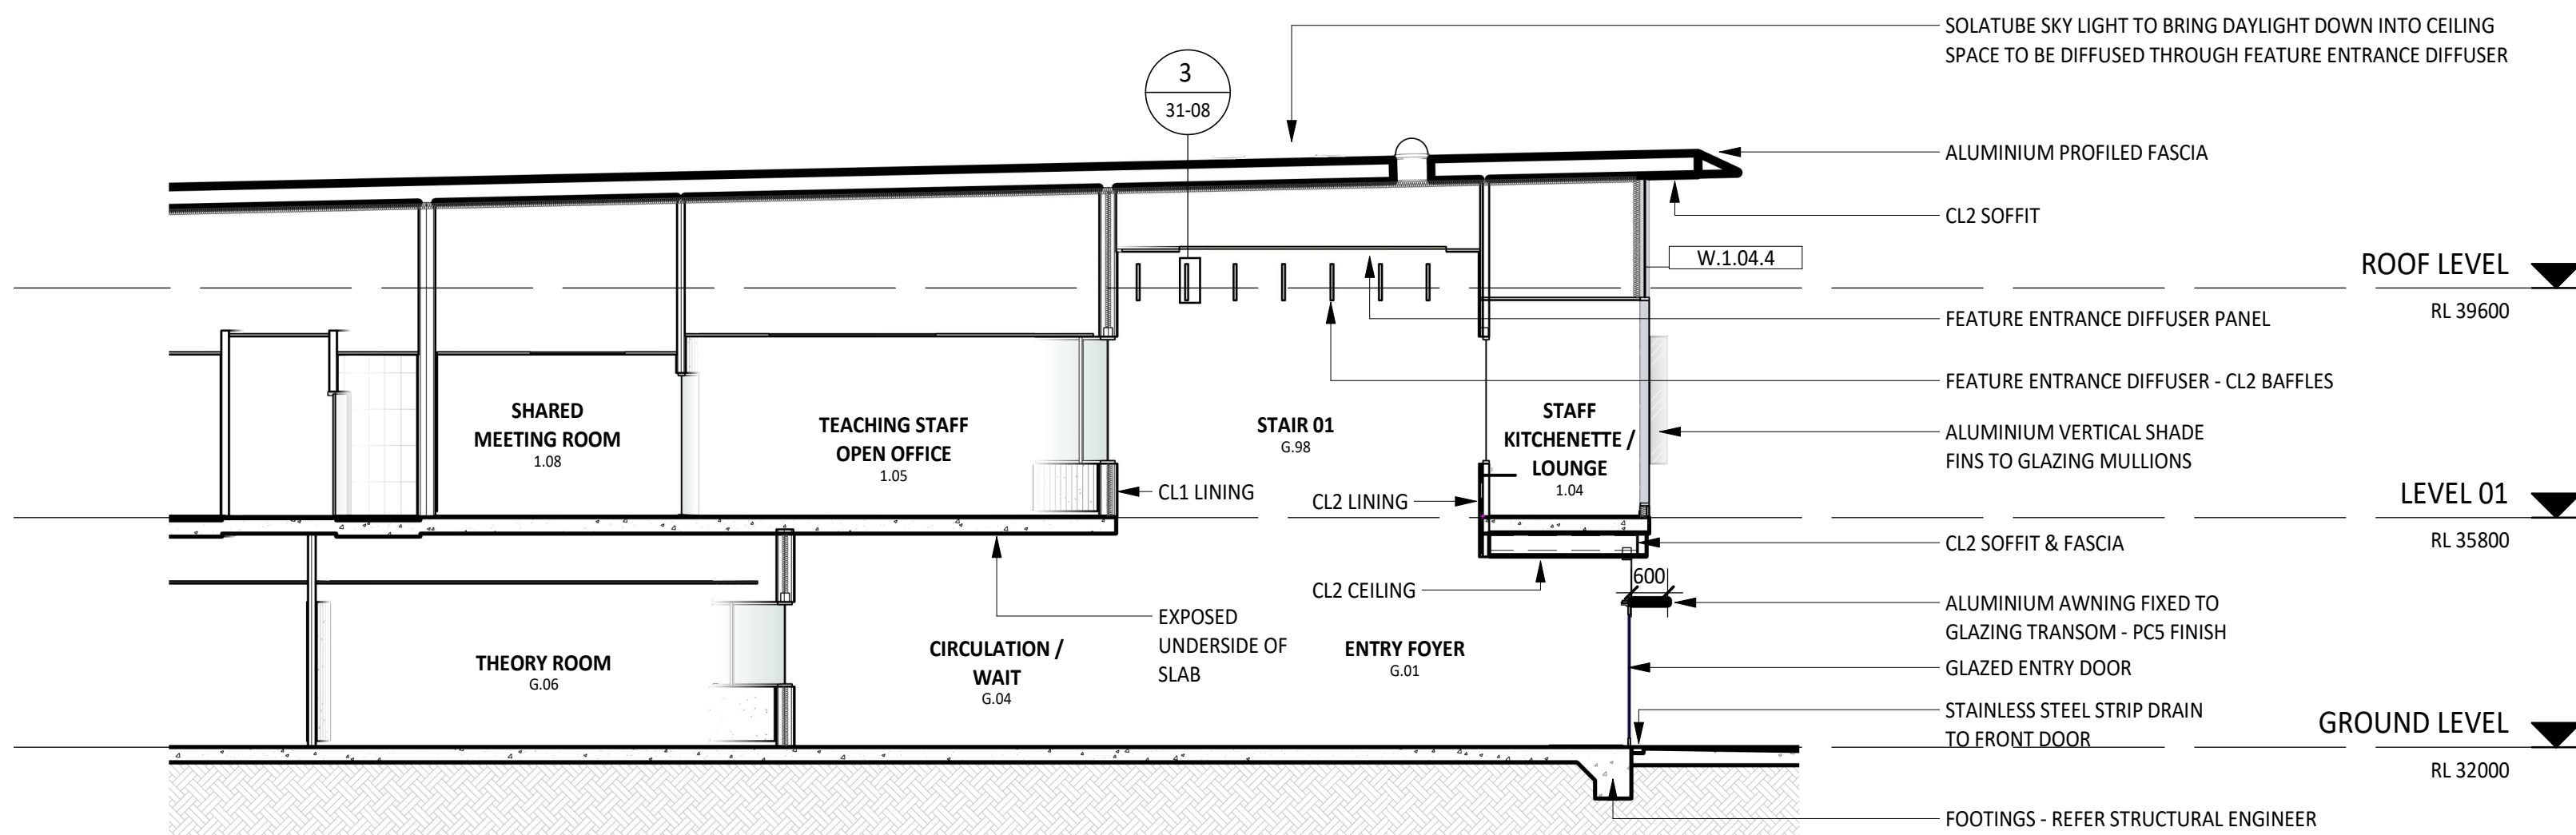

1
21-02
BUILDING SECTION - 10
1 : 100

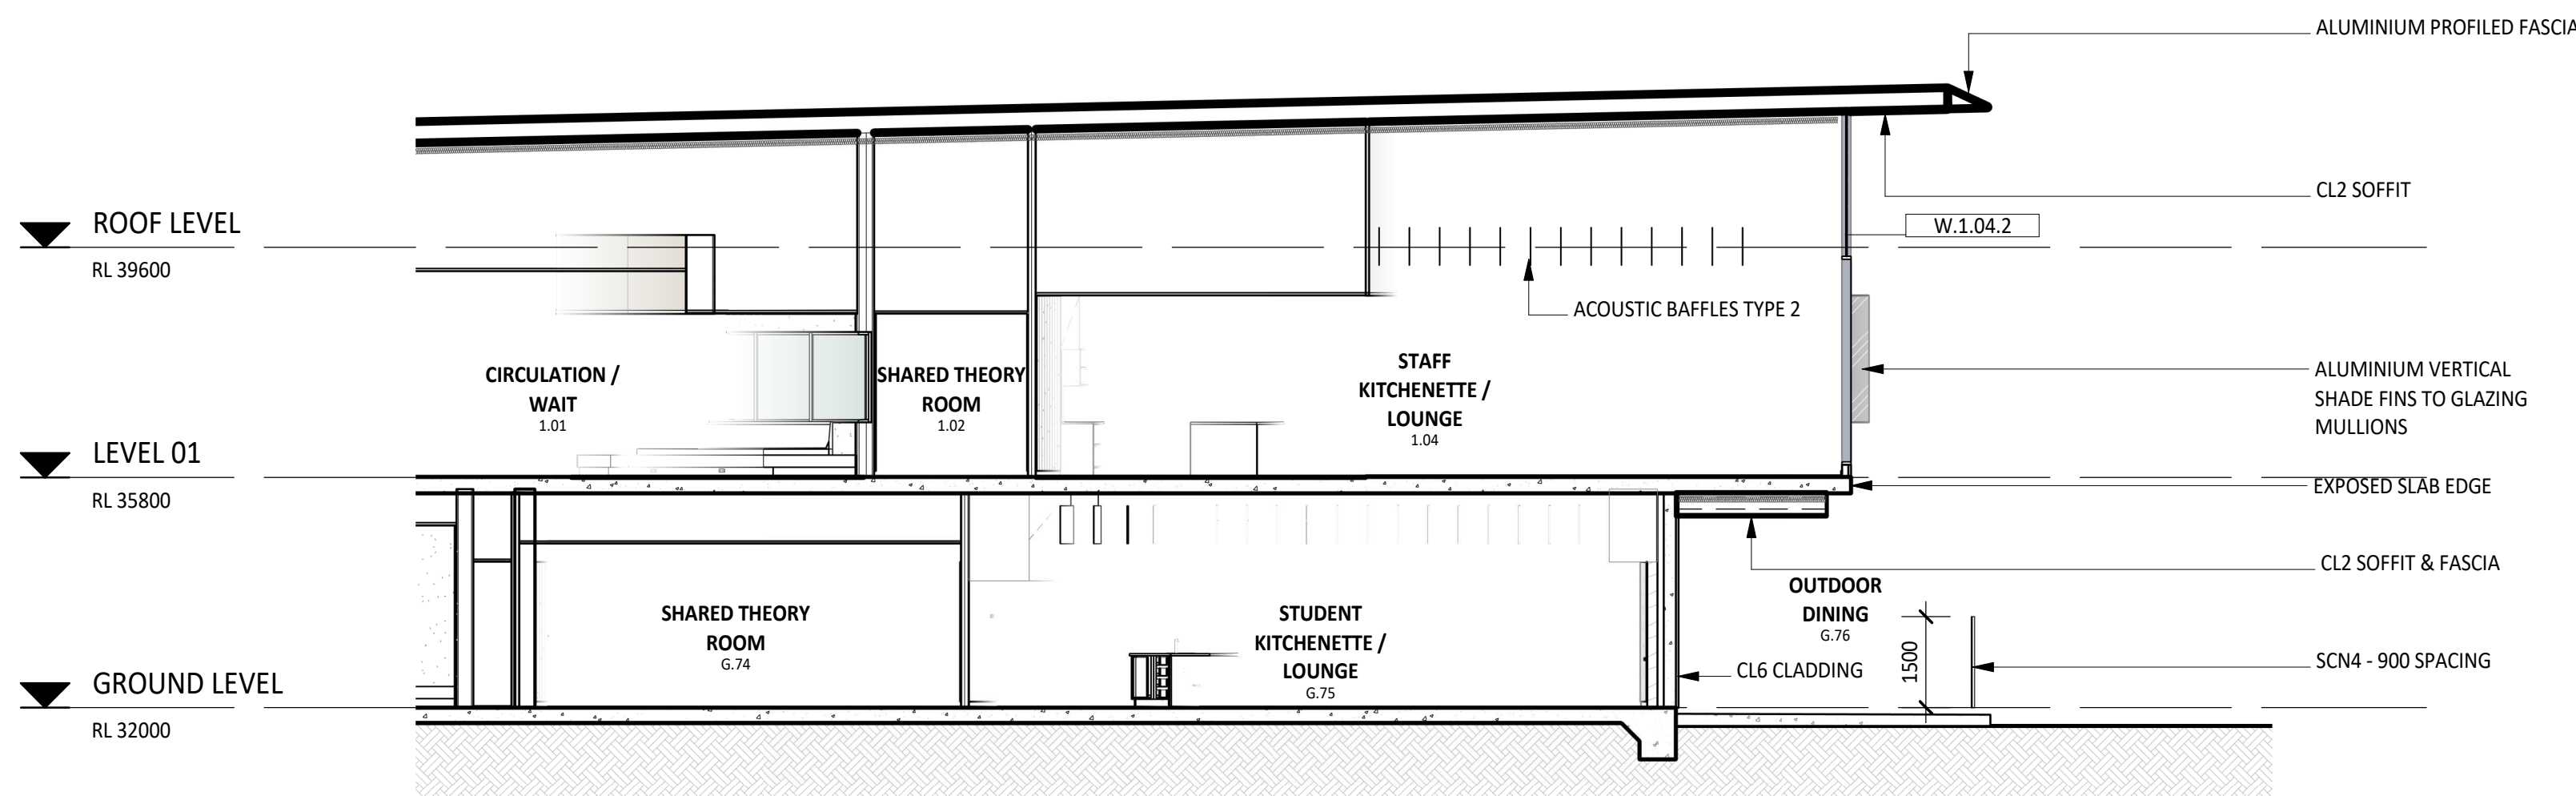

2
21-02
BUILDING SECTION - 11
1 : 100

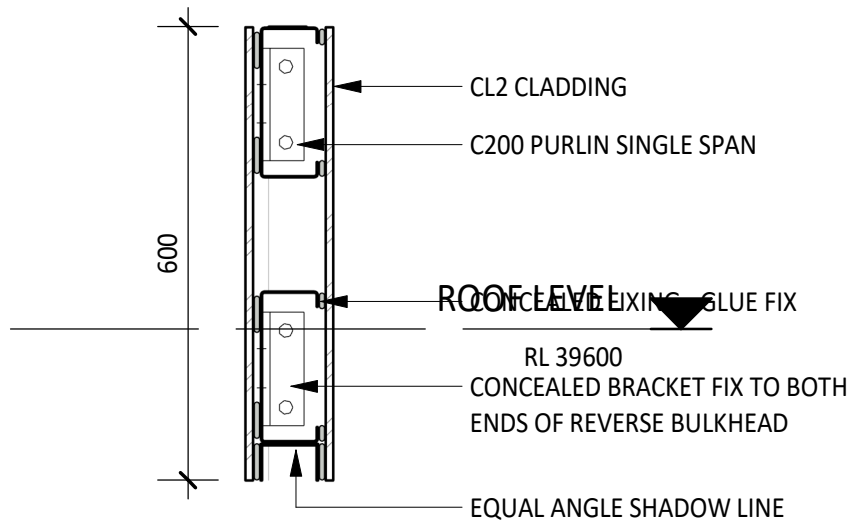

3
31-08
DETAIL - FEATURE ENTRANCE DIFFUSER - CL2 BAFFLE
1 : 10

ISSUED FOR TENDER