




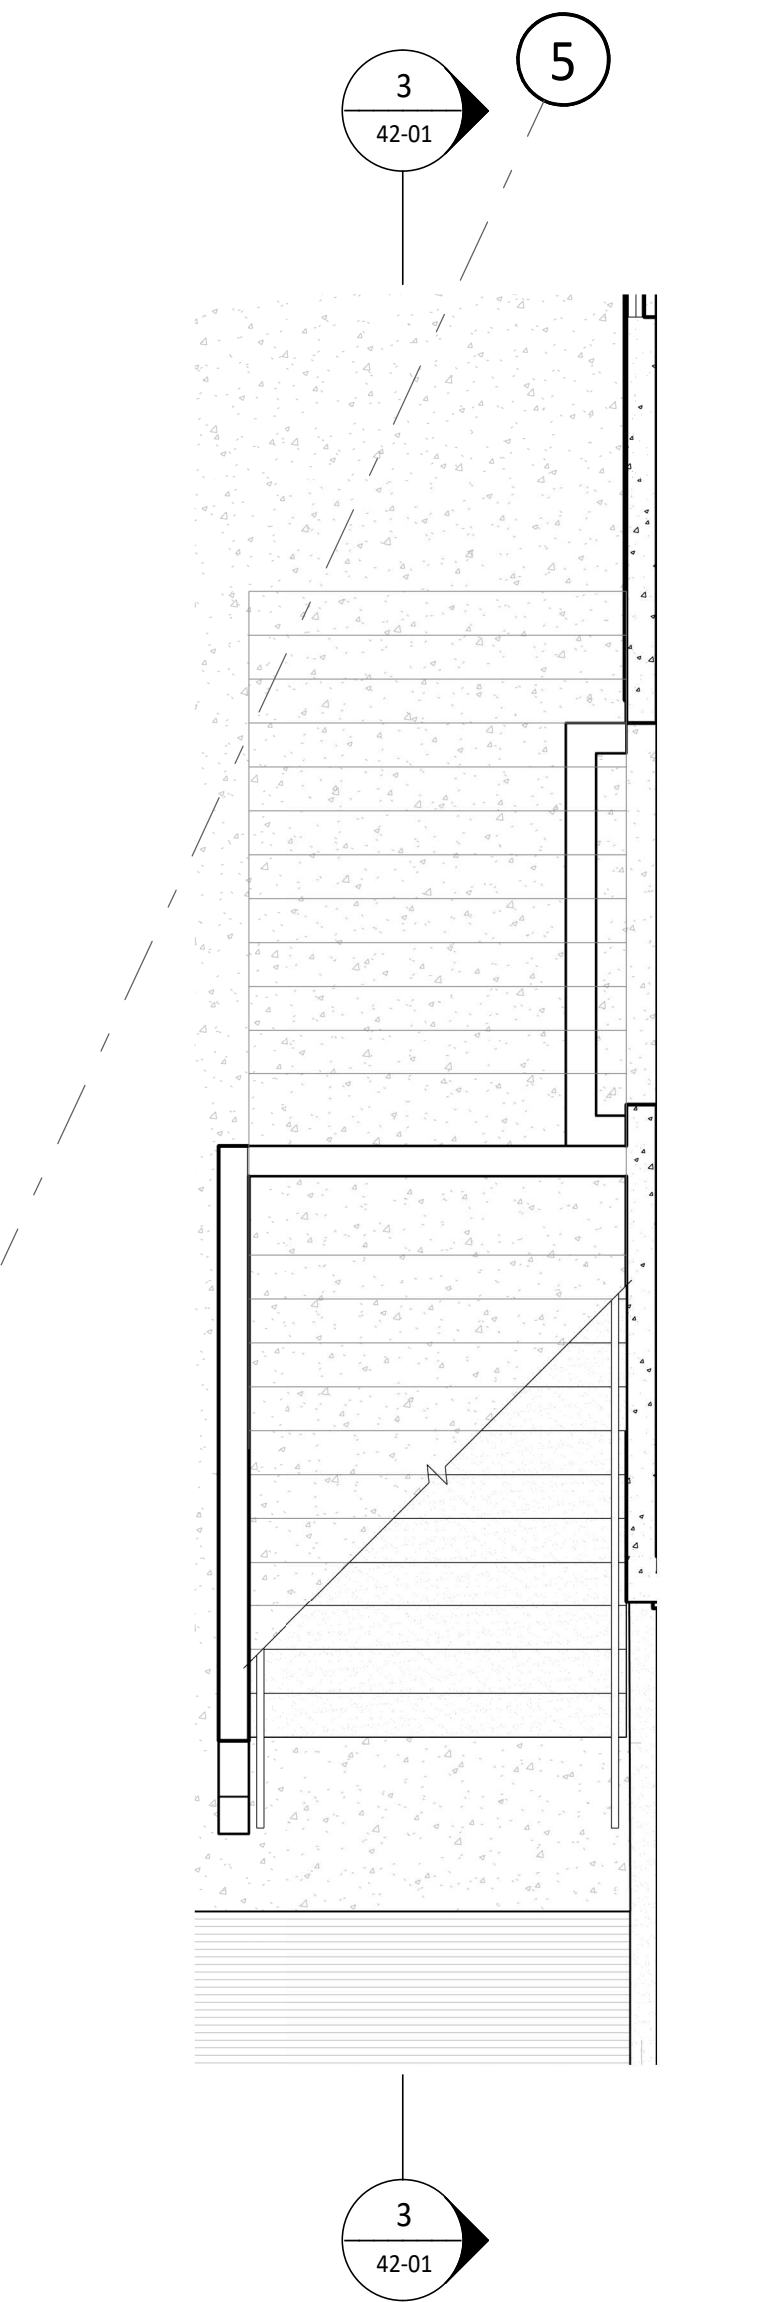

1 STAIR 01 - GROUND LEVEL
30-01 1 : 50

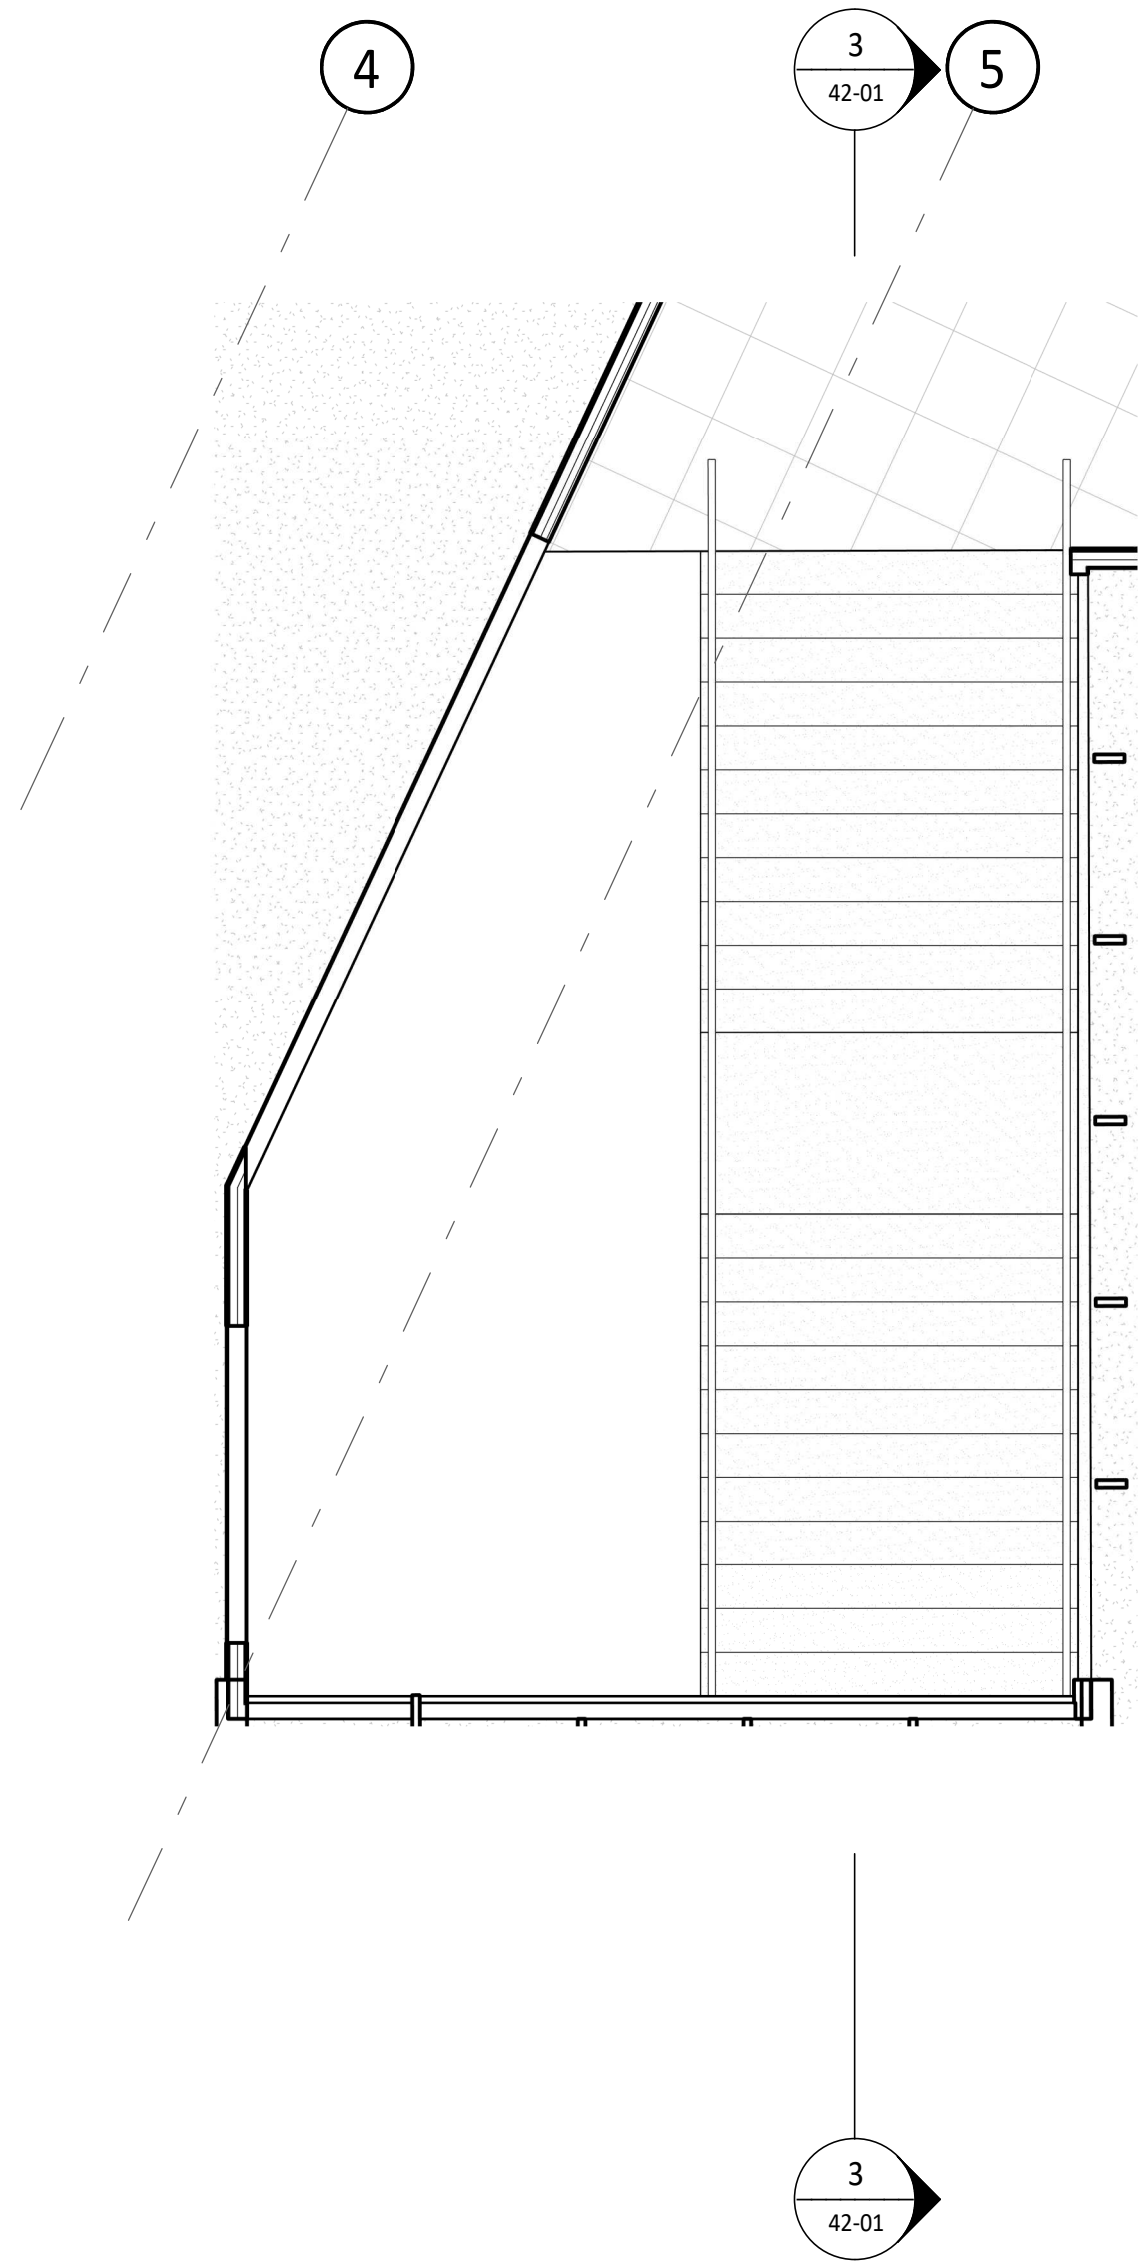

2 LEVEL 01
30-01 1 : 50

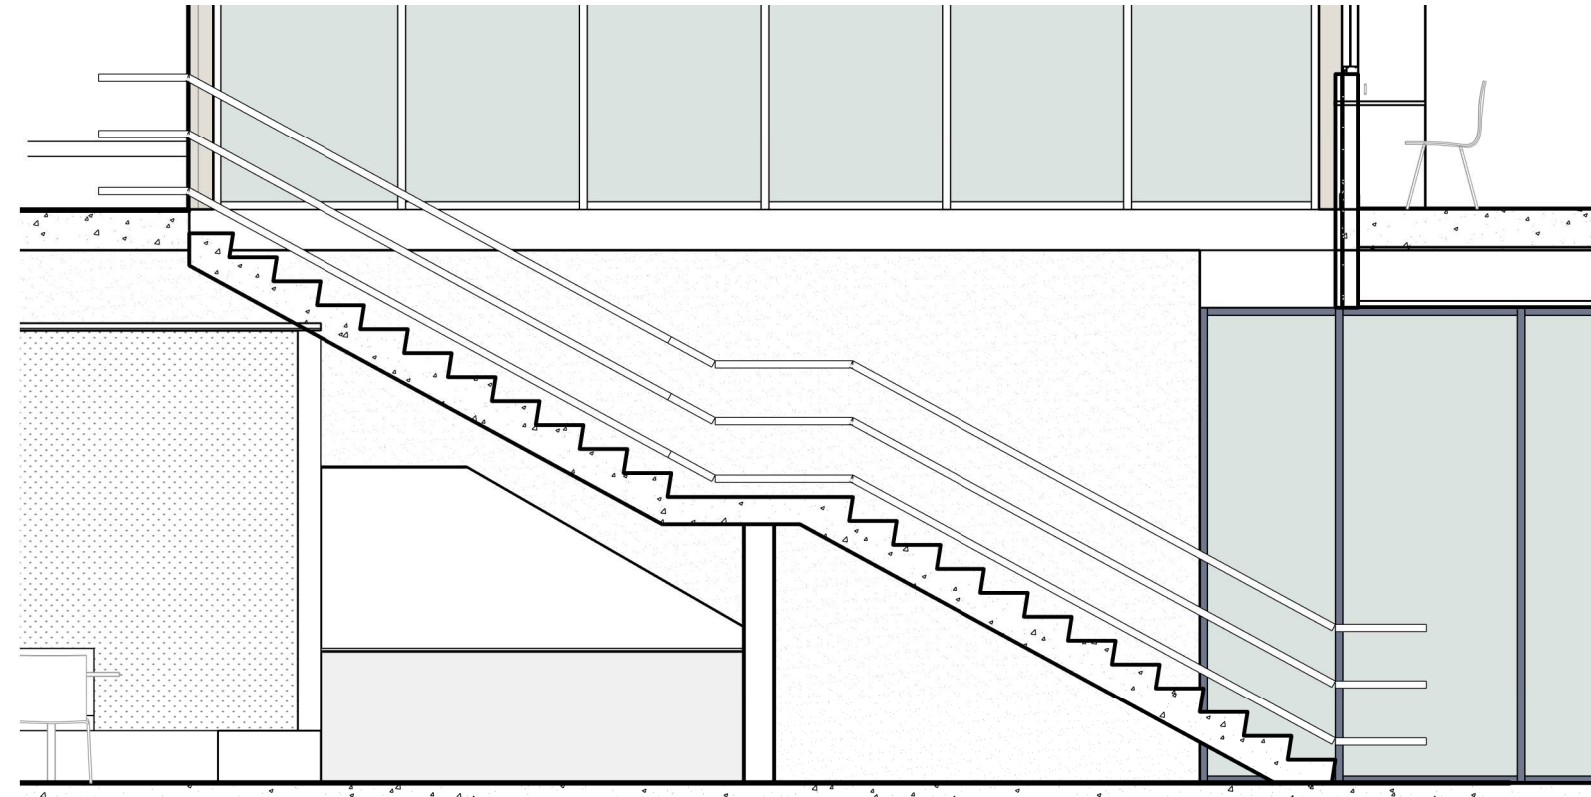

3 Section 13
42-01 1 : 50

ISSUED FOR TENDER

A	12/02/26	ISSUED FOR TENDER	BS
1	30/01/26	DRAFT 60% ISSUE	BS
rev	date	details	init.

drawn	date
PT	30/01/26
checked	date
BS	30/01/26
verified	date
BS	30/01/26

scale

STAIR 01 - DETAILS

scale project no.
1 : 50 @ A1 260018

revision

A

sheet no.

CQU-ROK-092-00-ARC-42-01