




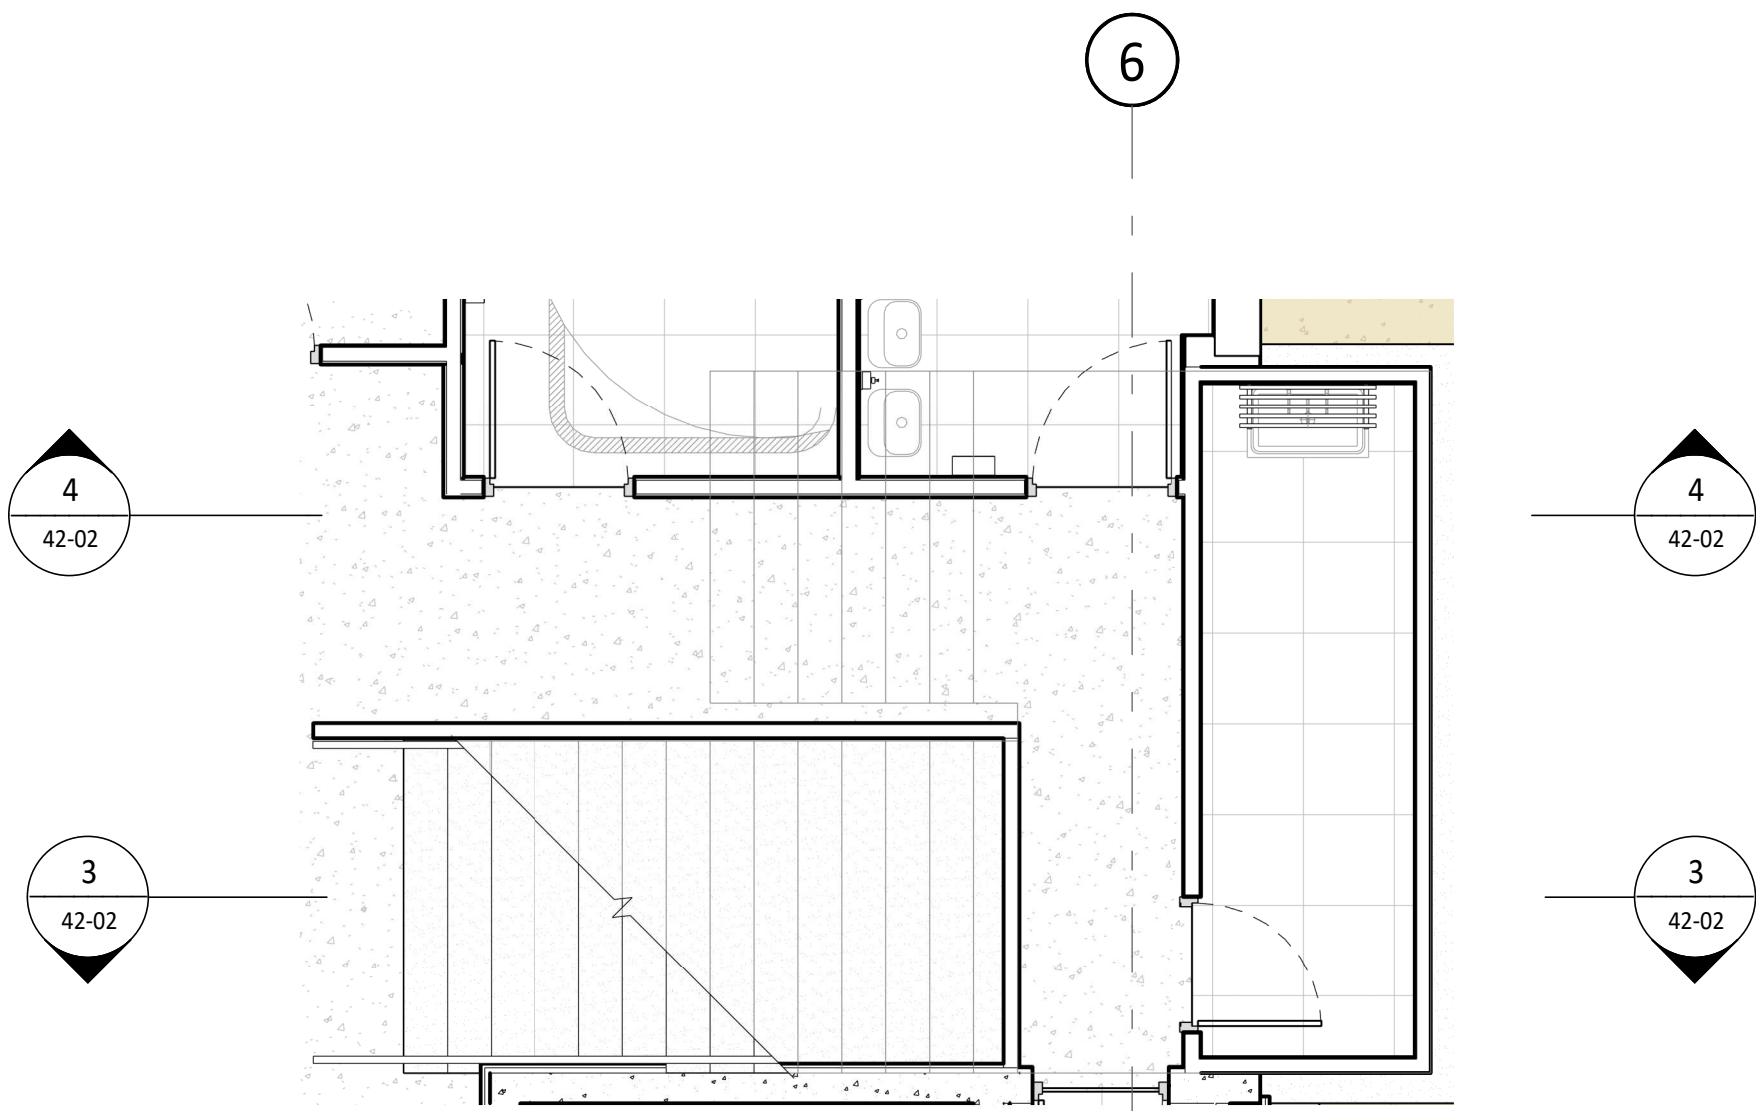


1 STAIR 02 - GROUND LEVEL
30-01 1 : 50

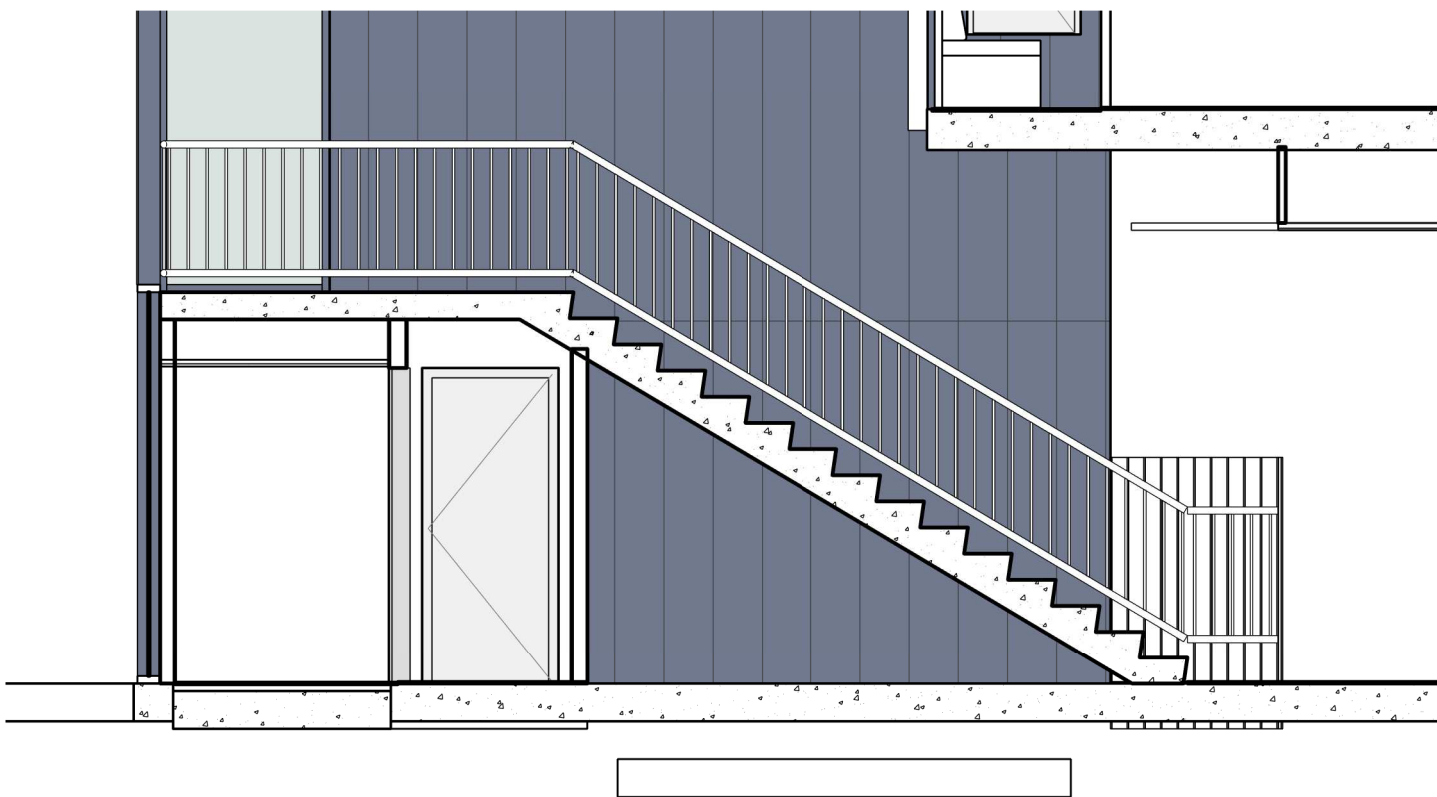

3 Section 14
42-02 1 : 50

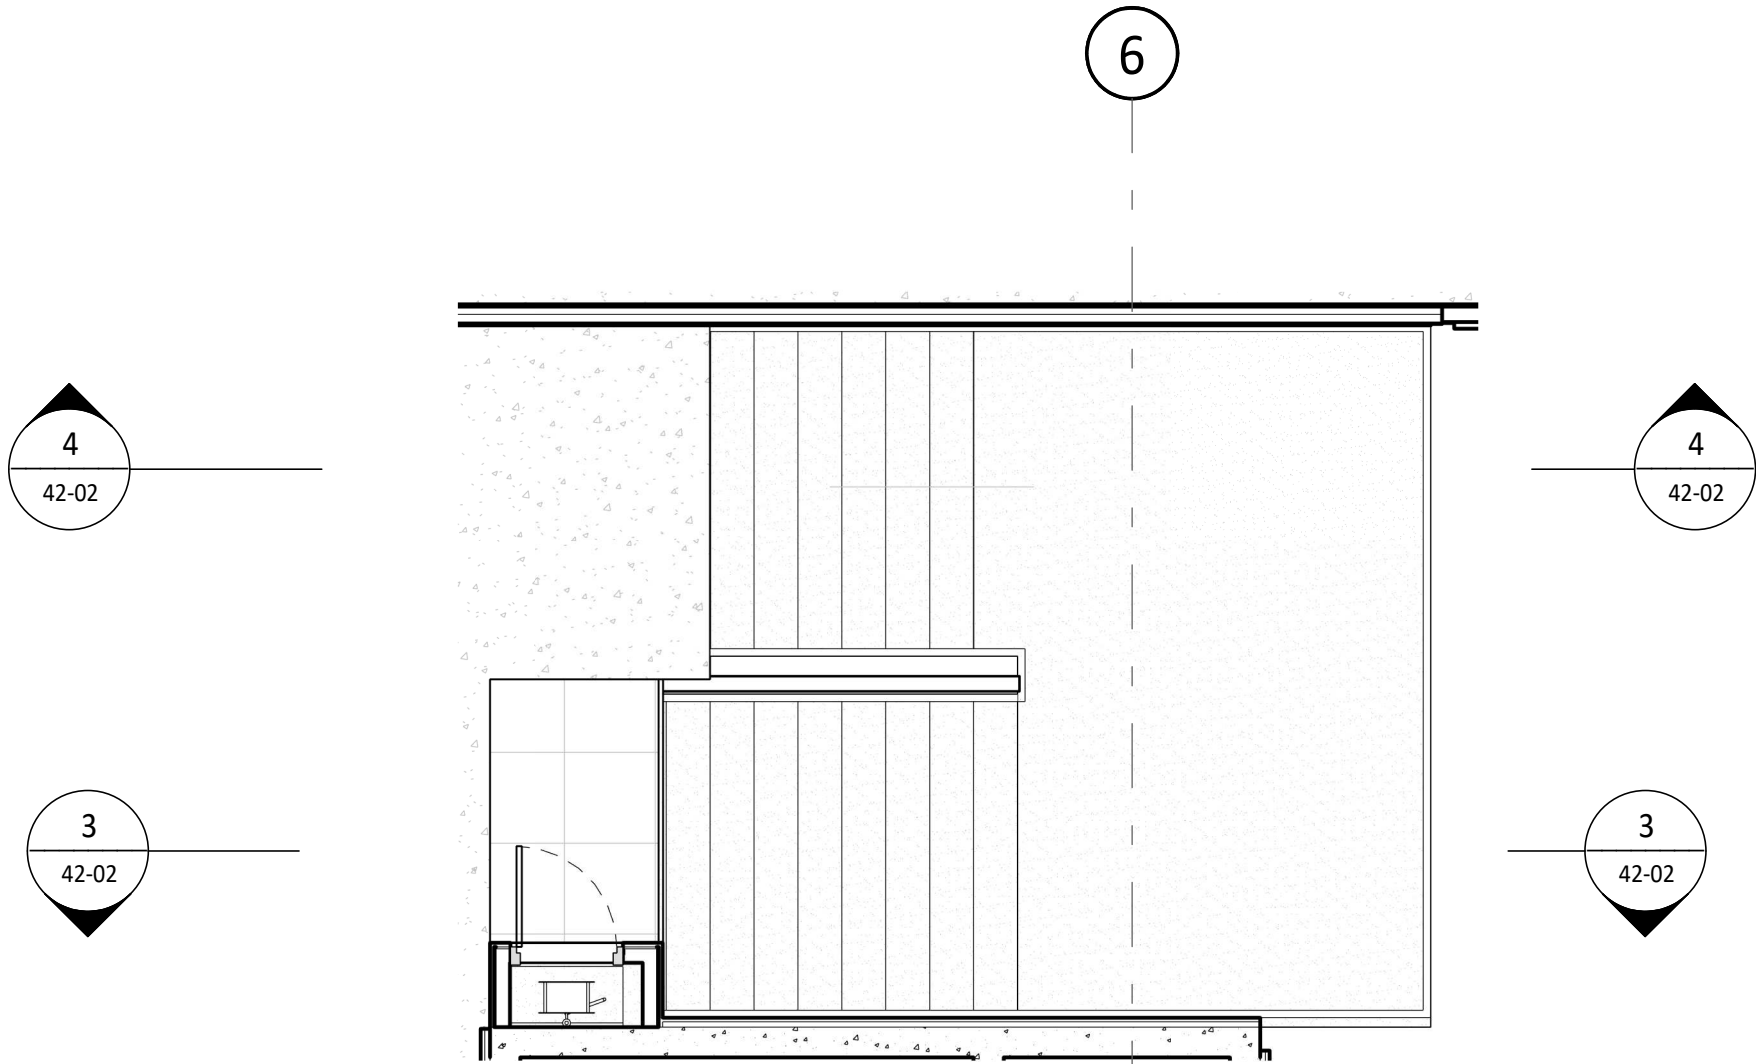

2 LEVEL 01
30-01 1 : 50

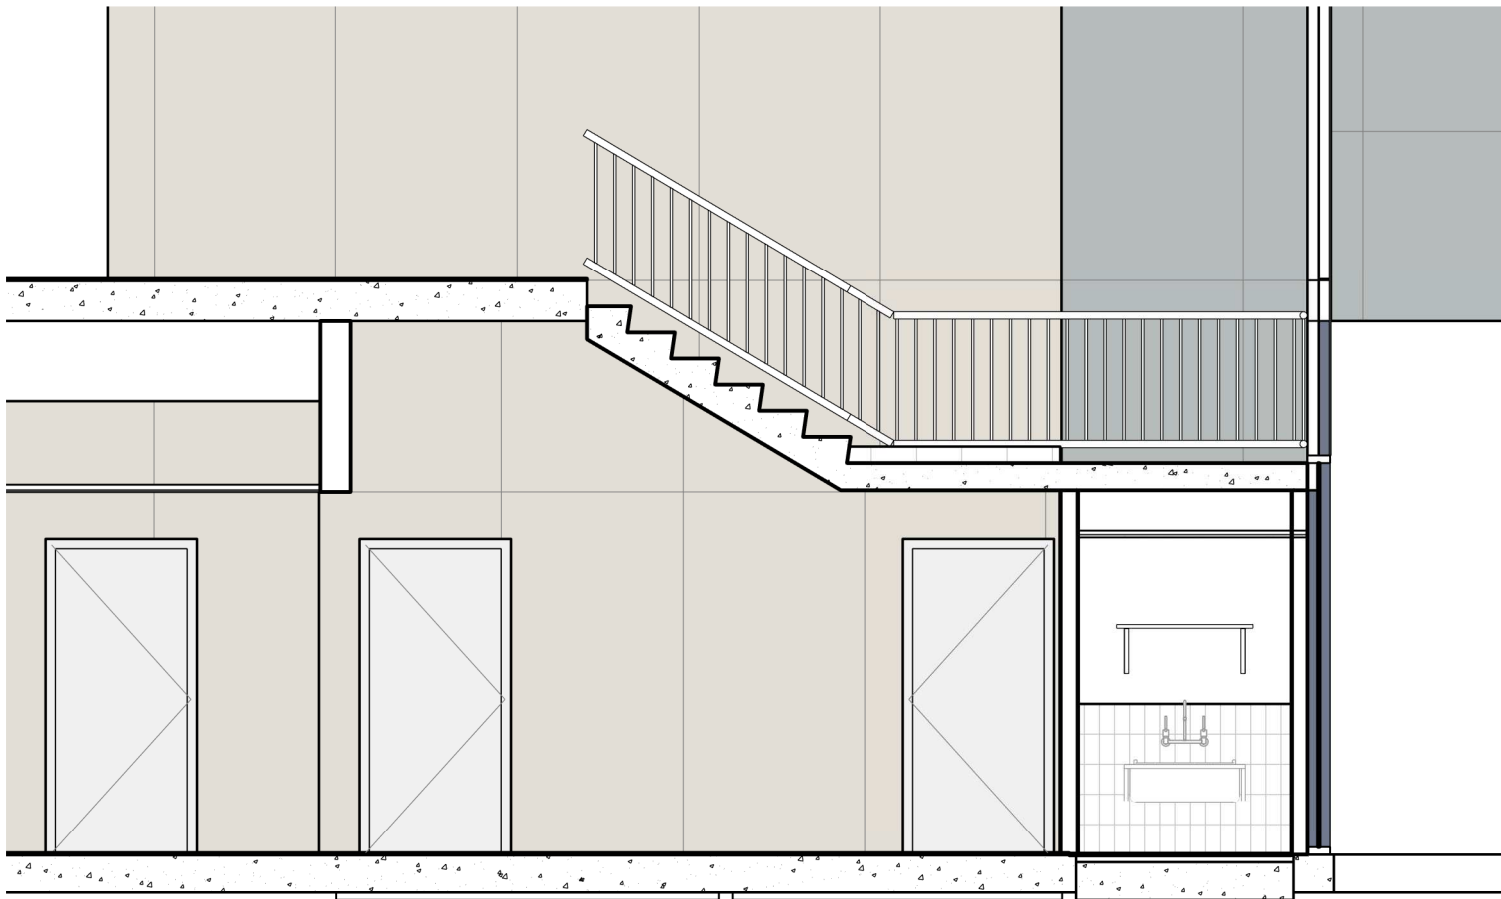

4 Section 15
42-02 1 : 50

thomson
adsett



Telephone +61 7 3840 9999
bne@thomsonadsett.com
Level 9, 470 St Pauls Terrace
Fortitude Valley
Qld 4006 Australia
thomsonadsett.com

© Copyright
These drawings and designs and the copyright thereof are the property of Thomson Adsett Pty Ltd and must not be used, retained or copied without written permission of Thomson Adsett Pty Ltd. ABN 76 105 314 654 Trading as ThomsonAdsett. Dimensions take precedence over scaling. Do not measure off drawings as print sizes may vary

CQU ROCKHAMPTON TAFE CONSOLIDATION - STAGE 2

554/700 Yaamba Rd, Norman
Gardens QLD 4701



A	12/02/26	ISSUED FOR TENDER	BS
1	30/01/26	DRAFT 60% ISSUE	BS
rev\	date	details	init.

drawn	date
PT	30/01/26
checked	date
BS	30/01/26
verified	date
BS	30/01/26

scale

STAIR 02 - DETAILS

scale project no.
1 : 50 @ A1 260018
revision
A
sheet no.
CQU-ROK-092-00-ARC-42-02

original sheet size - A1 (594mm x 841mm)

ISSUED FOR TENDER

12/02/2026 4:36:54 PM Autodesk Docs:/CQU ROK TAFE/260018_A_CQU-UNIVERSITY_BLD-TRADES_R25.rvt