

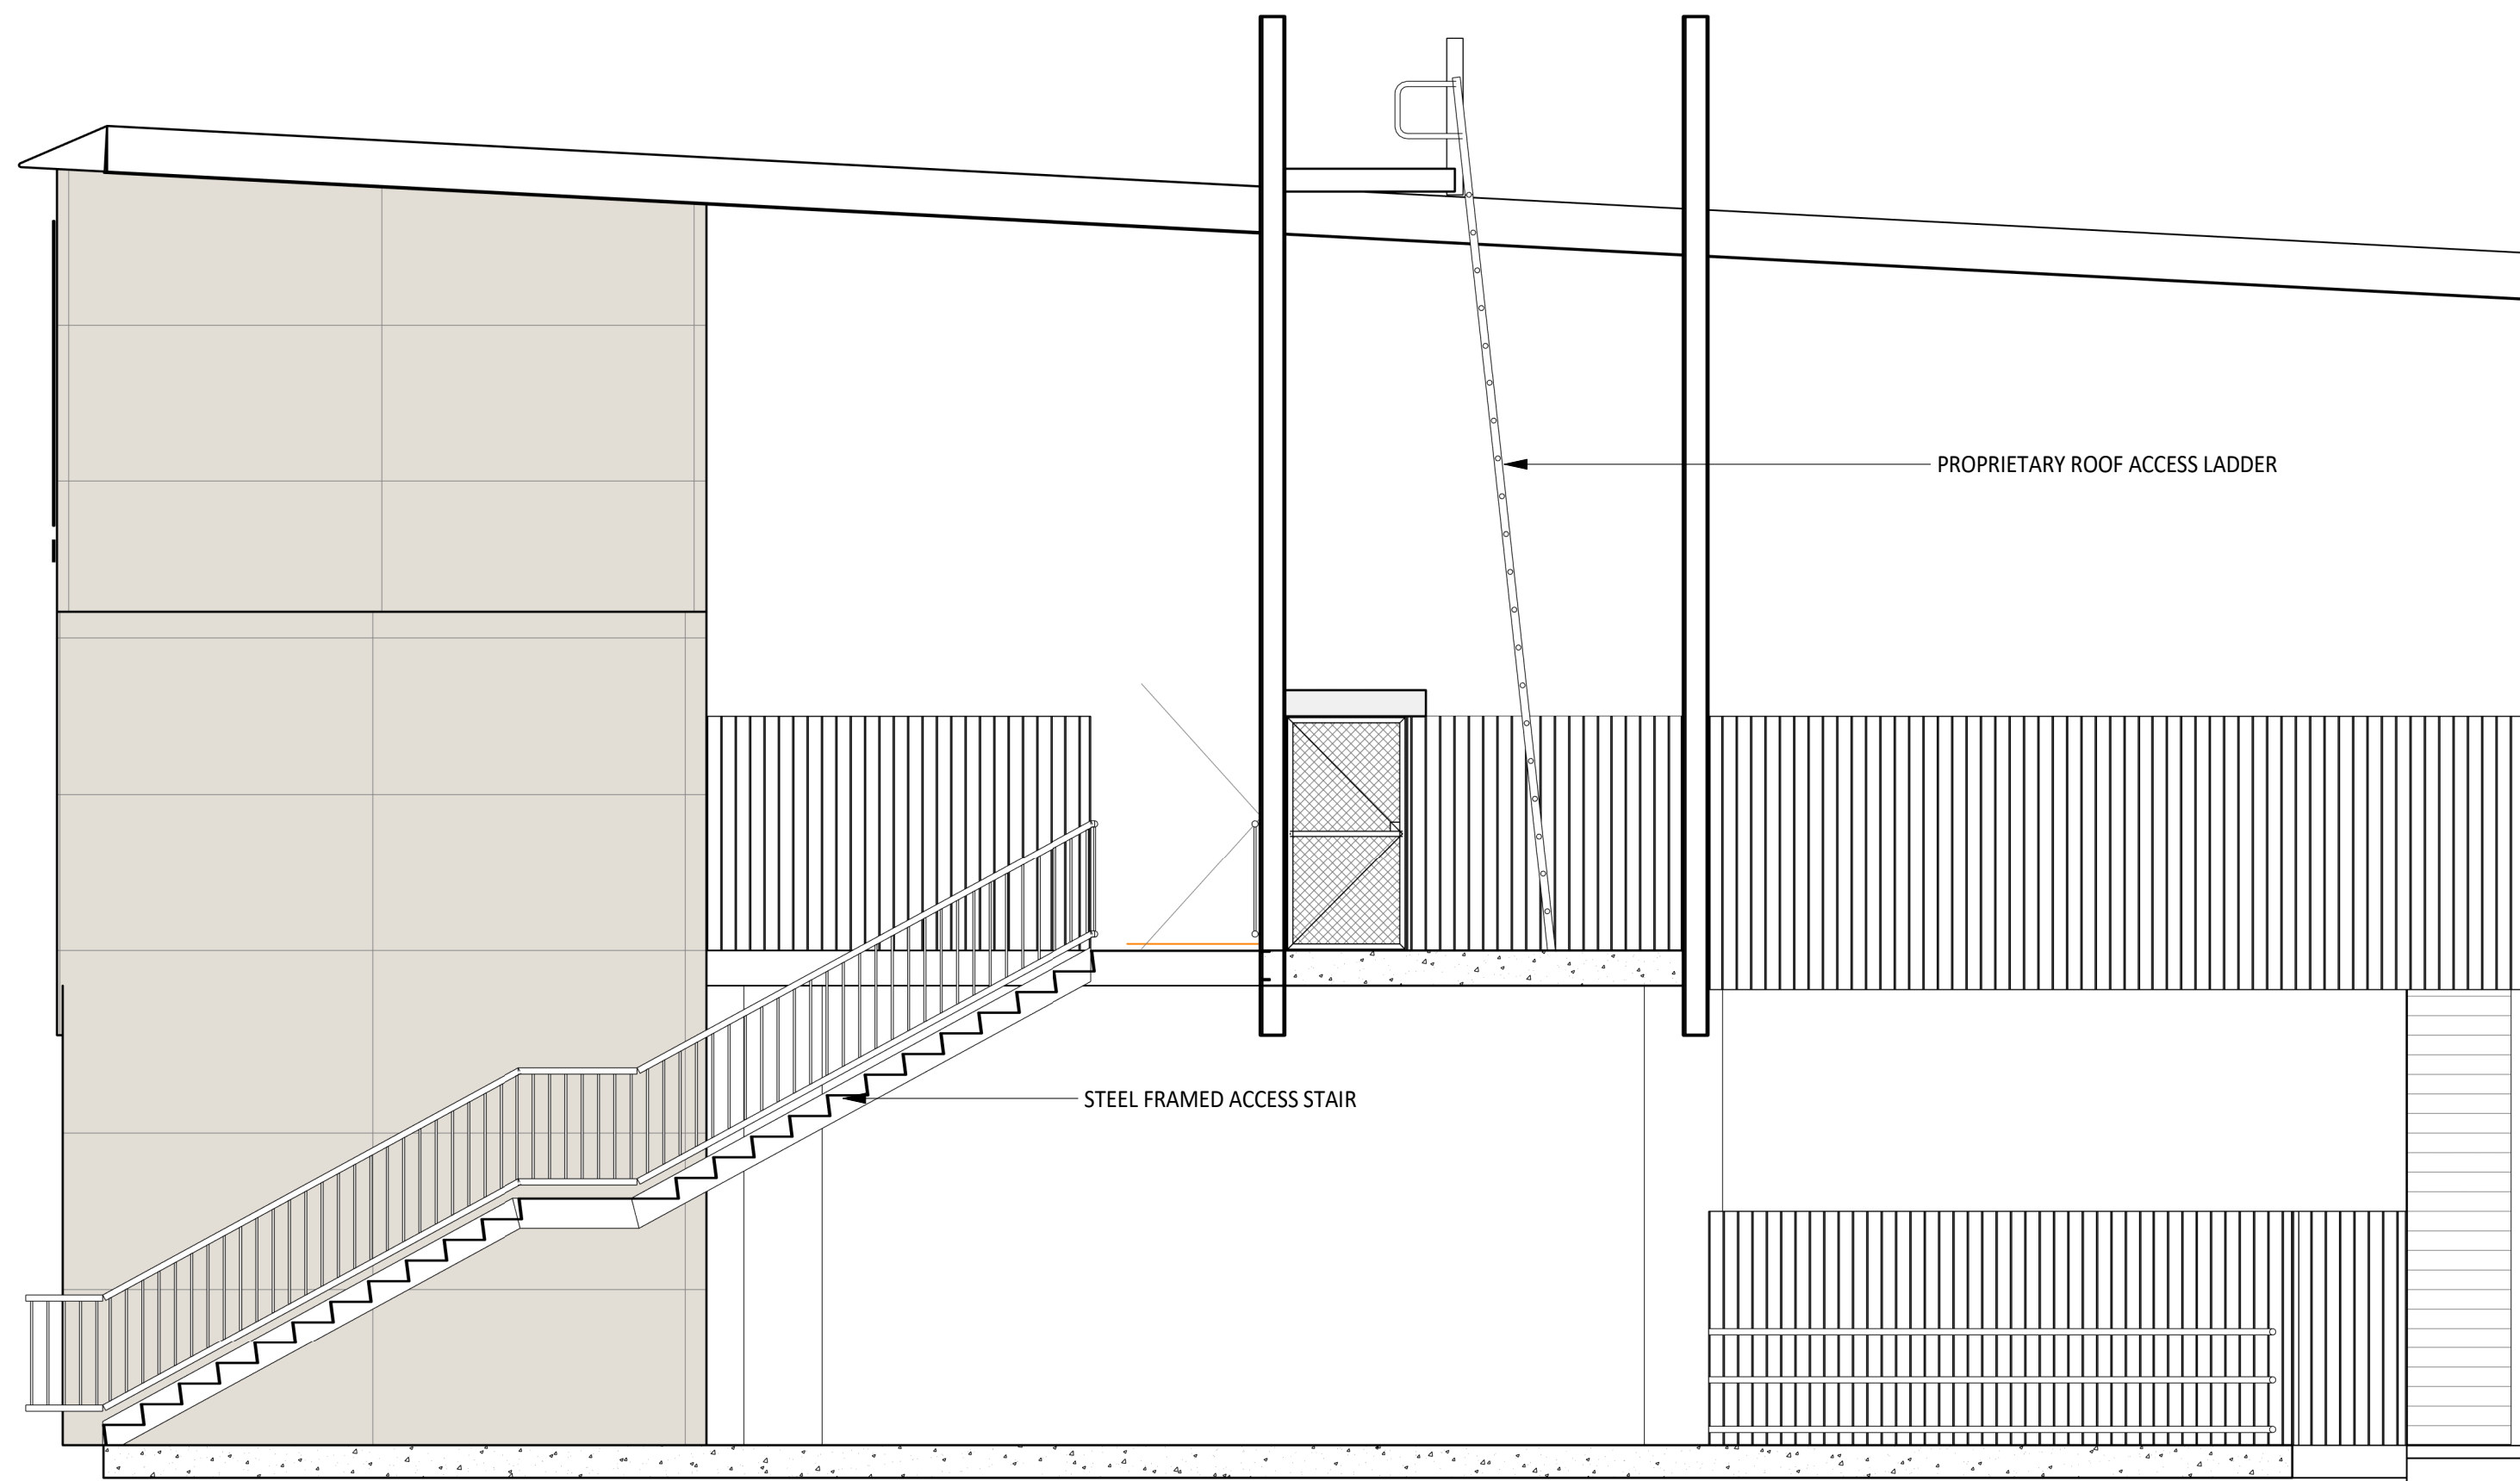


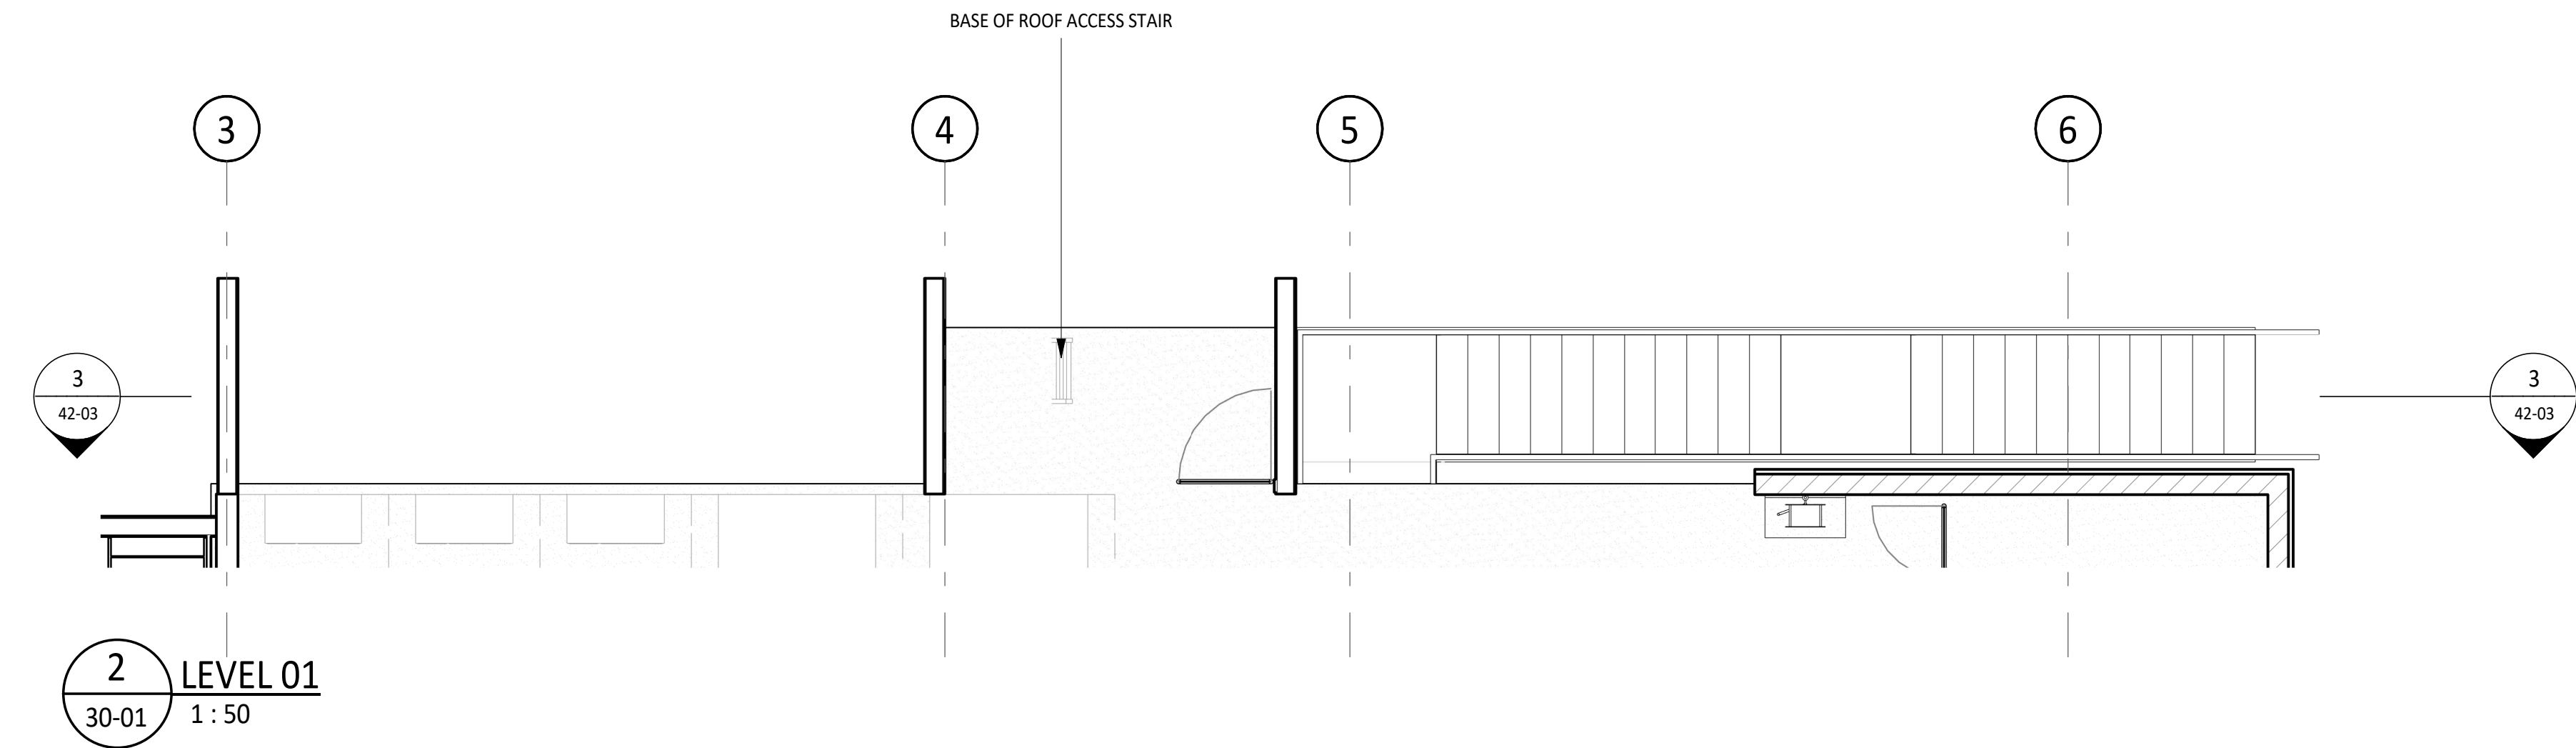

**CQU ROCKHAMPTON
TAFE
CONSOLIDATION -
STAGE 2**

554/700 Yaamba Rd, Norman
Gardens QLD 4701

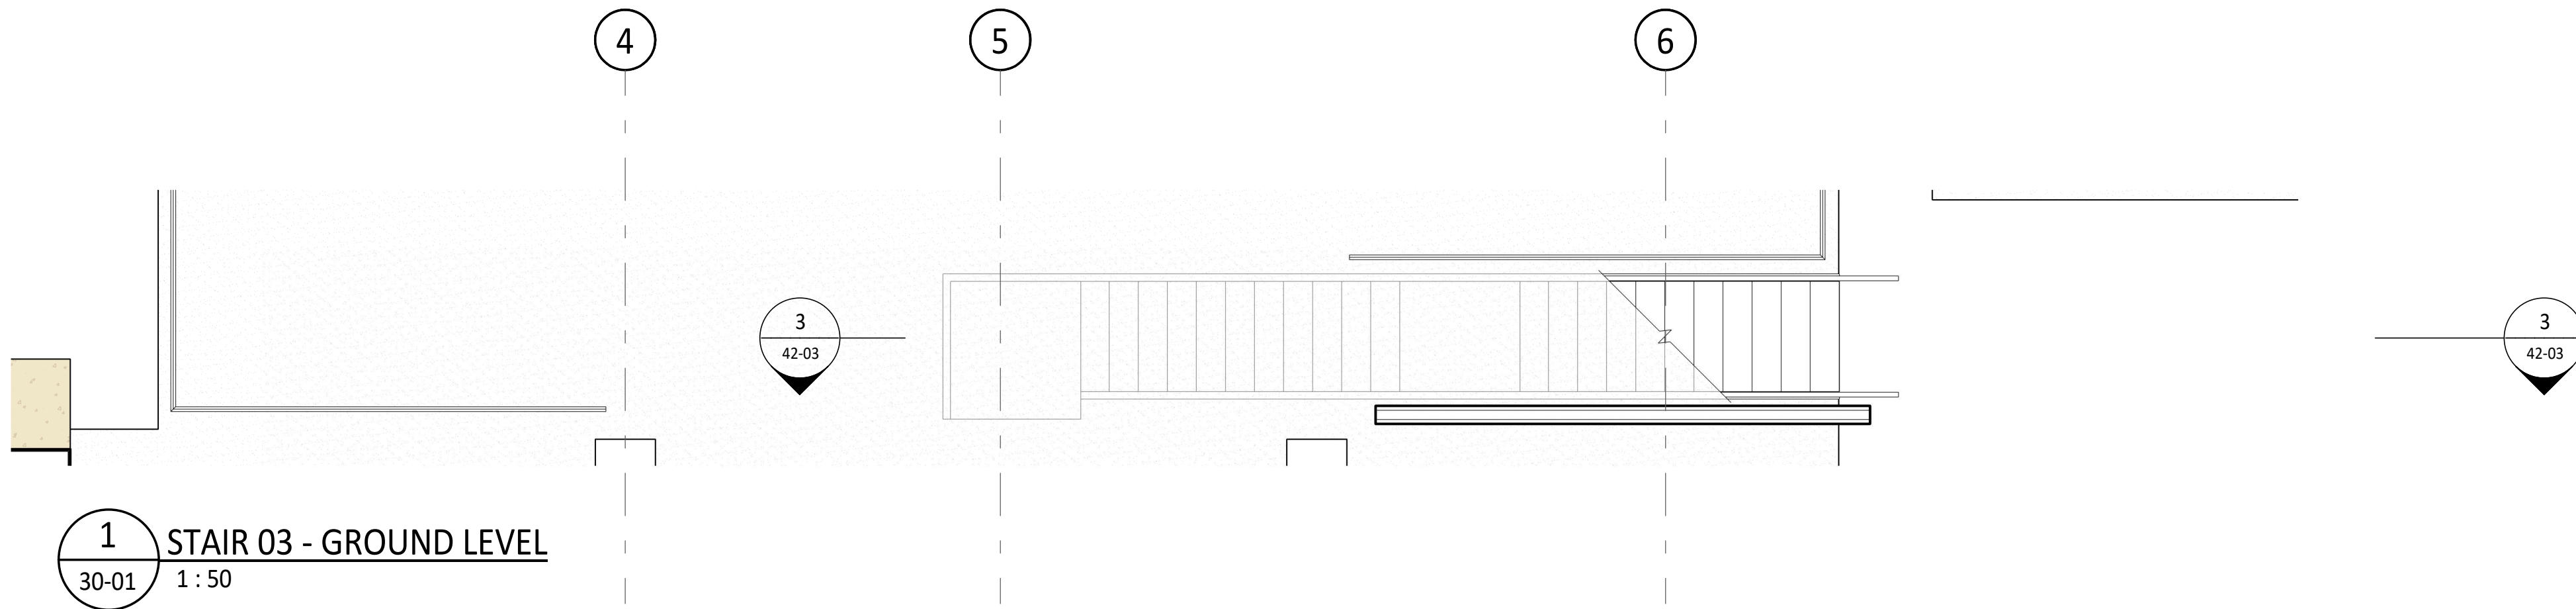

A	12/02/26	ISSUED FOR TENDER	BS
1	30/01/26	DRAFT 60% ISSUE	BS
rev\	date	details	init.

drawn	date
PT	30/01/26
checked	date
BS	30/01/26
verified	date
BS	30/01/26

scale

STAIR 03 - DETAILS

scale project no.
1 : 50 @ A1 260018

revision
A
sheet no.
CQU-ROK-092-00-ARC-42-03

ISSUED FOR TENDER