



2 EAST SHADE SCREEN ELEVATION
1 : 50

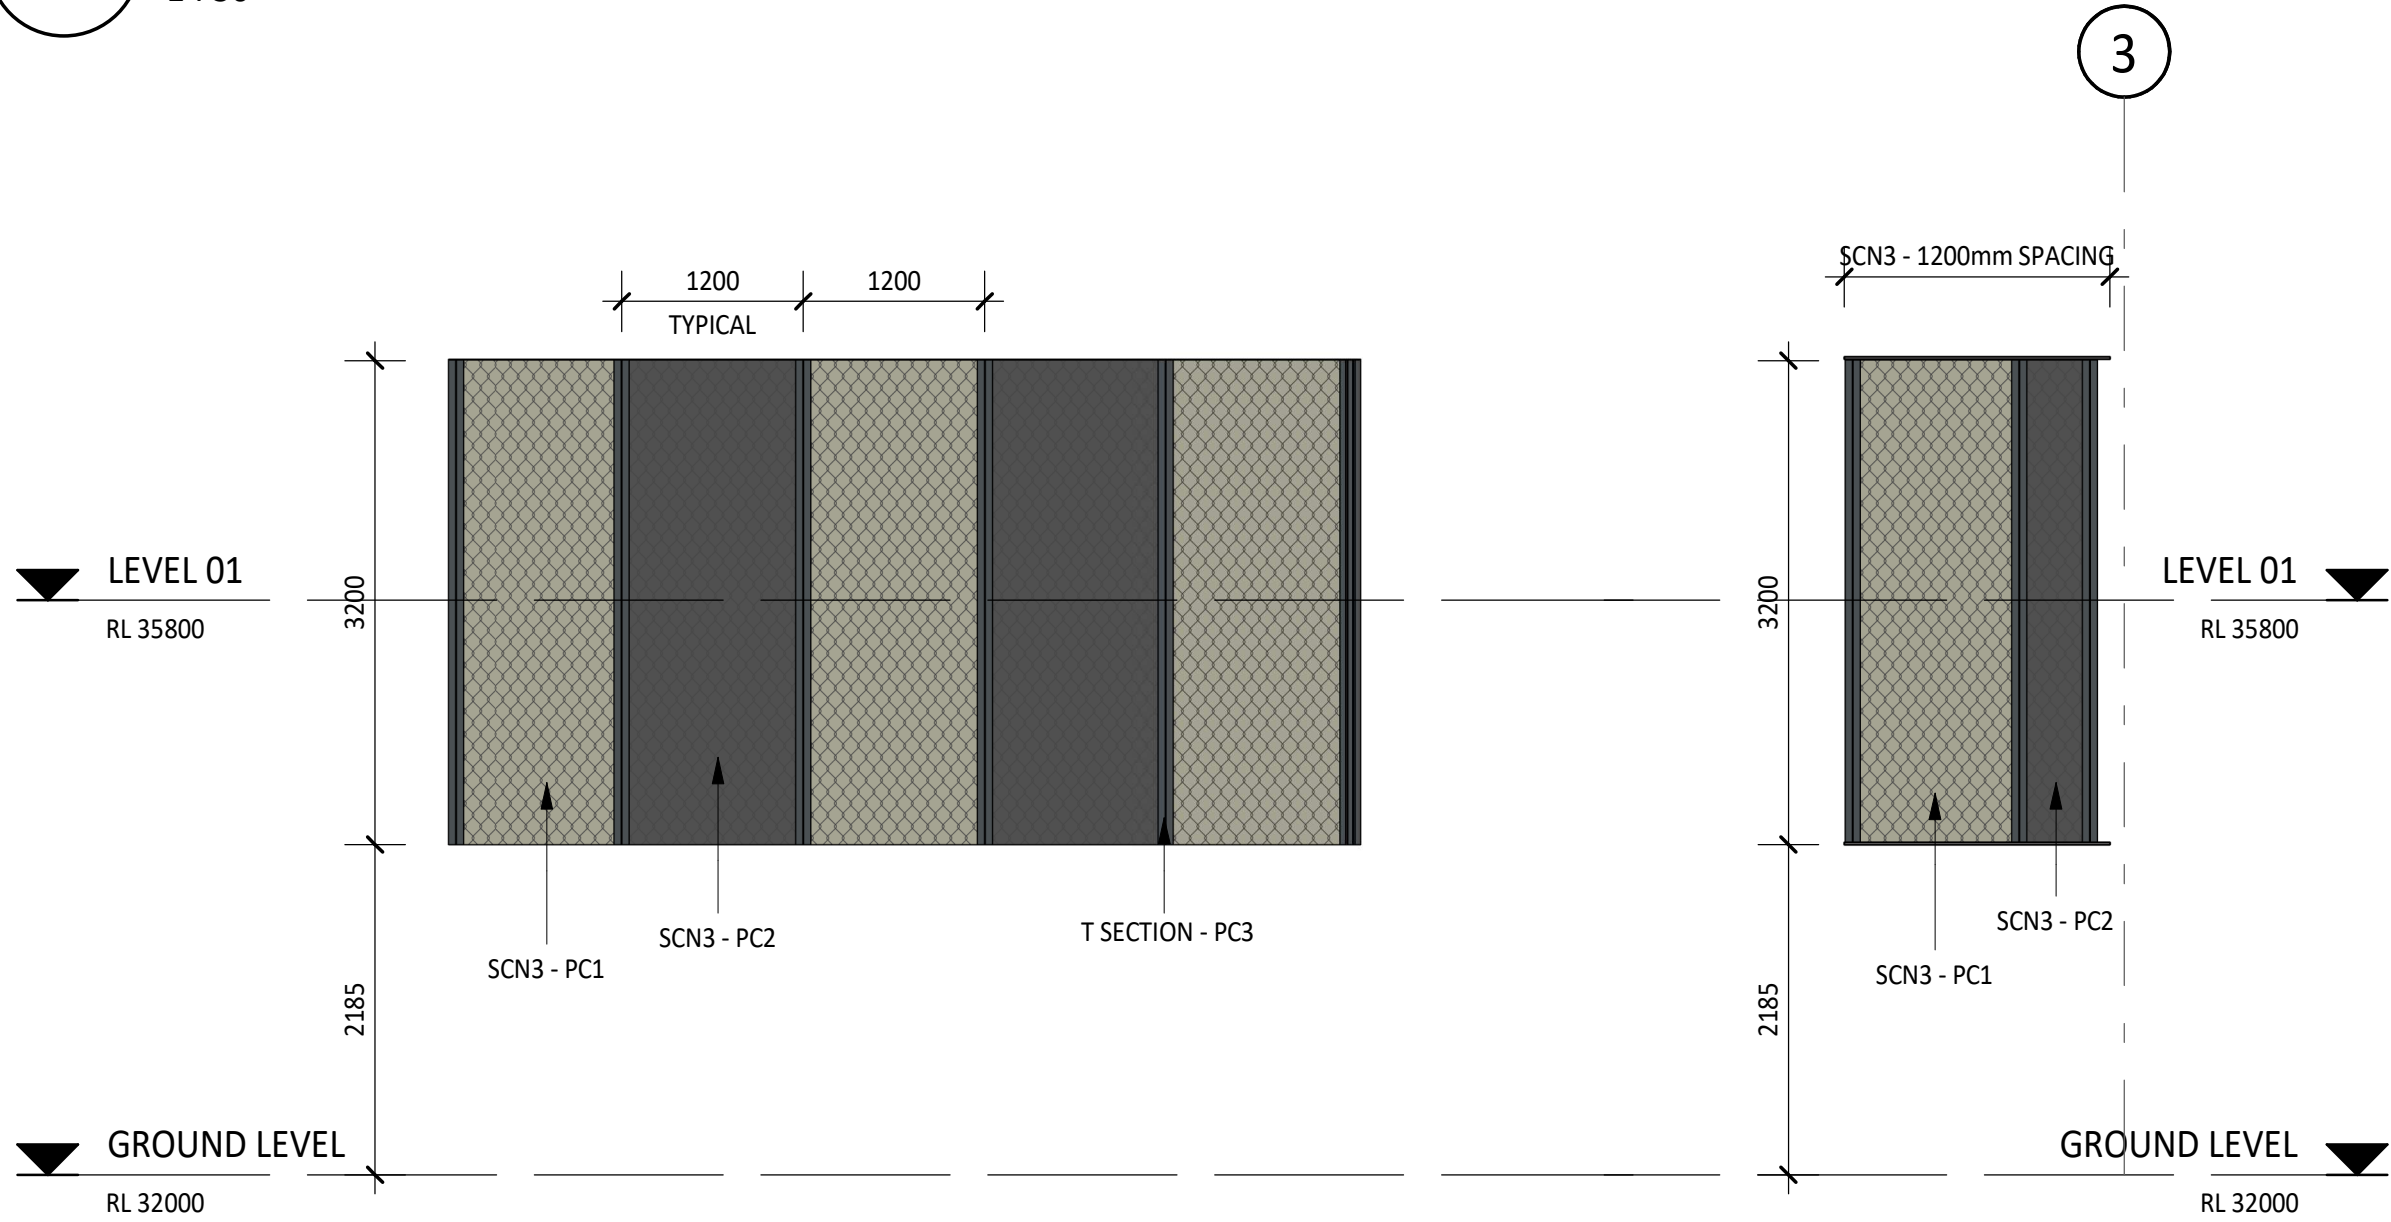


1 WEST SHADE SCREEN 1
1 : 50

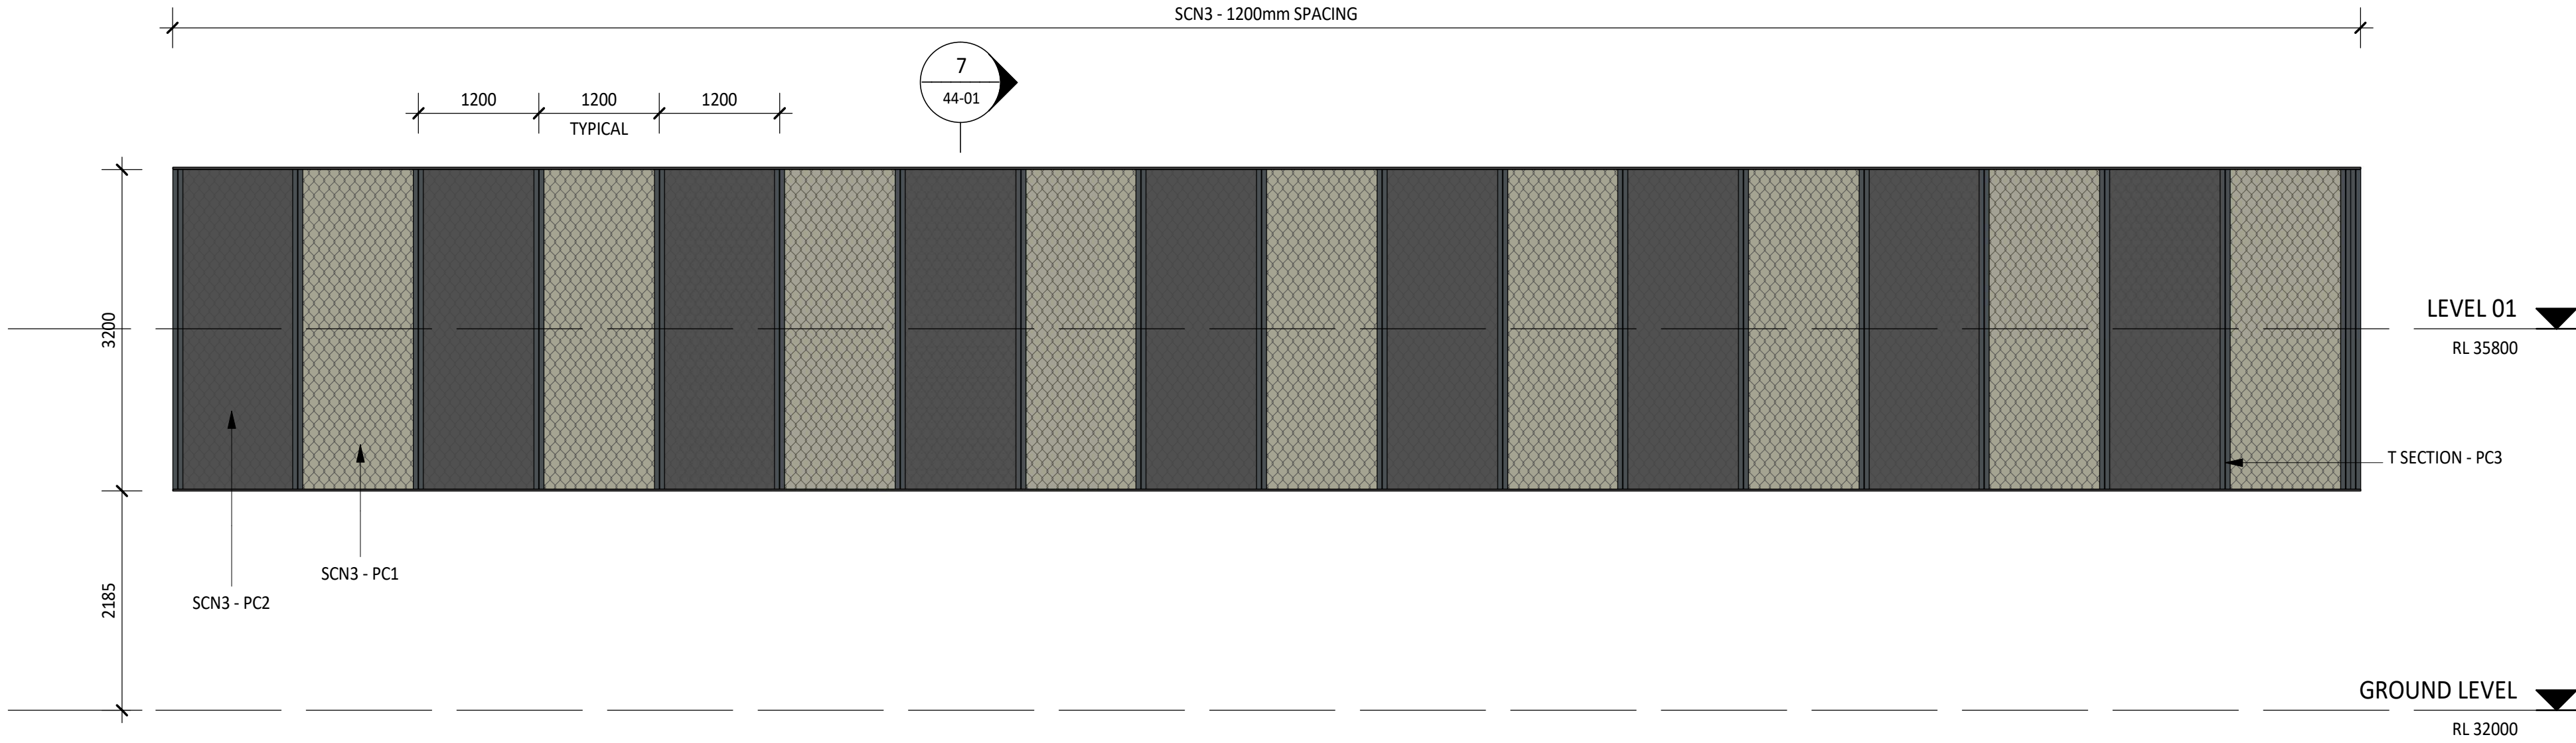


3 WEST SHADE SCREEN 2 ELEVATION
1 : 50

4 WEST SHADE SCREEN 3 ELEVATION
1 : 50


6 SHADING SCREEN PLAN
1 : 10

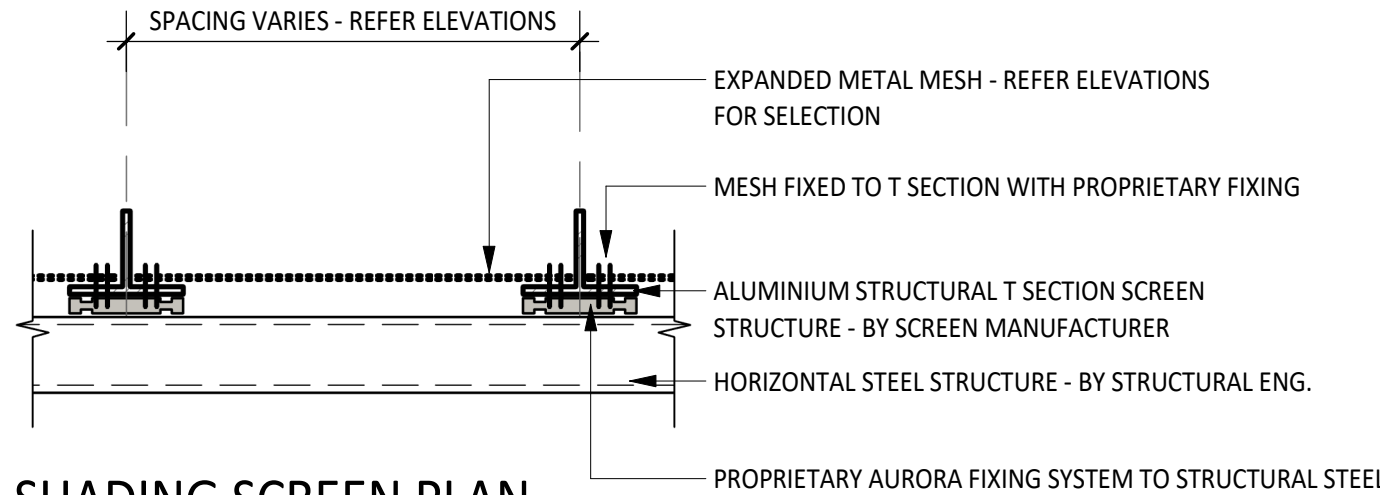


5 SHADE SCREEN SECTION
1 : 50

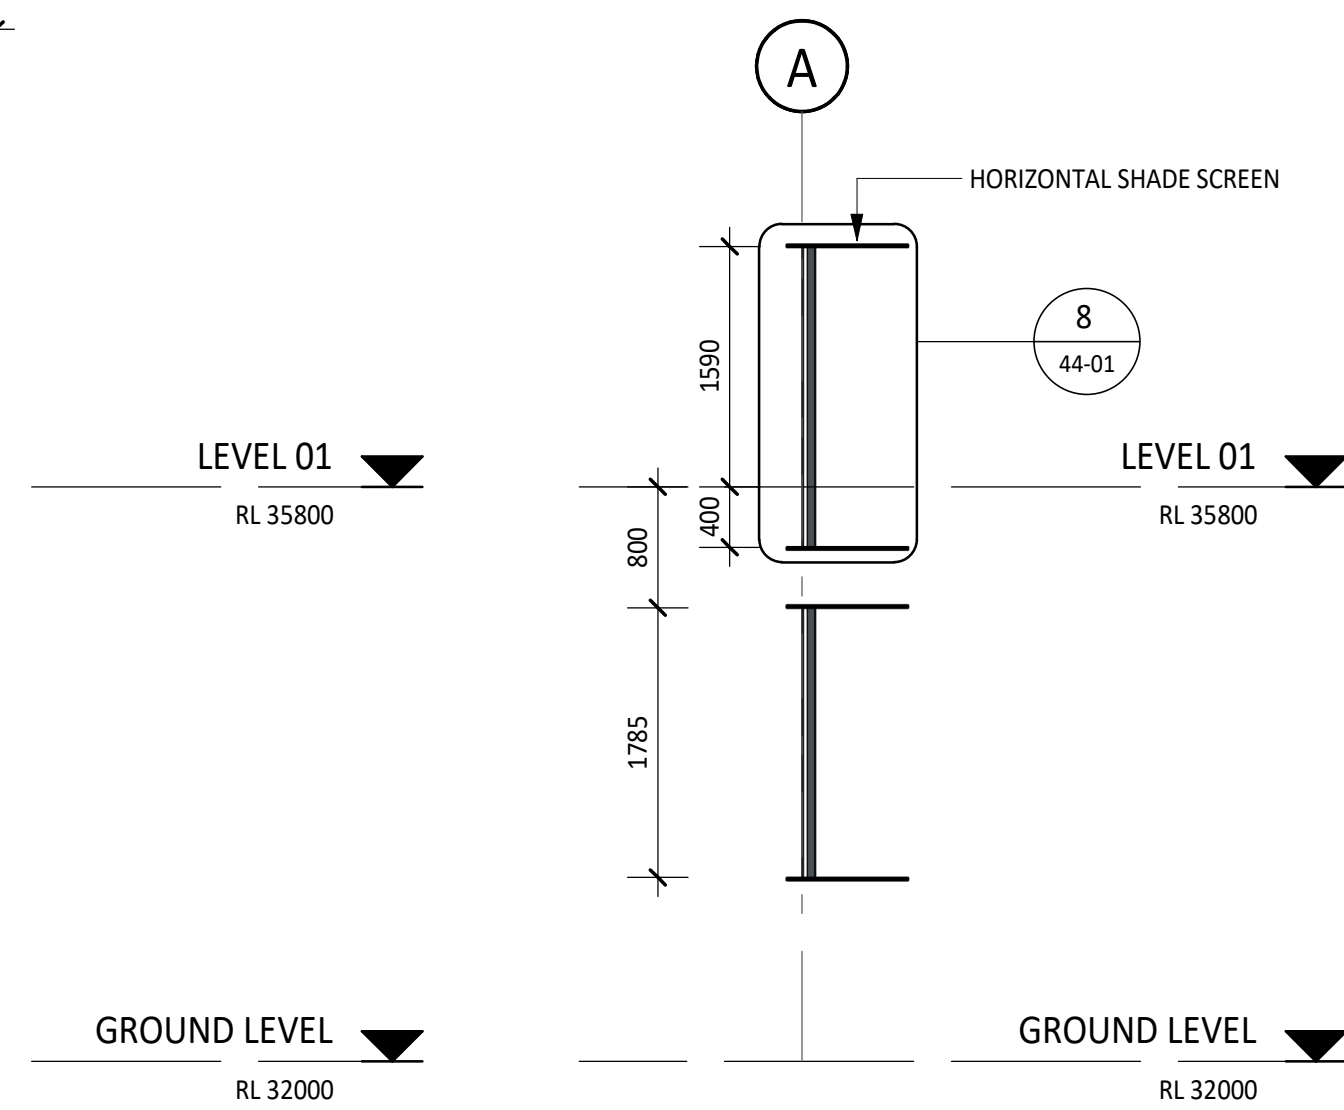

8 SHADE SCREEN SECTION - TYPICAL DETAIL
1 : 10

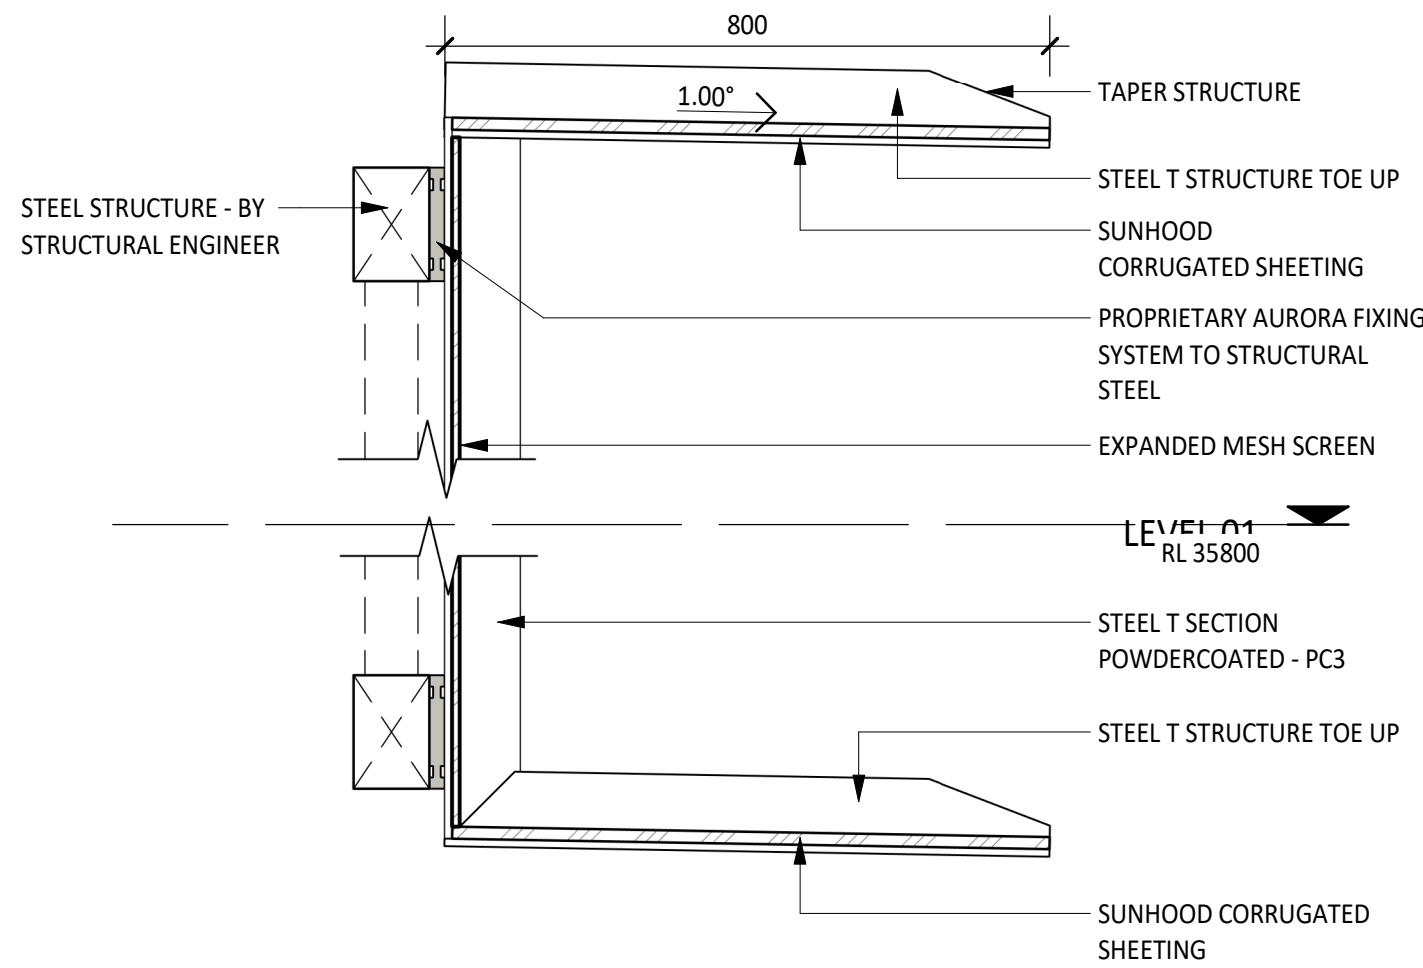

7 SHADE SCREEN SECTION
1 : 50

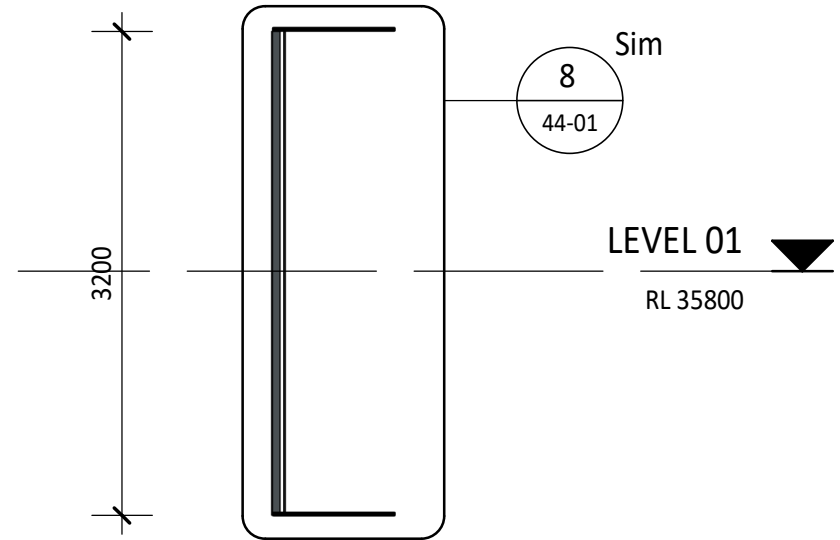

A	12/02/26	ISSUED FOR TENDER	BS
1	30/01/26	DRAFT 60% ISSUE	BS
rev	date	details	init.

drawn	date
PT	30/01/26
checked	date
BS	30/01/26
verified	date
BS	30/01/26

scale

SCREEN DETAILS

scale project no.

As indicated @ A1 260018

revision

A

sheet no.

CQU-ROK-092-00-ARC-44-01