




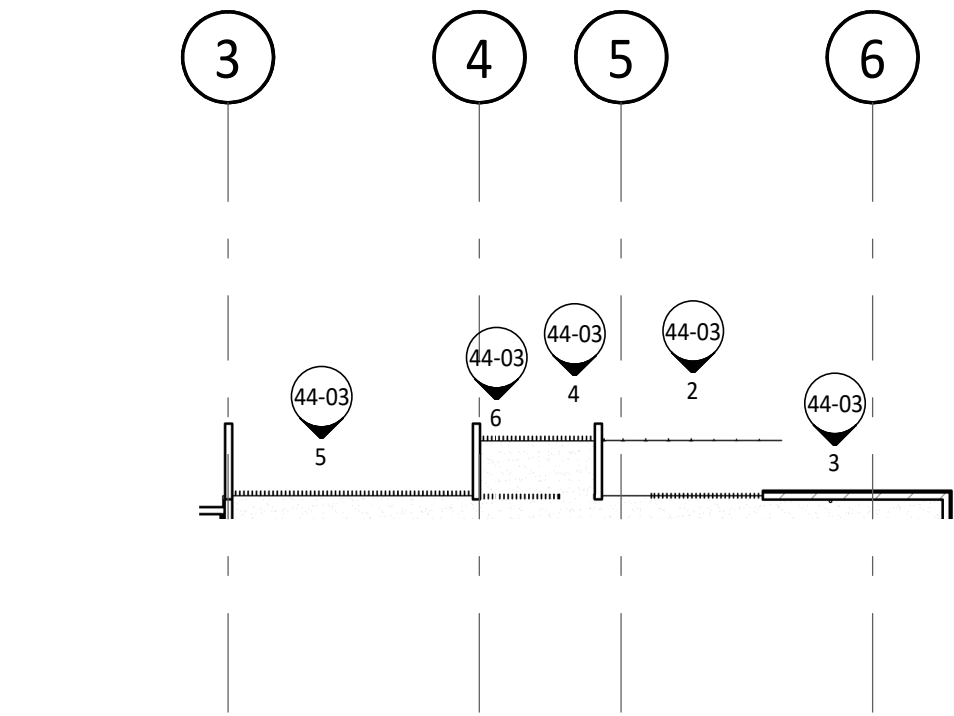


1 EXTERNAL STAIR SCREEN PLAN
1 : 200

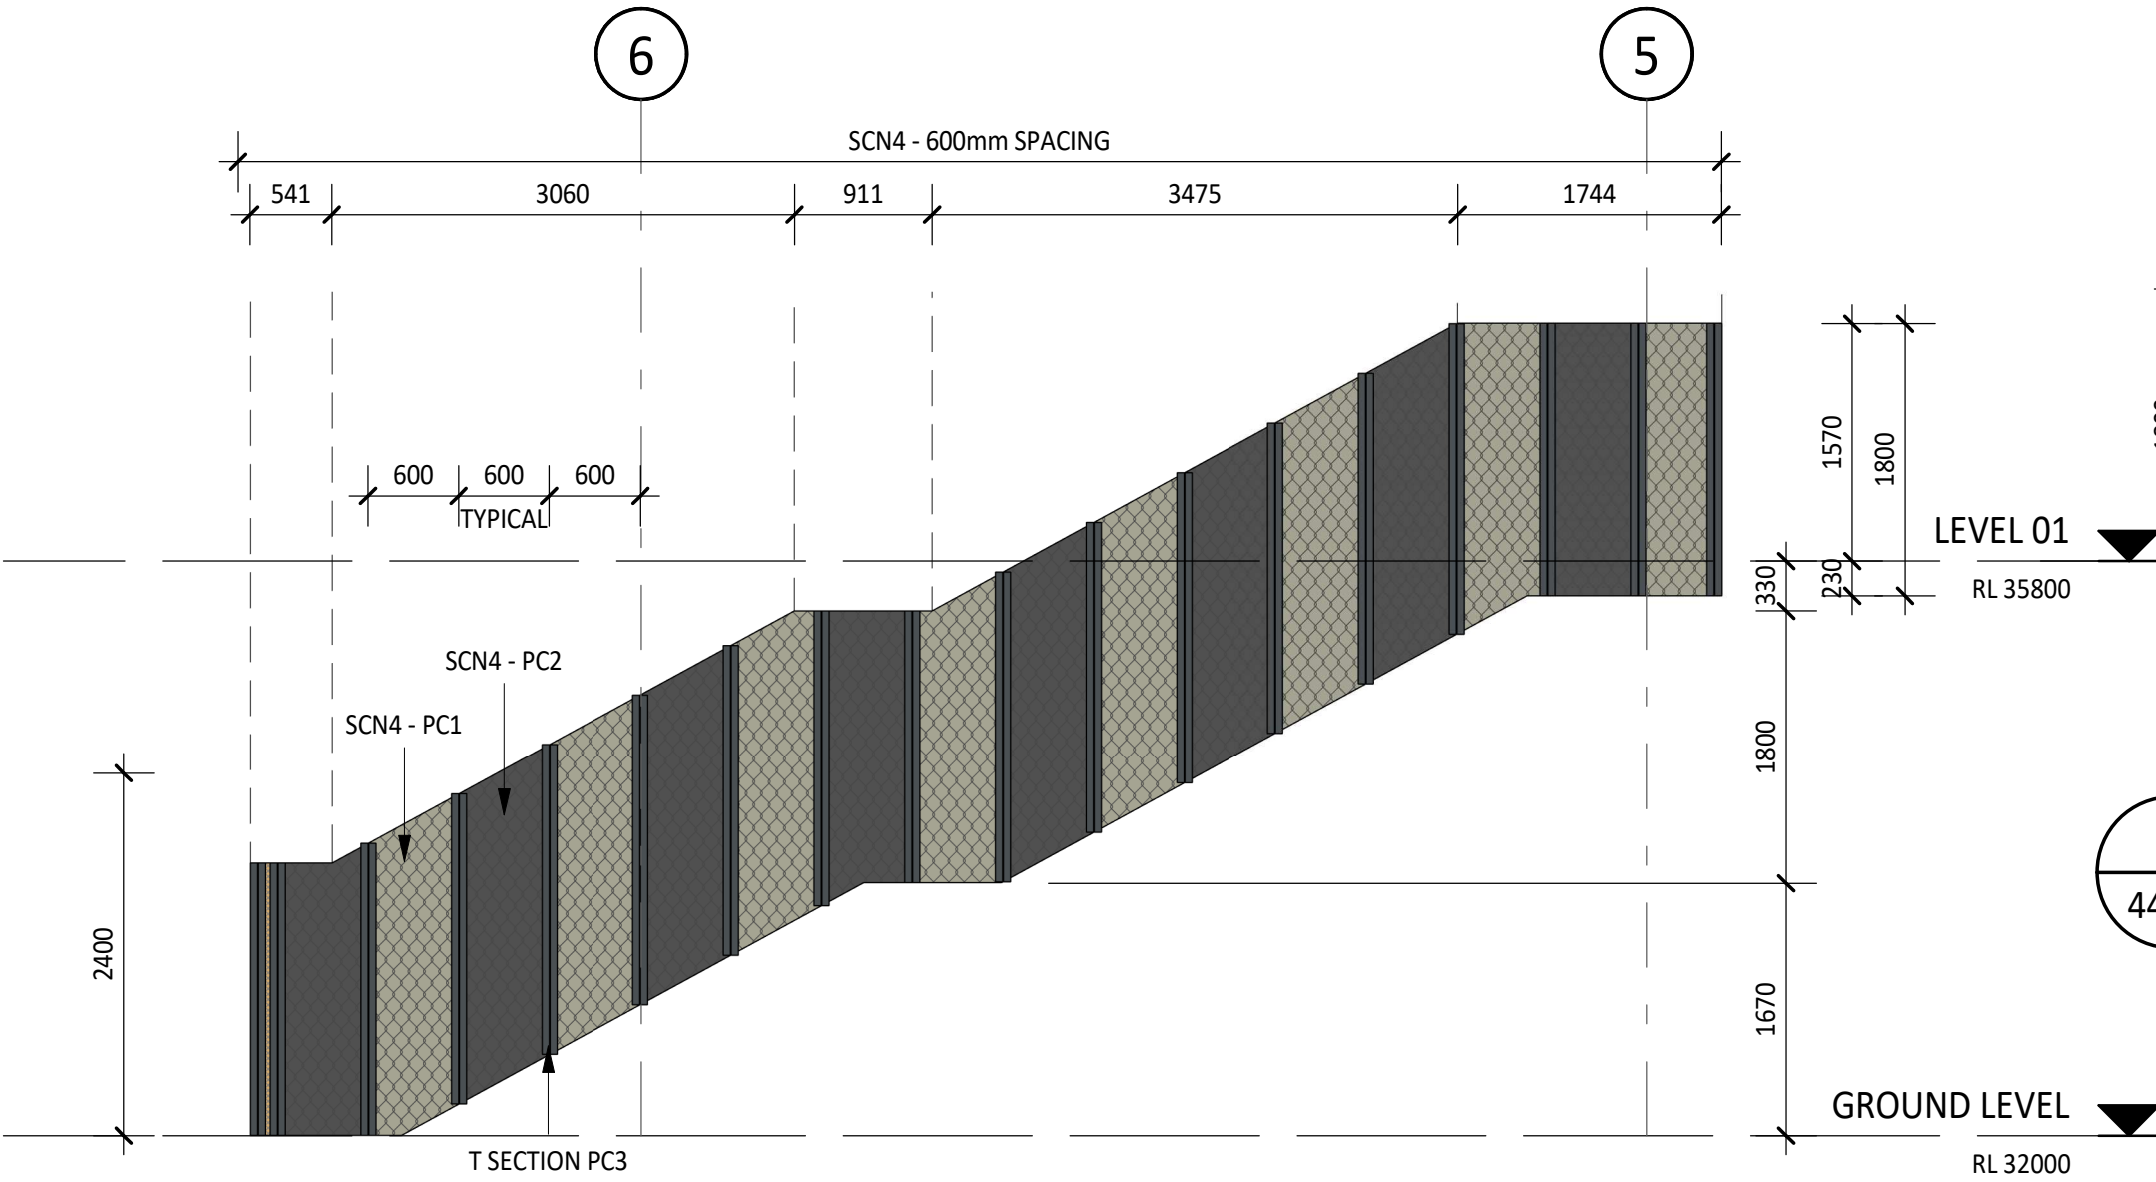


2 EXTERNAL STAIR SCREEN ELEVATION
44-02 1 : 50

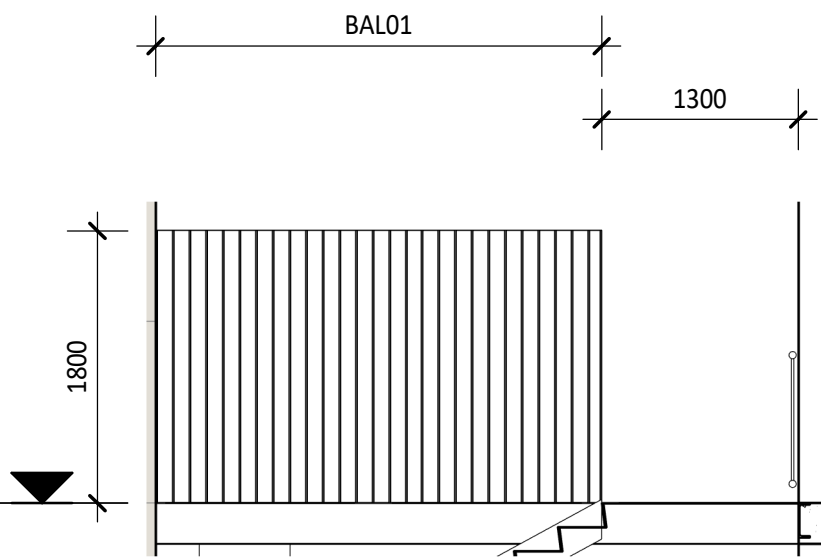


3 EXTERNAL STAIR SCREEN ELEVATION
44-03 1 : 50

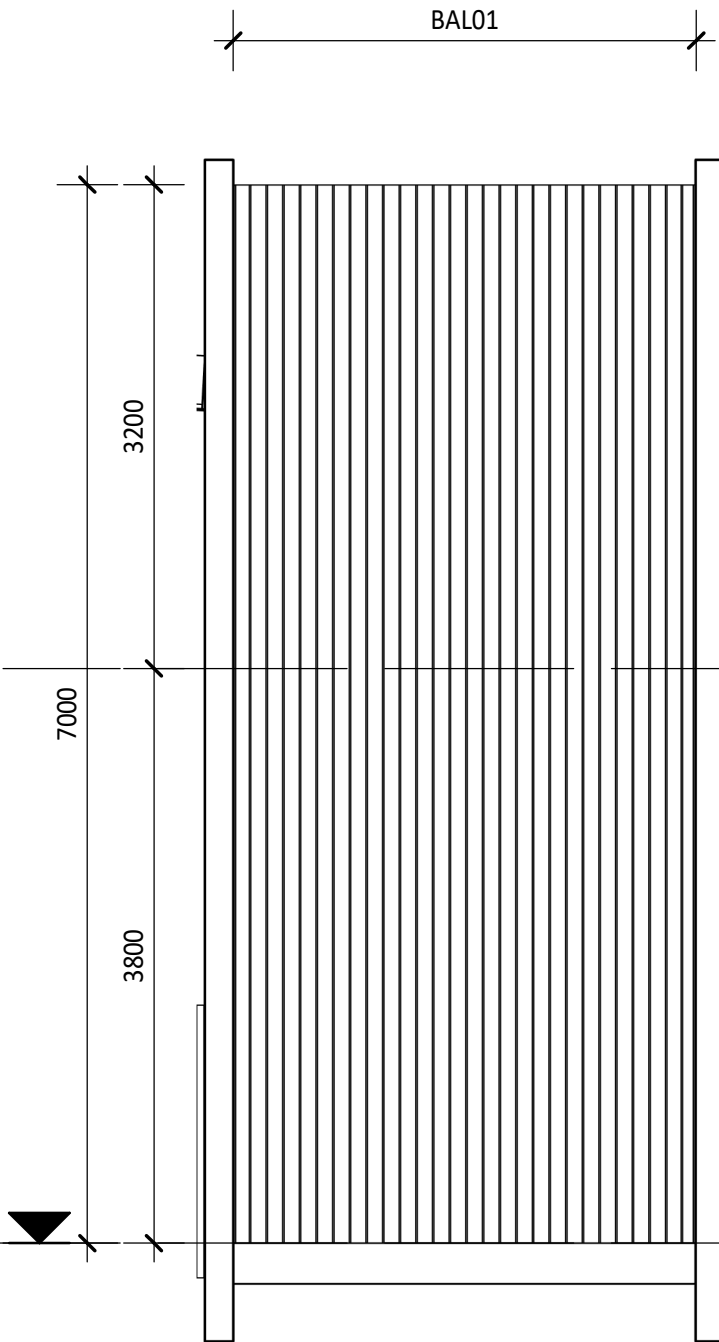

4 EXTERNAL STAIR SCREEN ELEVATION
44-03 1 : 50

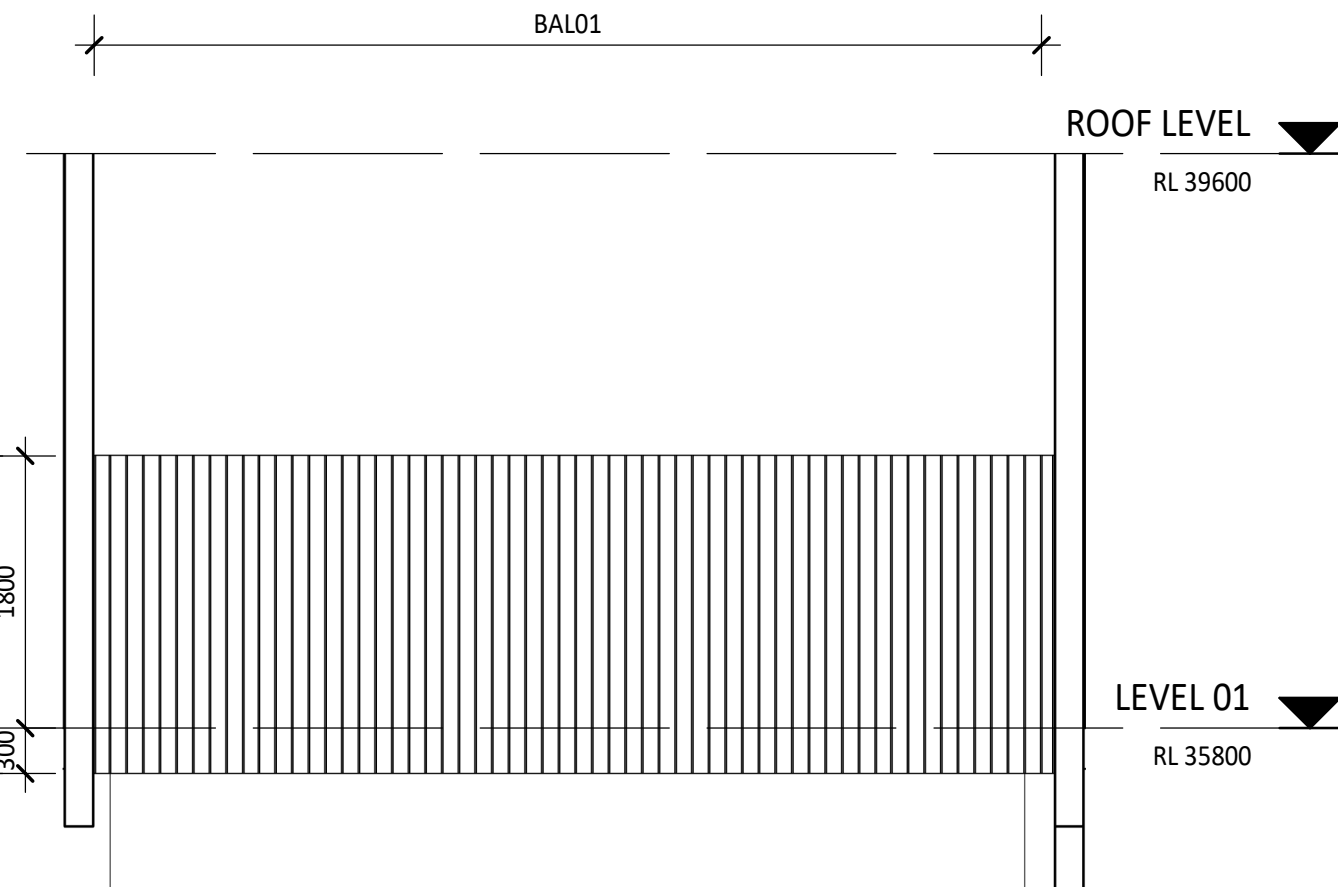

5 EXTERNAL STAIR SCREEN ELEVATION
44-03 1 : 50

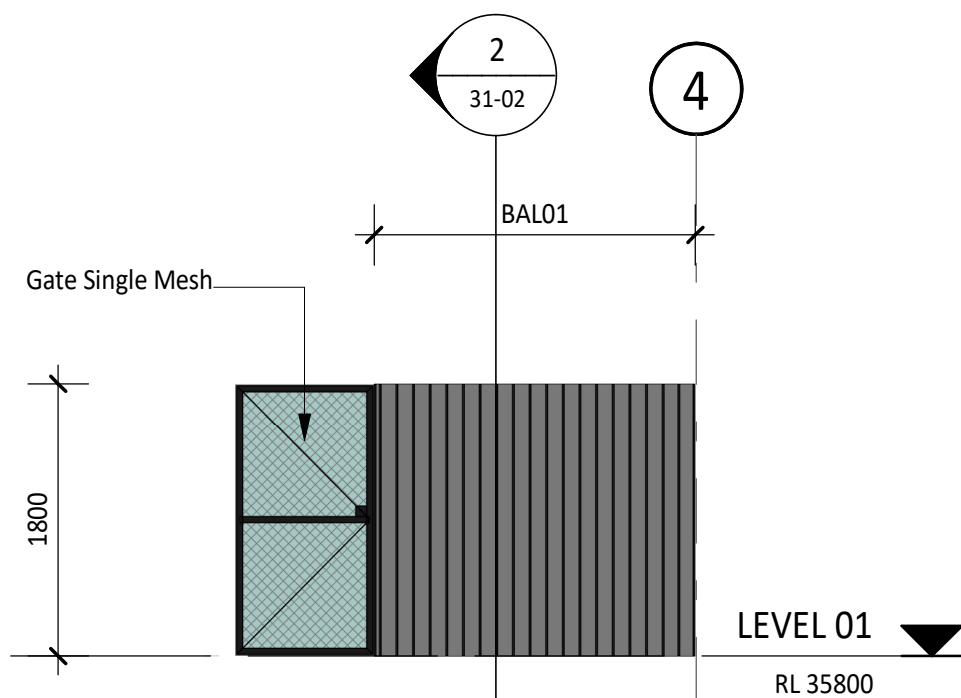

6 EXTERNAL STAIR SCREEN ELEVATION
44-03 1 : 50

ISSUED FOR TENDER

A	12/02/26	ISSUED FOR TENDER	BS
1	30/01/26	DRAFT 60% ISSUE	BS
rev	date	details	init.

drawn	date
PT	30/01/26
checked	date
BS	30/01/26
verified	date
BS	30/01/26

scale

SCREEN DETAILS

scale	project no.
As indicated @ A1	260018
revision	
A	
sheet no.	
CQU-ROK-092-00-ARC-44-03	