




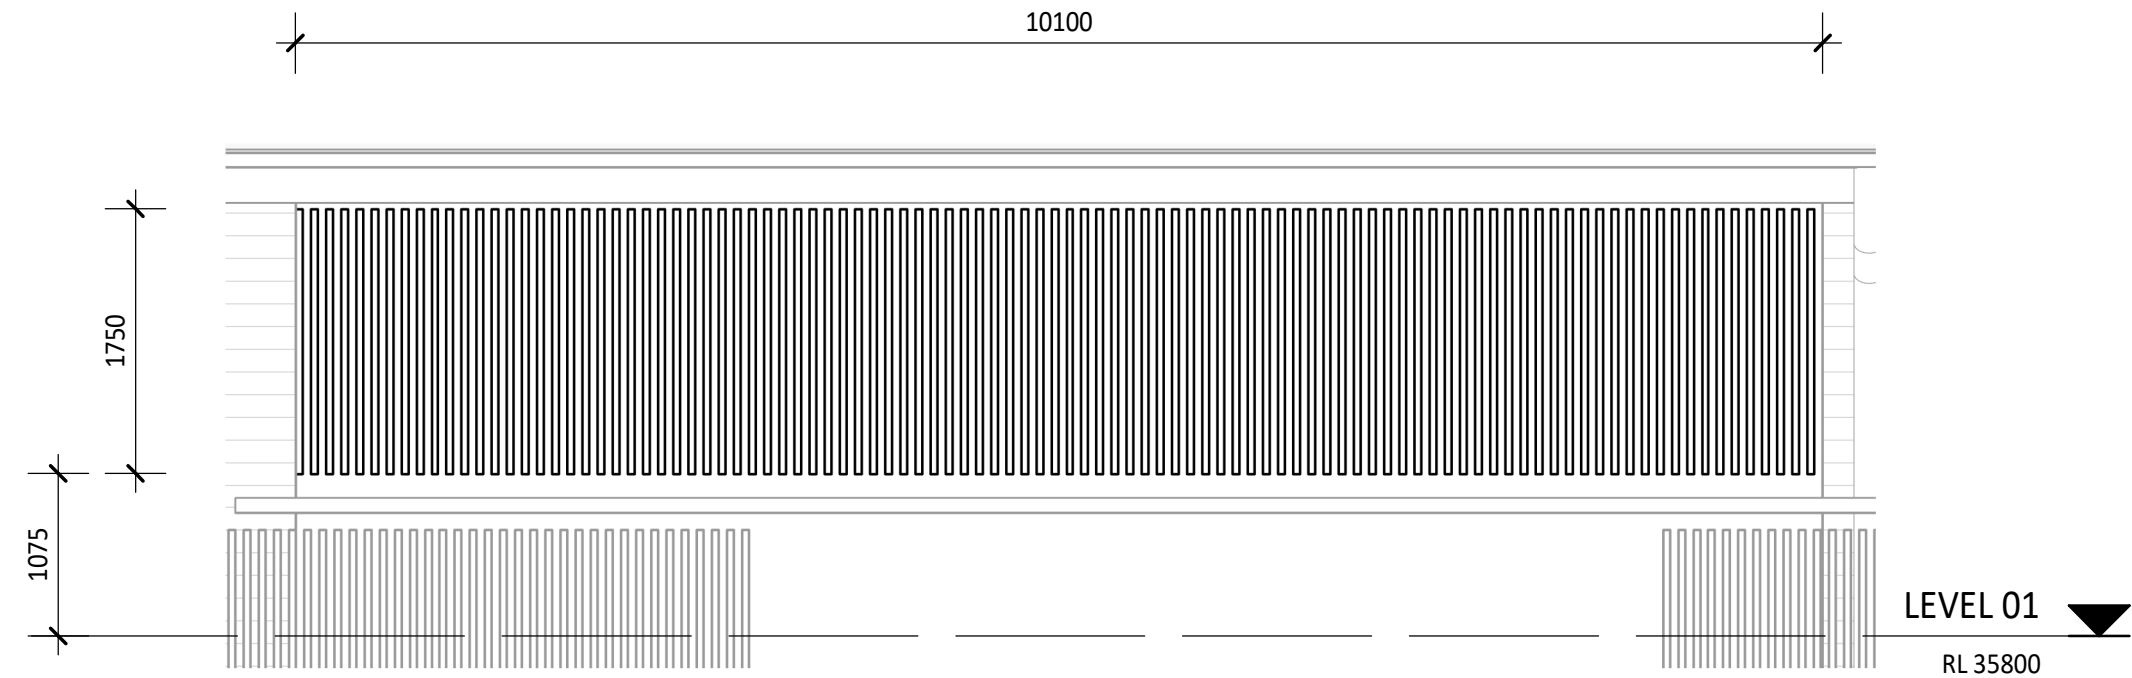

1 BATTEN 1 Copy 1
1 : 50

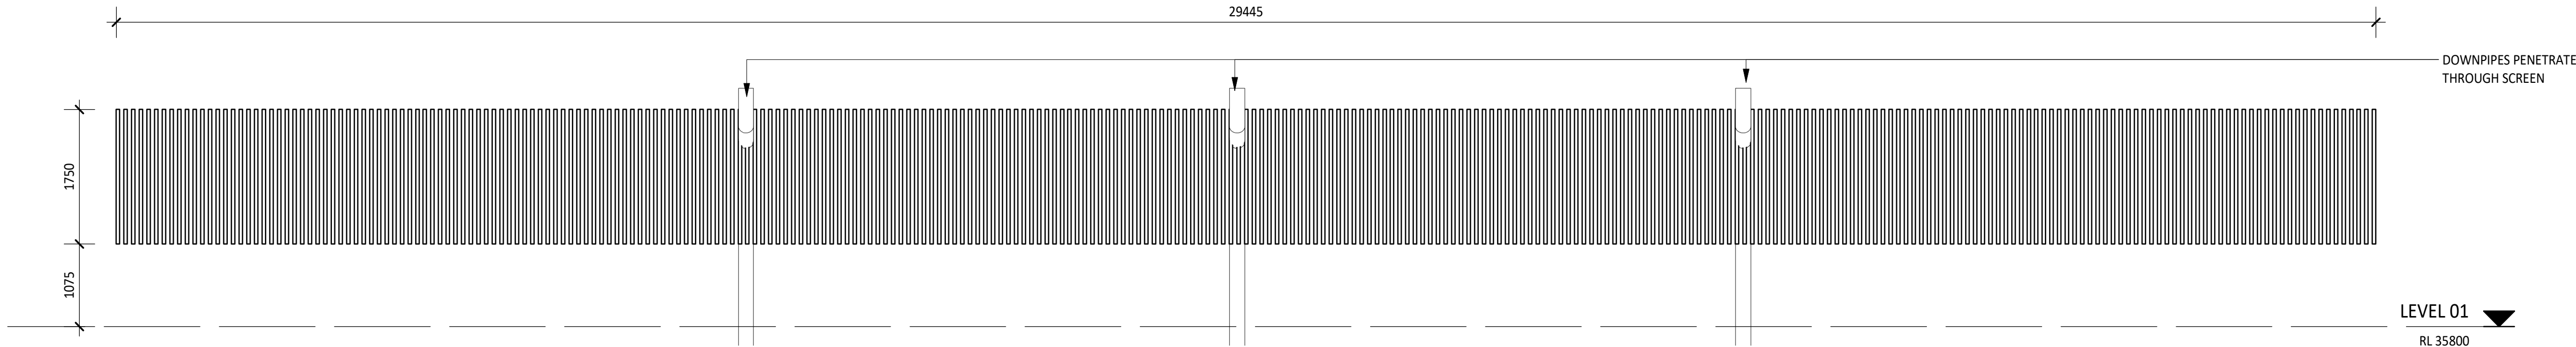


2 BATTEN 3 Copy 1
1 : 50

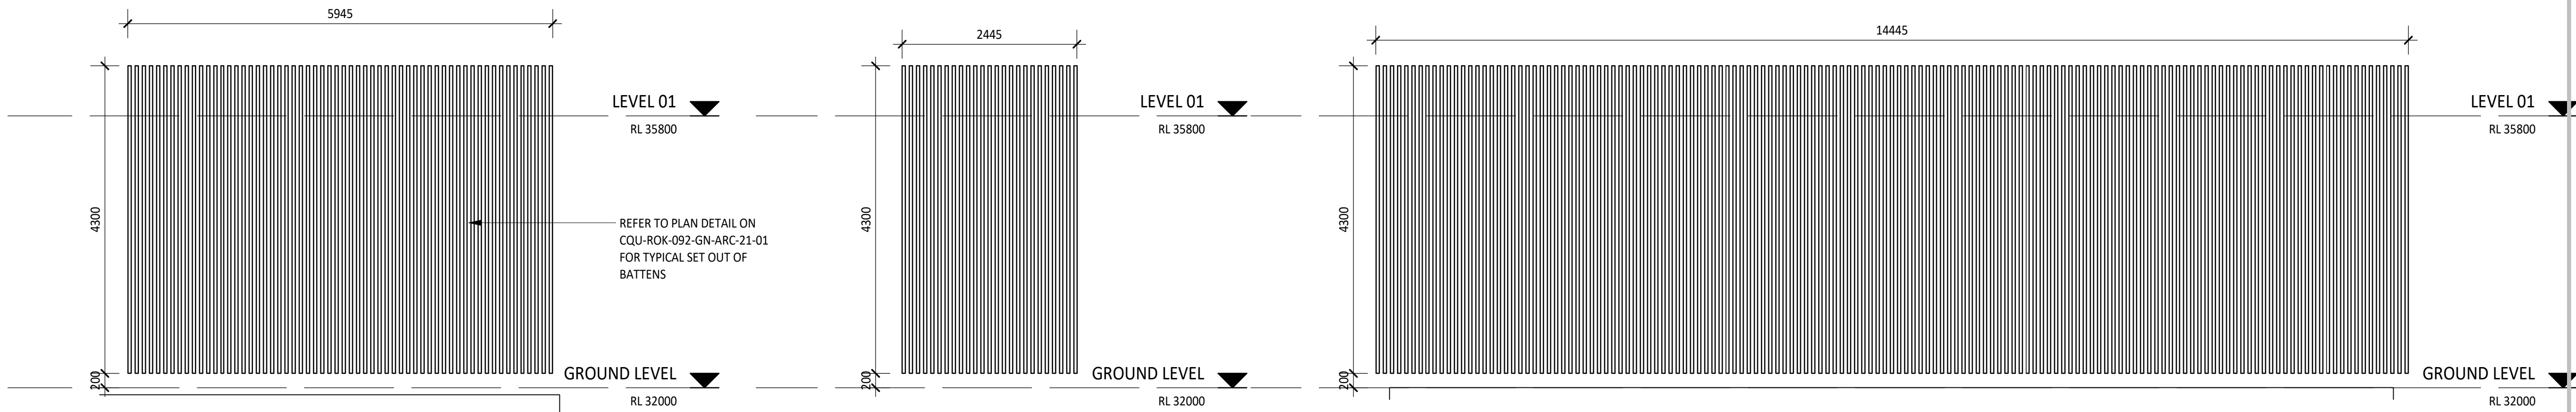


3 BATTEN 1
1 : 50

4 BATTEN 1 Copy 1 Copy 1
1 : 50

5 BATTEN 2
1 : 50

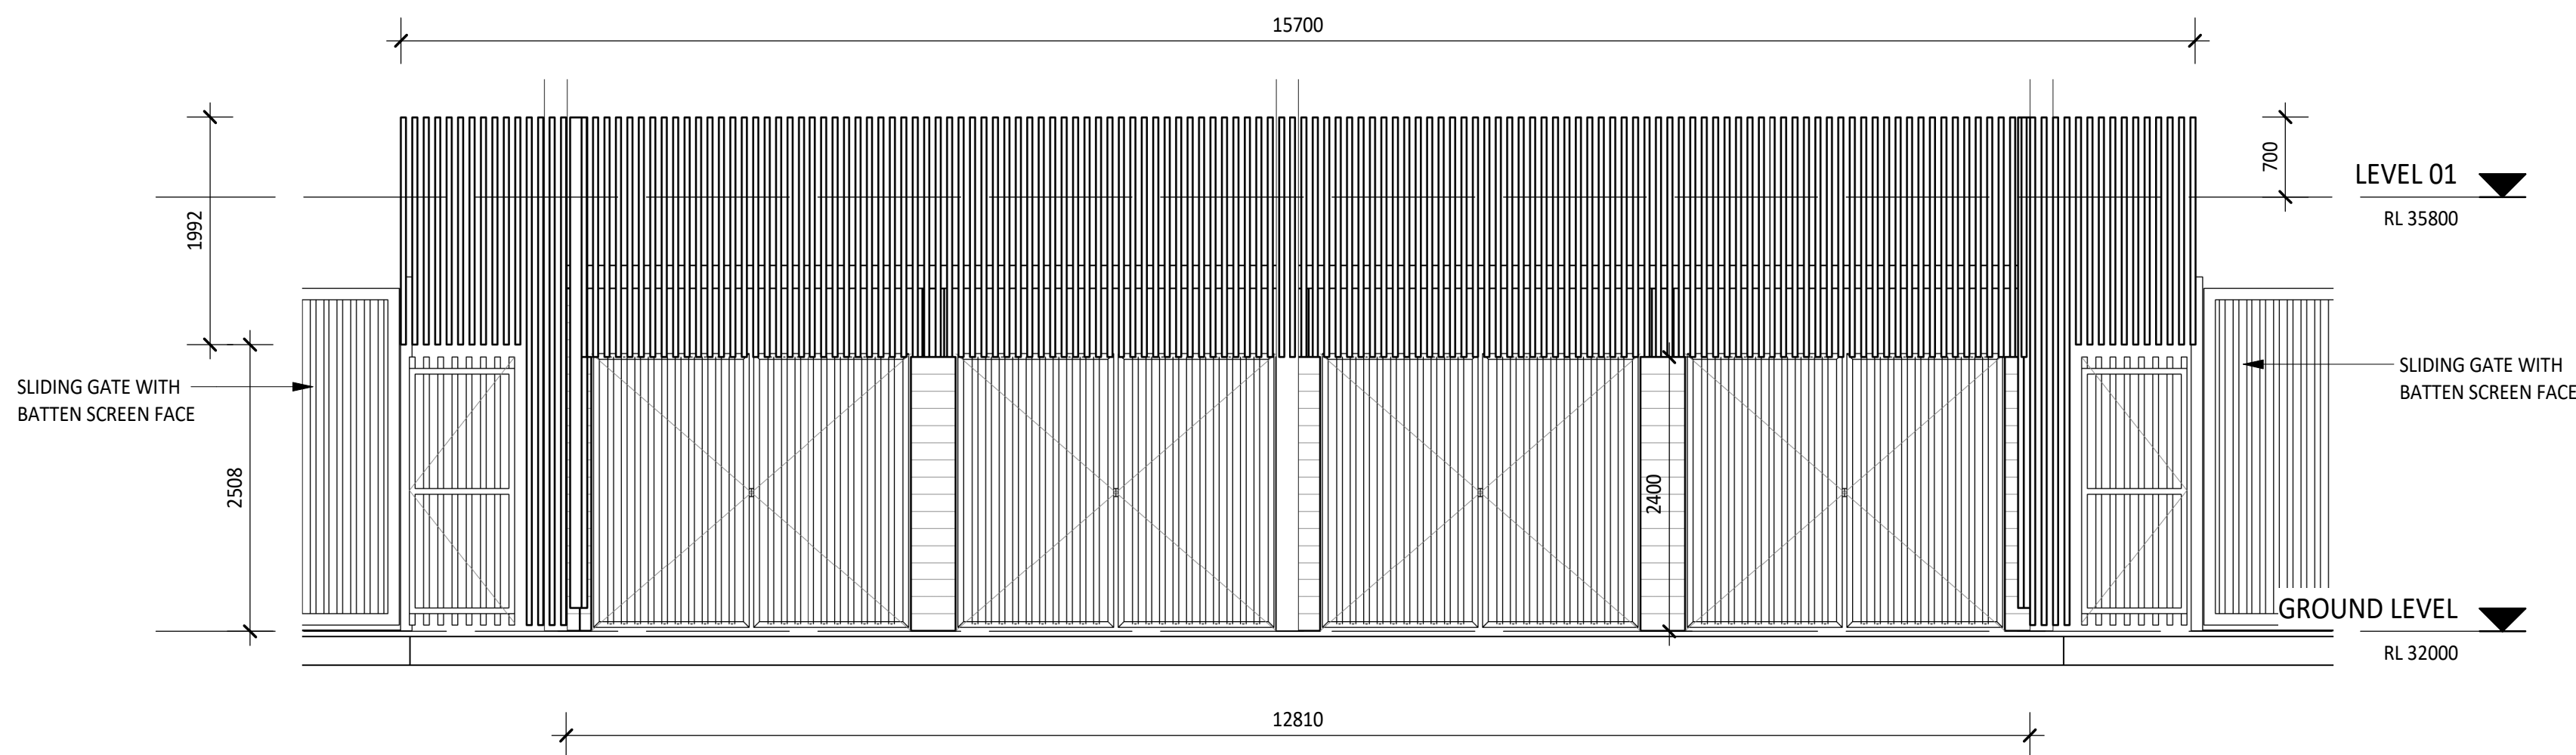

6 BATTEN 3
1 : 50

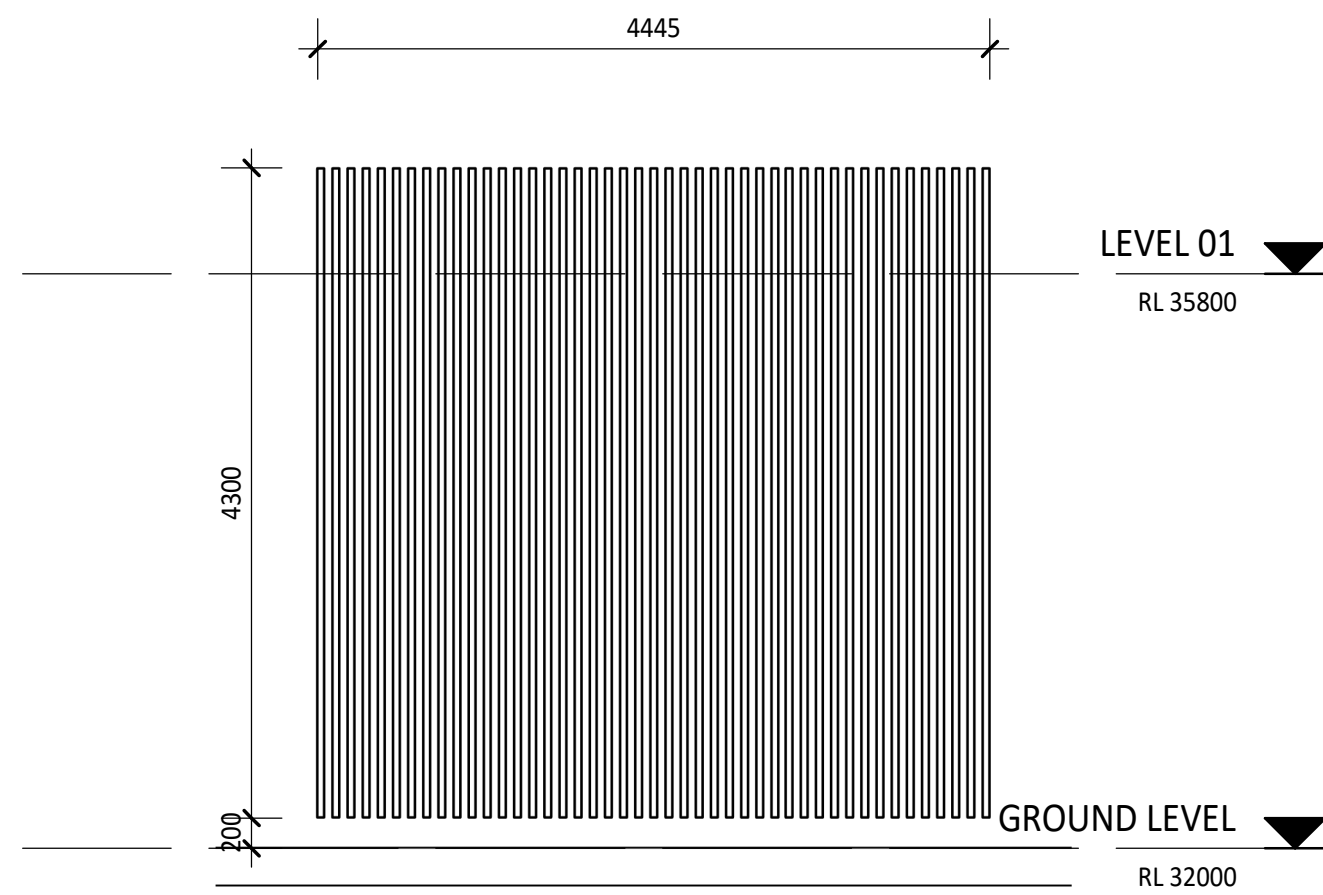

7 BATTEN 4
1 : 50

CQU ROCKHAMPTON TAFE CONSOLIDATION - STAGE 2

554/700 Yaamba Rd, Norman
Gardens QLD 4701

for



A	12/02/26	ISSUED FOR TENDER	BS
1	30/01/26	DRAFT 60% ISSUE	BS
rev/	date	details	init.

drawn	date
PT	30/01/26
checked	date
BS	30/01/26
verified	date
BS	30/01/26

scale

SCREEN DETAILS

scale	project no.
1 : 50 @ A1	260018

revision	
A	

sheet no.
CQU-ROK-092-00-ARC-44-04

ISSUED FOR TENDER