




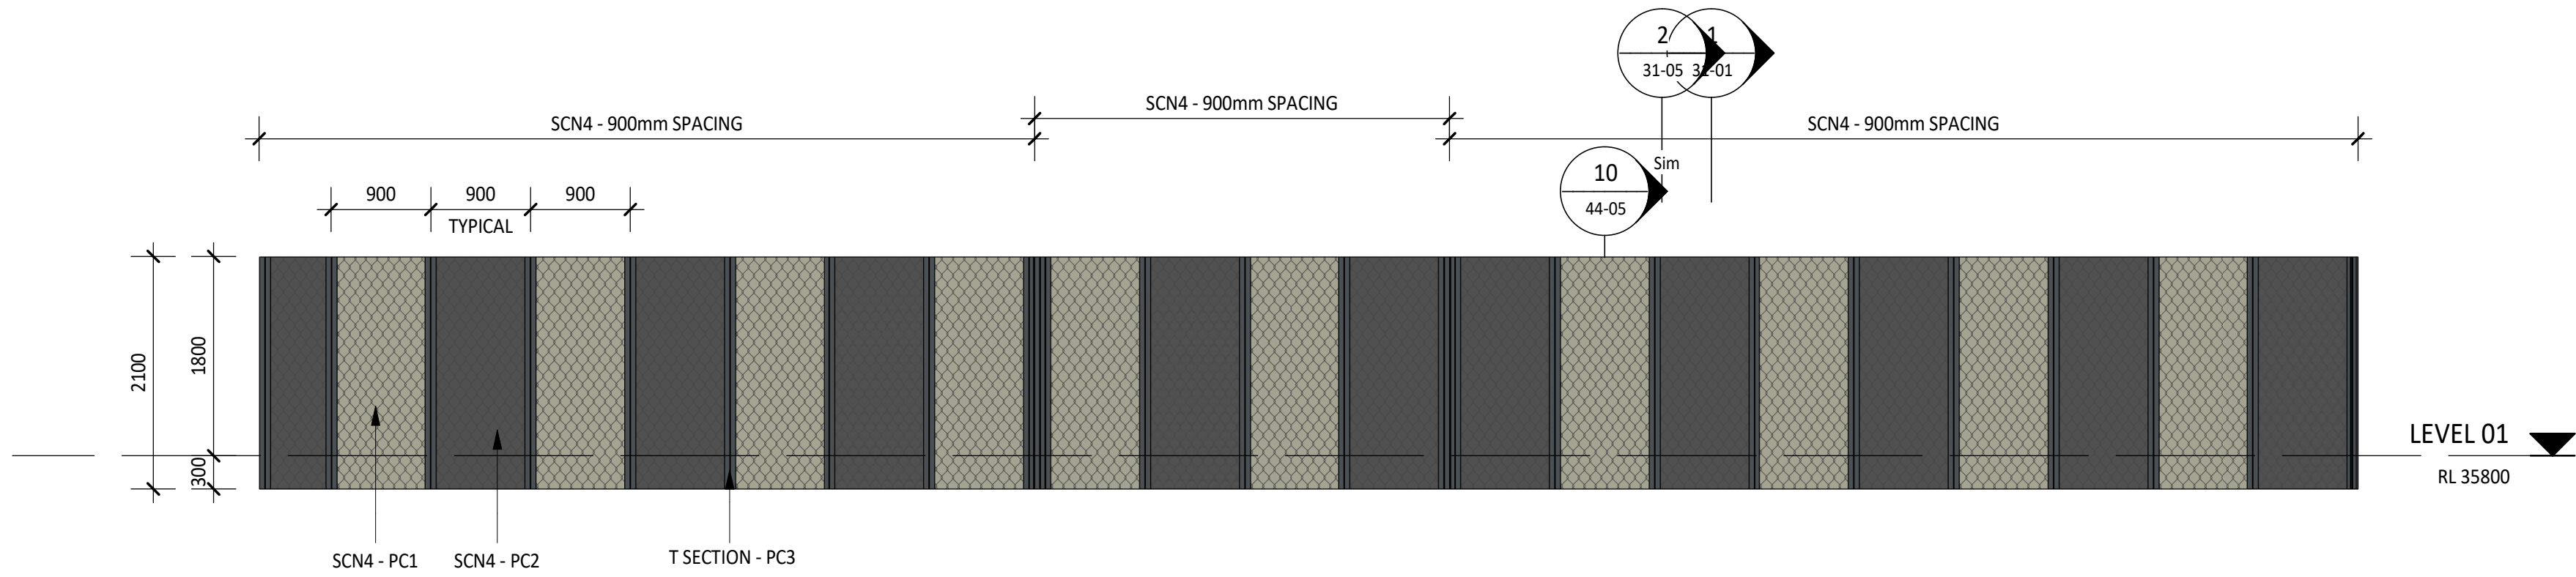


2 REFRIGERATION WORKSHOP BALCONY SCREEN
44-05 1 : 50

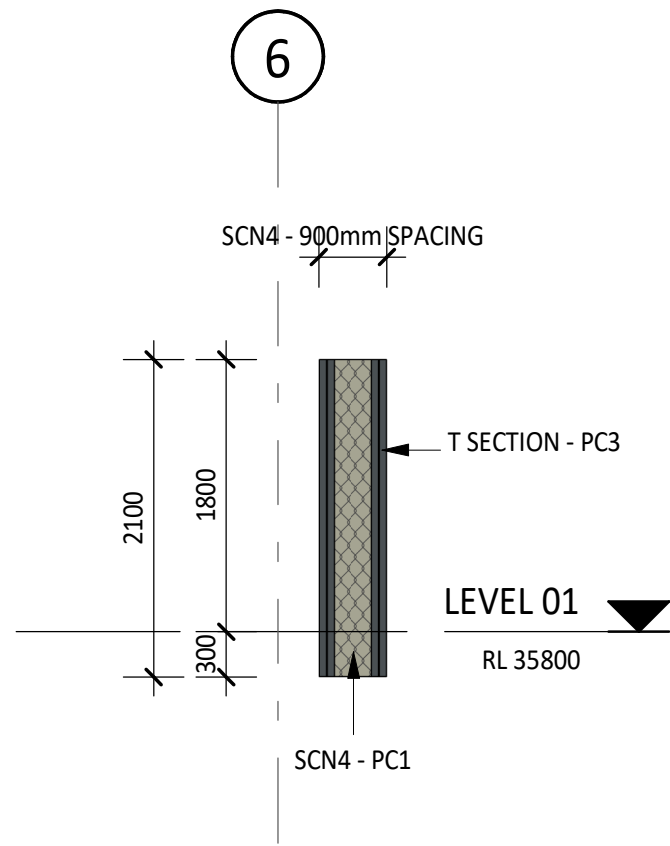


3 REFRIGERATION WORKSHOP BALCONY SCREEN
44-05 1 : 50

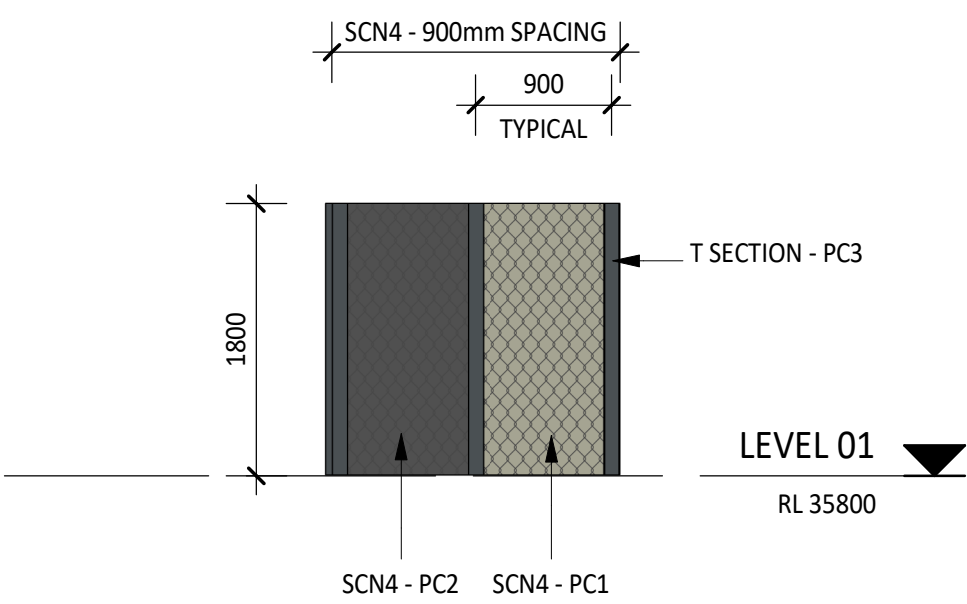


5 REFRIGERATION WORKSHOP BALCONY SCREEN
44-05 1 : 50

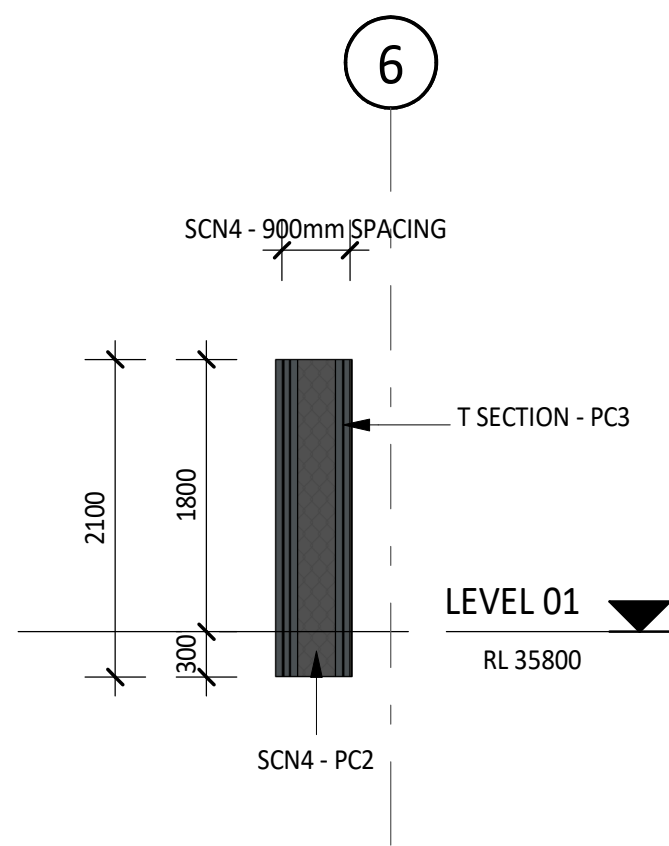


4 REFRIGERATION WORKSHOP BALCONY SCREEN
44-05 1 : 50

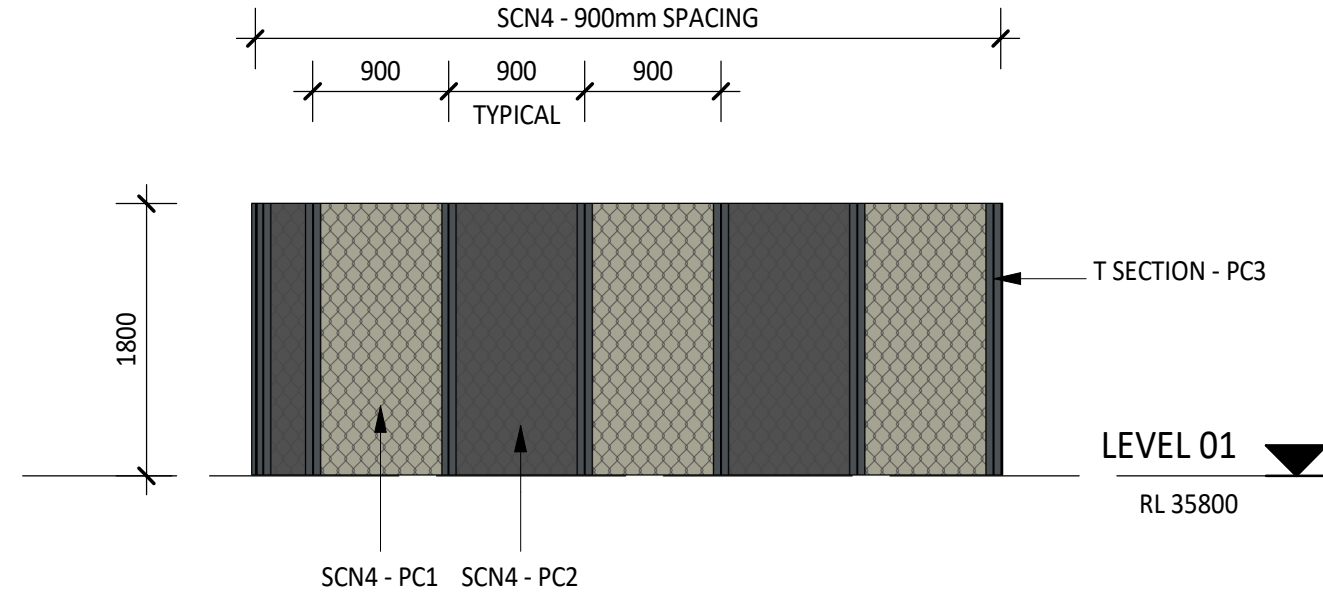


6 REFRIGERATION WORKSHOP BALCONY SCREEN
44-05 1 : 50

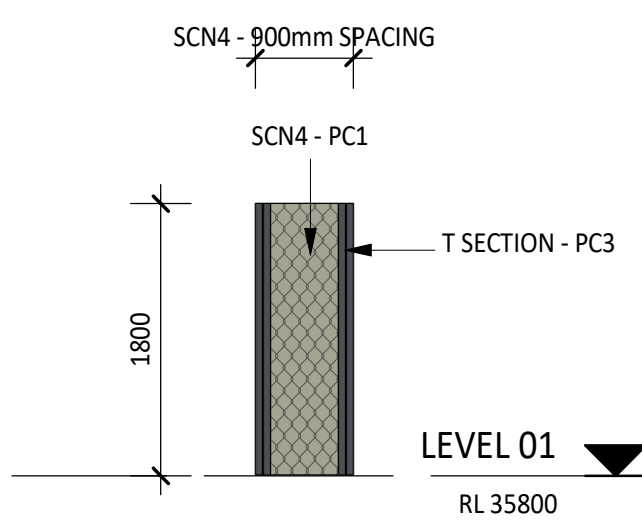

7 REFRIGERATION WORKSHOP BALCONY SCREEN
44-05 1 : 50

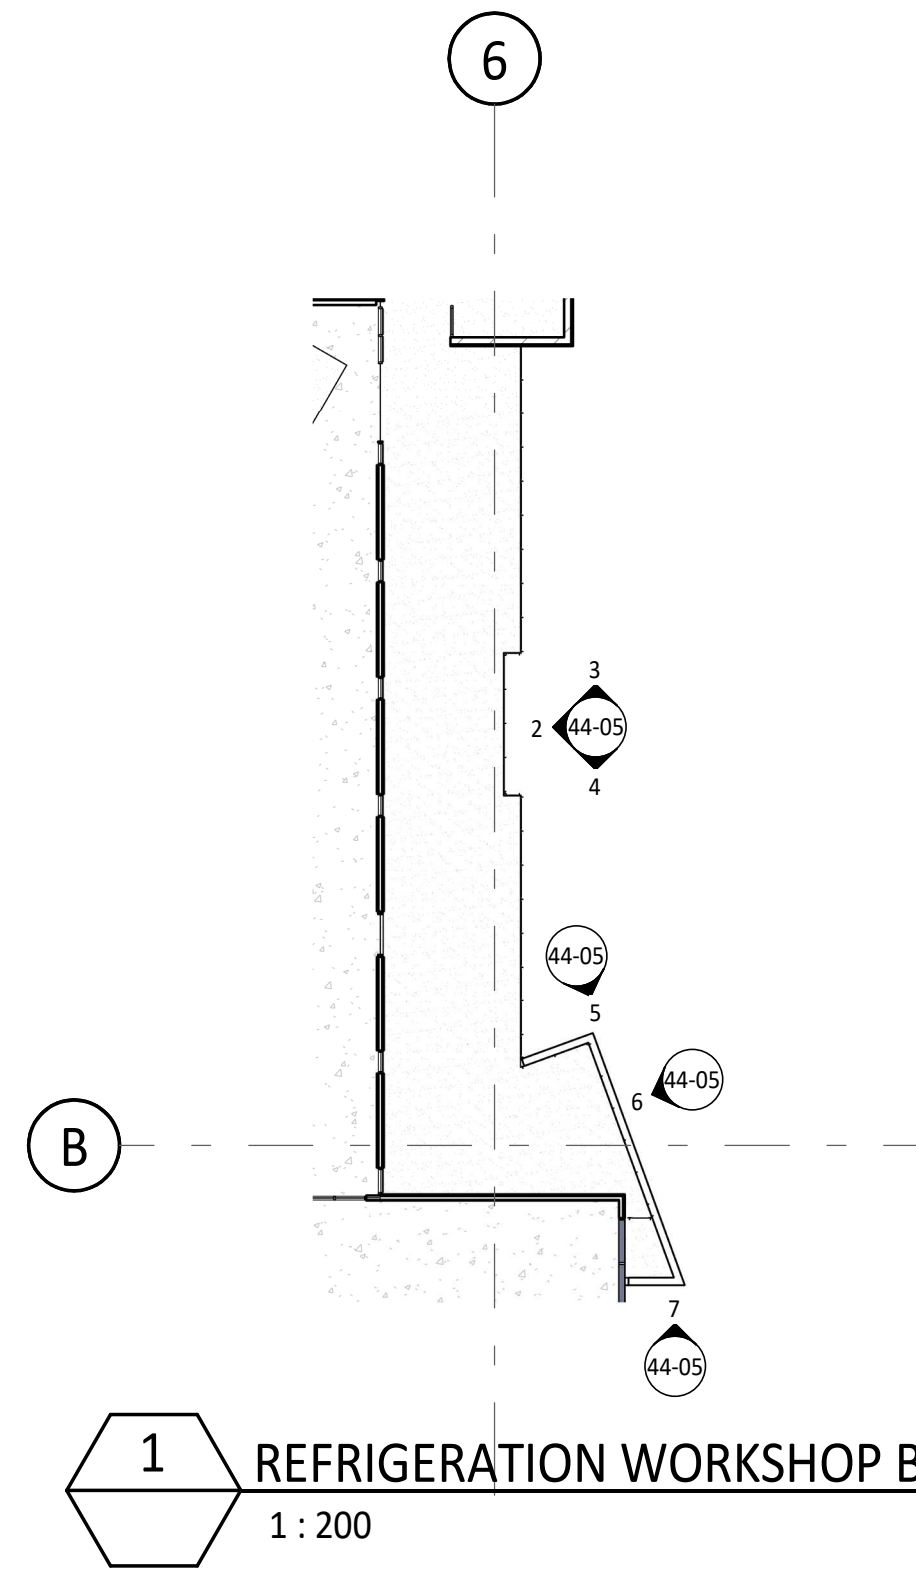

1 REFRIGERATION WORKSHOP BALCONY SCREEN PLAN
1 : 200

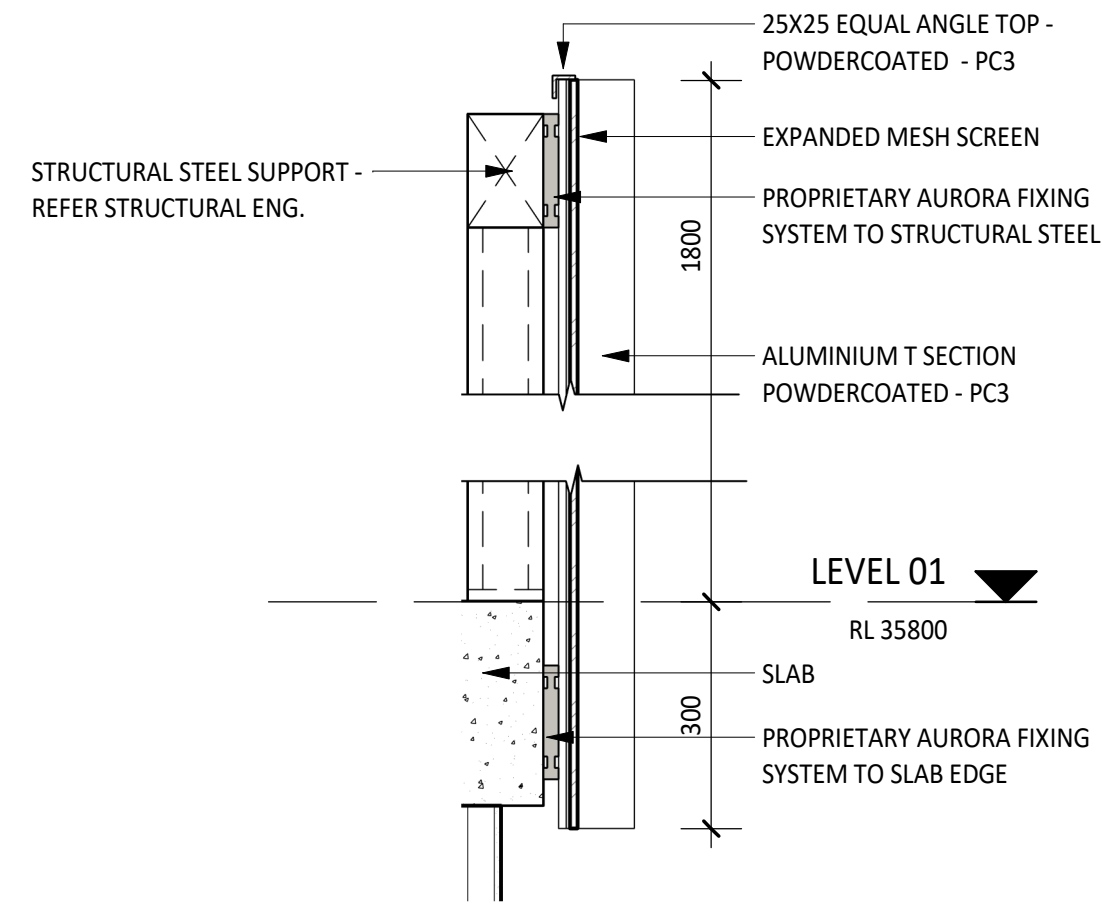

10 DETAIL SCN4 BALUSTRADE - TYPICAL SECTION
44-05 1 : 10

ISSUED FOR TENDER

© Copyright
These drawings and designs and the copyright thereof are the property of Thomson Adsett Pty Ltd and must not be used, retained or copied without written permission of Thomson Adsett Pty Ltd. ABN 76 105 314 654 Trading as ThomsonAdsett. Dimensions take precedence over scaling. Do not measure off drawings as print sizes may vary

**CQU ROCKHAMPTON
TAFE
CONSOLIDATION -
STAGE 2**

554/700 Yaamba Rd, Norman
Gardens QLD 4701



A	12/02/26	ISSUED FOR TENDER	BS
1	30/01/26	DRAFT 60% ISSUE	BS
rev/	date	details	init.

drawn	date
PT	30/01/26
checked	date
BS	30/01/26
verified	date
BS	30/01/26

scale

1

SCREEN DETAILS

scale project no.
As indicated @ A1 260018

revision
A

sheet no.
CQU-ROK-092-00-ARC-44-05