
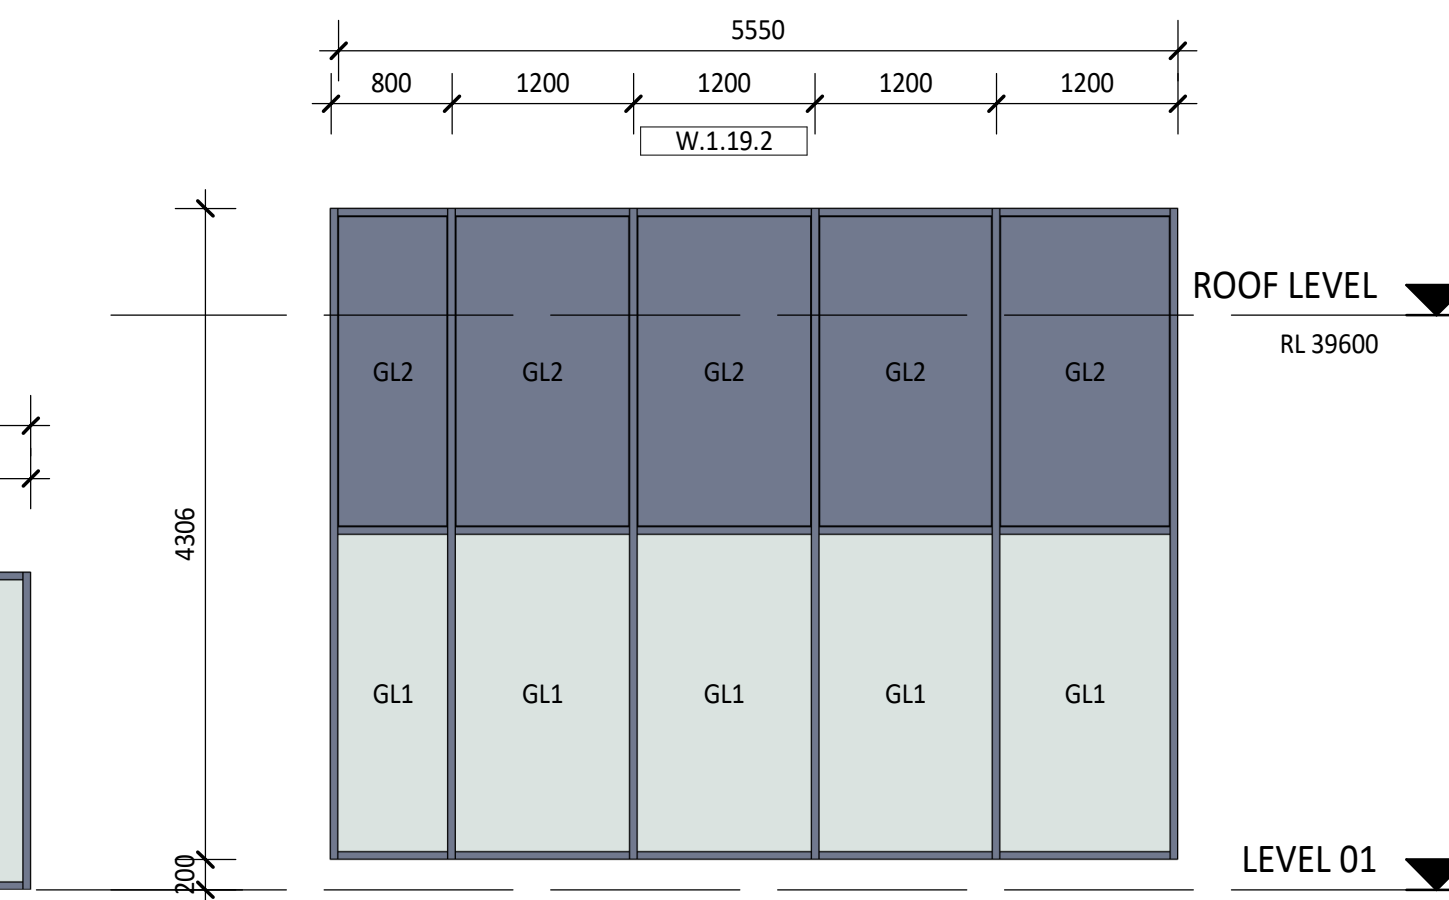
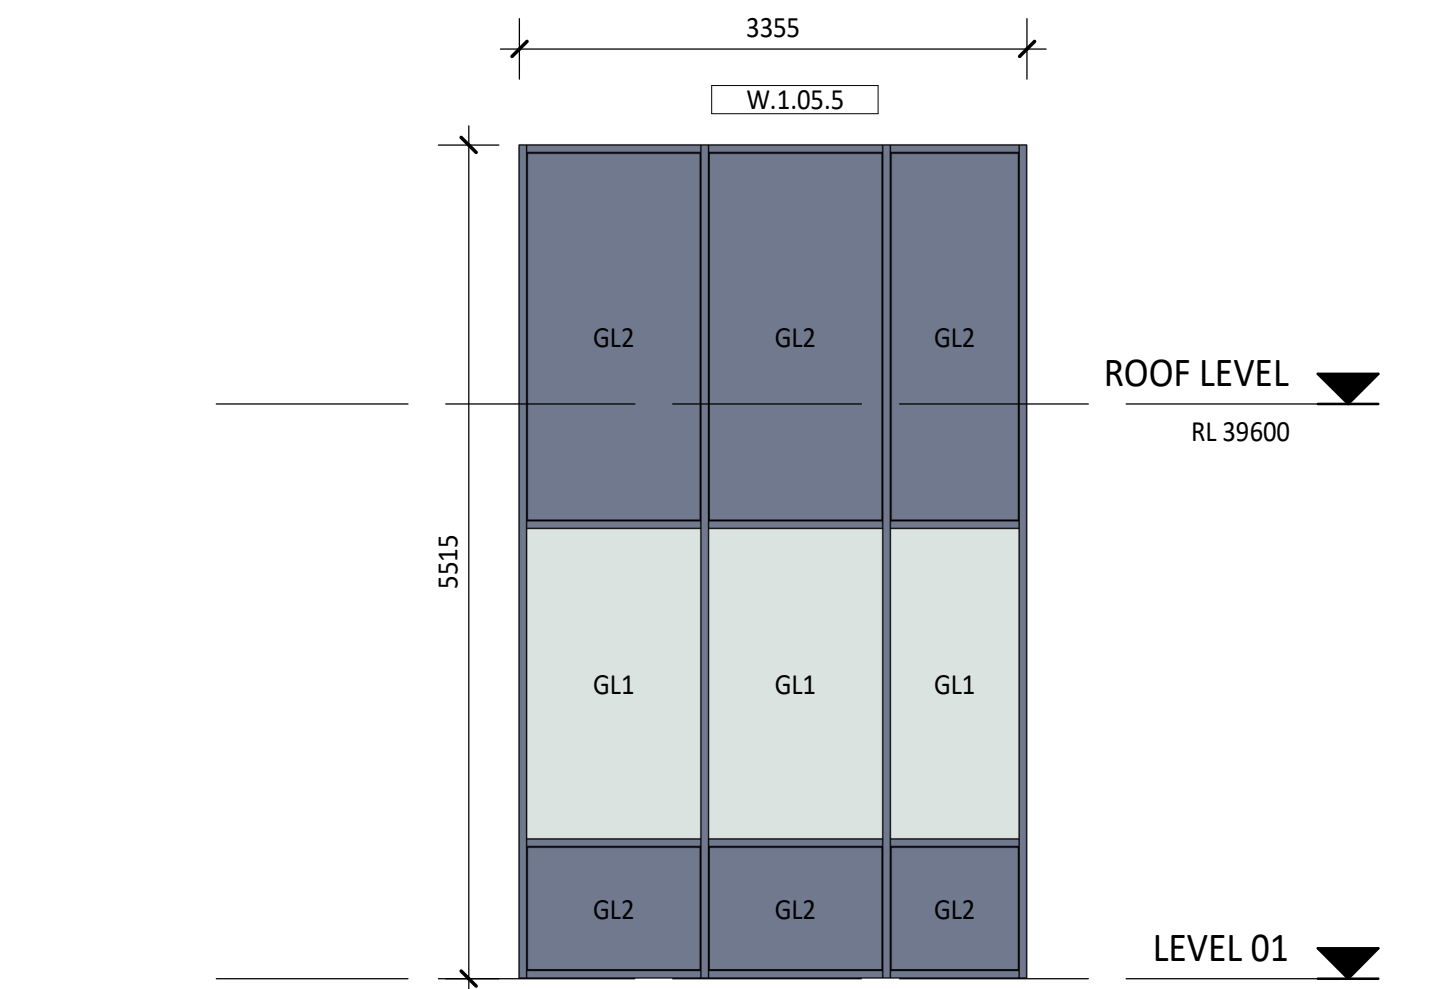
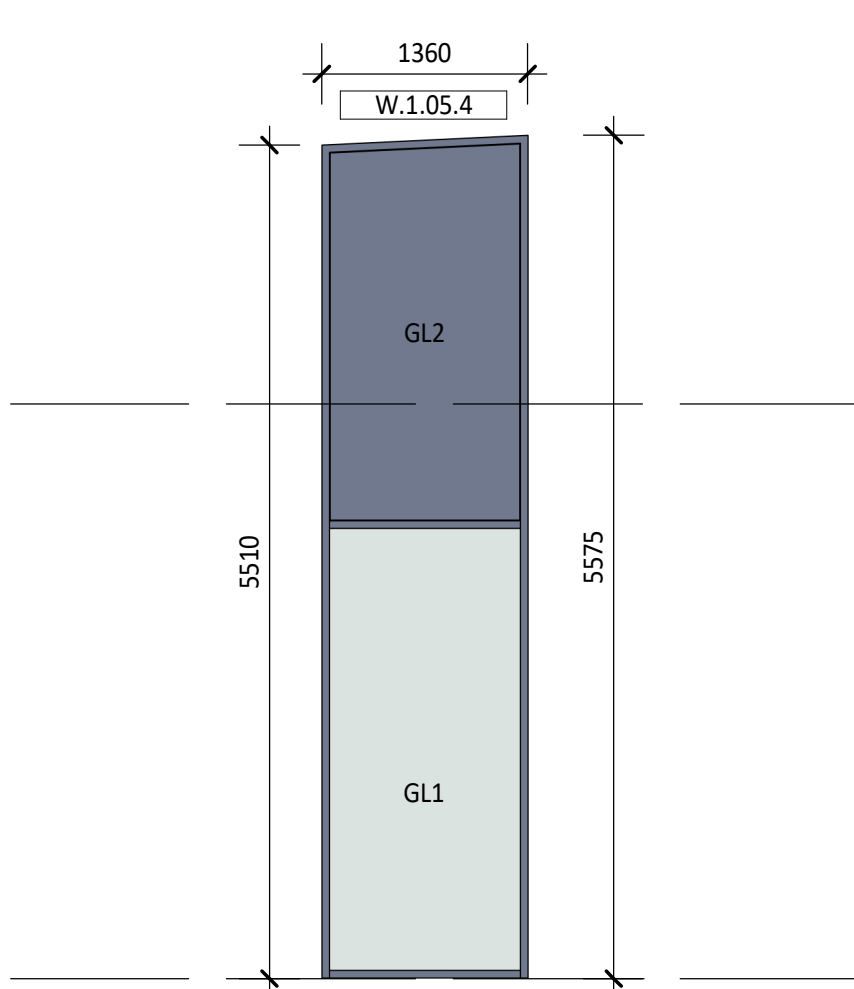
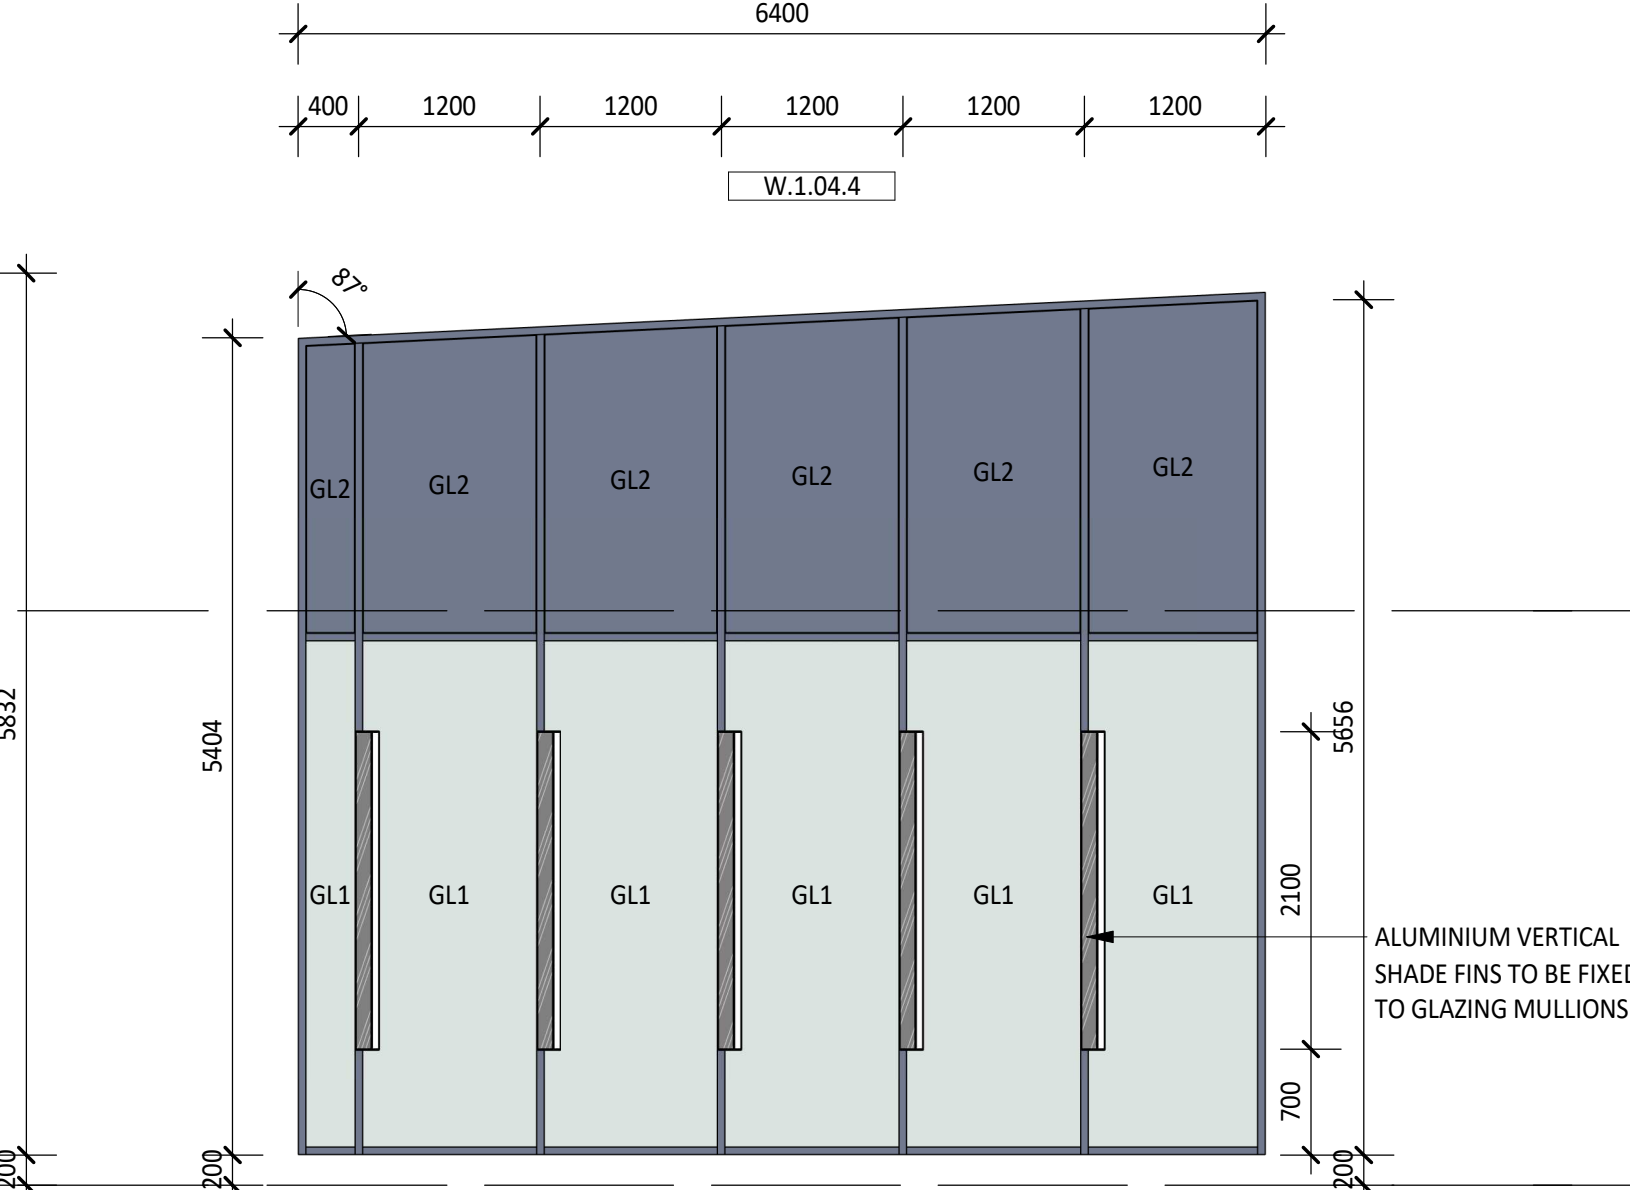
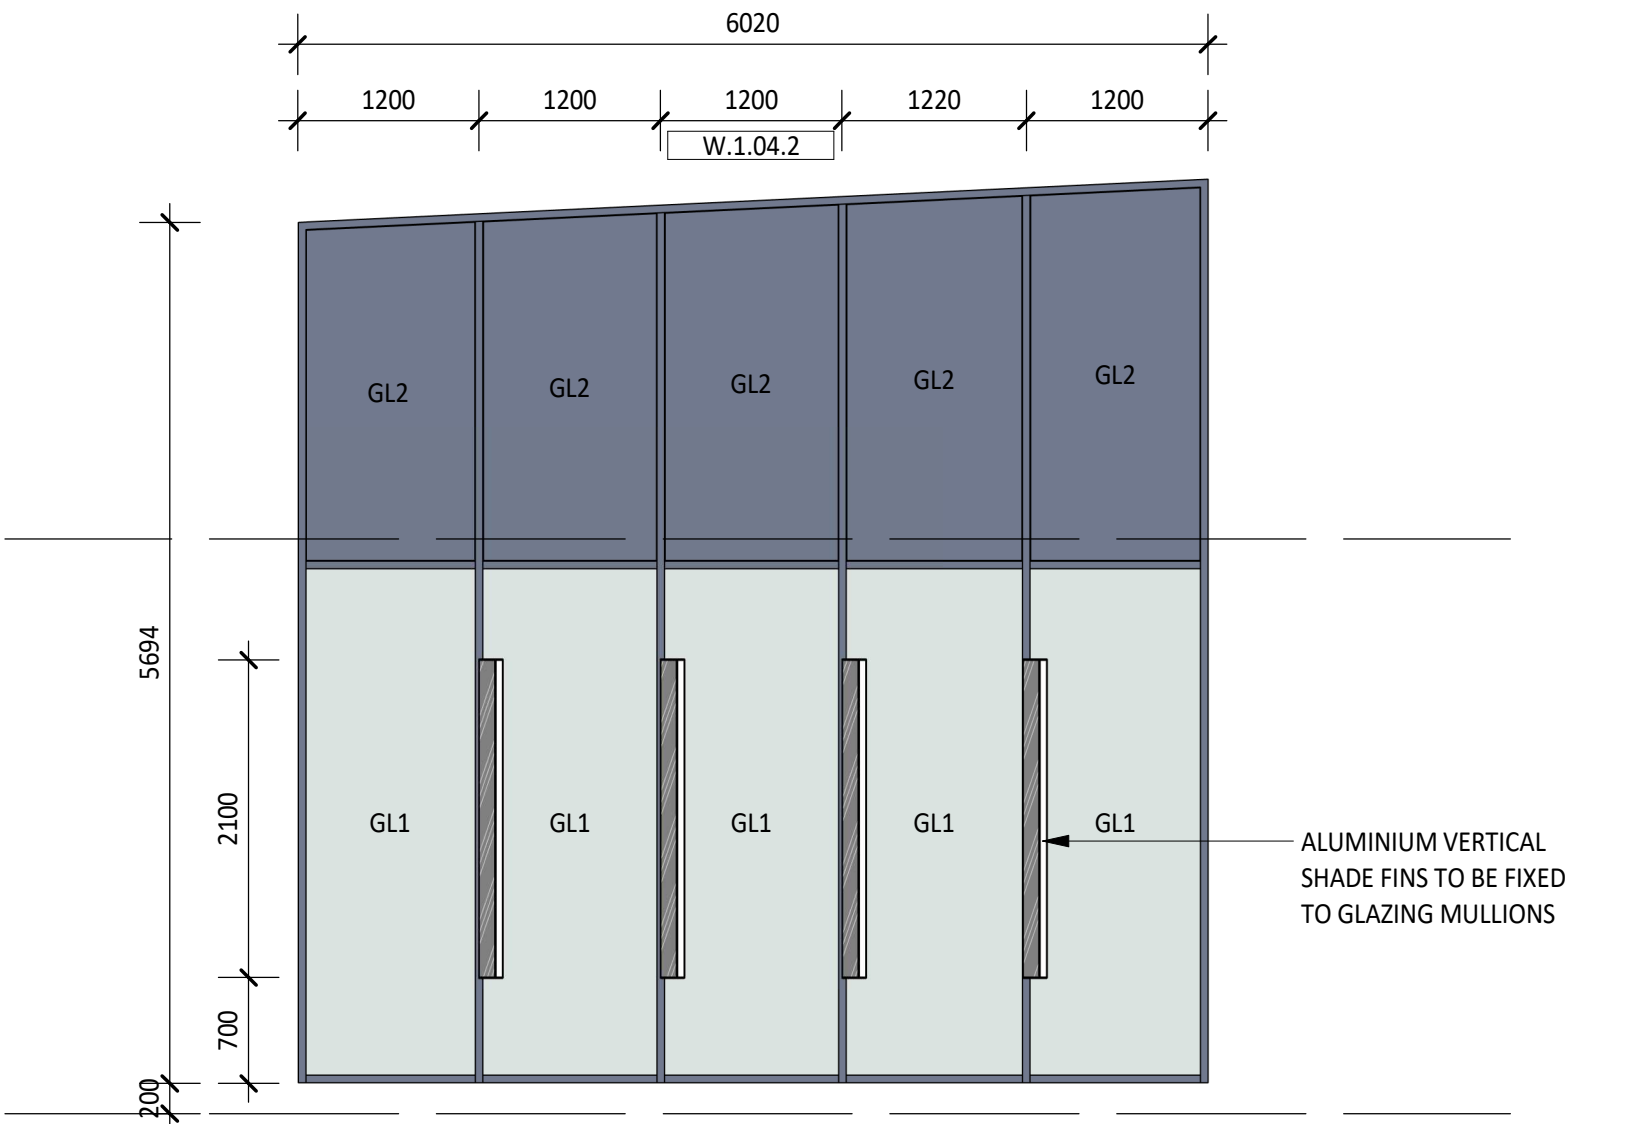
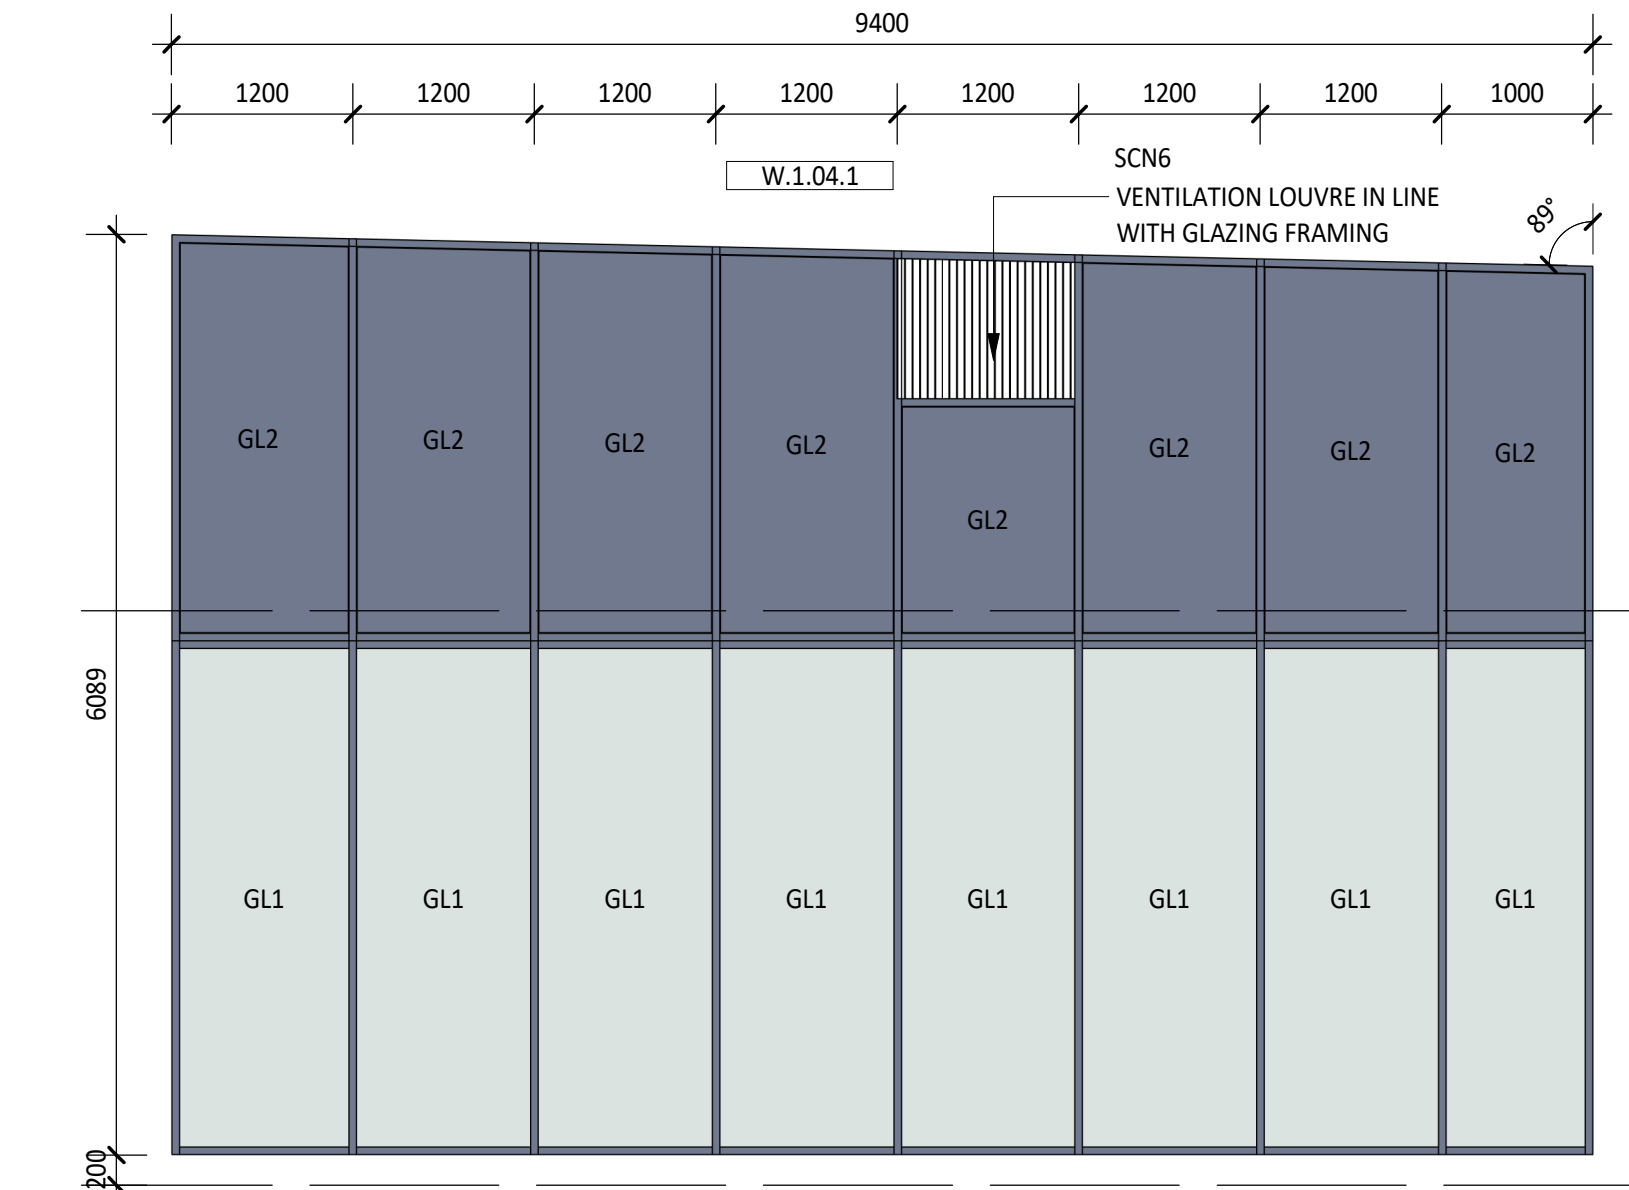
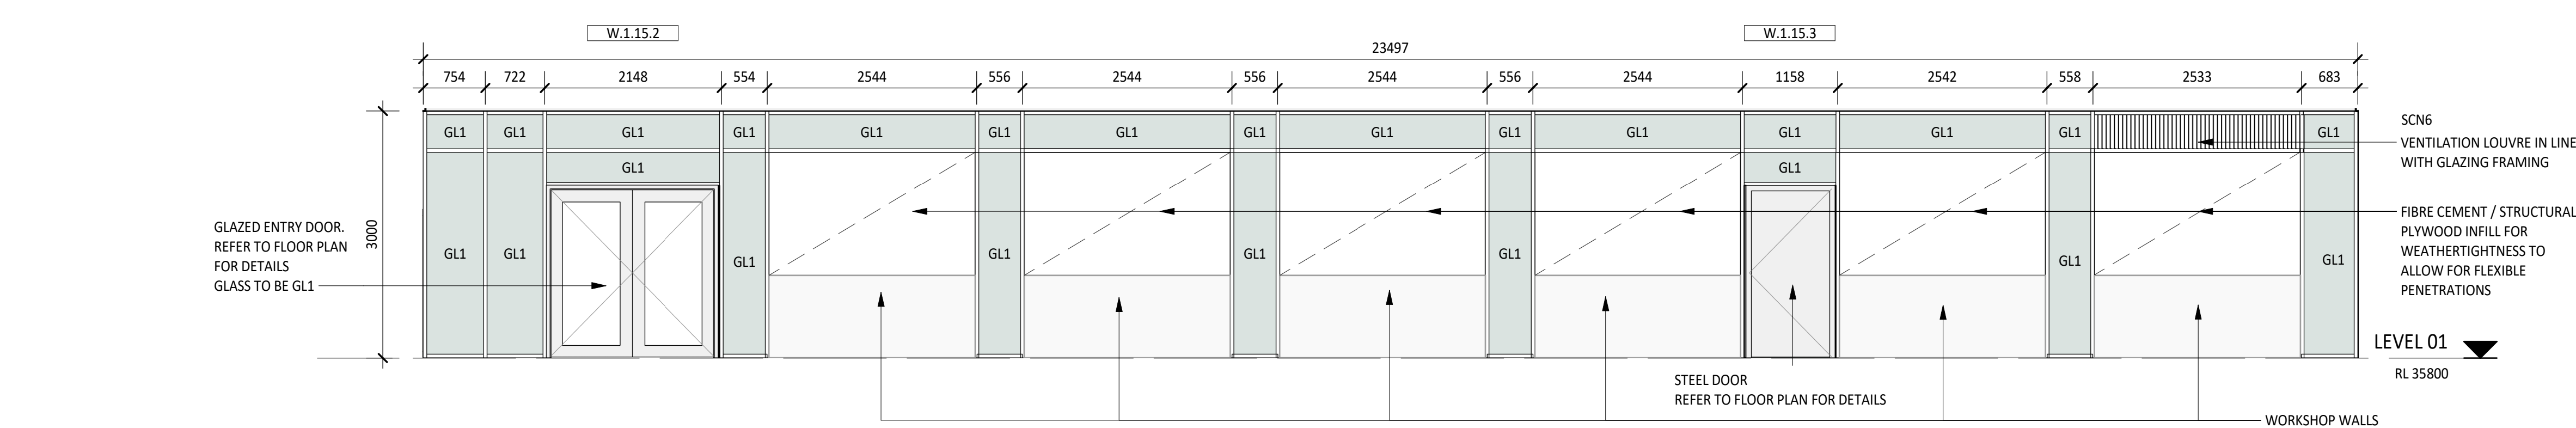
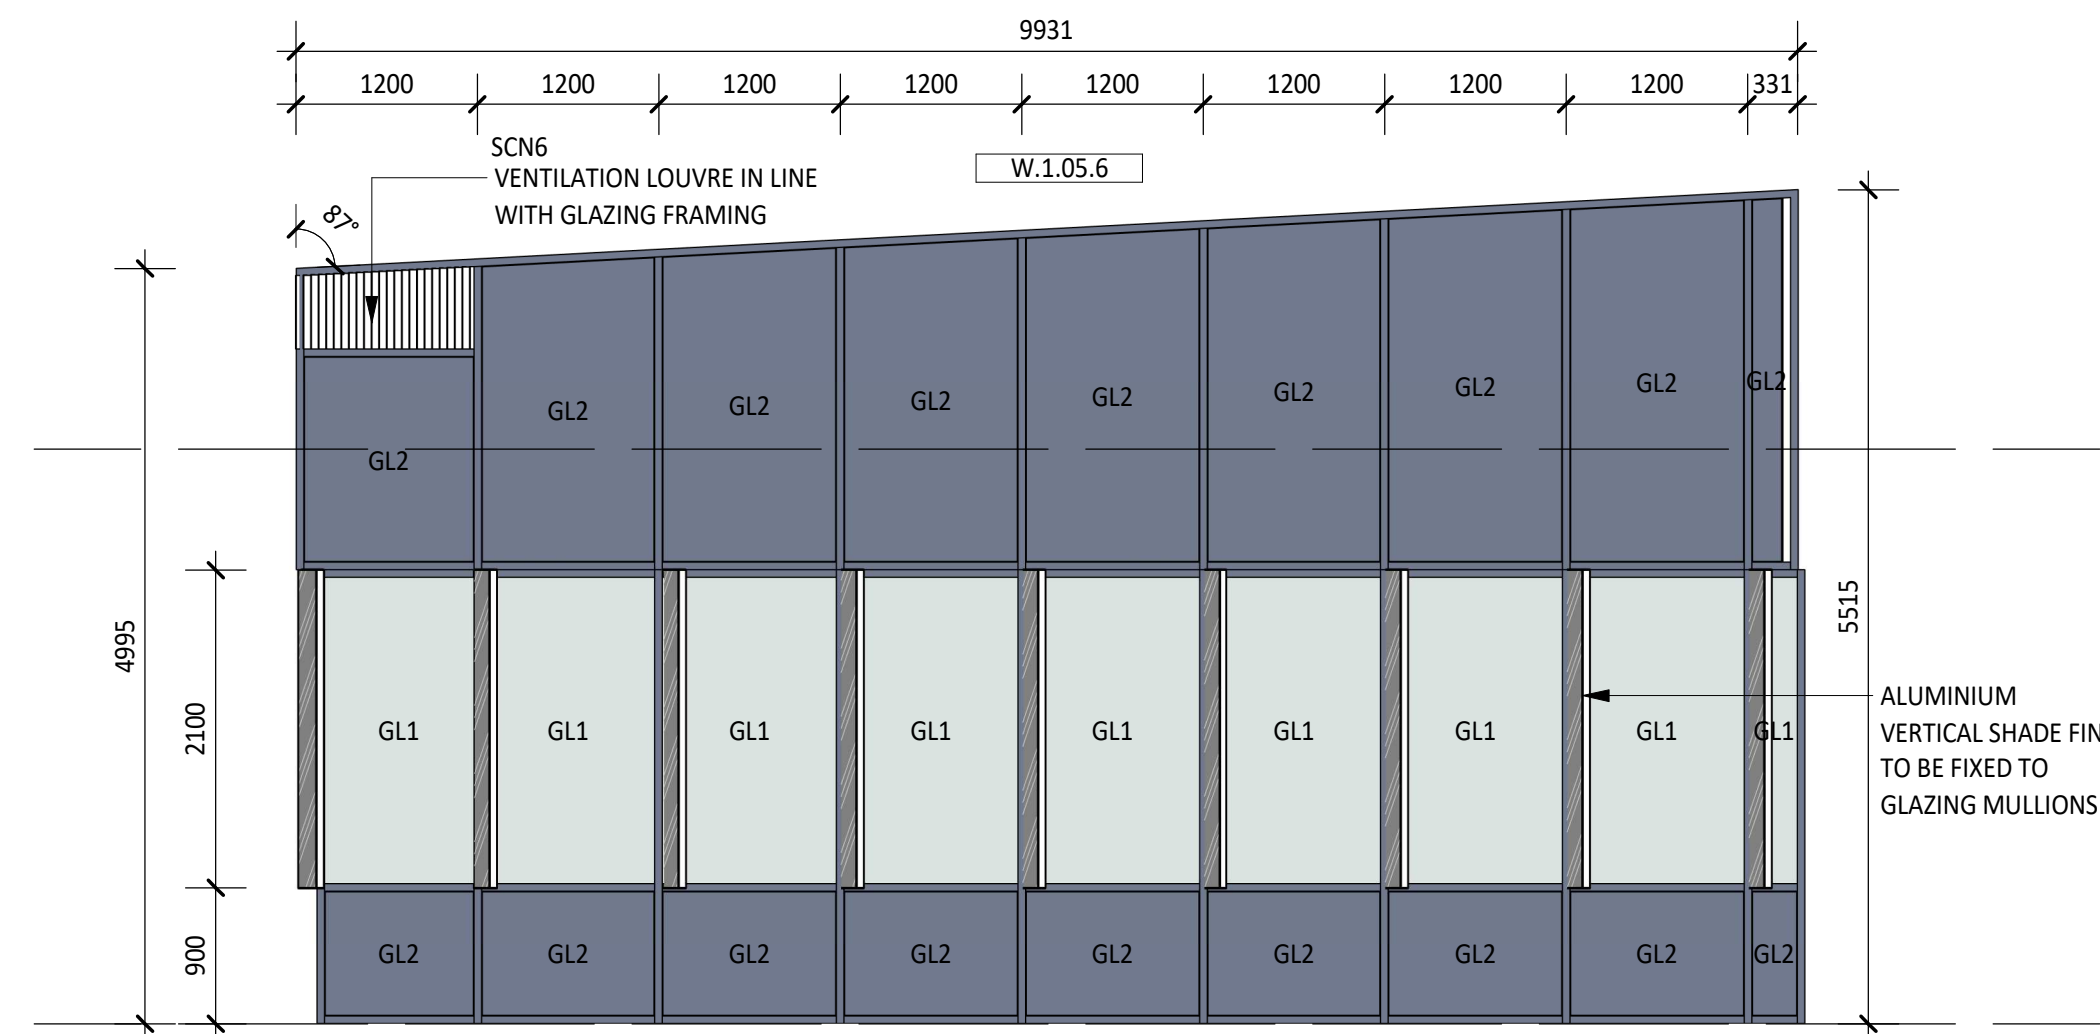


EXTERNAL GLAZING SCHEDULE						
Window Number	Type	Location		Size		Comments
		Room Number	Room Name	Width	Height	
GROUND LEVEL						
W.G.01.1		G.01	ENTRY FOYER	3320	3150	FRAME FINISH - PCS
W.G.01.2		G.01	ENTRY FOYER	5600	3150	FRAME FINISH - PCS
W.G.04.2		G.04	CIRCULATION / WAIT	3450	2550	FRAME FINISH - PCS
W.G.05.1		G.05	SHARED THEORY ROOM	9205	2200	FRAME FINISH - PCS VERTICAL SHADE FINS FIXED TO MULLION
W.G.65.1	E-TYPE 1	G.65	THEORY ROOM 3	8400	2200	FRAME FINISH - PCS
W.G.66.1	E-TYPE 1	G.66	THEORY ROOM 4	8400	2200	FRAME FINISH - PCS
W.G.67.1		G.67	SECOND FOYER	3080	2400	FRAME FINISH - PCS
W.G.70.1		G.70	MALE STUDENTS	3141	1000	FRAME FINISH - PCS
W.G.71.1		G.71	CLEANER	1125	3550	FRAME FINISH - PCS
W.G.71.2		G.71	CLEANER	4800	9790	FRAME FINISH - PCS
W.G.71.3		G.71	CLEANER	1125	7800	FRAME FINISH - PCS
W.G.72.1		G.72	FEMALE STUDENTS	2850	1000	FRAME FINISH - PCS
W.G.74.1		G.74	SHARED THEORY ROOM	6200	2800	FRAME FINISH - PCS
W.G.75.1		G.75	STUDENT KITCHENETTE / LOUNGE	6000	2950	FRAME FINISH - PCS
LEVEL 01						
W.1.01.1		1.01	CIRCULATION / WAIT	3300	5930	FRAME FINISH - PCS
W.1.02.1		1.02	SHARED THEORY ROOM	8500	4306	FRAME FINISH - PCS
W.1.04.1		1.04	STAFF KITCHENETTE / LOUNGE	9400	3400	FRAME FINISH - PCS
W.1.04.2		1.04	STAFF KITCHENETTE / LOUNGE	6020	3400	FRAME FINISH - PCS VERTICAL SHADE FINS FIXED TO MULLION
W.1.04.3		1.04	STAFF KITCHENETTE / LOUNGE	778	3400	FRAME FINISH - PCS
W.1.04.4		1.04	STAFF KITCHENETTE / LOUNGE	6500	3400	FRAME FINISH - PCS VERTICAL SHADE FINS FIXED TO MULLION
W.1.05.4		1.05	TEACHING STAFF OPEN OFFICE	1362	3000	FRAME FINISH - PCS
W.1.05.5		1.05	TEACHING STAFF OPEN OFFICE	3357	3000	FRAME FINISH - PCS
W.1.05.6		1.05	TEACHING STAFF OPEN OFFICE	9838	3000	FRAME FINISH - PCS VERTICAL SHADE FINS FIXED TO MULLION
W.1.05.7		1.05	TEACHING STAFF OPEN OFFICE	3625	2100	FRAME FINISH - PCS
W.1.15.1		1.15	REFRIGERATION WORKSHOP	10600	2100	FRAME FINISH - PCS
W.1.15.2		1.15	REFRIGERATION WORKSHOP	23597	500	FRAME FINISH - PCS
W.1.15.3		1.15	REFRIGERATION WORKSHOP	1200	2500	FRAME FINISH - PCS
W.1.19.2		1.19	THEORY ROOM	5600	4306	FRAME FINISH - PCS

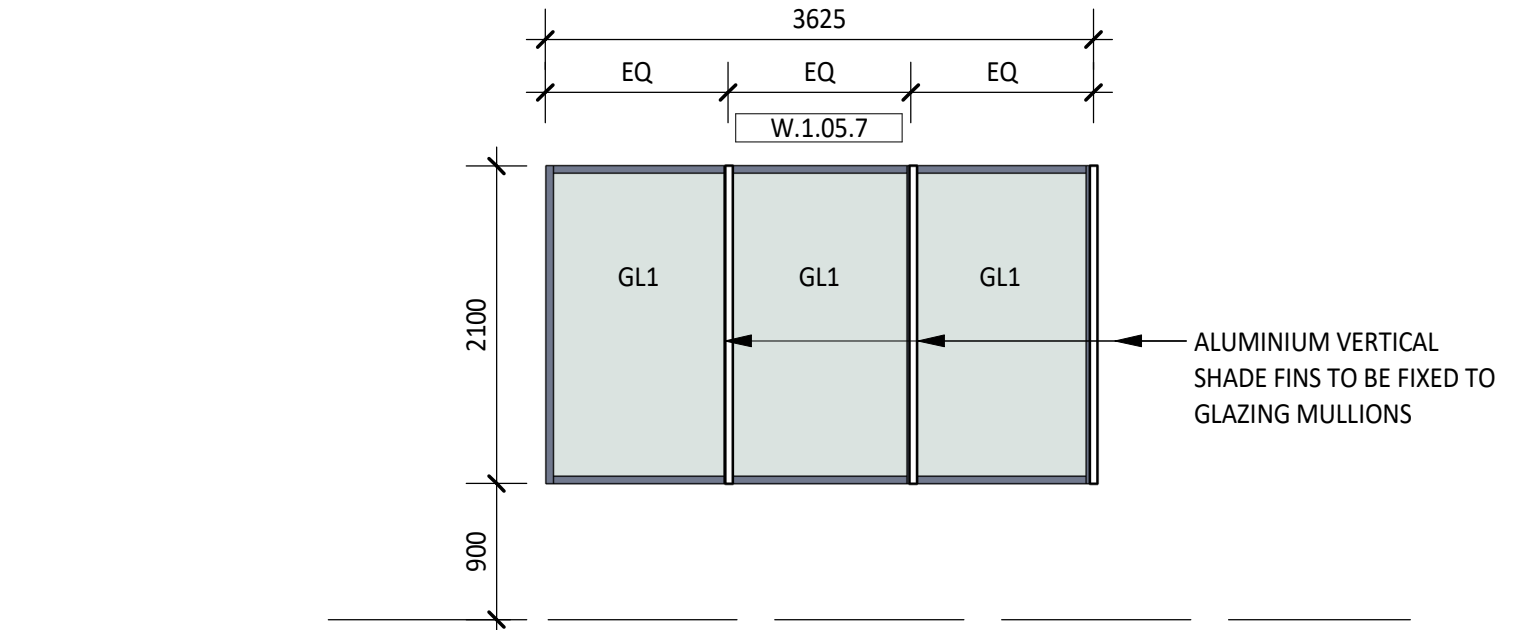

thomson
adsett

PEDDLE THORP
architecture | interiors | health | planning

Telephone +61 7 3840 9999
bne@thomsonadsett.com
Level 9, 470 St Pauls Terrace
Fortitude Valley
Qld 4006 Australia
thomsonadsett.com

© Copyright
These drawings and designs and the copyright thereof are the property of Thomson Adsett Pty Ltd and must not be used, retained or copied without written permission of Thomson Adsett Pty Ltd. ABN 76 105 314 654 Trading as ThomsonAdsett. Dimensions take precedence over scaling. Do not measure off drawings as print sizes may vary

CQU ROCKHAMPTON TAFE CONSOLIDATION - STAGE 2

554/700 Yaamba Rd, Norman Gardens QLD 4701

for

A	12/02/26	ISSUED FOR TENDER	BS
1	30/01/26	DRAFT 60% ISSUE	BS
rev/	date	details	init.
drawn	date		
PT	30/01/26		
checked	date		
BS	30/01/26		
verified	date		
BS	30/01/26		

scale

EXTERNAL GLAZING ELEVATIONS

scale
1 : 50 @ A1

project no.
260018

revision
A

sheet no.
CQU-ROK-092-00-ARC-52-02

ISSUED FOR TENDER