

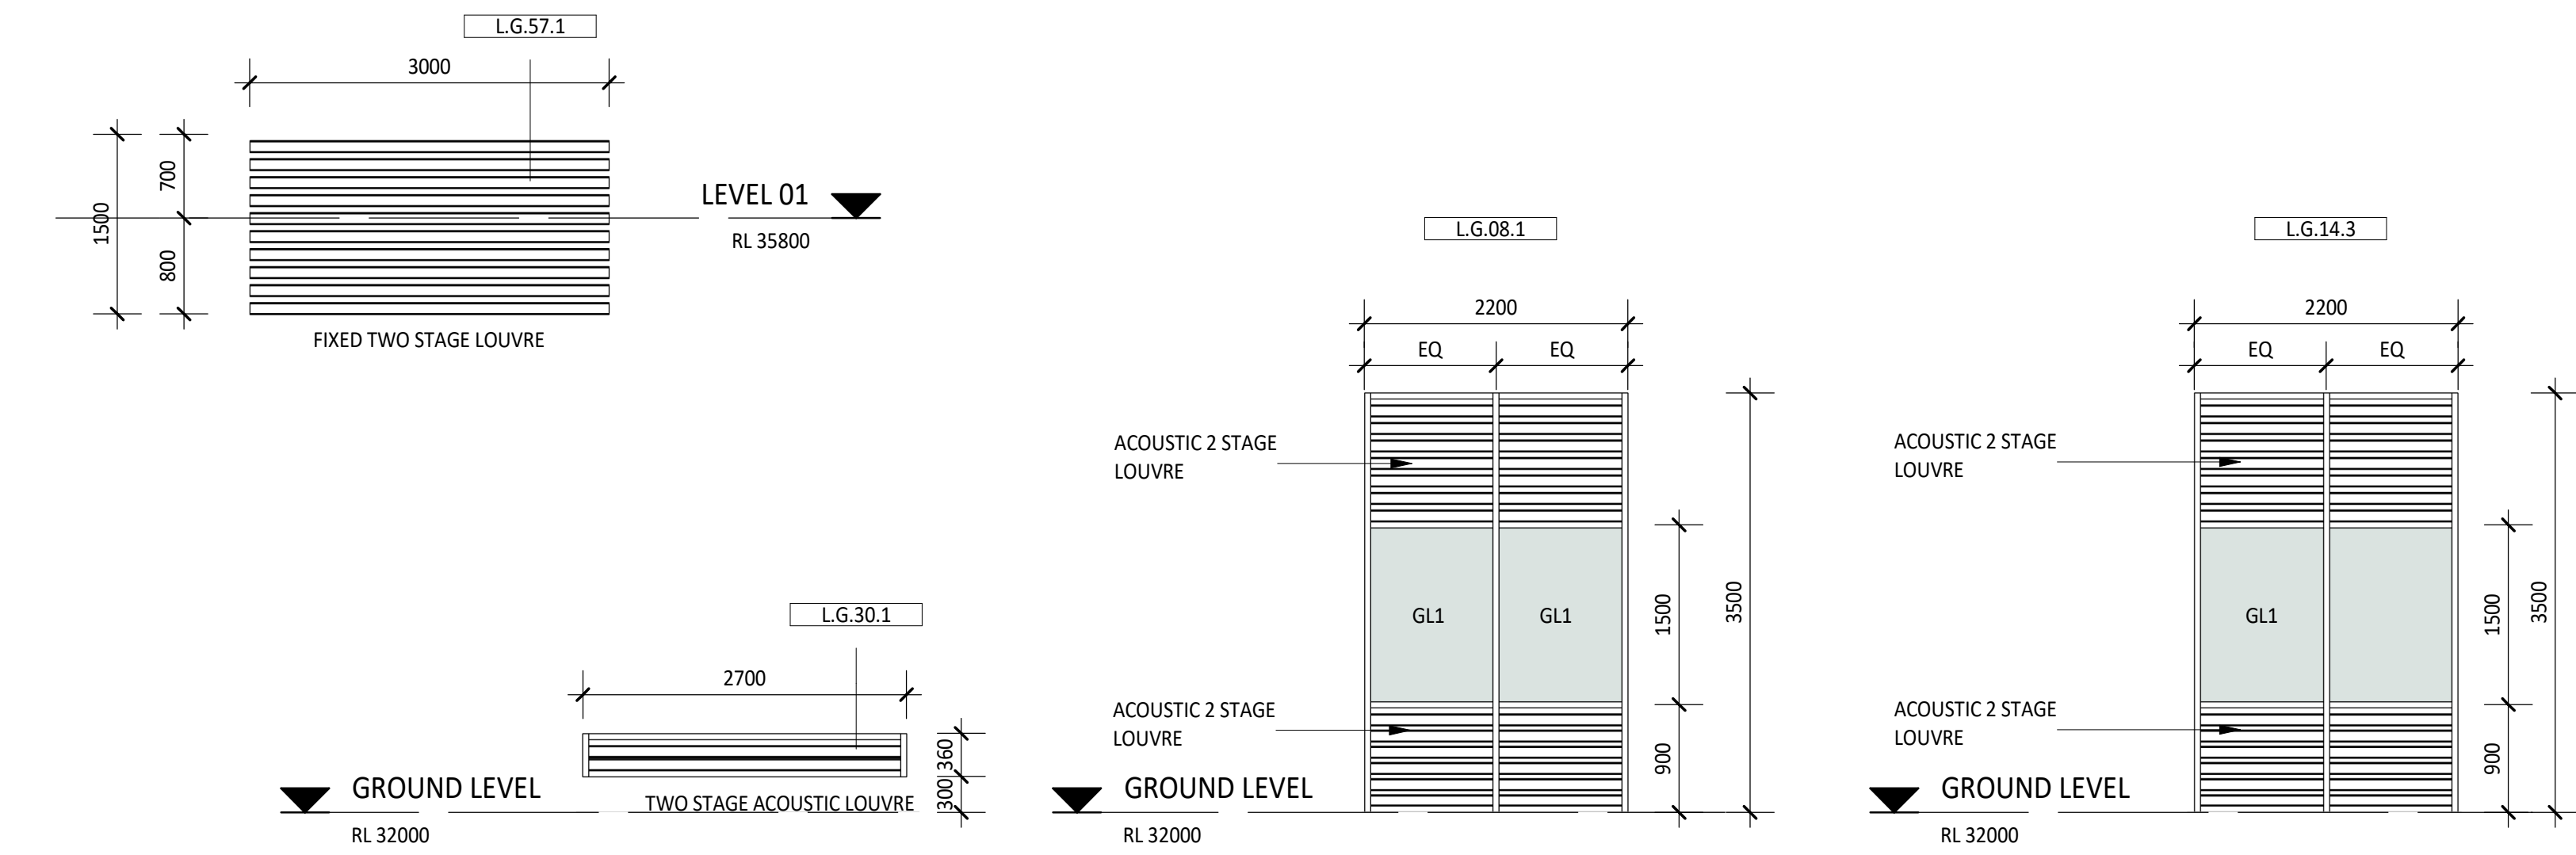
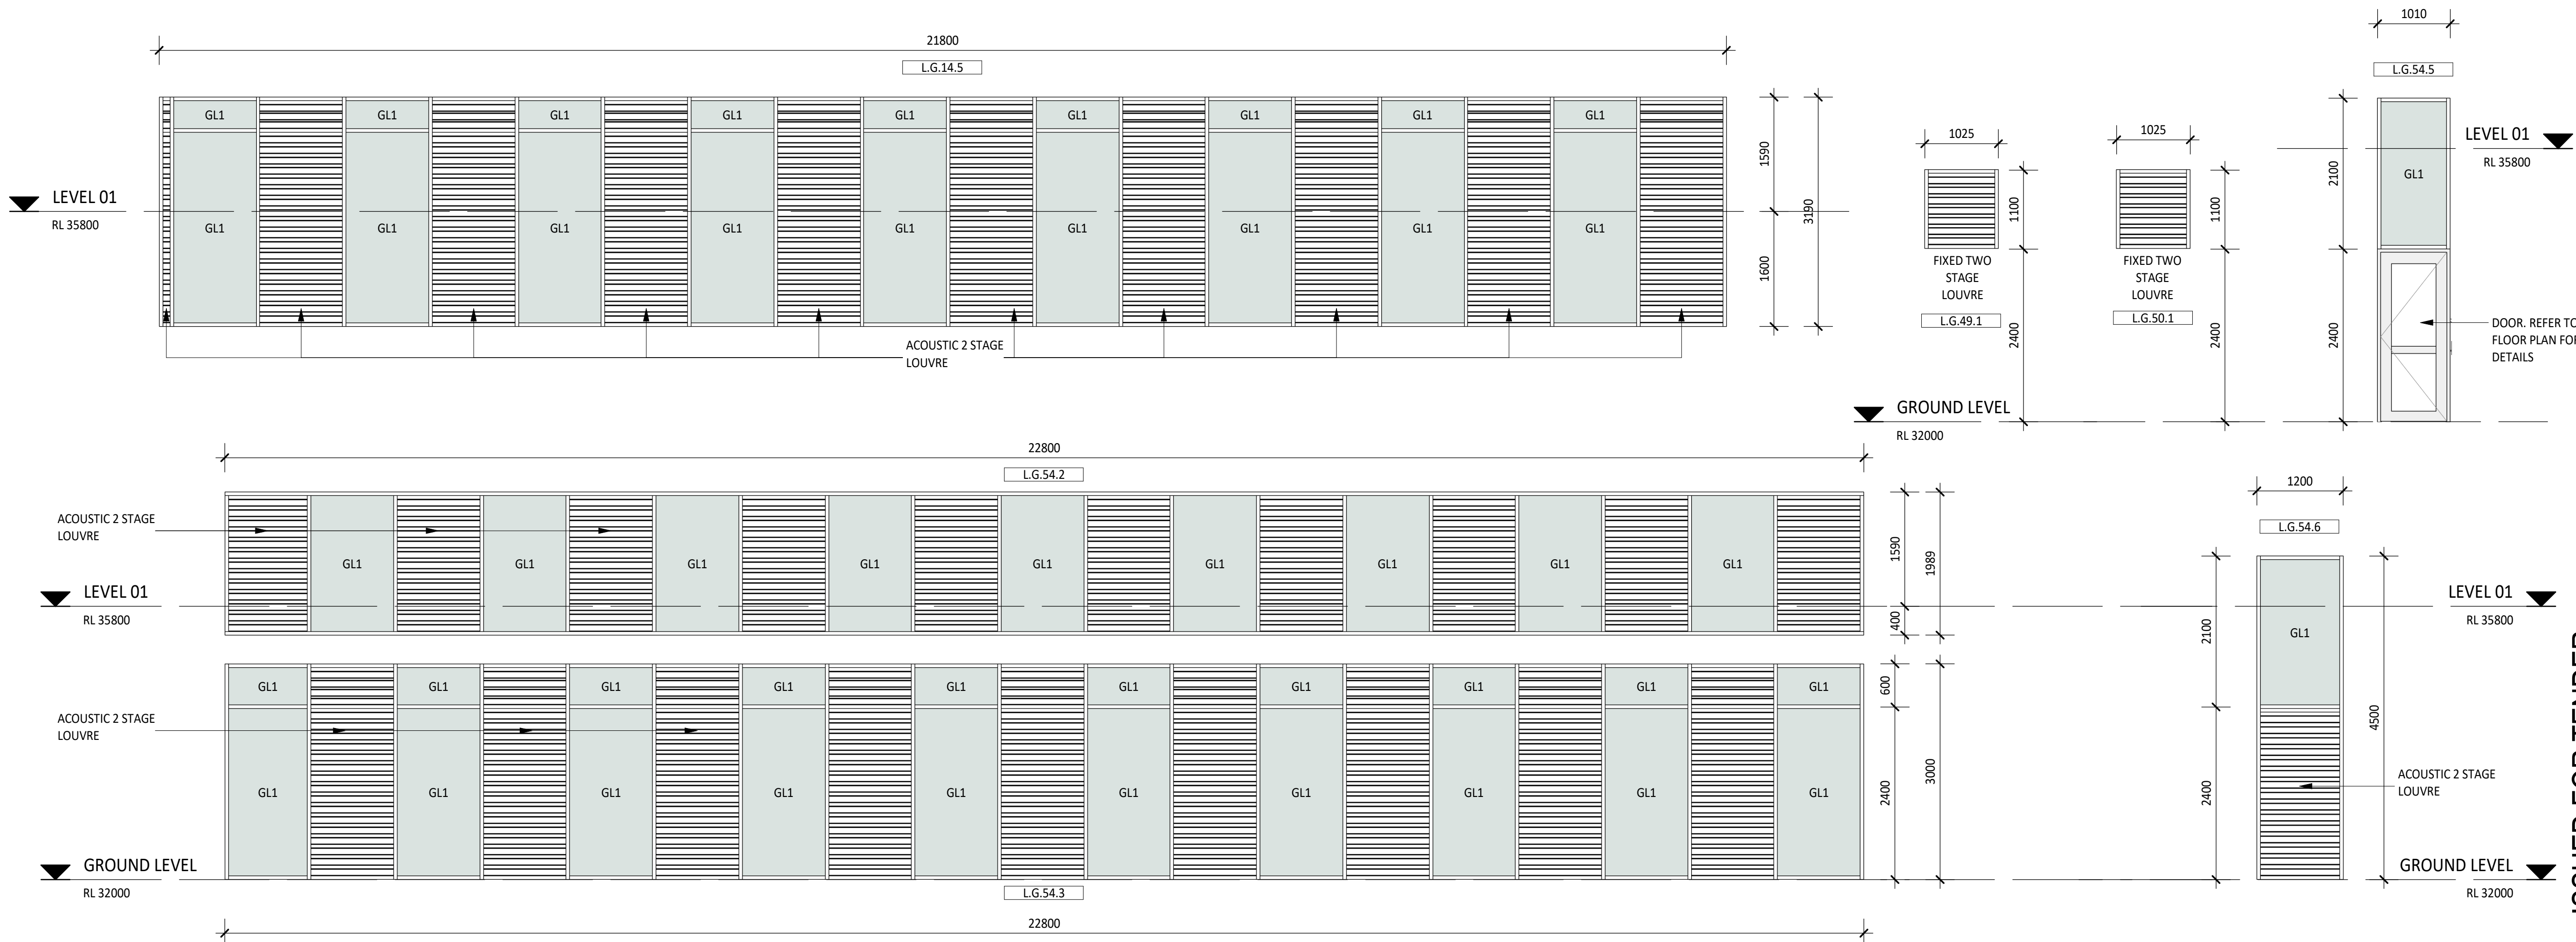


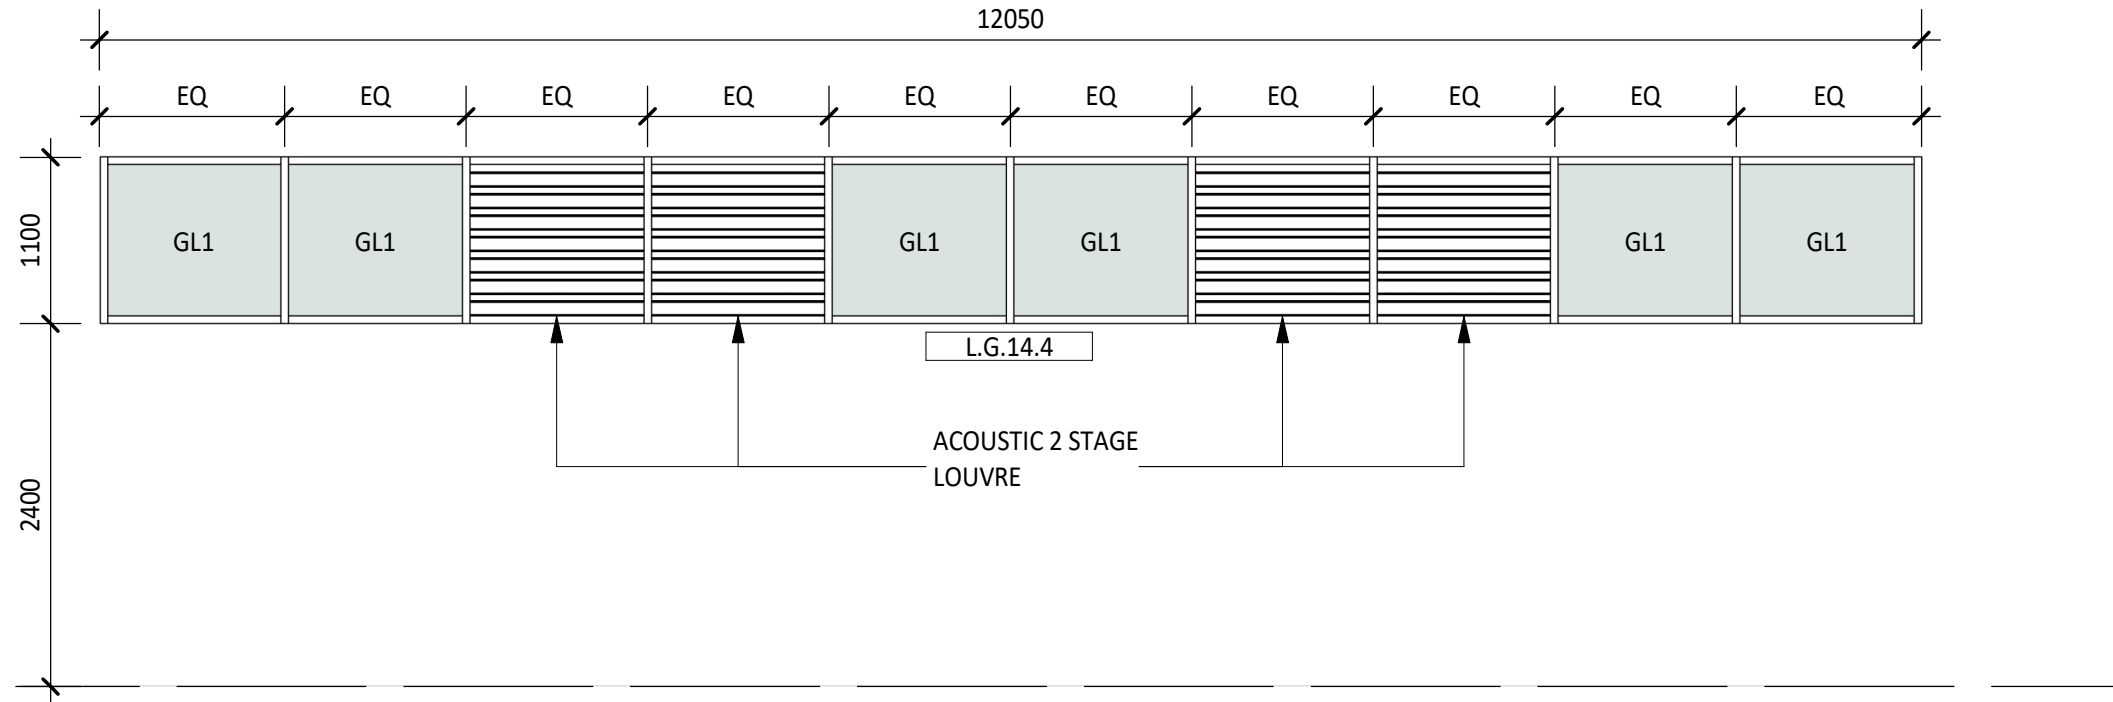

EXTERNAL LOUVRE SCHEDULE					
Window Number	Location		Size		Comments
	Room Number	Room Name	Width	Height	
GROUND LEVEL					
L-G.61.1	G.61	CHILLER PLANT	9027	2400	ACOUSTIC TWO STAGE LOUVRE
L-G.61.2	G.61	CHILLER PLANT	5961	2400	ACOUSTIC TWO STAGE LOUVRE
L-G.61.3	G.61	CHILLER PLANT	9027	2400	ACOUSTIC TWO STAGE LOUVRE
L-G.61.4	G.61	CHILLER PLANT	5961	2400	ACOUSTIC TWO STAGE LOUVRE
L.G.08.1	G.08	WORKSHOP	2200	3500	FRAME FINISH - PCS
L.G.14.1	G.14	ARC WELDING / METAL FABRICATION	1751	5389	FRAME FINISH - PCS
L.G.14.2	G.14	ARC WELDING / METAL FABRICATION	6049	5390	FRAME FINISH - PCS
L.G.14.3	G.14	ARC WELDING / METAL FABRICATION	2200	3500	FRAME FINISH - PCS
L.G.14.4	G.14	ARC WELDING / METAL FABRICATION	12050	1100	FRAME FINISH - PCS
L.G.30.1			2700	360	FIXED TWO STAGE LOUVRE
L.G.30.2			2700	360	FIXED TWO STAGE LOUVRE
L.G.30.3			2700	360	FIXED TWO STAGE LOUVRE
L.G.30.4			2700	360	FIXED TWO STAGE LOUVRE
L.G.30.5			2700	360	FIXED TWO STAGE LOUVRE
L.G.30.6			2700	360	FIXED TWO STAGE LOUVRE
L.G.30.7			2700	360	FIXED TWO STAGE LOUVRE
L.G.49.1	G.49	EXTERNAL COVERED HARDSTAND	1024	1100	FIXED TWO STAGE LOUVRE
L.G.50.1	G.49	EXTERNAL COVERED HARDSTAND	1024	1100	FIXED TWO STAGE LOUVRE
L.G.54.3	G.54	WORKSHOP	22800	3000	
L.G.54.5	G.54	WORKSHOP	1010	2100	FRAME FINISH - PCS
L.G.54.6	G.54	WORKSHOP	1200	4500	FRAME FINISH - PC6
L.G.57.1			3000	1500	FIXED TWO STAGE LOUVRE
LEVEL 01					
L.G.14.5	G.14	ARC WELDING / METAL FABRICATION	21800	3189	FRAME FINISH - PCS
L.G.54.2	G.54	WORKSHOP	22800	1989	

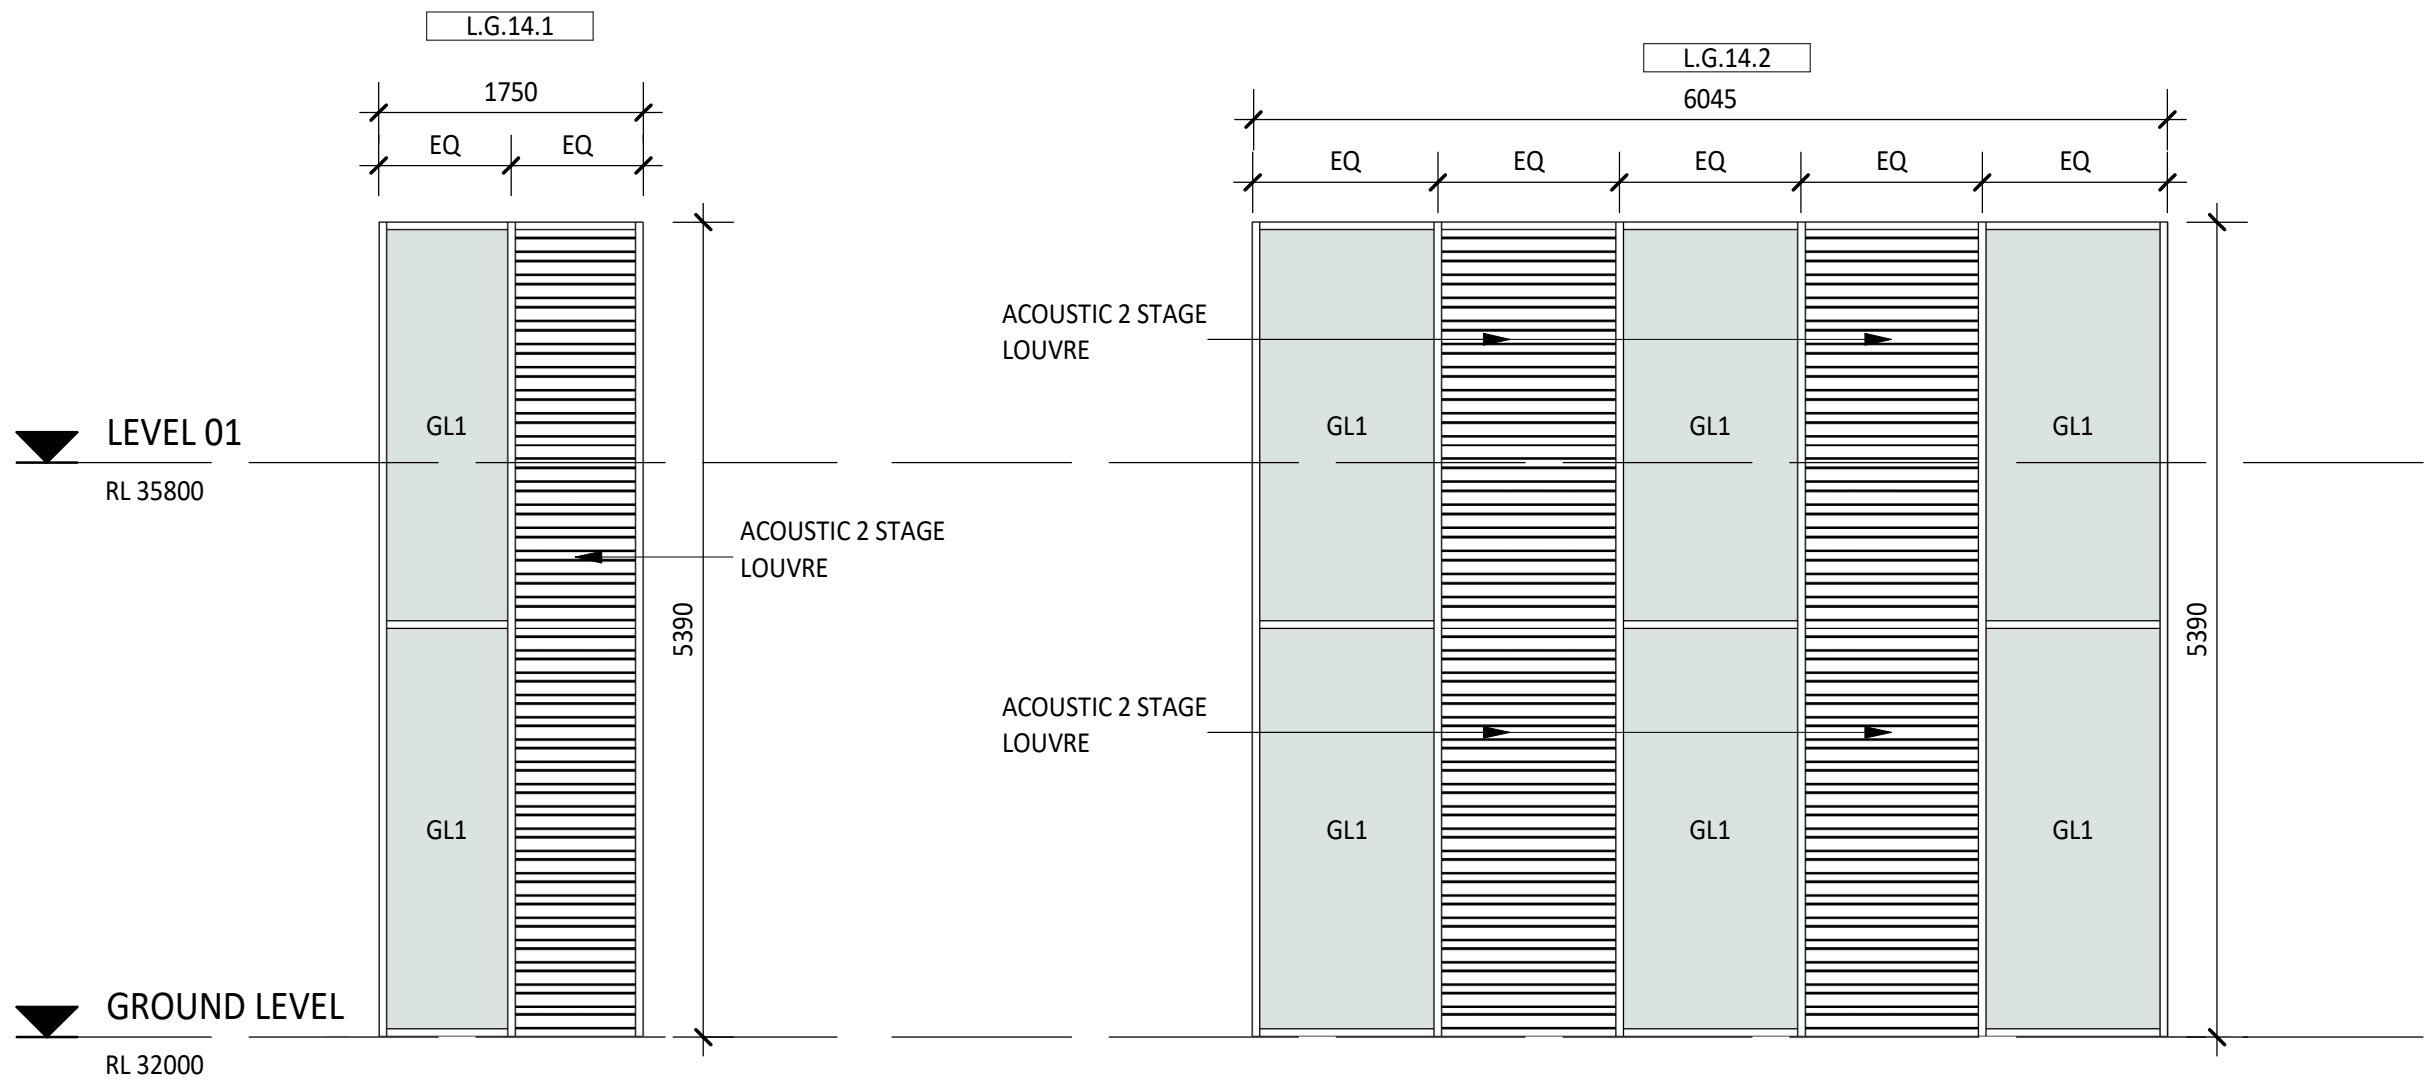

thomson
adsett

PEDDLE THORP
architecture | interiors | health | planning

Telephone +61 7 3840 9999
bne@thomsonadsett.com
Level 9, 470 St Pauls Terrace
Fortitude Valley
Qld 4006 Australia
thomsonadsett.com

© Copyright
These drawings and designs and the copyright thereof are the property of Thomson Adsett Pty Ltd and must not be used, retained or copied without written permission of Thomson Adsett Pty Ltd. A.B.N 76 105 314 654 Trading as ThomsonAdsett. Dimensions take precedence over scaling. Do not measure off drawings as print sizes may vary

**CQU ROCKHAMPTON
TAFE
CONSOLIDATION -
STAGE 2**

554/700 Yaamba Rd, Norman
Gardens QLD 4701

for

**CQUniversity
AUSTRALIA**

B	05/03/26	ISSUED FOR TENDER	BS
A	12/02/26	ISSUED FOR TENDER	BS
1	30/01/26	DRAFT 60% ISSUE	BS
rev	date	details	init.

drawn	date
PT	30/01/26
checked	date
BS	30/01/26
verified	date
BS	30/01/26

scale

LOUVRE ELEVATIONS

scale 1 : 50 @ A1 project no. 260018
revision B
sheet no. CQU-ROK-092-00-ARC-52-03

ISSUED FOR TENDER