


| INTERNAL GLAZING SCHEDULE |             |                              |       |        |                                                                    |
|---------------------------|-------------|------------------------------|-------|--------|--------------------------------------------------------------------|
| Window Number             | Location    |                              | Size  |        | Comments                                                           |
|                           | Room Number | Room Name                    | Width | Height |                                                                    |
| GROUND LEVEL              |             |                              |       |        |                                                                    |
| W.G.04.1                  | G.04        | CIRCULATION / WAIT           | 6351  | 1400   | FRAME FINISH - PC6. MULLION SET OUT TO MATCH CFC PANELS            |
| W.G.04.3                  | G.04        | CIRCULATION / WAIT           | 7256  | 1400   | FRAME FINISH - PC6                                                 |
| W.G.04.4                  | G.04        | CIRCULATION / WAIT           | 7290  | 1400   | FRAME FINISH - PC6                                                 |
| W.G.05.3                  | G.05        | SHARED THEORY ROOM           | 2065  | 1500   | FRAME FINISH - PC6                                                 |
| W.G.06.1                  | G.06        | THEORY ROOM                  | 7282  | 1500   | FRAME FINISH - PC6                                                 |
| W.G.07.1                  | G.07        | CLASS ROOM / THEORY          | 5515  | 2400   | FRAME FINISH - PC6                                                 |
| W.G.08.1                  | G.08        | WORKSHOP                     | 300   | 2400   | FRAME FINISH - PC6                                                 |
| W.G.11.1                  | G.11        | HEAT TREATMENT ROOM          | 900   | 2400   | FRAME FINISH - PC6                                                 |
| W.G.11.2                  | G.11        | HEAT TREATMENT ROOM          | 350   | 2400   | FRAME FINISH - PC6                                                 |
| W.G.12.1                  | G.12        | PRECISION MEASURE            | 3730  | 2400   | FRAME FINISH - PC6                                                 |
| W.G.13.1                  | G.13        | CAD CLASSROOM                | 6660  | 1400   | FRAME FINISH - PC6                                                 |
| W.G.13.2                  | G.13        | CAD CLASSROOM                | 5310  | 2400   | FRAME FINISH - PC6                                                 |
| W.G.15.1                  | G.15        | DEMONSTRATION                | 1477  | 1500   | FRAME FINISH - PC6. TINTED GLAZING - CATEGORY 3 FOR EYE PROTECTION |
| W.G.55.1                  | G.55        | CHASIS DYNAMOMETER           | 1200  | 2400   | FRAME FINISH - PC6                                                 |
| W.G.55.2                  | G.55        | CHASIS DYNAMOMETER           | 2127  | 2400   | FRAME FINISH - PC6                                                 |
| W.G.62.1                  | G.62        | THEORY ROOM 1                | 7310  | 2400   | FRAME FINISH - PC6                                                 |
| W.G.63.1                  | G.63        | THEORY ROOM 2                | 7054  | 1400   | FRAME FINISH - PC6                                                 |
| W.G.63.2                  | G.63        | THEORY ROOM 2                | 6620  | 2400   | FRAME FINISH - PC6                                                 |
| W.G.64.1                  | G.64        | ONLINE TEACHING              | 600   | 1380   | FRAME FINISH - PC6                                                 |
| W.G.64.2                  | G.64        | ONLINE TEACHING              | 1309  | 2400   | FRAME FINISH - PC6                                                 |
| W.G.65.2                  | G.65        |                              | 5760  | 1200   | FRAME FINISH - PC6                                                 |
| W.G.65.3                  |             |                              | 436   | 2400   | FRAME FINISH - PC6                                                 |
| W.G.66.2                  | G.66        |                              | 7060  | 1200   | FRAME FINISH - PC6                                                 |
| W.G.66.3                  |             |                              | 1644  | 2400   | FRAME FINISH - PC6                                                 |
| W.G.74.2                  | G.74        | SHARED THEORY ROOM           | 6000  | 1400   | FRAME FINISH - PC6. MULLION SET OUT TO MATCH CFC PANELS            |
| W.G.75.2                  | G.75        | STUDENT KITCHENETTE / LOUNGE | 1830  | 2100   | FRAME FINISH - PC6                                                 |
| LEVEL 01                  |             |                              |       |        |                                                                    |
| W.1.01.2                  | 1.01        | CIRCULATION / WAIT           | 1600  | 2100   | FRAME FINISH - PC6                                                 |
| W.1.02.2                  | 1.02        | SHARED THEORY ROOM           | 6660  | 1500   | FRAME FINISH - PC6                                                 |
| W.1.04.5                  | 1.04        | STAFF KITCHENETTE / LOUNGE   | 5524  | 2100   | FRAME FINISH - PC6                                                 |
| W.1.04.6                  | 1.04        | STAFF KITCHENETTE / LOUNGE   | 7314  | 3000   | FRAME FINISH - PC6                                                 |
| W.1.05.2                  | 1.05        | TEACHING STAFF OPEN OFFICE   | 4745  | 2100   | FRAME FINISH - PC6                                                 |
| W.1.05.3                  | 1.05        | TEACHING STAFF OPEN OFFICE   | 2100  | 600    | FRAME FINISH - PC6                                                 |
| W.1.05.8                  | 1.05        | TEACHING STAFF OPEN OFFICE   | 12144 | 2100   | FRAME FINISH - PC6                                                 |
| W.1.05.9                  |             |                              | 1942  | 3000   | FRAME FINISH - PC6                                                 |
| W.1.07.1                  | 1.07        | 1 PERSON MEETING ROOM        | 1900  | 2400   | FRAME FINISH - PC6                                                 |
| W.1.08.1                  | 1.08        | SHARED MEETING ROOM          | 2200  | 2400   | FRAME FINISH - PC6                                                 |
| W.1.08.2                  | 1.08        | SHARED MEETING ROOM          | 3400  | 2400   | FRAME FINISH - PC6                                                 |
| W.1.13.1                  | 1.13        | CLEAN WORKSHOP               | 15310 | 2000   | FRAME FINISH - PC6                                                 |
| W.1.13.2                  | 1.13        | CLEAN WORKSHOP               | 13885 | 2100   | FRAME FINISH - PC6                                                 |
| W.1.15.4                  | 1.15        | REFRIGERATION WORKSHOP       | 1915  | 2400   | FRAME FINISH - PC6                                                 |
| W.1.15.5                  | 1.15        | REFRIGERATION WORKSHOP       | 13578 | 2100   | FRAME FINISH - PC6                                                 |
| W.1.19.1                  | 1.19        | THEORY ROOM                  | 2492  | 2400   | FRAME FINISH - PC6                                                 |
| W.1.19.3                  | 1.19        | THEORY ROOM                  | 2451  | 2400   | FRAME FINISH - PC6                                                 |
| W.1.19.4                  |             |                              | 2936  | 2400   | FRAME FINISH - PC6                                                 |

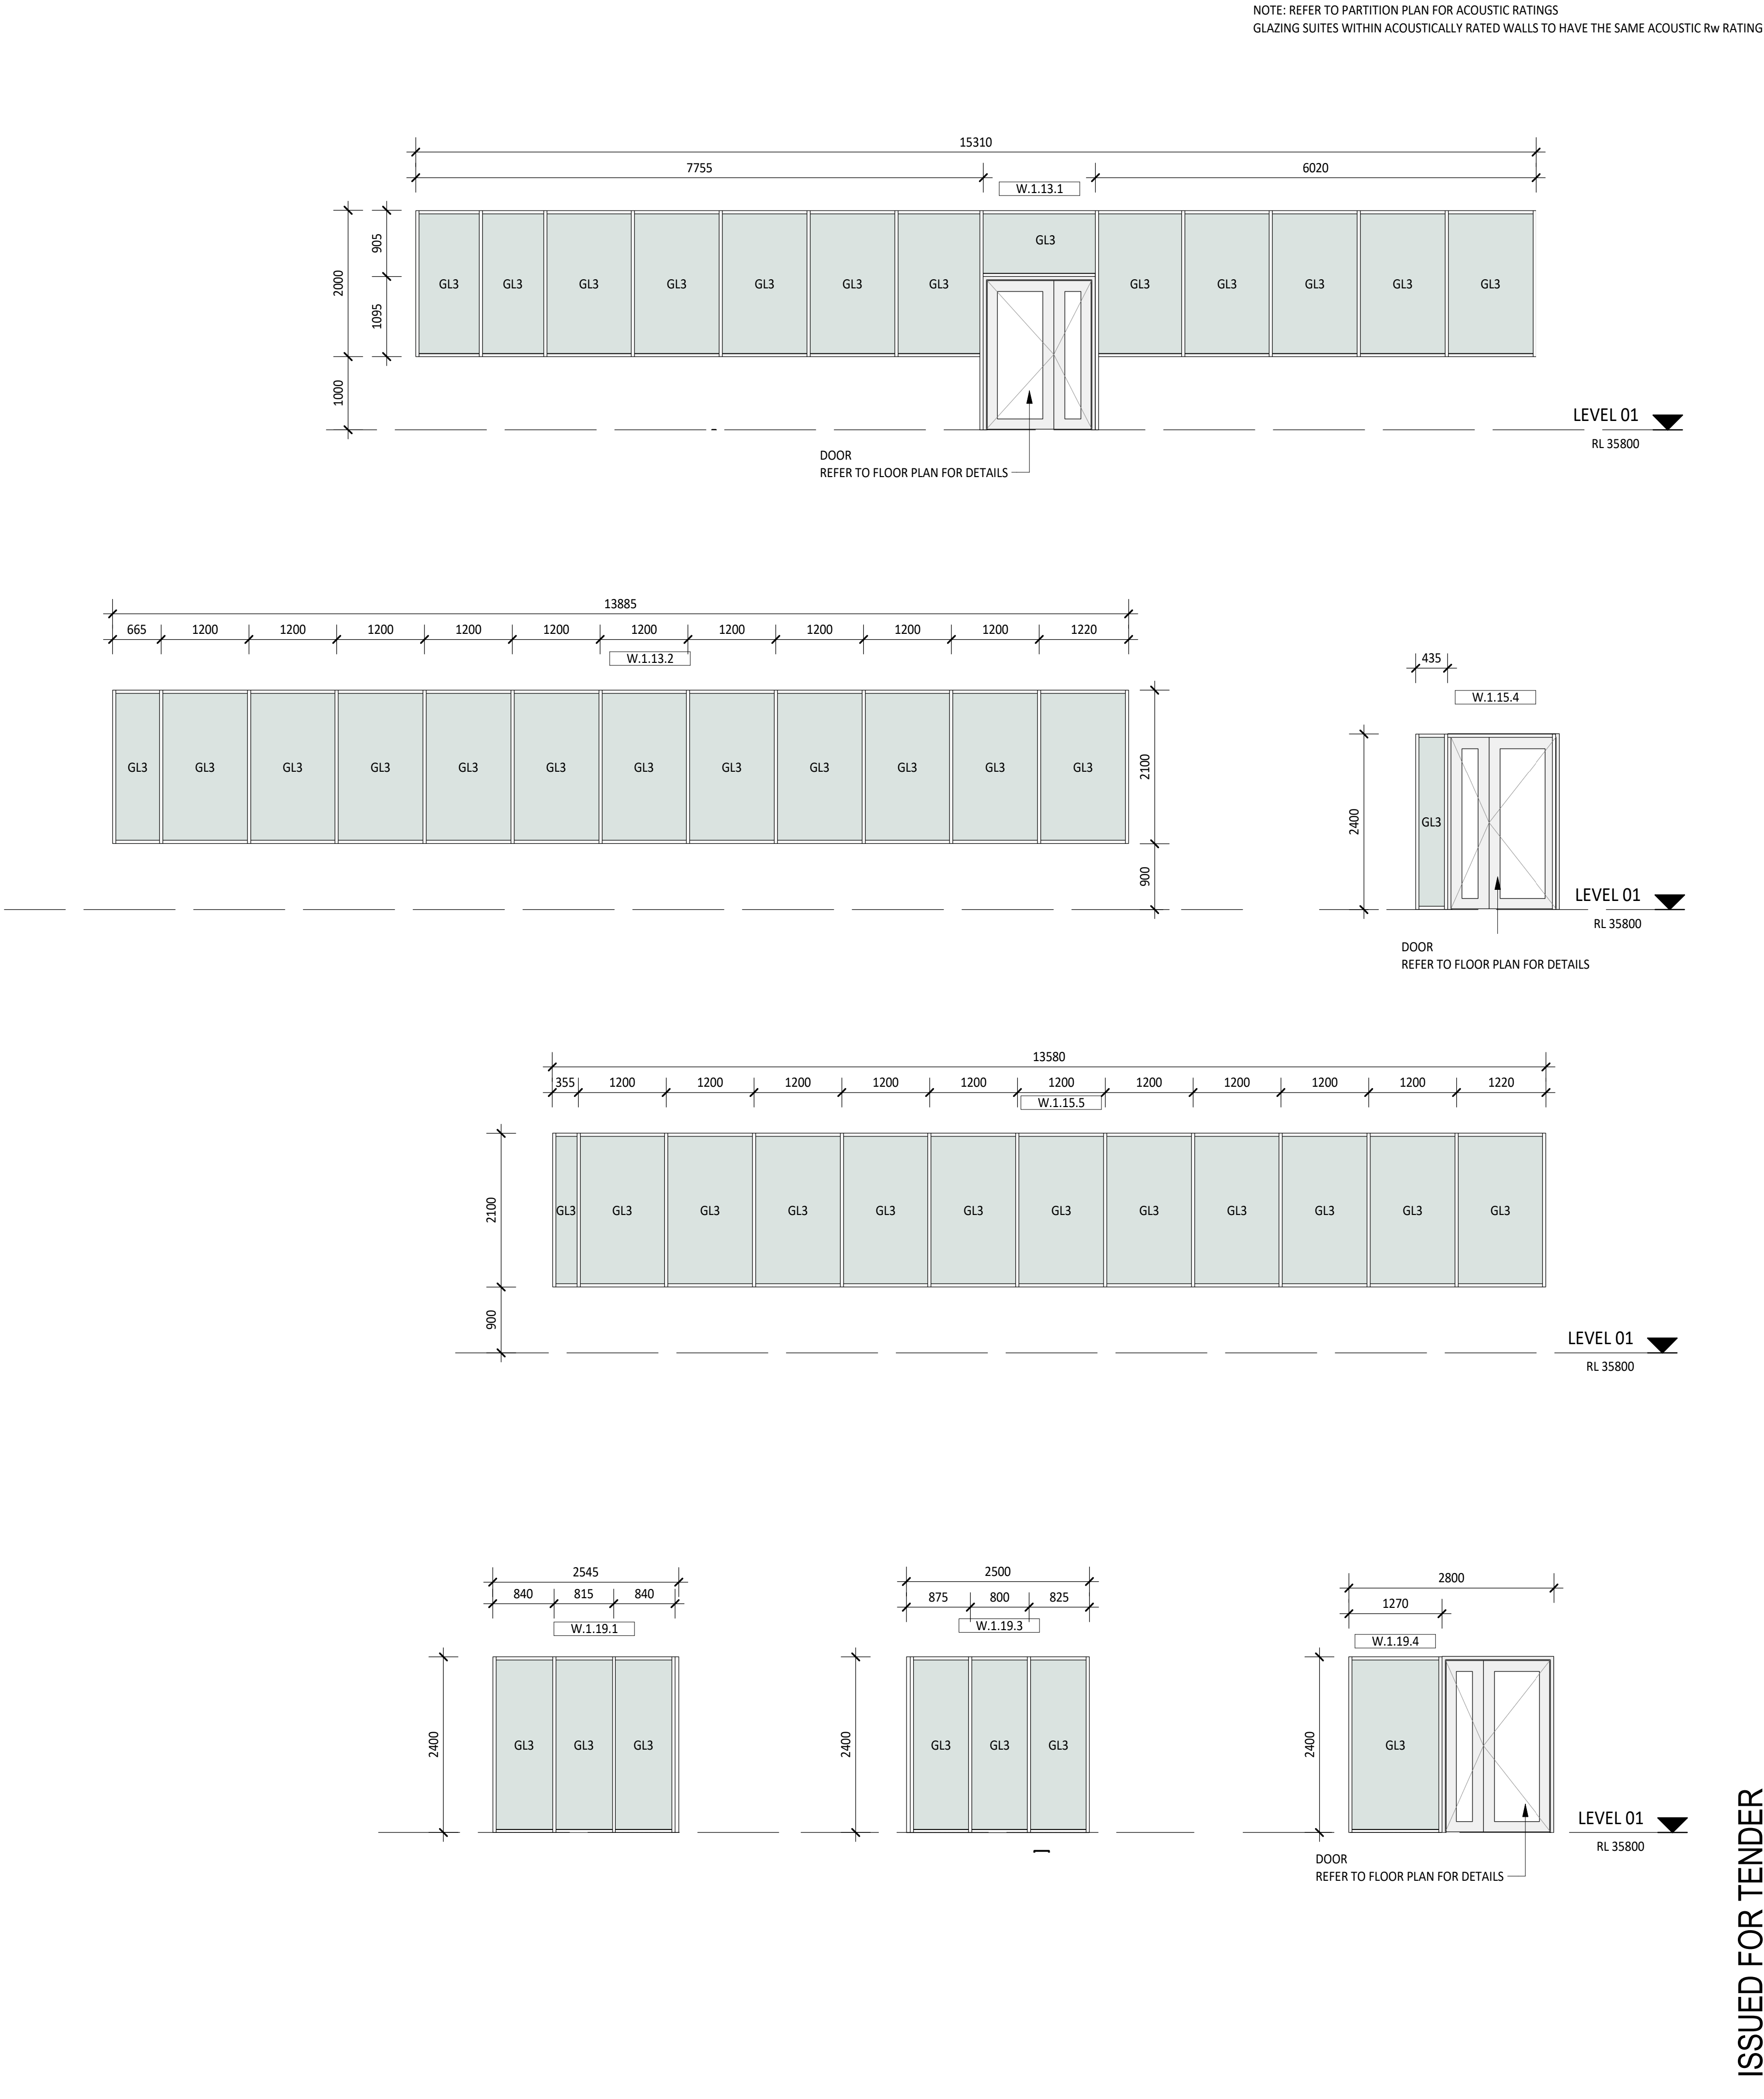

thomson  
adsett

architecture | interiors | health | planning

Telephone +61 7 3840 9999  
bne@thomsonadsett.com  
Level 9, 470 St Pauls Terrace  
Fortitude Valley  
Qld 4006 Australia  
thomsonadsett.com

© Copyright  
These drawings and designs and the copyright thereof are the property of Thomson Adsett Pty Ltd and must not be used, retained or copied without written permission of Thomson Adsett Pty Ltd. ABN 76 105 314 654 Trading as ThomsonAdsett. Dimensions take precedence over scaling. Do not measure off drawings as print sizes may vary

CQU ROCKHAMPTON  
TAFE  
CONSOLIDATION -  
STAGE 2  
554/700 Yaamba Rd, Norman  
Gardens QLD 4701

for  

CQUniversity  
AUSTRALIA

A 12/02/26 ISSUED FOR TENDER BS

rev/ date details init.

drawn PT 09/02/26

checked BS 09/02/26

verified BS 09/02/26

scale

scale 1 : 50 @ A1 project no. 260018 revision A sheet no. CQU-ROK-092-00-ARC-52-13

Autodesk Docs: CQU ROK TAFE/260018\_A\_CQ-UNIVERSITY\_BLD-TRADES\_R25.rvt 12/02/2026 4:43:46 PM