

CQU ROCKHAMPTON TAFE CONSOLIDATION - STAGE 2

554/700 Yaamba Rd, Norman
Gardens QLD 4701



B	20/02/26	CQU DIRECTED CHANGE TO FLOOR FINISH	BS
A	12/02/26	ISSUED FOR TENDER	BS
1	30/01/26	DRAFT 60% ISSUE	BS
rev/	date	details	init.

drawn	date
PT	30/01/26
checked	date
BS	30/01/26
verified	date
BS	30/01/26

scale

RLS - F&M - GF - WORKSHOP (FITTING & MACHINING)

scale
1 : 50 @ A1

revision


B

sheet no.

CQU-ROK-092-GN-ARC-60-011

original sheet size - A1 (594mm x 841mm)

ISSUED FOR TENDER

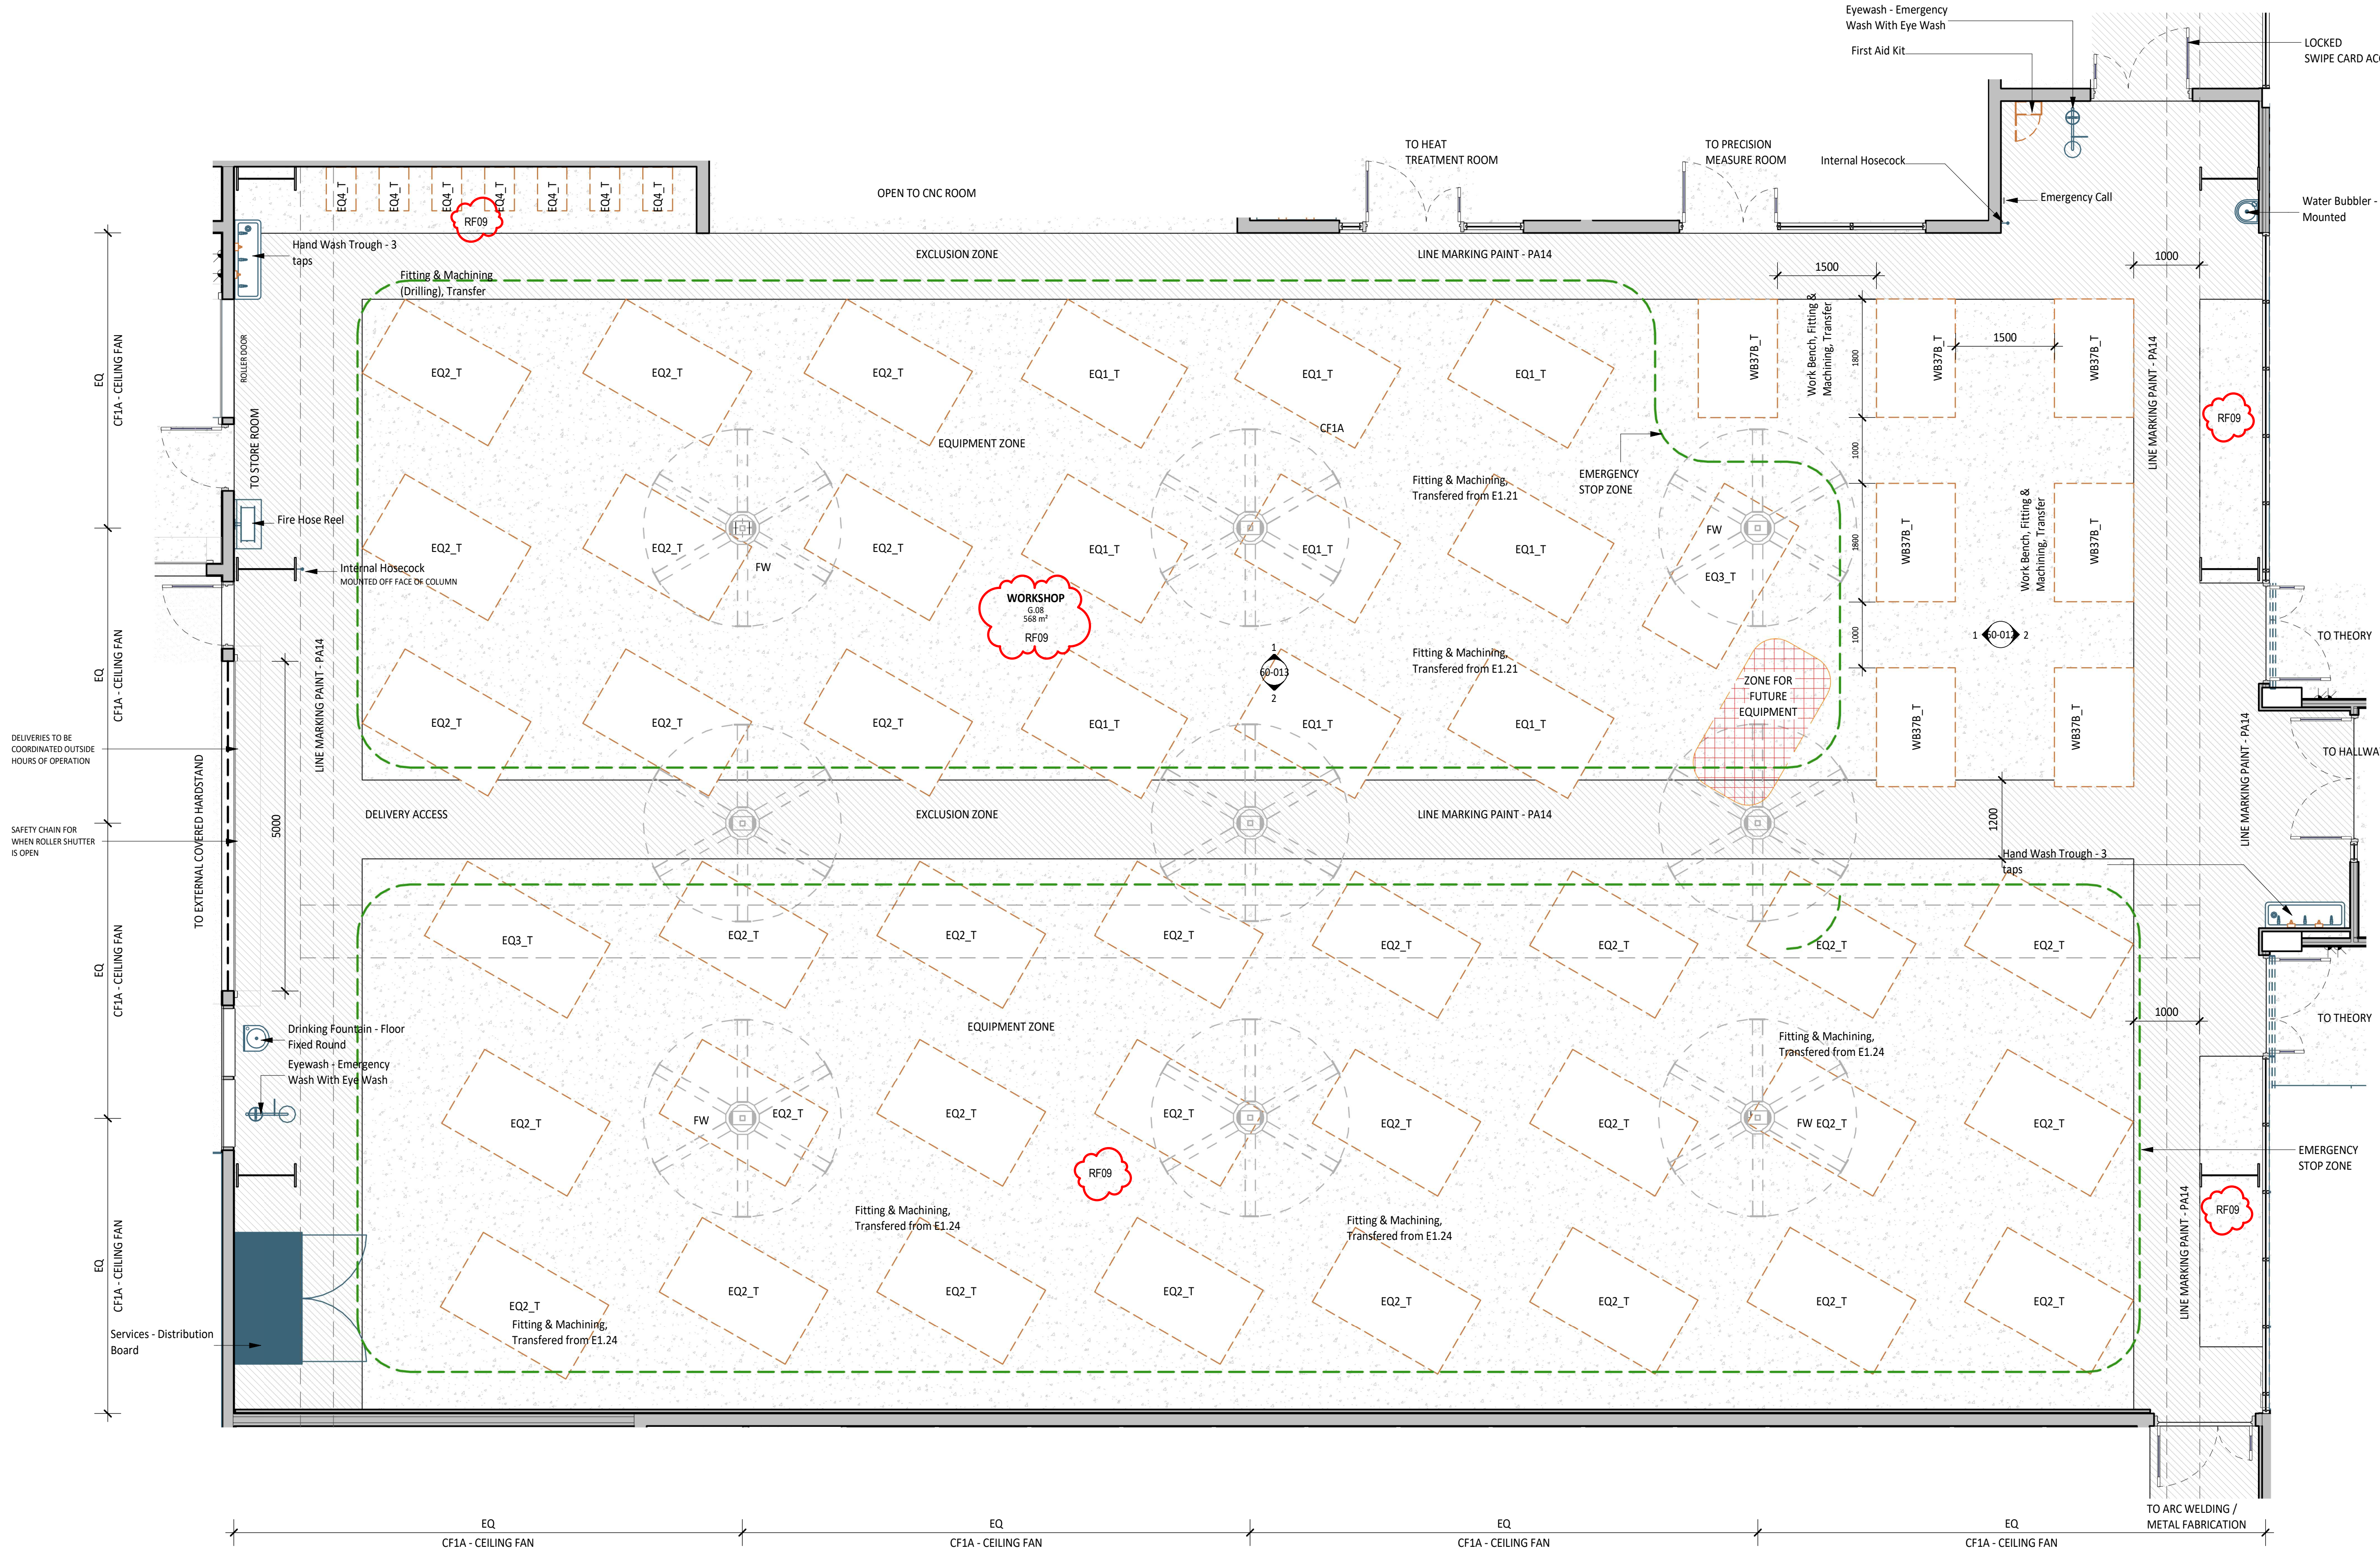

40-LEGEND FFE - WORKSHOP G.08				
Code	Description	Group	Count	
BN11A	Hand Wash Trough - 3 taps	1	2	
CD3A	Emergency Call	1	1	
CF1A	Ceiling Fan - Powerfoil D, 6 Aluminum Airfoils	1	9	
DB	Services - Distribution Board	1	1	
EQ23	Crane & Gantry 3.2 Ton	1	1	
FHR	Fire Hose Reel	1	1	
HY6A	Water Bubbler - Wall Mounted	1	1	

40-LEGEND FFE - WORKSHOP G.08				
Code	Description	Group	Count	
HY7A	Drinking Fountain - Floor Fixed Round	1	1	
SR1A	Eyewash - Emergency Wash With Eye Wash	1	2	
TW3A	Internal Hosecock	1	2	
CA1A	First Aid Kit	2	1	
DS12A	Dispenser - Soap	2	4	
EQ1_T	Fitting & Machining, Transferred from E1.21	2T	9	
EQ2_T	Fitting & Machining, Transferred from E1.24	2T	32	
EQ3_T	Fitting & Machining, Transferred from E1.24	2T	2	
EQ4_T	Fitting & Machining (Drilling), Transfer	2T	7	
WB37B_T	Work Bench, Fitting & Machining, Transfer	2T	17	