

**CQU ROCKHAMPTON
TAFE
CONSOLIDATION -
STAGE 2**

554/700 Yaamba Rd, Norman
Gardens QLD 4701

for



A	12/02/26	ISSUED FOR TENDER	BS
1	30/01/26	DRAFT 60% ISSUE	BS
rev\	date	details	init.

drawn	date
PT	30/01/26
checked	date
BS	30/01/26
verified	date
BS	30/01/26

scale

**RLS - F&M - GF -
WORKSHOP (FITTING &
MACHINING)**


scale project no.
1 : 50 @ A1 260018

revision
A


sheet no.
CQU-ROK-092-GN-ARC-60-013

original sheet size - A1 (594mm x 841mm)

ISSUED FOR TENDER

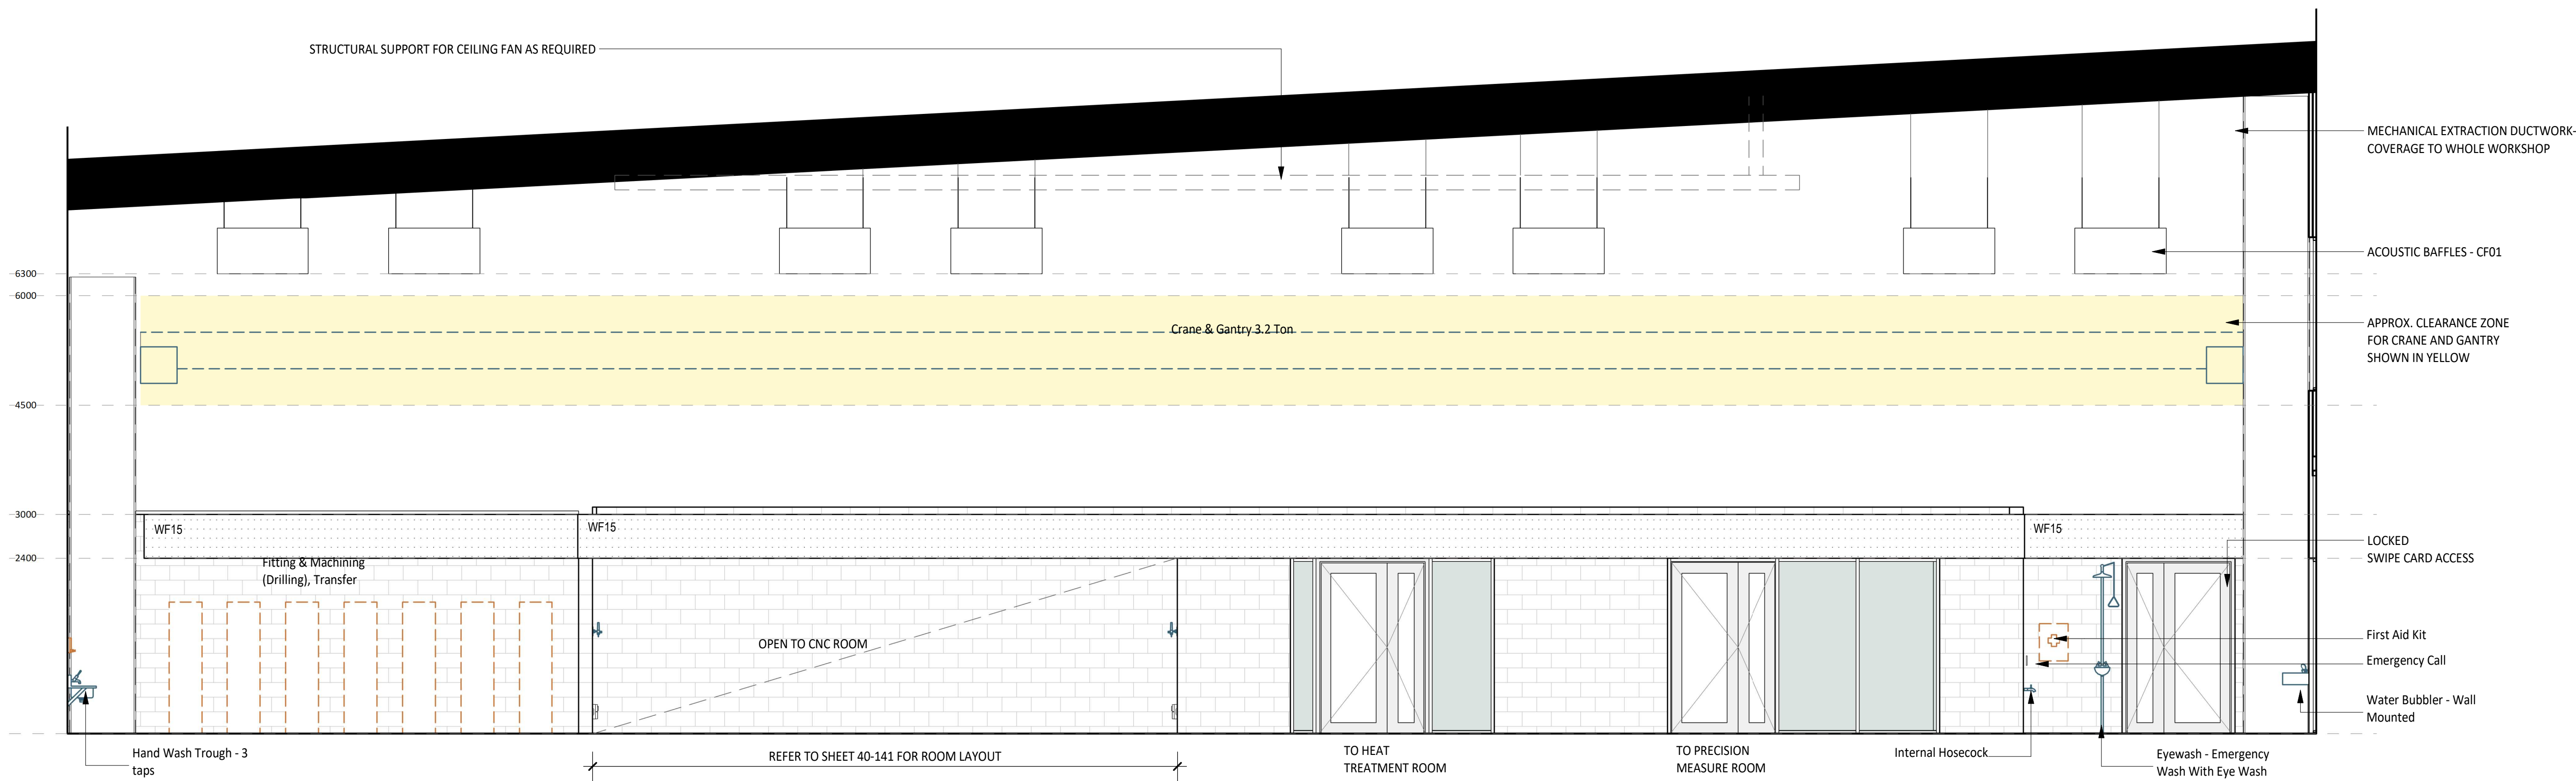

1 ELEVATION DETAIL
60-011 1 : 50

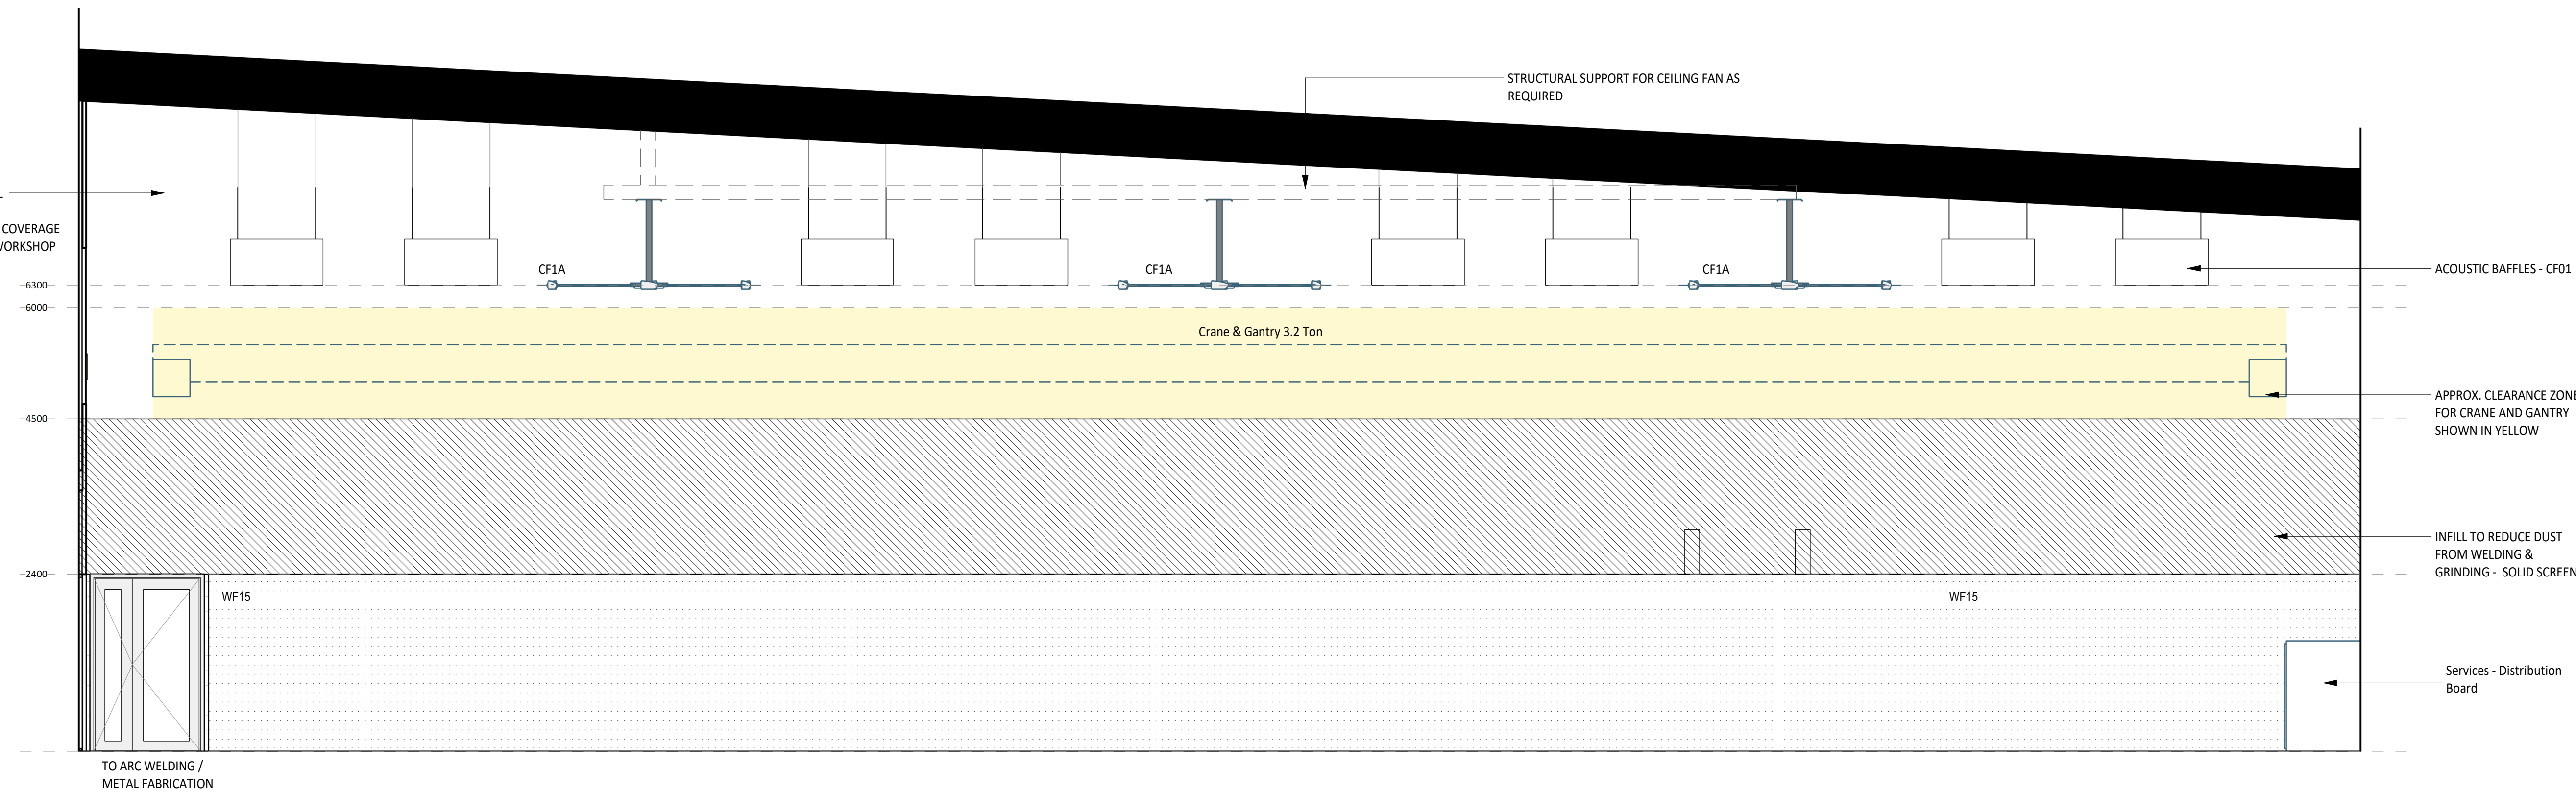

2 ELEVATION DETAIL
60-011 1 : 50