

**CQU ROCKHAMPTON
TAFE
CONSOLIDATION -
STAGE 2**554/700 Yaamba Rd, Norman
Gardens QLD 4701

for



B	05/03/26	ISSUED FOR TENDER	BS
A	12/02/26	ISSUED FOR TENDER	BS
1	30/01/26	DRAFT 60% ISSUE	BS

rev	date	details	init.
-----	------	---------	-------

drawn	date
PT	30/01/26
checked	date
BS	30/01/26
verified	date
BS	30/01/26

scale

**RLS - METFAB - GF - ARC
WELDING / METAL
FABRICATION**scale
1 : 50 @ A1

project no.

260018

revision


B

sheet no.

CQU-ROK-092-GN-ARC-60-020

original sheet size - A1 (594mm x 841mm)

ISSUED FOR TENDER

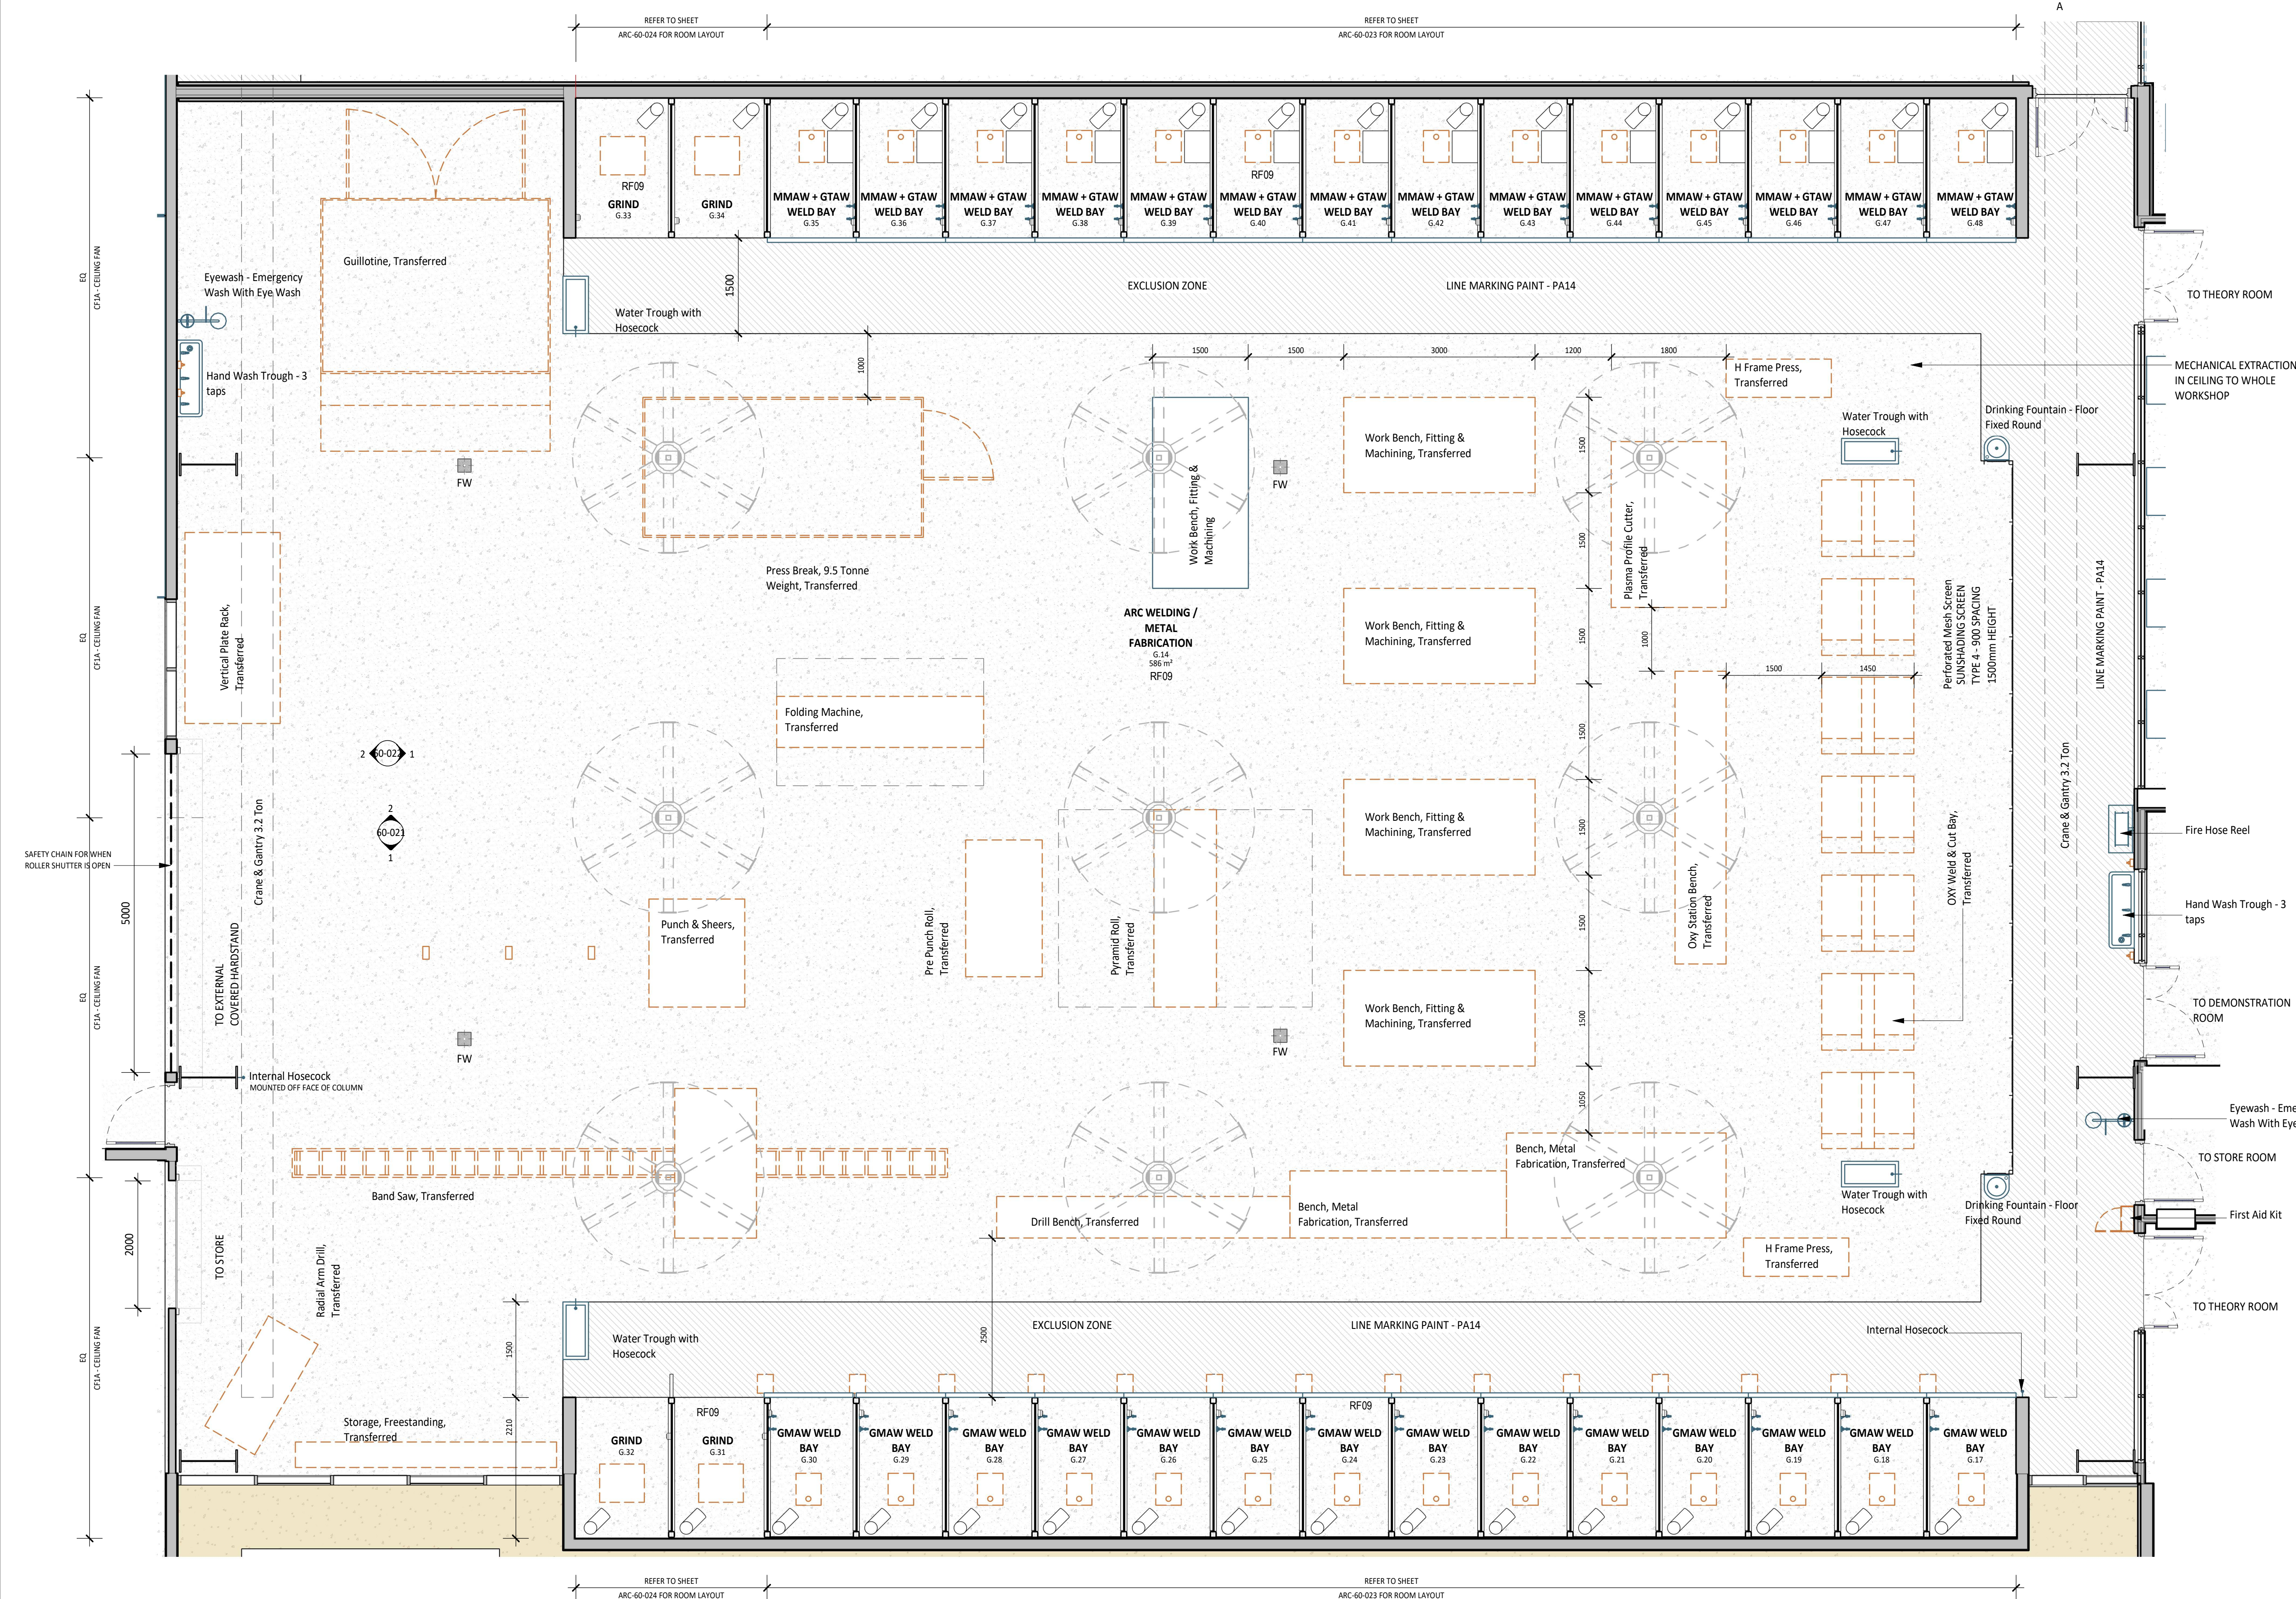

40-LEGEND FFE - ARC WELDING G.14				
Code	Description	Group	Count	
	Water Trough with Hosecock	1	4	
BN11A	Hand Wash Trough - 3 taps	1	2	
CD3A	Emergency Call	1	1	
CF1A	Ceiling Fan - Powerfull D, 6 Aluminium Airfalls	1	9	
FHR	Fire Hose Reel	1	1	
HY7A	Drinking Fountain - Floor Fixed Round	1	2	
SR1A	Eyewash - Emergency Wash With Eye Wash	1	2	
TW3A	Internal Hosecock	1	2	
WB37C	Work Bench, Fitting & Machining	1	1	
WT3DA	Water Trough with Hosecock	1	4	
CA1A	First Aid Kit	2	1	

40-LEGEND FFE - ARC WELDING G.14				
Code	Description	Group	Count	
DS12A	Dispenser - Soap	2	4	
EQ5_T	Bench, Metal Fabrication, Transferred	2T	1	
EQ6_T	Bench, Metal Fabrication, Transferred	2T	1	
EQ7_T	H Frame Press, Transferred	2T	2	
EQ8_T	Oxy Station Bench, Transferred	2T	1	
EQ9_T	OXY Weld & Cut Bay, Transferred	2T	7	
EQ10_T	Guillotine, Transferred	2T	1	
EQ11_T	Drill Bench, Transferred	2T	1	
EQ12_T	Vertical Plate Rack, Transferred	2T	1	
EQ15_T	Plasma Profile Cutter, Transferred	2T	1	
EQ16_T	Band Saw, Transferred	2T	1	

40-LEGEND FFE - ARC WELDING G.14				
Code	Description	Group	Count	
EQ17_T	Storage, Freestanding, Transferred	2T	1	
EQ18_T	Punch & Shears, Transferred	2T	1	
EQ19_T	Press Break, 9.5 Tonne Weight, Transferred	2T	1	
EQ20_T	Pyramid Roll, Transferred	2T	1	
EQ21_T	Pre Punch Roll, Transferred	2T	1	
EQ22_T	Radial Arm Drill, Transferred	2T	1	
EQ23_T	Folding Machine, Transferred	2T	1	
EQ25_T	Weld Equipment, Transferred	2T	14	
EQ26_T	Weld Equipment, Transferred	2T	14	
WB37C_T	Work Bench, Fitting & Machining, Transferred	2T	4	