



**CQU ROCKHAMPTON
TAFE
CONSOLIDATION -
STAGE 2**

554/700 Yaamba Rd, Norman
Gardens QLD 4701

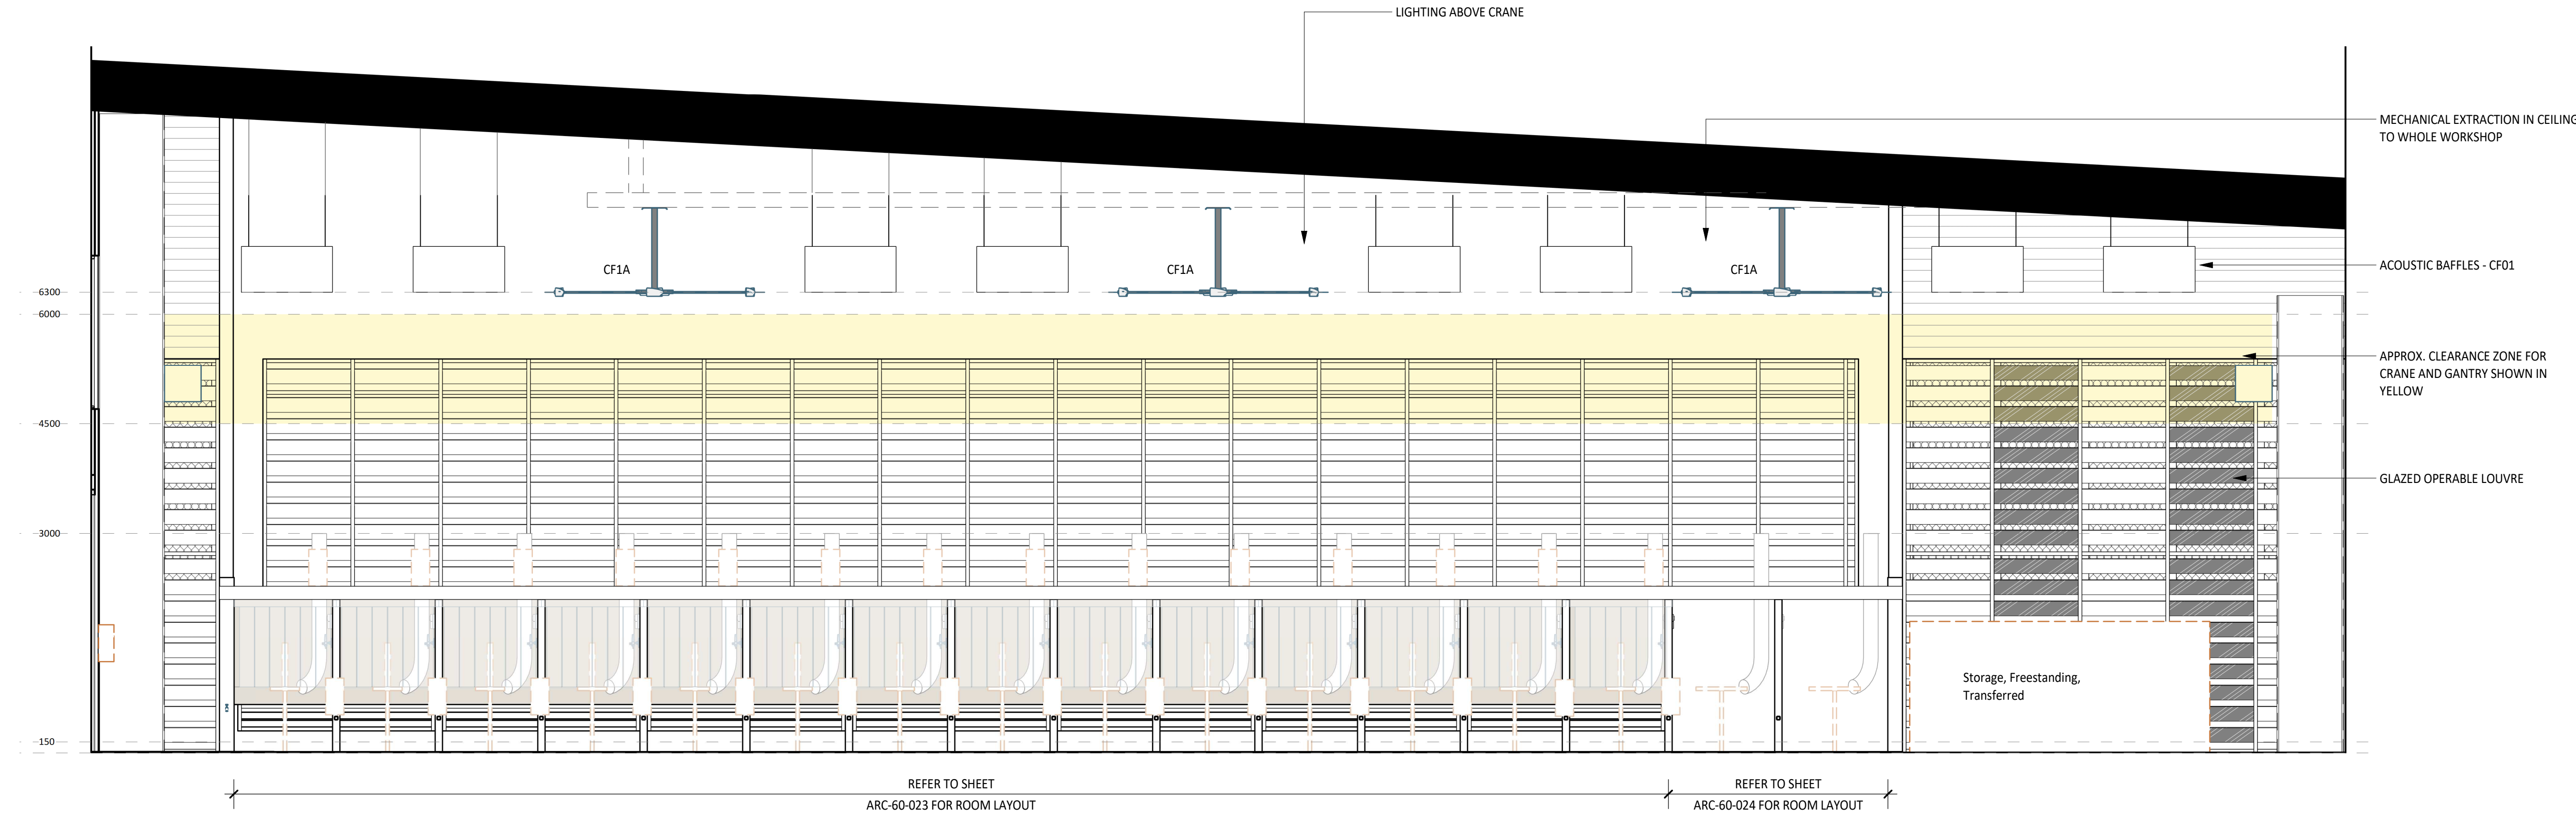

1
60-020
ELEVATION DETAIL
1 : 50

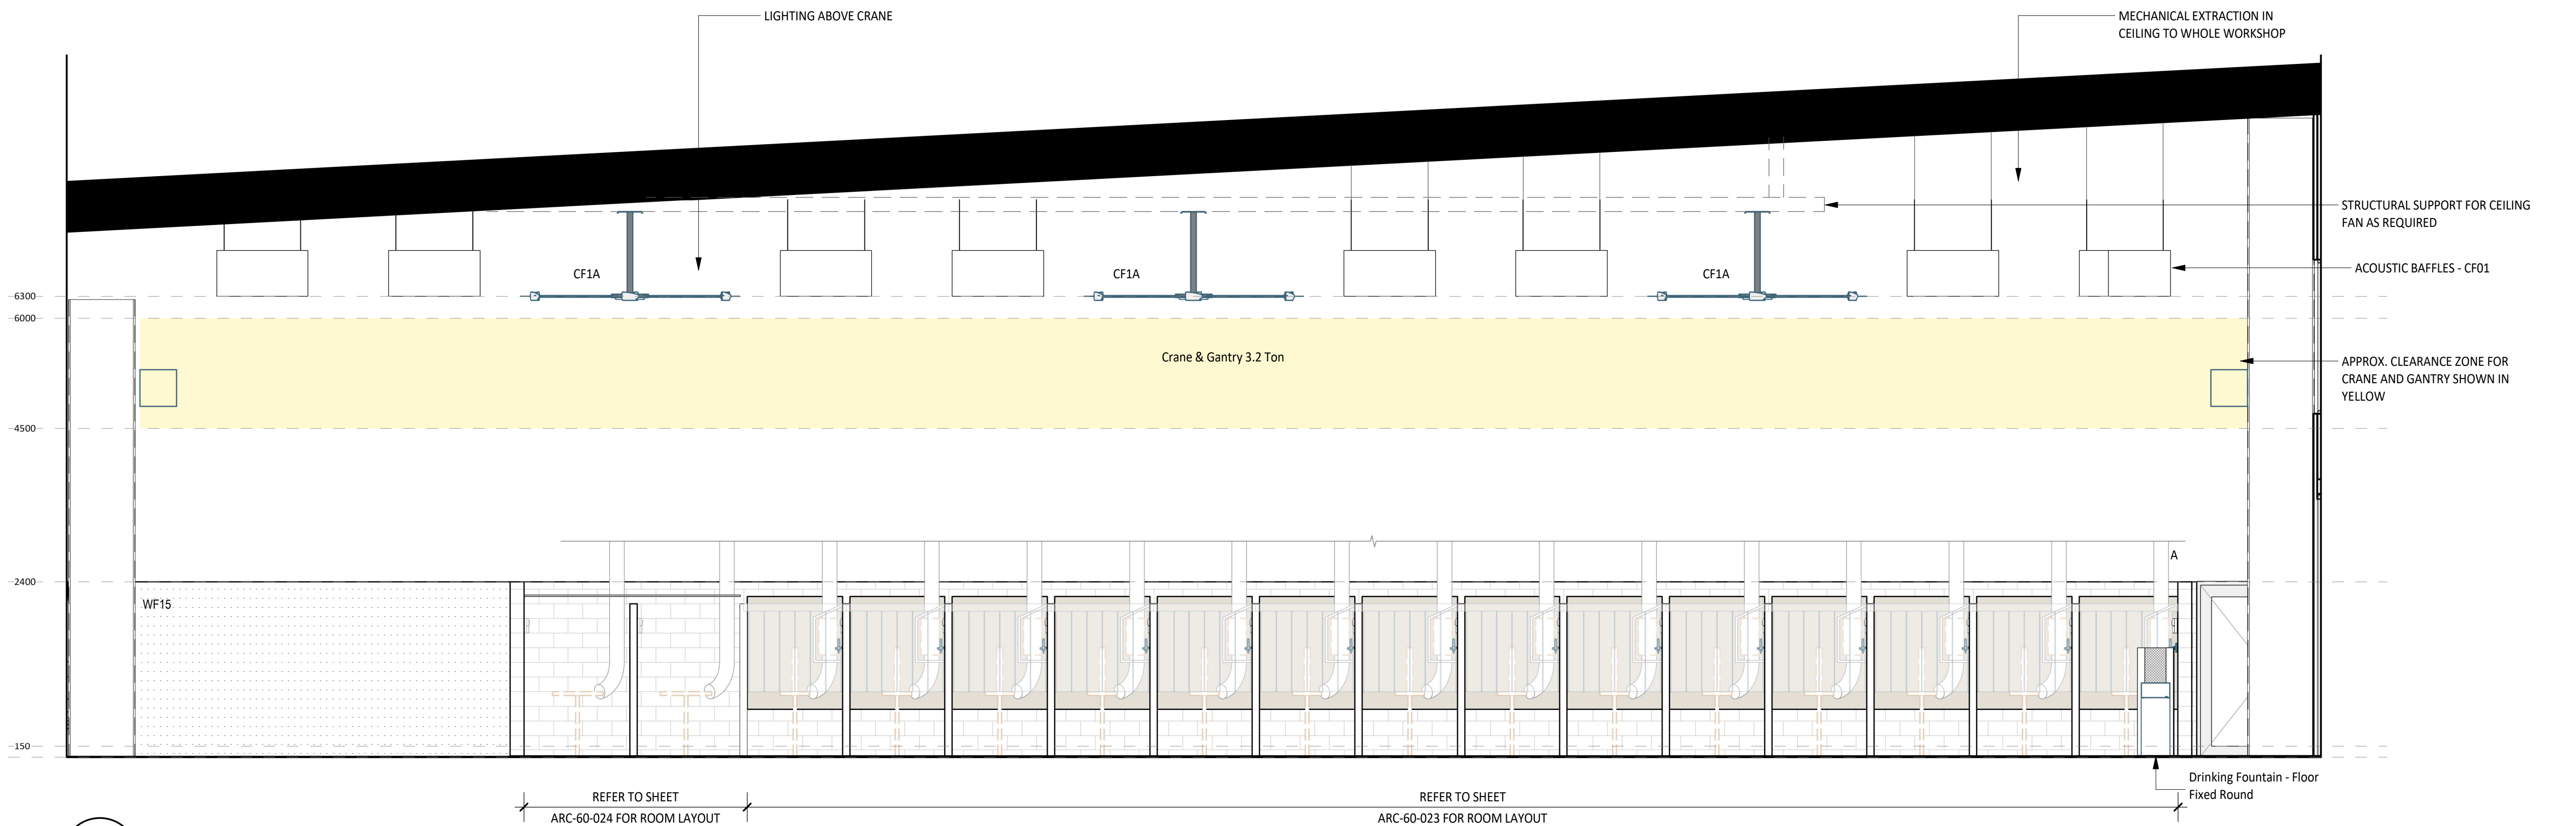

2
60-020
ELEVATION DETAIL
1 : 50

A	12/02/26	ISSUED FOR TENDER	BS
1	30/01/26	DRAFT 60% ISSUE	BS
rev/	date	details	init.

drawn	date
PT	30/01/26
checked	date
BS	30/01/26
verified	date
BS	30/01/26

scale

**RLS - METFAB - GF - ARC
WELDING / METAL
FABRICATION**

scale
1 : 50 @ A1
project no.
260018

revision
A
sheet no.
CQU-ROK-092-GN-ARC-60-021

ISSUED FOR TENDER