



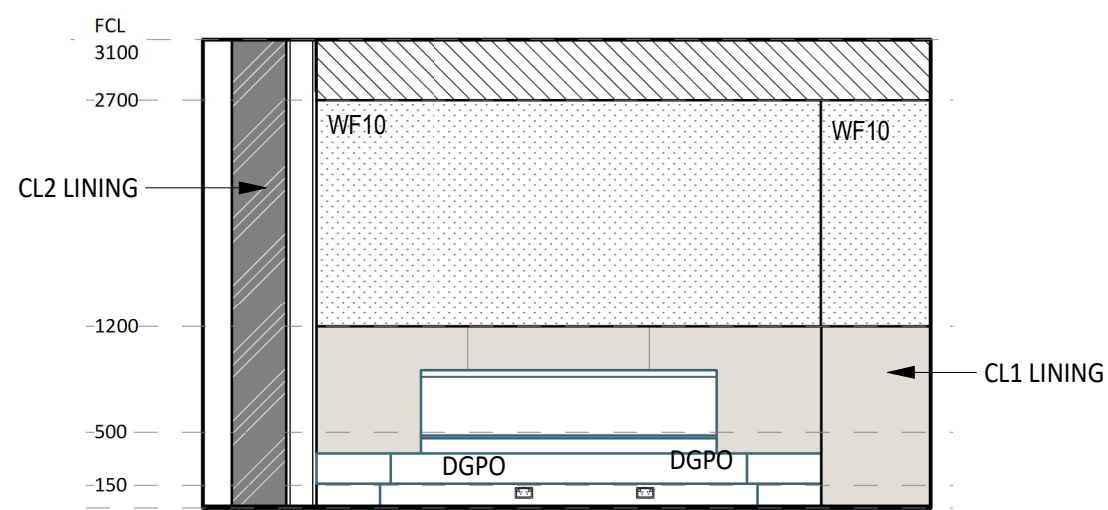


4 ELEVATION DETAIL
60-036 1 : 50

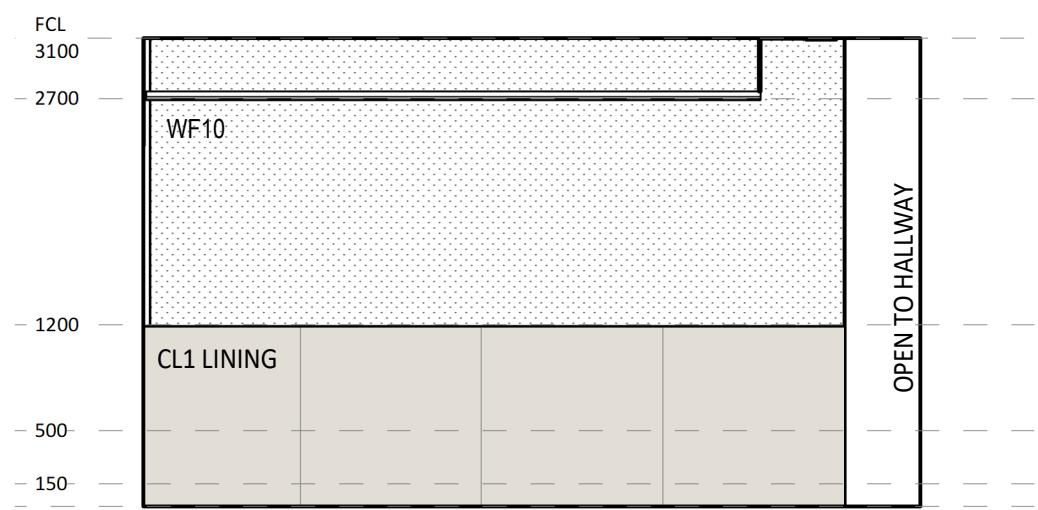


5 ELEVATION DETAIL
60-001 1 : 50

60-00 SCHEDULE JOINERY-CIRCULATION / WAIT G.04	
Mark	Comments
J.NTB.5	BENCH SEAT WITH POWER
J.NTB.6	BENCH SEAT WITH POWER
J.NTB.7	BENCH SEAT WITH POWER
J.NTB.8	BENCH SEAT
J.NTB.9	BENCH SEAT WITH POWER
J.NTB.11	BENCH SEAT WITH POWER


40-LEGEND FFE - CIRCULATION / WAIT G.04			
Code	Description	Group	Count
CH61A	Chair - Breakout Four Legs Upholstered Seat Pad	1	6
CH61B	Chair - Breakout Four Legs Upholstered Seat Pad	1	10
CH61C	Chair - Breakout Four Legs Upholstered Seat Pad	1	8
TB4B	Table - Round - 900dia	1	16
TB12B	Table - Meeting - 1500x750	1	2
DGPO	Double GPO Power Outlet Wall Mounted	ELEC	17

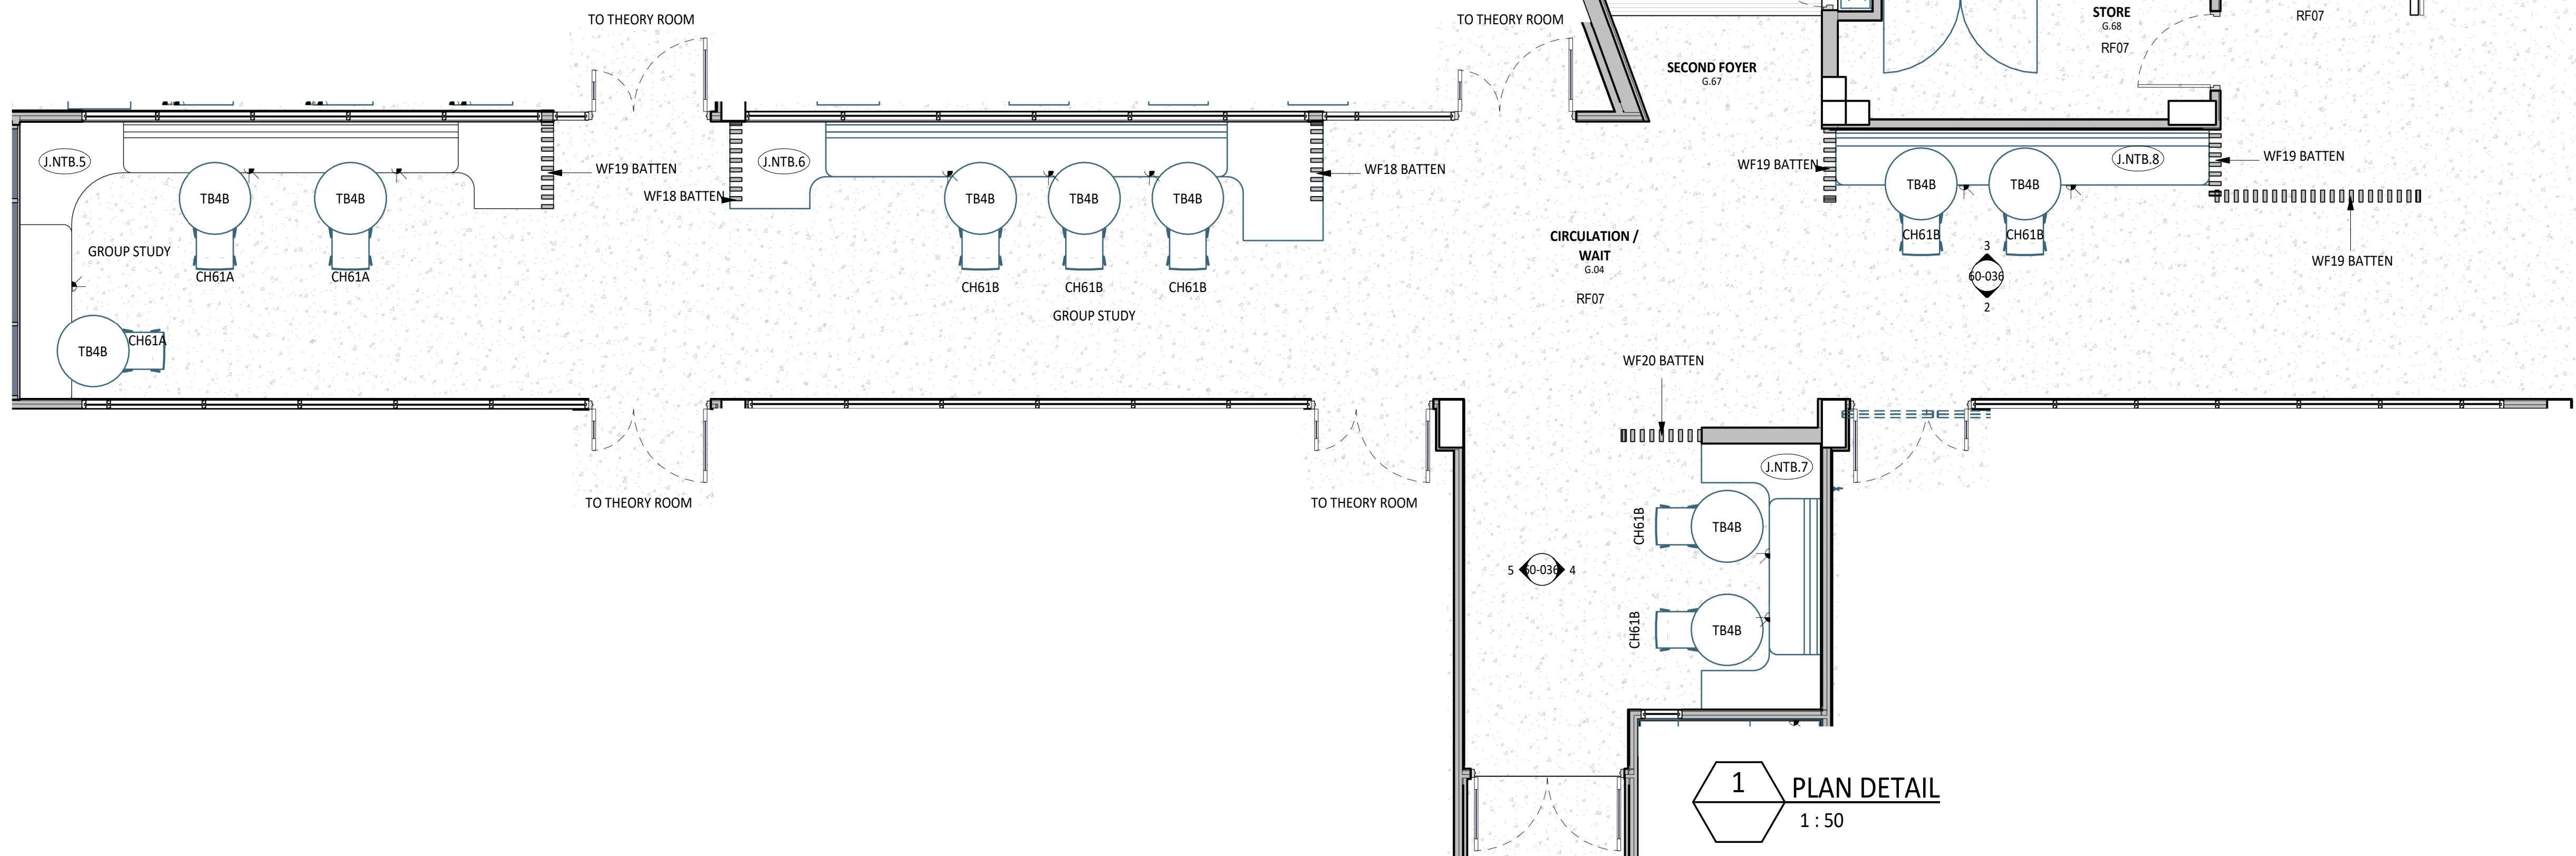

1 PLAN DETAIL
1 : 50

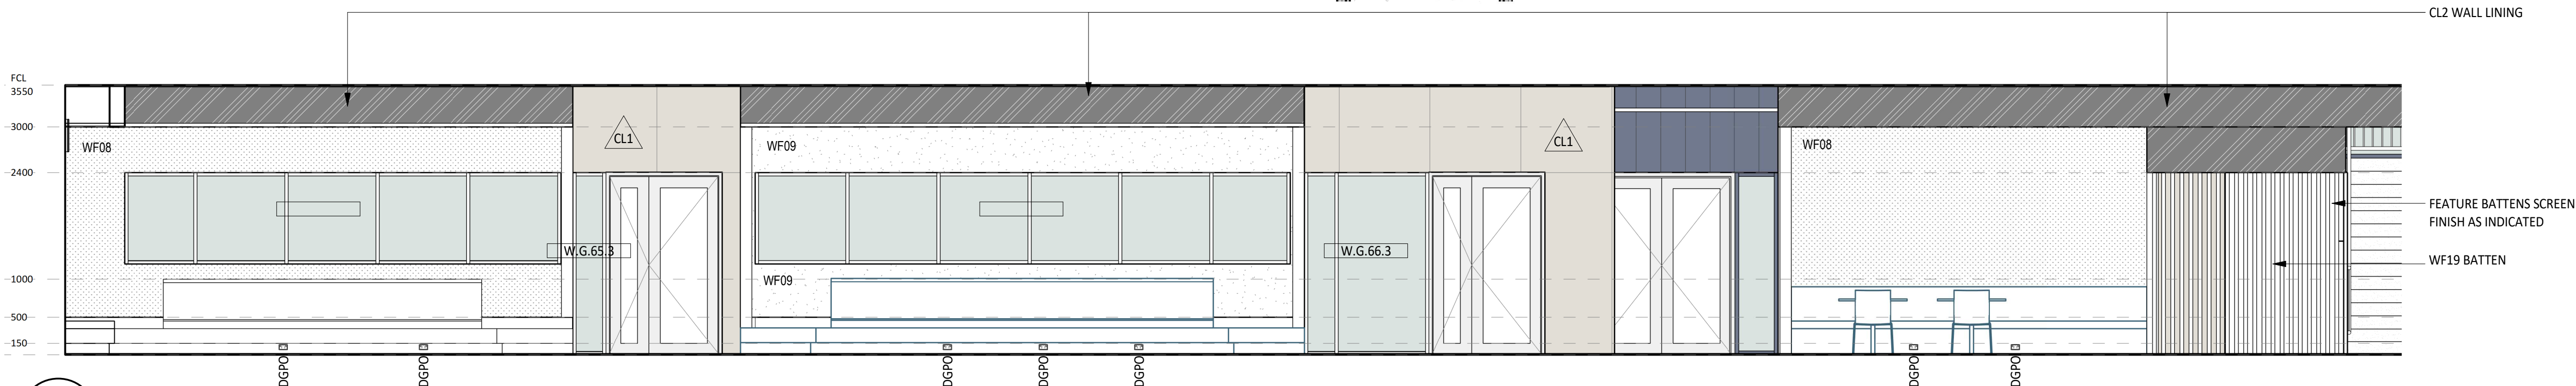

3 ELEVATION DETAIL
60-010 1 : 50

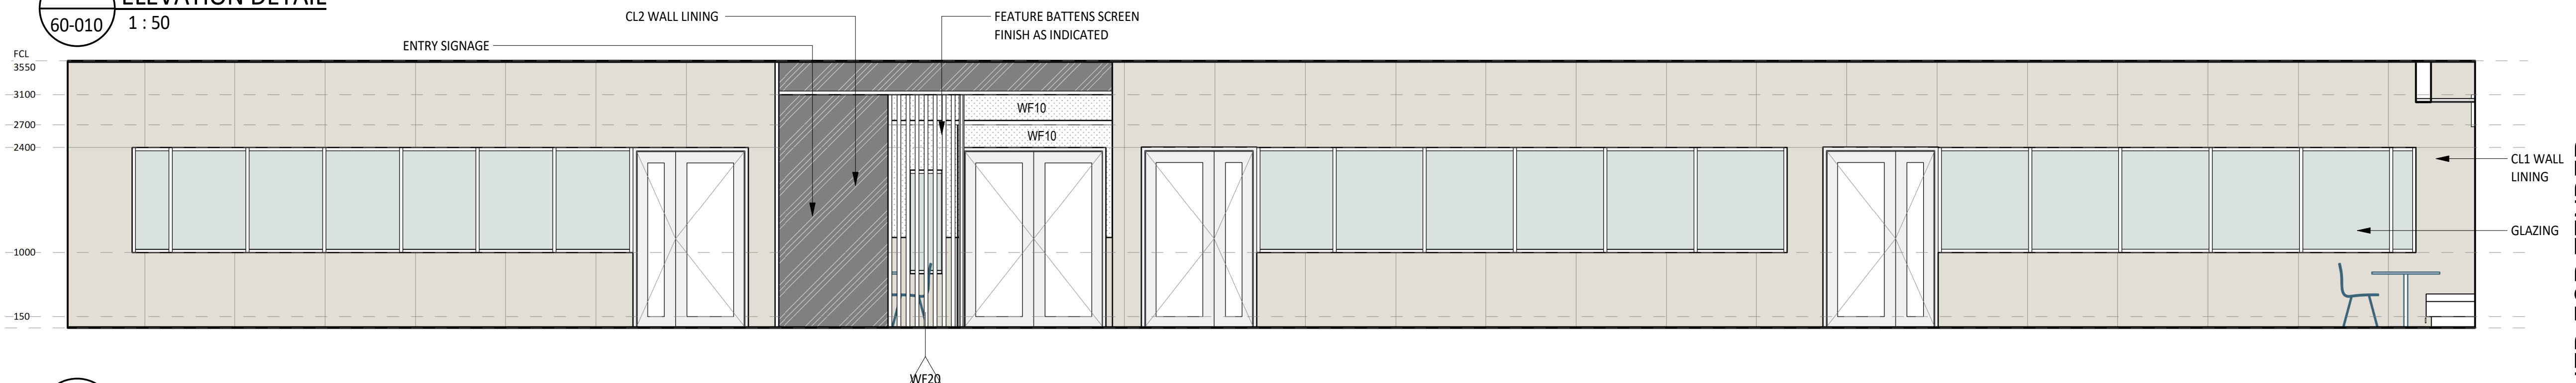

2 ELEVATION DETAIL
60-010 1 : 50

thomson
adsett



Telephone +61 7 3840 9999
bne@thomsonadsett.com
Level 9, 470 St Pauls Terrace
Fortitude Valley
Qld 4006 Australia
thomsonadsett.com

© Copyright
These drawings and designs and the copyright thereof are the property of Thomson Adsett Pty Ltd and must not be used, retained or copied without written permission of Thomson Adsett Pty Ltd. ABN 76 105 314 654 Trading as ThomsonAdsett. Dimensions take precedence over scaling. Do not measure off drawings as print sizes may vary

CQU ROCKHAMPTON TAFE CONSOLIDATION - STAGE 2

554/700 Yaamba Rd, Norman
Gardens QLD 4701



A	12/02/26	ISSUED FOR TENDER	BS
1	30/01/26	DRAFT 60% ISSUE	BS

rev	date	details	init.
drawn	date		
PT	30/01/26		
checked	date		
BS	30/01/26		
verified	date		
BS	30/01/26		

scale

RLS - TRADES - GF - CIRCULATION / WAIT

scale project no.
1 : 50 @ A1 260018

revision
A
sheet no.
CQU-ROK-092-GN-ARC-60-036

original sheet size - A1 (594mm x 841mm)

12/02/2026 4:38:23 PM Autodesk Docs/CQU ROCK TAFE/260018_A_CQU-UNIVERSITY_BLD-TRADES_R25.rvt