




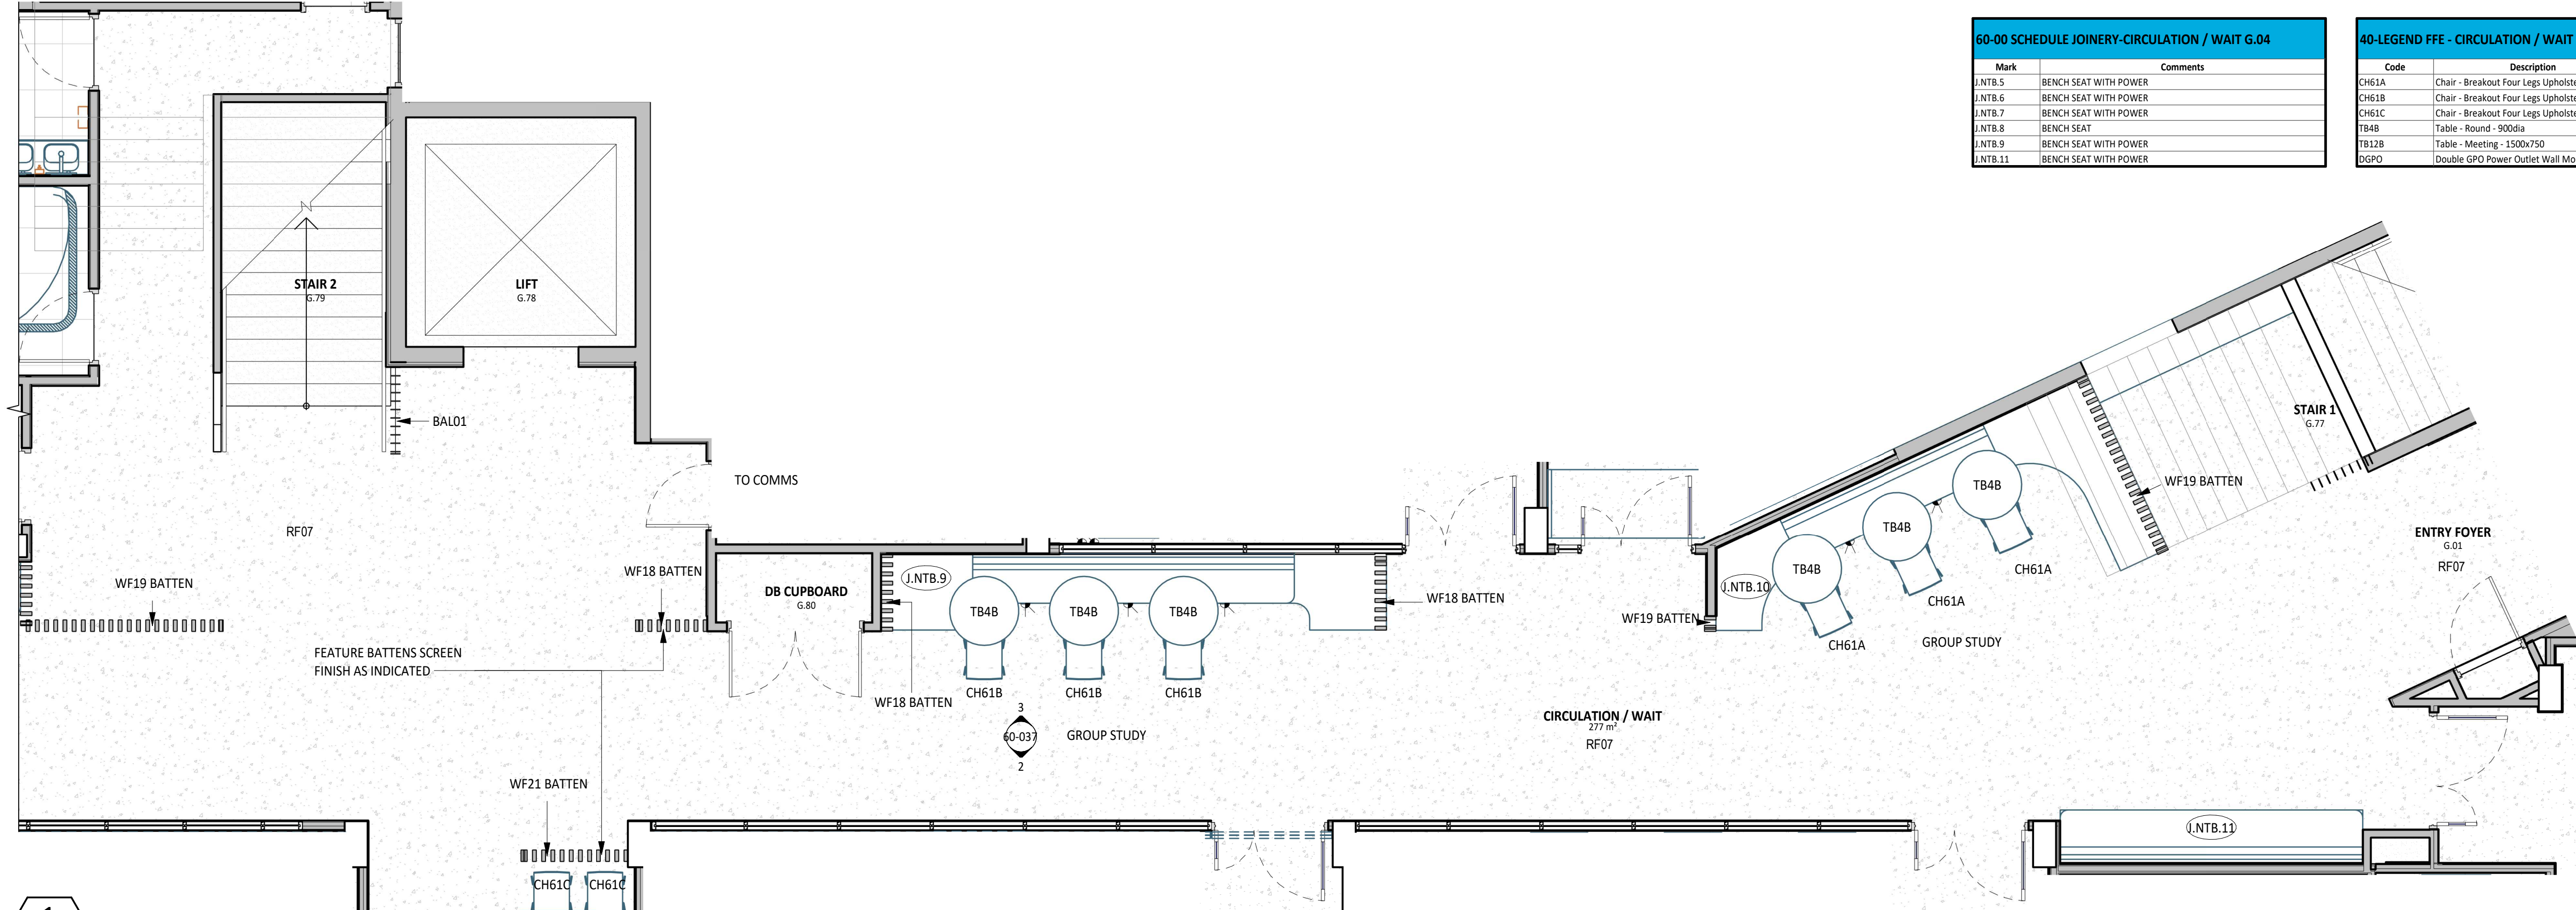


1 PLAN DETAIL  
30-01 1 : 50

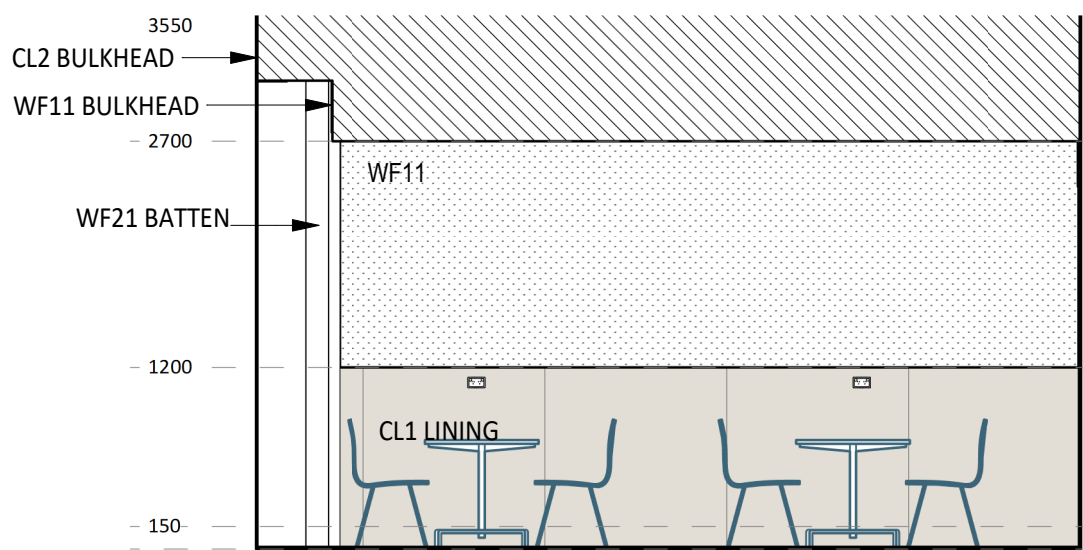


4 ELEVATION DETAIL  
60-037 1 : 50

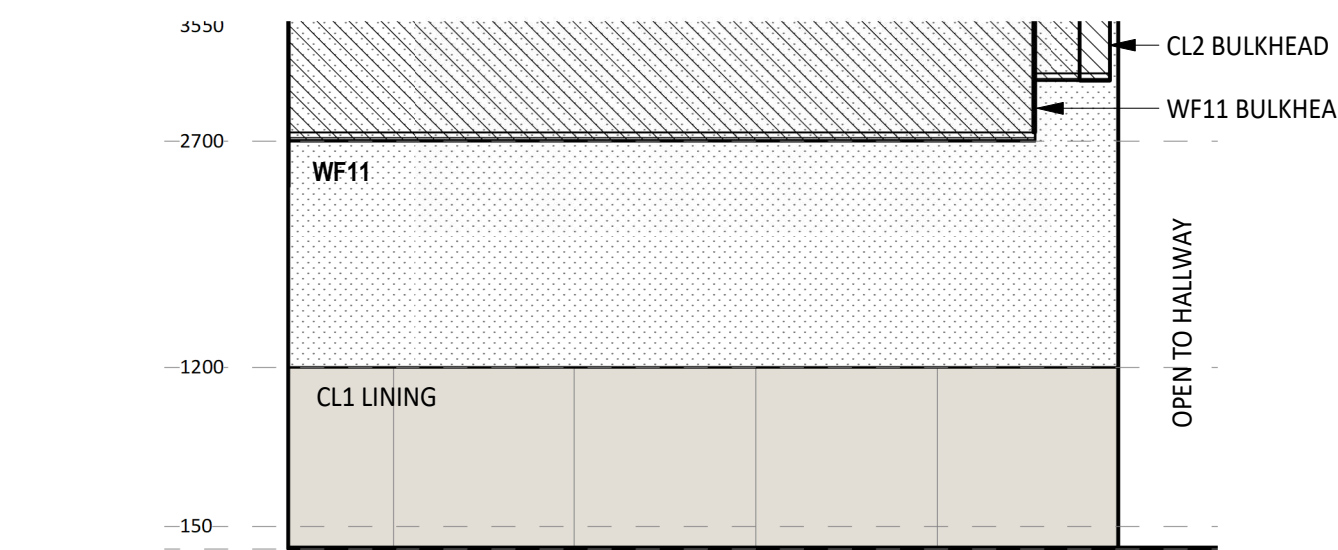

5 ELEVATION DETAIL  
60-011 1 : 50

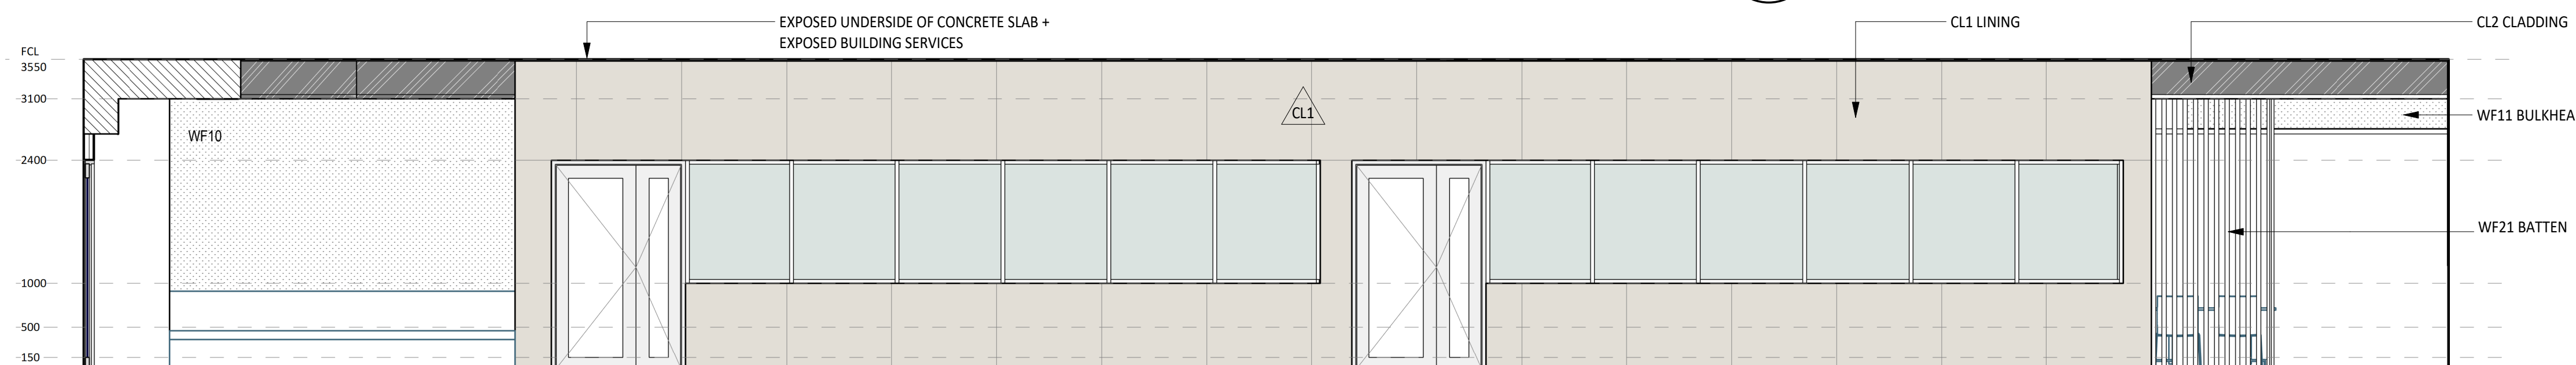

2 ELEVATION DETAIL  
60-030 1 : 50

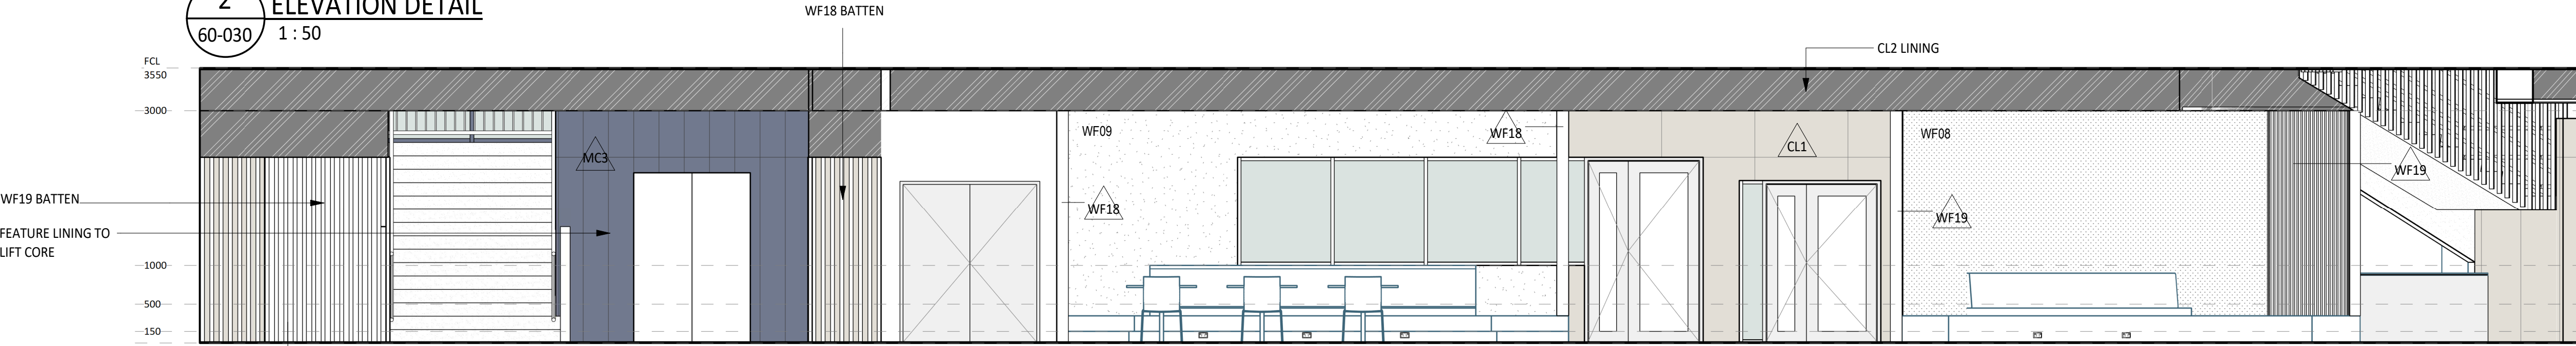

3 ELEVATION DETAIL  
60-036 1 : 50

| 60-00 SCHEDULE JOINERY-CIRCULATION / WAIT G.04 |                       |
|------------------------------------------------|-----------------------|
| Mark                                           | Comments              |
| J.NTB.5                                        | BENCH SEAT WITH POWER |
| J.NTB.6                                        | BENCH SEAT WITH POWER |
| J.NTB.7                                        | BENCH SEAT WITH POWER |
| J.NTB.8                                        | BENCH SEAT            |
| J.NTB.9                                        | BENCH SEAT WITH POWER |
| J.NTB.11                                       | BENCH SEAT WITH POWER |

| 40-LEGEND FFE - CIRCULATION / WAIT G.04 |                                                 |       |       |
|-----------------------------------------|-------------------------------------------------|-------|-------|
| Code                                    | Description                                     | Group | Count |
| CH61A                                   | Chair - Breakout Four Legs Upholstered Seat Pad | 1     | 6     |
| CH61B                                   | Chair - Breakout Four Legs Upholstered Seat Pad | 1     | 10    |
| CH61C                                   | Chair - Breakout Four Legs Upholstered Seat Pad | 1     | 8     |
| TB4B                                    | Table - Round - 900dia                          | 1     | 16    |
| TB12B                                   | Table - Meeting - 1500x750                      | 1     | 2     |
| DGPO                                    | Double GPO Power Outlet Wall Mounted            | ELEC  | 17    |

thomson  
adsett

**PEDDLE THORP**  
architecture | interiors | health | planning

Telephone +61 7 3840 9999  
bne@thomsonadsett.com  
Level 9, 470 St Pauls Terrace  
Fortitude Valley  
Qld 4006 Australia  
thomsonadsett.com

© Copyright  
These drawings and designs and the copyright thereof are the property of Thomson Adsett Pty Ltd and must not be used, retained or copied without written permission of Thomson Adsett Pty Ltd. A.B.N 76 105 314 654 Trading as ThomsonAdsett. Dimensions take precedence over scaling. Do not measure off drawings as print sizes may vary

**CQU ROCKHAMPTON  
TAFE  
CONSOLIDATION -  
STAGE 2**

554/700 Yaamba Rd, Norman  
Gardens QLD 4701

for

**CQUniversity**  
AUSTRALIA

|     |          |                   |       |
|-----|----------|-------------------|-------|
| A   | 12/02/26 | ISSUED FOR TENDER | BS    |
| 1   | 30/01/26 | DRAFT 60% ISSUE   | BS    |
| rev | date     | details           | init. |

|          |          |
|----------|----------|
| drawn    | date     |
| PT       | 30/01/26 |
| checked  | date     |
| BS       | 30/01/26 |
| verified | date     |
| BS       | 30/01/26 |

scale

**RLS - TRADES - GF -  
CIRCULATION / WAIT**

scale  
1 : 50 @ A1

project no.  
260018

revision  
**A**

sheet no.  
**CQU-ROK-092-GN-ARC-60-037**

ISSUED FOR TENDER