


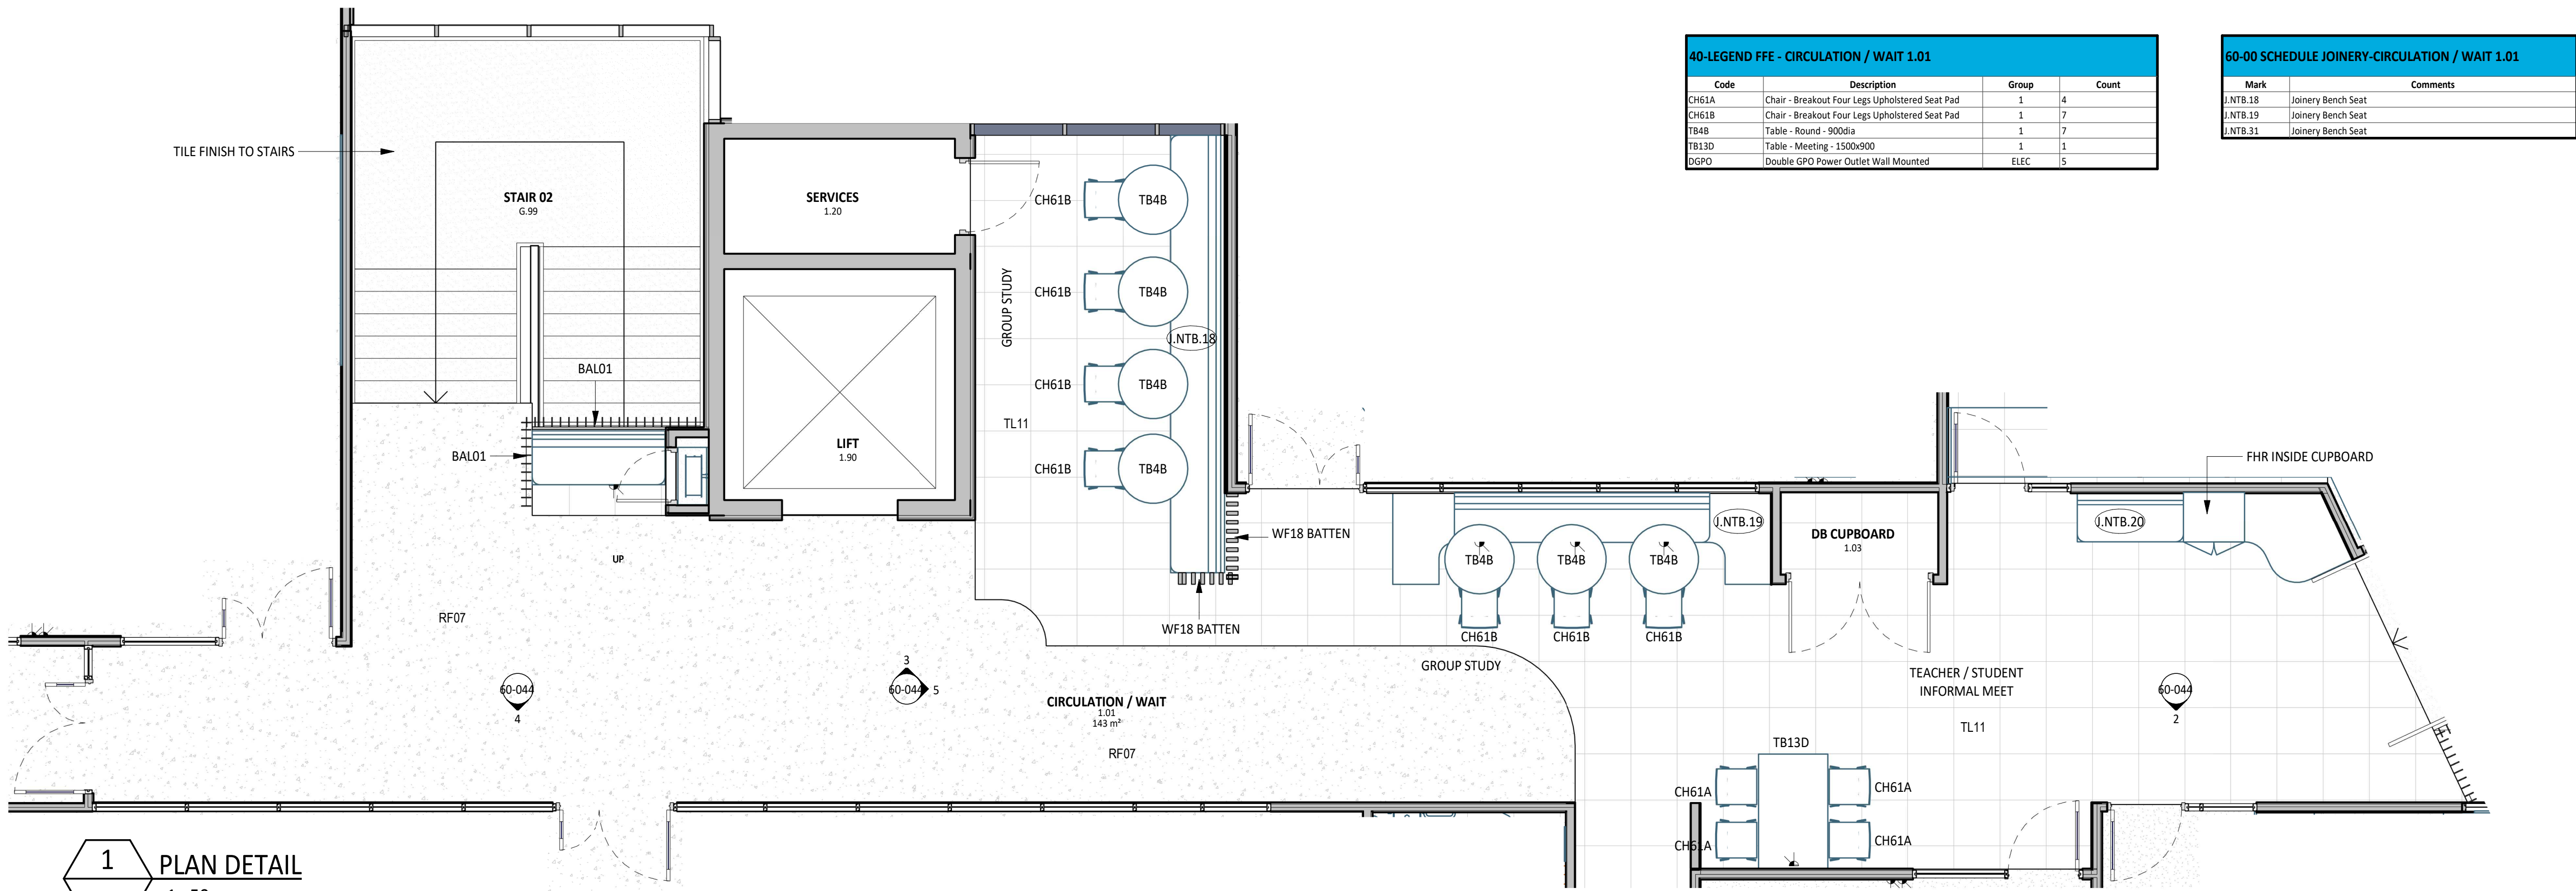


40-LEGEND FFE - CIRCULATION / WAIT 1.01			
Code	Description	Group	Count
CH61A	Chair - Breakout Four Legs Upholstered Seat Pad	1	4
CH61B	Chair - Breakout Four Legs Upholstered Seat Pad	1	7
TB4B	Table - Round - 900dia	1	7
TB13D	Table - Meeting - 1500x900	1	1
DGPO	Double GPO Power Outlet Wall Mounted	ELEC	5

60-00 SCHEDULE JOINERY-CIRCULATION / WAIT 1.01		
Mark	Joinery Bench Seat	Comments
J.NTB.18	Joinery Bench Seat	
J.NTB.19	Joinery Bench Seat	
J.NTB.31	Joinery Bench Seat	


1 PLAN DETAIL
1:50




2 ELEVATION DETAIL
60-038 1:50

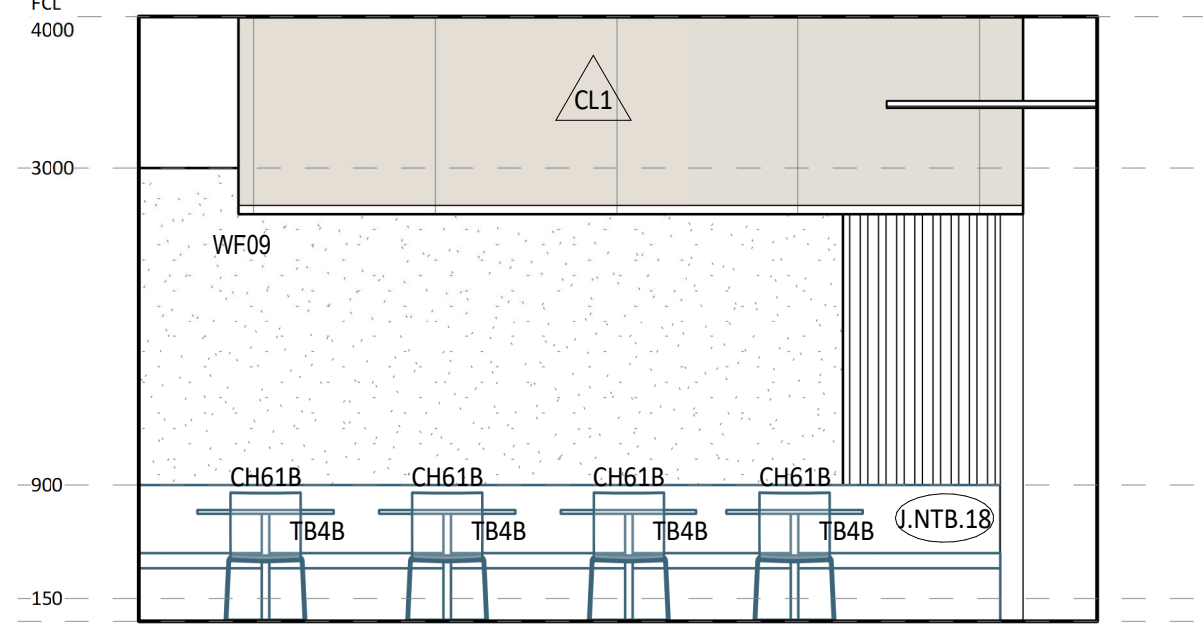

5 ELEVATION DETAIL
60-044 1:50

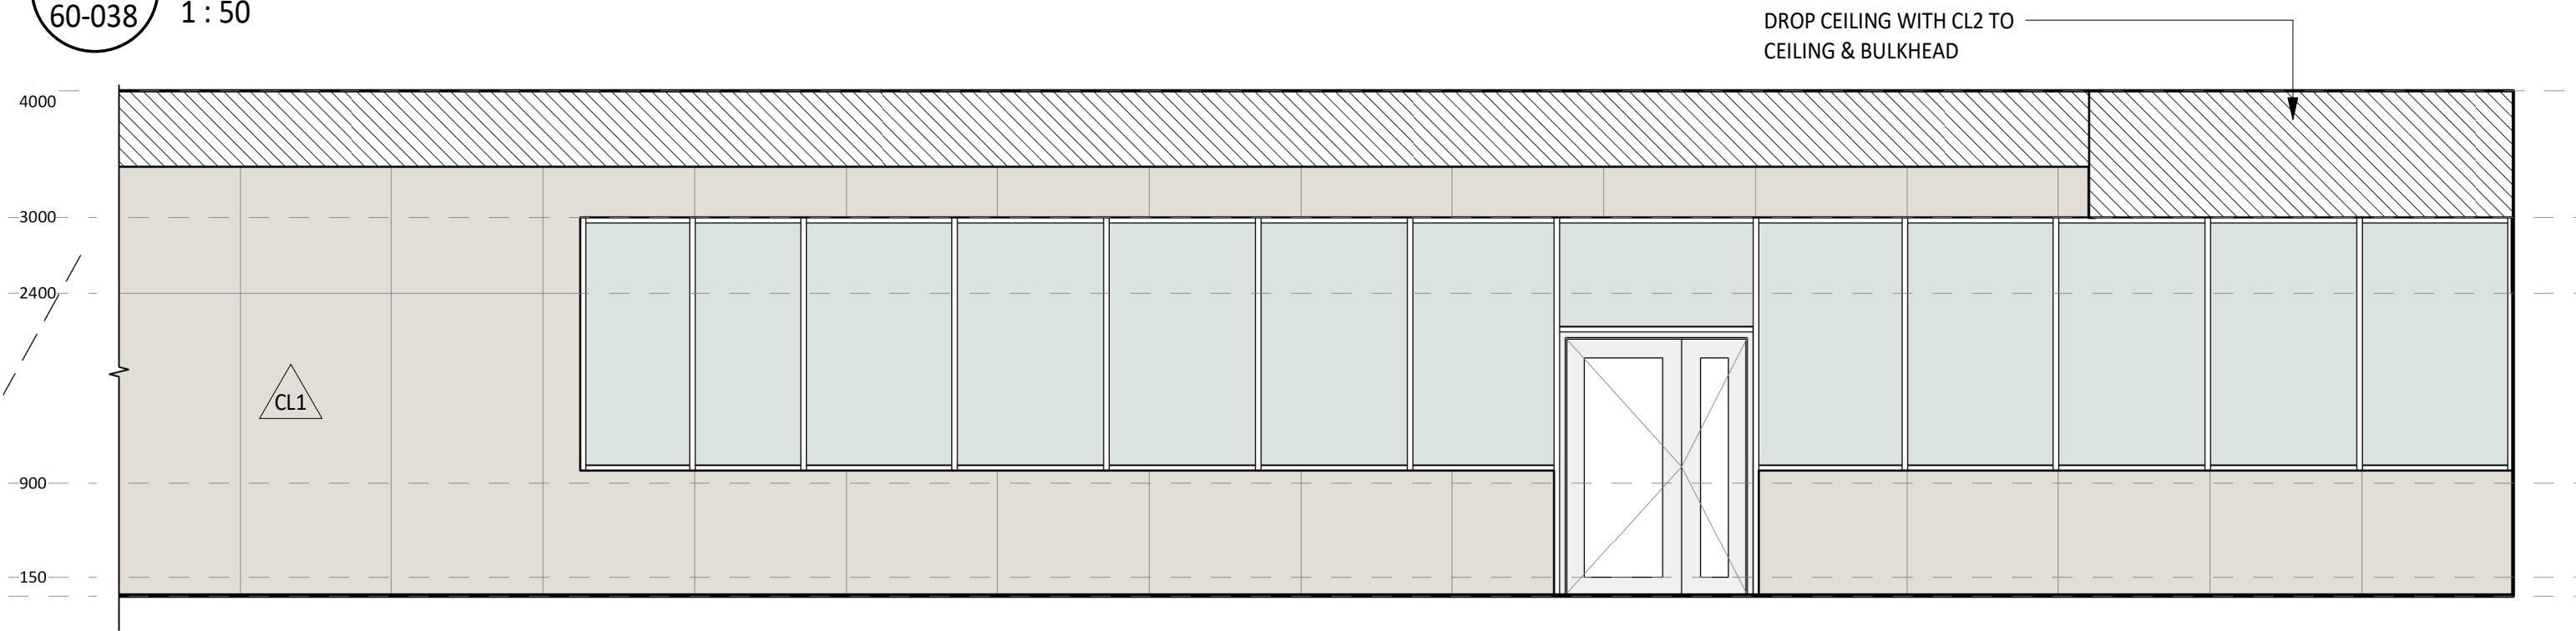

4 ELEVATION DETAIL
60-039 1:50

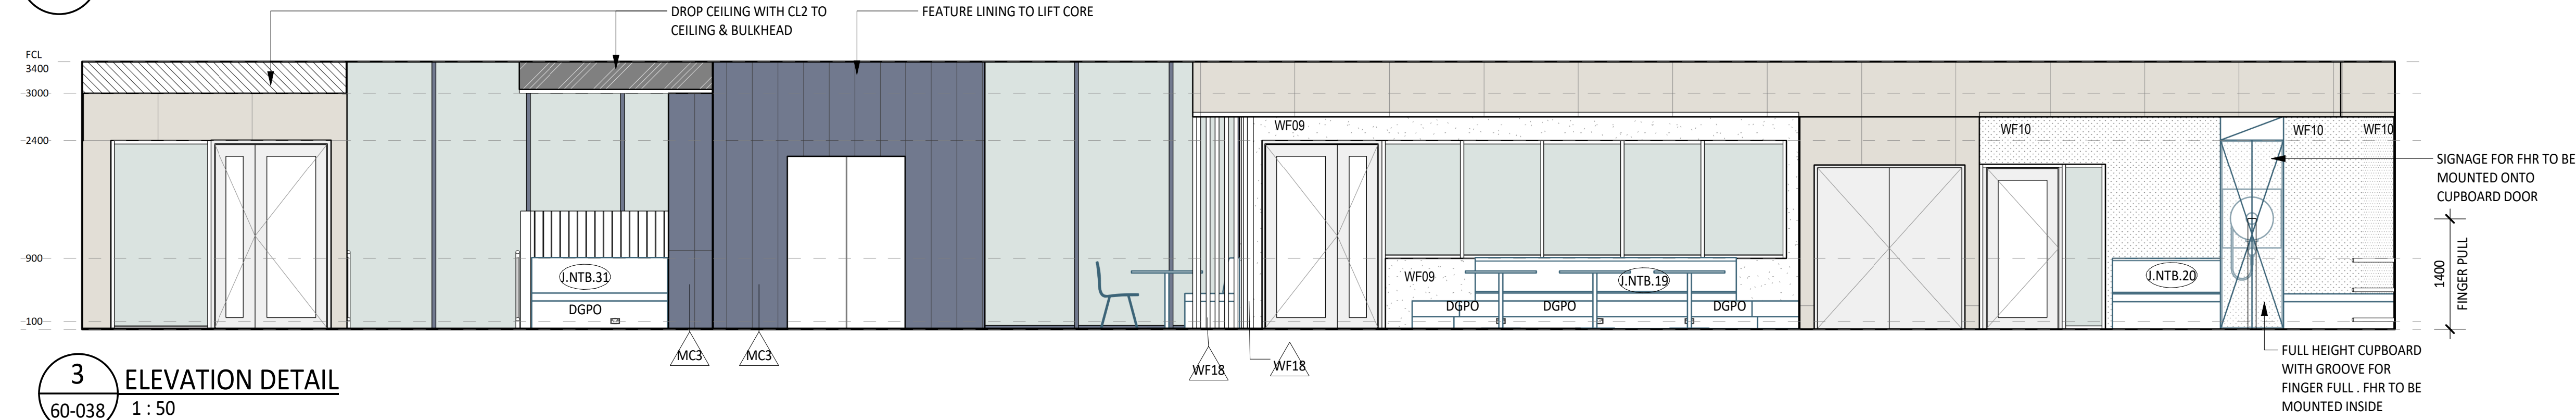

3 ELEVATION DETAIL
60-038 1:50

thomson
adsett

PEDDLE THORP
architecture | interiors | health | planning

Telephone +61 7 3840 9999
bne@thomsonadsett.com
Level 9, 470 St Pauls Terrace
Fortitude Valley
Qld 4006 Australia
thomsonadsett.com

© Copyright
These drawings and designs and the copyright thereof are the property of Thomson Adsett Pty Ltd and must not be used, retained or copied without written permission of Thomson Adsett Pty Ltd. A.B.N 76 105 314 654 Trading as ThomsonAdsett. Dimensions take precedence over scaling. Do not measure off drawings as print sizes may vary

CQU ROCKHAMPTON TAFE CONSOLIDATION - STAGE 2

554/700 Yaamba Rd, Norman
Gardens QLD 4701

for
CQUniversity
AUSTRALIA

A	12/02/26	ISSUED FOR TENDER	BS
1	30/01/26	DRAFT 60% ISSUE	BS
rev	date	details	init.

drawn	date
PT	30/01/26
checked	date
BS	30/01/26
verified	date
BS	30/01/26

scale

RLS - TRADES - L1 - CIRCULATION / WAIT

scale project no.
1:50 @ A1 260018

revision
A
sheet no.
CQU-ROK-092-01-ARC-60-044

ISSUED FOR TENDER

original sheet size - A1 (594mm x 841mm)